Зажимы натяжные клиновые


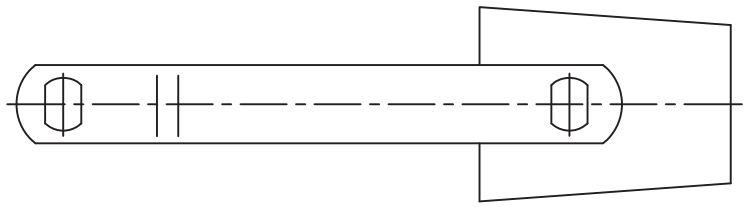


Таблица 5

Обозначение	Провод по ГОСТ 839-80		Комплект клиньев	Разрушающая нагрузка зажима, кгс	Масса, кг
	Марка	Диаметр, мм			
НК-300-1	АС240/32, АС240/39, АС240/56	21,6 21,6 22,4	Клин №1 и №2	11900	5,1
	АС300/39, АС300/48, АС330/30, АС330/43	24,0 24,1 24,8 25,2	Клин №1 и №3		
НК-400-1	АС300/66, АС300/67, АС400/18, АС400/22	24,5 24,5 26,0 26,6	Клин №1 и №2	14480	5,2
	АС400/51, АС400/64	27,5 27,7	Клин №1 и №3		
НК-500-1	АС400/93, АС500/27, АС500/26, АС500/64	29,1 29,4 30,0 30,6	Клин №1 и №2	19920	5,3

Протекторы защитные спиральные типа ПЭС-Dпр-ОХ, смонтированные на проводе в лодочке поддерживающего зажима ПГН-5-3, ПГН-5-4

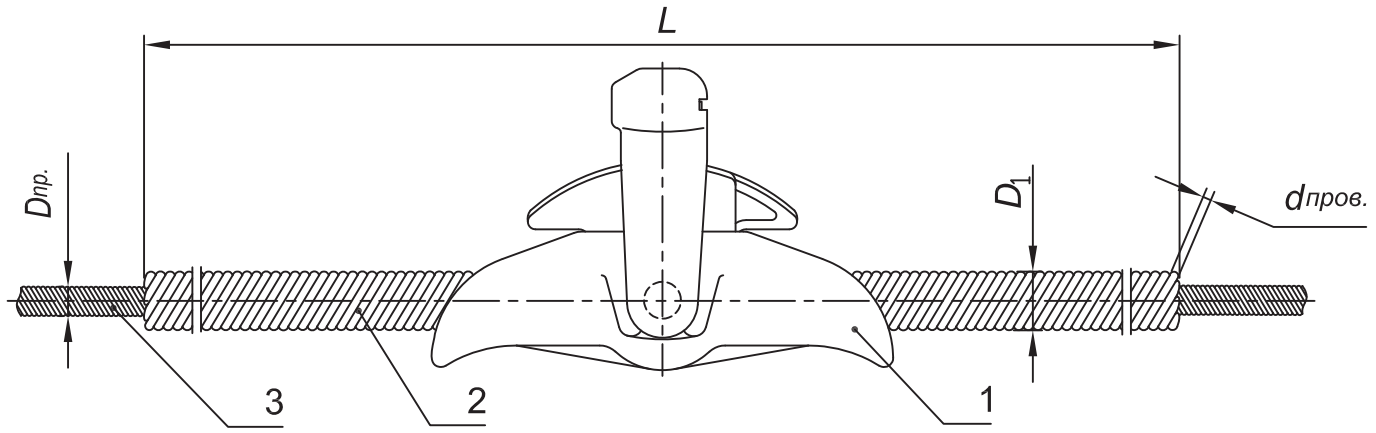


1 - зажим поддерживающий; 2 - протектор; 3 - провод.

Таблица 6

Обозначение	Провод по ГОСТ 839-80		L*, мм	dпров., мм	D 1, мм	Масса, кг
	Сечение, мм2	Диаметр, мм				
ПЗС-21,6-01 ПЗС-21,6-03	240/32 240/39	21,6	2200	3,8 5,0	29,2 31,6	3,0 1,8
ПЗС-22,4-01 ПЗС-22,4-03	240/56	22,4	2200	3,8 5,0	30,3 32,4	3,2 1,8
ПЗС-24,1-01	300/39	24,0	2300	3,2 4,0	30,5 32,1	4,2 1,7
ПЗС-24,1-03	300/48	24,1		3,2 6,0	30,9 36,5	4,3 2,5
ПЗС-24,5-01 ПЗС-24,5-03	300/67	24,5	2300	3,2 6,0	31,2 37,2	4,4 2,6
ПЗС-24,8-01	330/30	24,8	2300	3,2 6,0	31,6 32,1	4,6 1,7
ПЗС-24,8-03	330/48	25,2	2300	3,2 6,0	32,4 37,2	4,6 2,6
ПЗС-26,0-01	400/18	26,0	2300	3,2 5,0	33,0 32,1	5,0 1,7
ПЗС-26,0-03	400/22	26,6	2300	3,2 5,0	33,0 36,6	5,0 2,2
ПЗС-27,5-03	400/51	27,5	2300	5,0	37,5	2,3

В комплект поставки протектора входит дистанционная прокладка для ПГН-5-3, ПГН-5-4.

** По согласованию с Заказчиком и с учетом условий работы проводов длина протектора может быть изменена.*

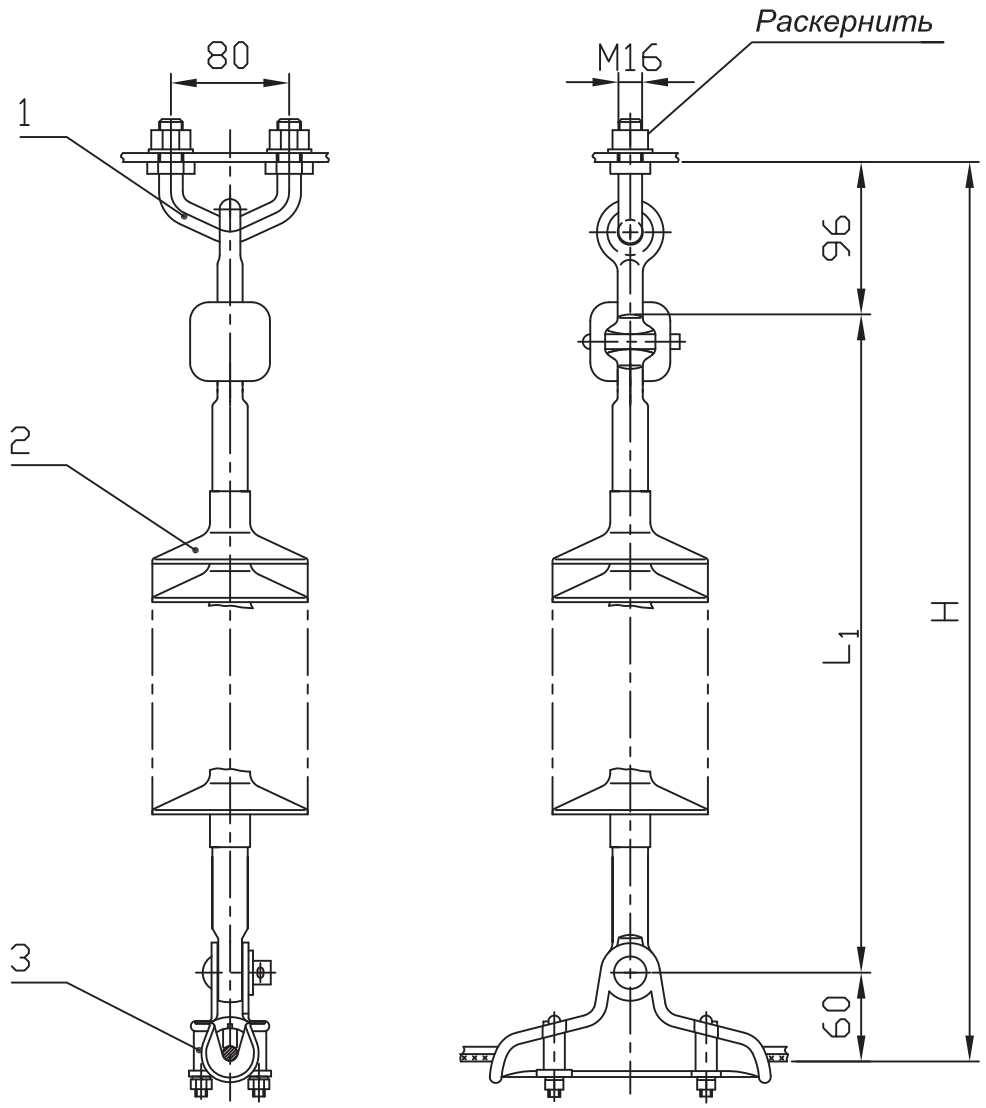

Поз.	Обозначение	Наименование	Кол.	Масса ед. кг	Прим.
1	КГП-7-2В	Узел крепления	1	0,7	
2		Изолятор исп. ГС	1	См. табл.	
3	ПГ-25/6-12	Зажим поддерживающ.	1	1,01	
Масса арматуры, кг				1,71	
Масса изолирующей подвески, кг				См. табл.	

Напряжение ВЛ, кВ	Изолятор, поз.2			Изолирующая подвеска	
	Тип	L_1, мм	Масса, кг	H, мм	Масса, кг
35	ЛК70/35	513	1,5	669	3,2
110	ЛК70/110	1213	3,5	1369	5,2


Взам. инв. N

Подп. и дата

Инв. N подл.

				ЭСИП-0001		
				ЭСС.001 ТМ - т.1		
Утв.	Вигдергауз			Поддерживающие одноцепные изолирующие с полимерными изоляторами ряда 70 кН подвески провода АС70/11 к металлическим и ж/б промежуточным опорам ВЛ 35, 110 кВ	Стадия	Лист	Листов
					Р		1
Пров.	Липунцов				Филиал ОАО "ФСК ЕЭС" "Электросетьсервис"		
Разраб.	Власкина						

Формат А3

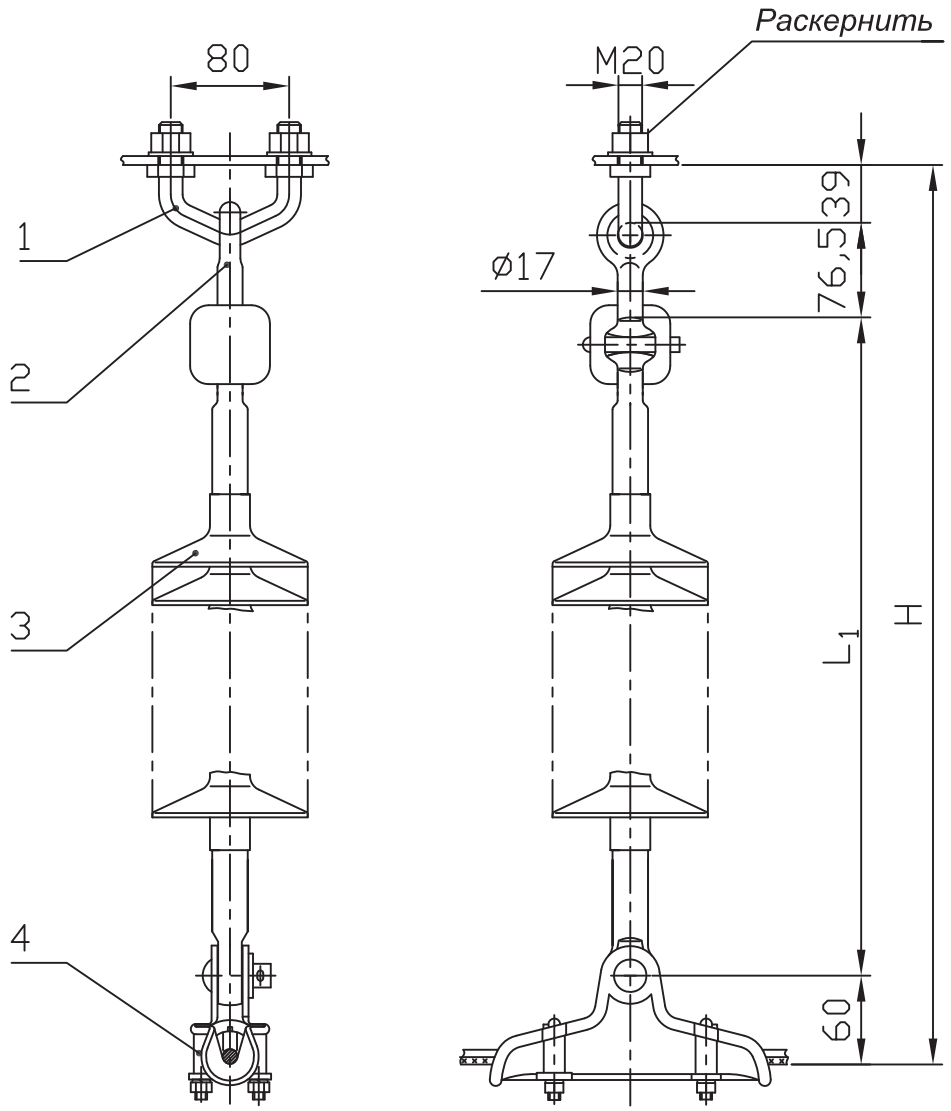

Поз.	Обозначение	Наименование	Кол.	Масса ед. кг	Прим.
1	КГП-16-3	Узел крепления	1	0,81	
2	СРС-7-16	Серьга специальная	1	0,32	
3		Изолятор исп. ГС	1	См. табл.	
4	ПГ-25/6-12	Зажим поддерживающ.	1	1,01	
Масса арматуры, кг				2,14	
Масса изолирующей подвески, кг				См. табл.	

Напряжение ВЛ, кВ	Изолятор, поз.3			Изолирующая подвеска	
	Тип	L_1, мм	Масса, кг	H, мм	Масса, кг
35	ЛК70/35	513	1,5	688,5	3,64
110	ЛК70/110	1213	3,5	1388,5	5,64


Взам. инв. N

Подп. и дата

Инв. N подл.

				ЭСИП-0002	
				ЭСС.001 ТМ - т.1	
Утв.	Вигдергауз			Поддерживающие одноцепные изолирующие с полимерными изоляторами ряда 70 кН подвески провода АС70/11 к металлическим, ж/б промежуточным и деревянным опорам ВЛ 35, 110 кВ	Стадия: Р; Лист: ; Листов: 1
Пров.	Липунцов				Филиал ОАО "ФСК ЕЭС" "Электросетьсервис"
Разраб.	Власкина				

Формат А3

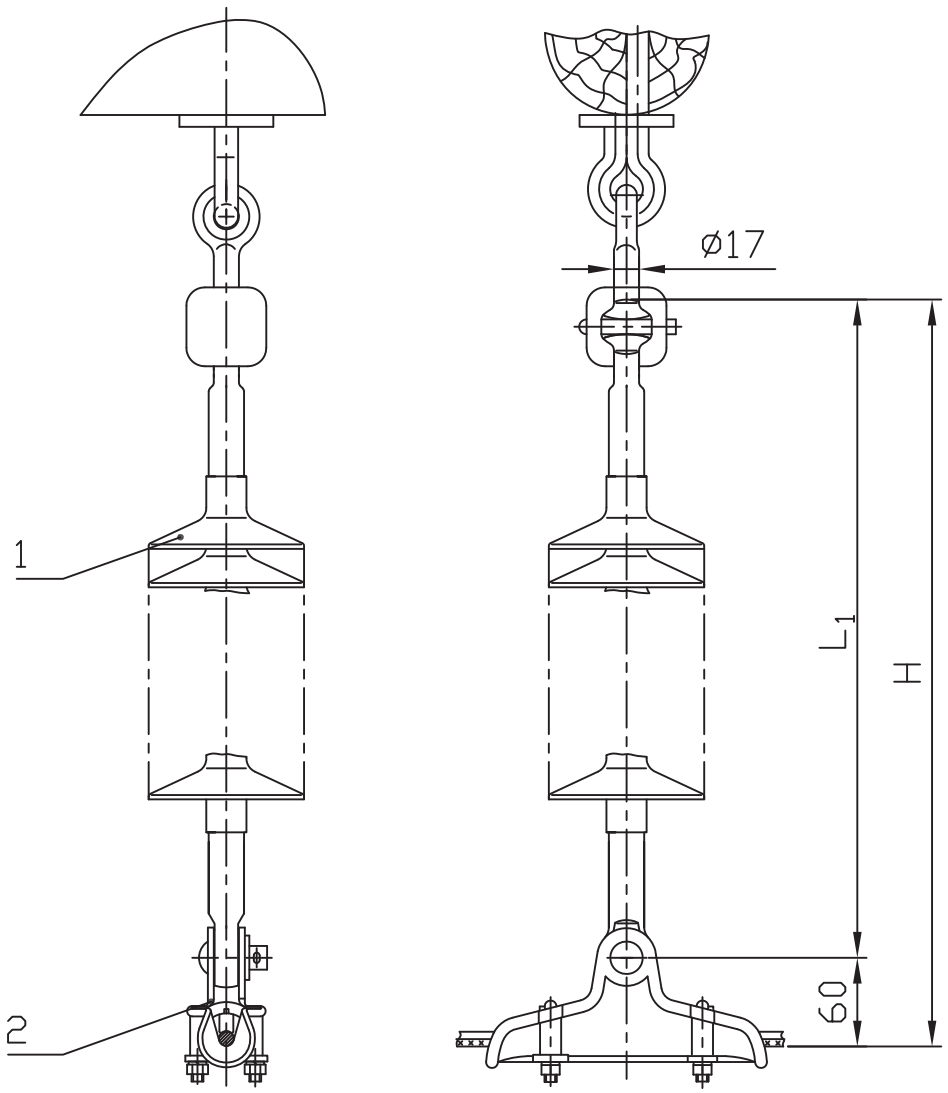

Поз.	Обозначение	Наименование	Кол.	Масса ед. кг	Прим.
1		Изолятор исп. ГС	1	См. табл.	
2	ПГ-25/6-12	Зажим поддерживающ.	1	1,01	
Масса арматуры, кг				1,01	
Масса изолирующей подвески, кг				См. табл.	


Напряжение ВЛ, кВ	Изолятор, поз.1			Изолирующая подвеска	
	Тип	L1, мм	Масса, кг	H, мм	Масса, кг
35	ЛК70/35	513	1,5	573	2,5
110	ЛК70/110	1213	3,5	1273	4,5

Взам. инв. N

Подп. и дата

Инв. N подл.

				ЭСИП-0003		
				ЭСС.001 ТМ - т.1		
Утв.	Вигдергауз			Поддерживающие одноцепные изолирующие с полимерными изоляторами ряда 70 кН подвески провода АС70/11 к промежуточным деревянным опорам ВЛ 35, 110 кВ	Стадия	Лист	Листов
					Р		1
Пров.	Липунцов				Филиал ОАО "ФСК ЕЭС" "Электросетьсервис"		
Разраб.	Власкина						

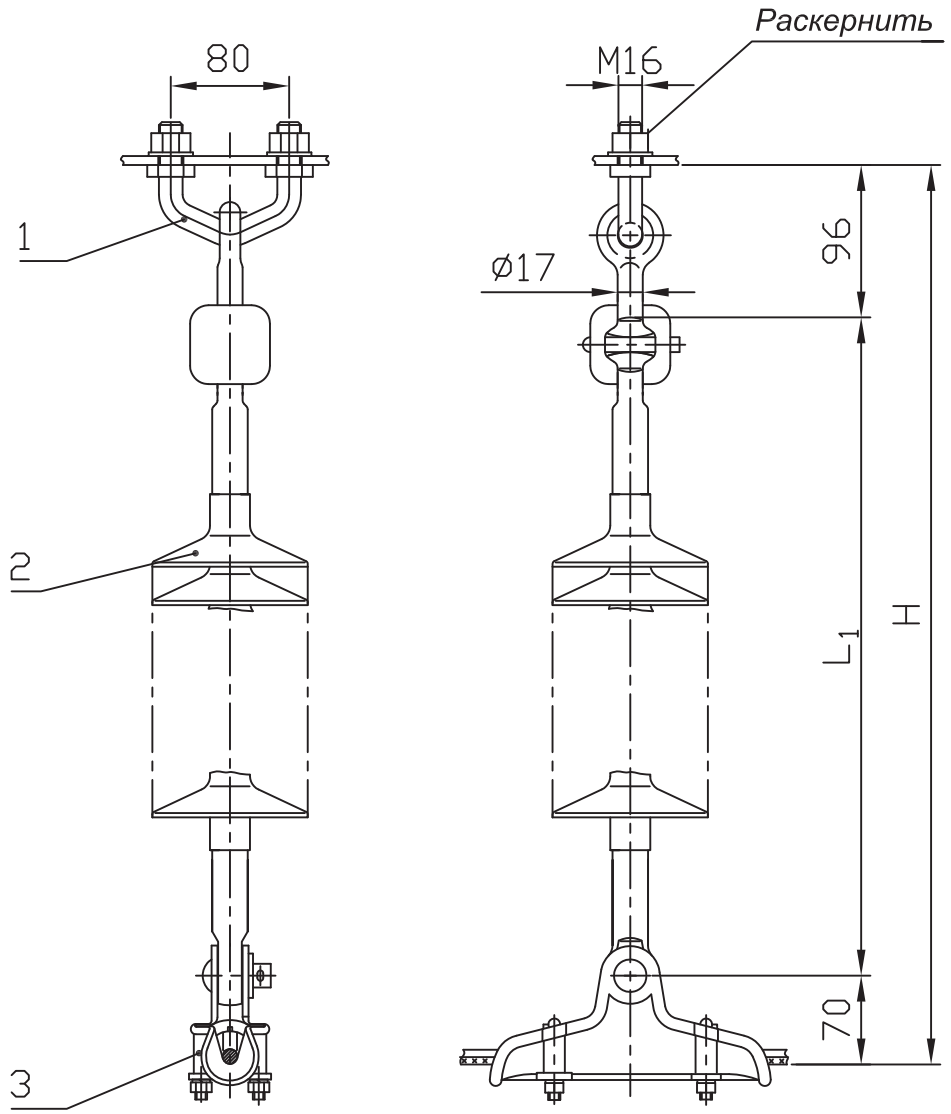

Поз.	Обозначение	Наименование	Кол.	Масса ед. кг	Прим.
1	КГП-7-2В	Узел крепления	1	0,7	
2		Изолятор исп. ГС	1	См. табл.	
3	ПГ-30/12-20	Зажим поддерживающ.	1	1,07	
Масса арматуры, кг				1,77	
Масса изолирующей подвески, кг				См. табл.	

Напряжение ВЛ, кВ	Провод по ГОСТ 839-80		Изолятор, поз.2			Изолирующая подвеска	
	Марка	Диаметр, мм	Тип	L_1, мм	Масса, кг	H, мм	Масса, кг
35	АС95/16, АС120/19, АС150/24	13,5 - 17,5	ЛК70/35	513	1,5	679	3,3
110	АС185/29	18,8	ЛК70/110	1213	3,5	1379	5,3

Взам. инв. N

Подп. и дата


Инв. N подл.

				ЭСИП-0004
				ЭСС.001 ТМ - т.1
Утв.	Вигдергауз			Поддерживающие одноцепные изолирующие с полимерными изоляторами ряда 70 кН подвески проводов к металлическим и ж/б промежуточным опорам ВЛ 35, 110 кВ
Пров.	Липунцов			
Разраб.	Власкина			

Стадия	Лист	Листов
Р		1

Филиал ОАО "ФСК ЕЭС" "Электросетьсервис"

Формат А3

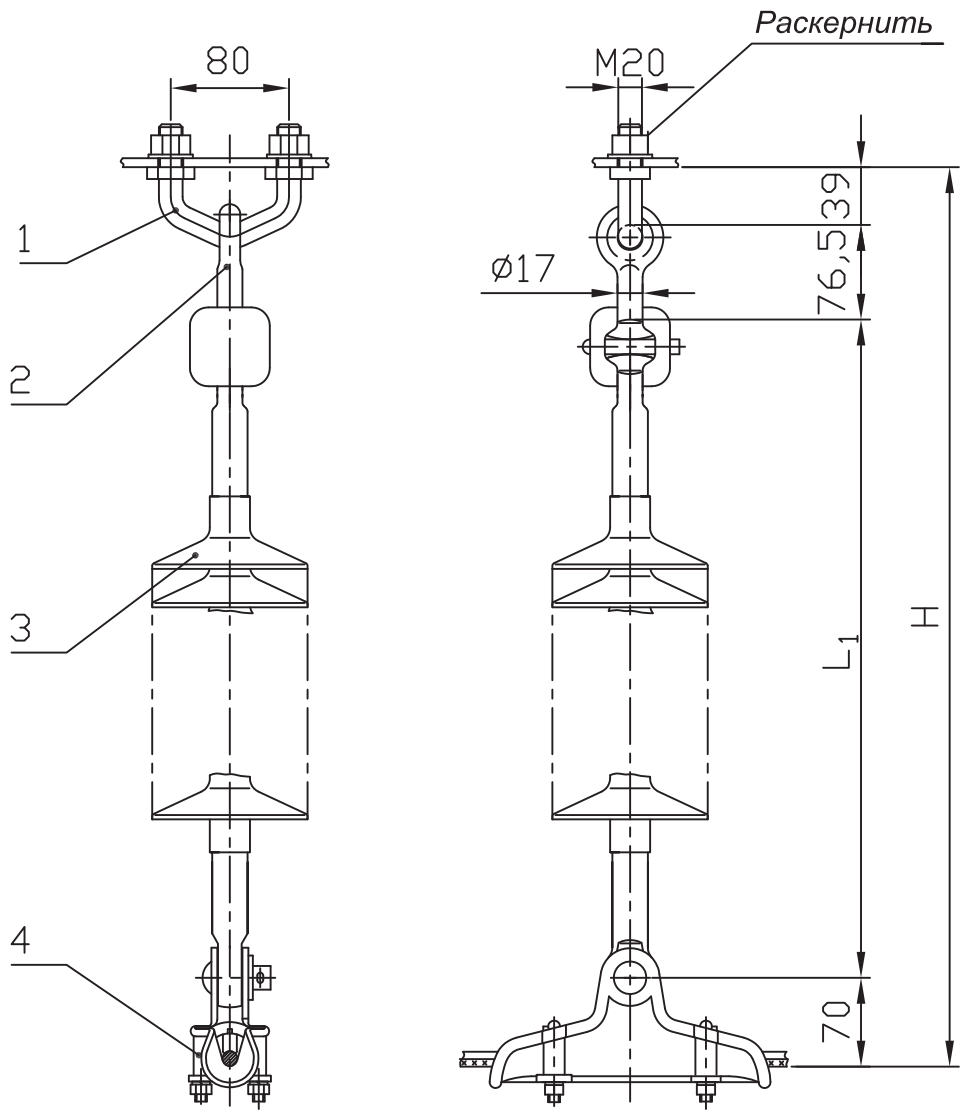

Поз.	Обозначение	Наименование	Кол.	Масса ед. кг	Прим.
1	КГП-16-3	Узел крепления	1	0,81	
2	СРС-7-16	Серьга специальная	1	0,32	
3		Изолятор исп. ГС	1	См. табл.	
4	ПГ-30/12-20	Зажим поддерживающ.	1	1,07	
Масса арматуры, кг				2,2	
Масса изолирующей подвески, кг				См. табл.	


Напряжение ВЛ, кВ	Провод по ГОСТ 839-80		Изолятор, поз.3			Изолирующая подвеска	
	Марка	Диаметр, мм	Тип	L_1, мм	Масса, кг	H, мм	Масса, кг
35	АС95/16, АС120/19, АС150/24	13,5 - 17,5	ЛК70/35	513	1,5	698,5	3,7
110	АС185/29	18,8	ЛК70/110	1213	3,5	1398,5	5,7

Взам. инв. N

Подп. и дата

Инв. N подл.

				ЭСИП-0005		
				ЭСС.001 ТМ - т.1		
Утв.	Вигдергауз			Поддерживающие одноцепные изолирующие с полимерными изоляторами ряда 70 кН подвески проводов к металлическим и ж/б промежуточным опорам ВЛ 35, 110 кВ	Стадия	Лист	Листов
					Р		1
Пров.	Липунцов				Филиал ОАО "ФСК ЕЭС" "Электросетьсервис"		
Разраб.	Власкина						

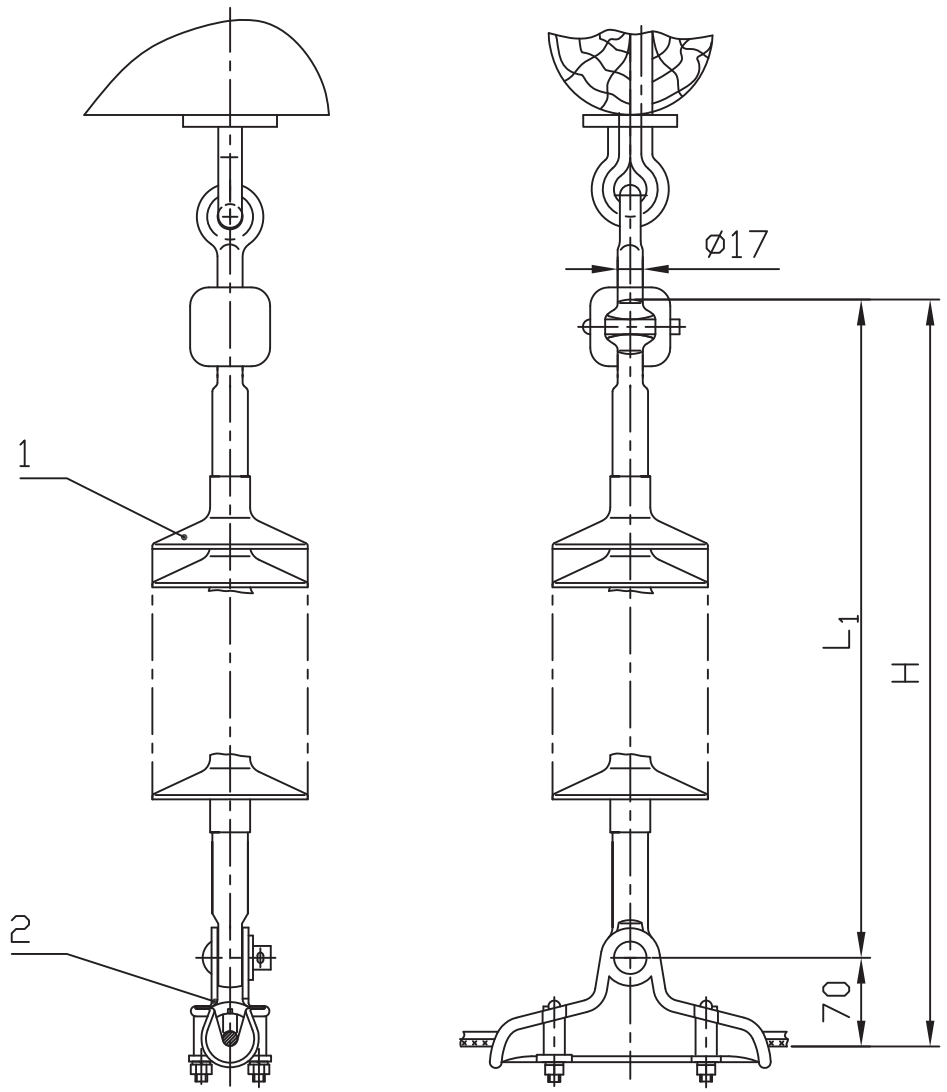

Поз.	Обозначение	Наименование	Кол.	Масса ед. кг	Прим.
1		Изолятор исп. ГС	1	См. табл.	
2	ПГ-30/12-20	Зажим поддерживающ.	1	1,07	
Масса арматуры, кг				1,07	
Масса изолирующей подвески, кг				См. табл.	

Напряжение ВЛ, кВ	Провод по ГОСТ 839-80		Изолятор, поз.1			Изолирующая подвеска	
	Марка	Диаметр, мм	Тип	L1, мм	Масса, кг	H, мм	Масса, кг
35	АС95/16, АС120/19, АС150/24	13,5 - 17,5	ЛК70/35	513	1,5	583	2,6
110	АС185/29	18,8	ЛК70/110	1213	3,5	1283	4,6


Взам. инв. N

Подп. и дата

Инв. N подл.

				ЭСИП-0006		
				ЭСС.001 ТМ - т.1		
Утв.	Вигдергауз			Поддерживающие одноцепные изолирующие с полимерными изоляторами ряда 70 кН подвески проводов к промежуточным деревянным опорам ВЛ 35, 110 кВ	Стадия	Лист	Листов
					Р		1
Пров.	Липунцов				Филиал ОАО "ФСК ЕЭС" "Электросетьсервис"		
Разраб.	Власкина						

Формат А3

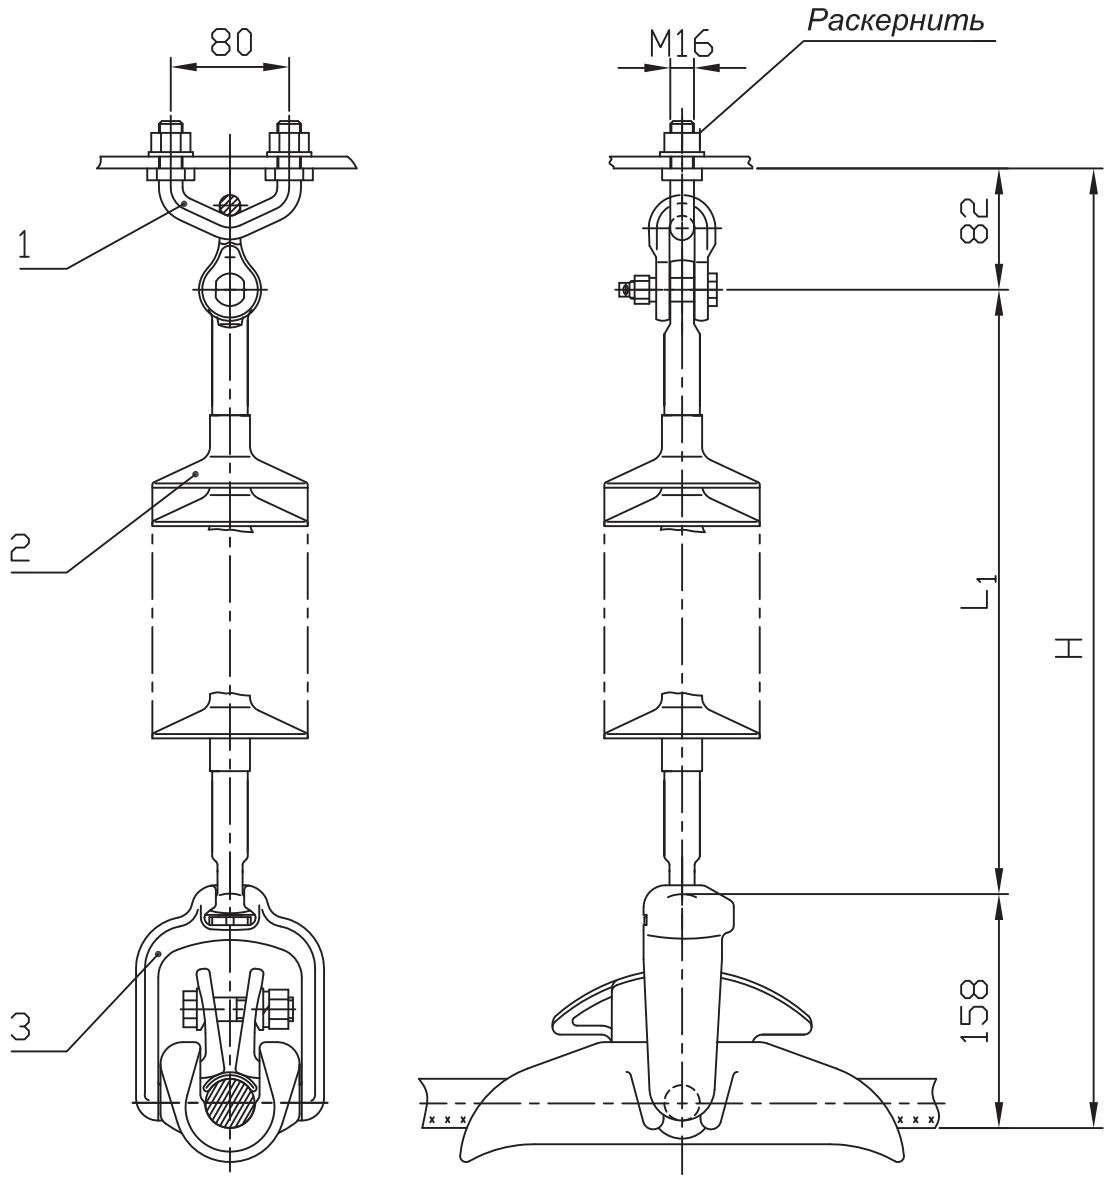

Поз.	Обозначение	Наименование	Кол.	Масса ед. кг	Прим.
1	КГП-7-1	Узел крепления	1	0,8	
2		Изолятор исп. СП	1	См. табл.	
3	ПГН-5-3	Зажим поддерживающ.	1	5,3	
Масса арматуры, кг				6,1	
Масса изолирующей подвески, кг				См. табл.	

Напряжение ВЛ, кВ	Изолятор, поз.2			Изолирующая подвеска	
	Тип	L_1, мм	Масса, кг	H, мм	Масса, кг
35	ЛК70/35	475	1,5	715	7,6
110	ЛК70/110	1175	3,5	1415	9,6

Взам. инв. N

Подп. и дата

Инв. N подл.

Утв.	Вигдергауз		
Пров.	Липунцов		
Разраб.	Власкина		

ЭСИП-0007


ЭСС.001 ТМ - т.1

Поддерживающие одноцепные изолирующие с полимерными изоляторами ряда 70 кН подвески проводов АС240/32, АС240/39 к промежуточным металлическим и ж/б опорам ВЛ 35, 110 кВ

Стадия	Лист	Листов
Р		1

Филиал ОАО "ФСК ЕЭС" "Электросетьсервис"

Формат А3

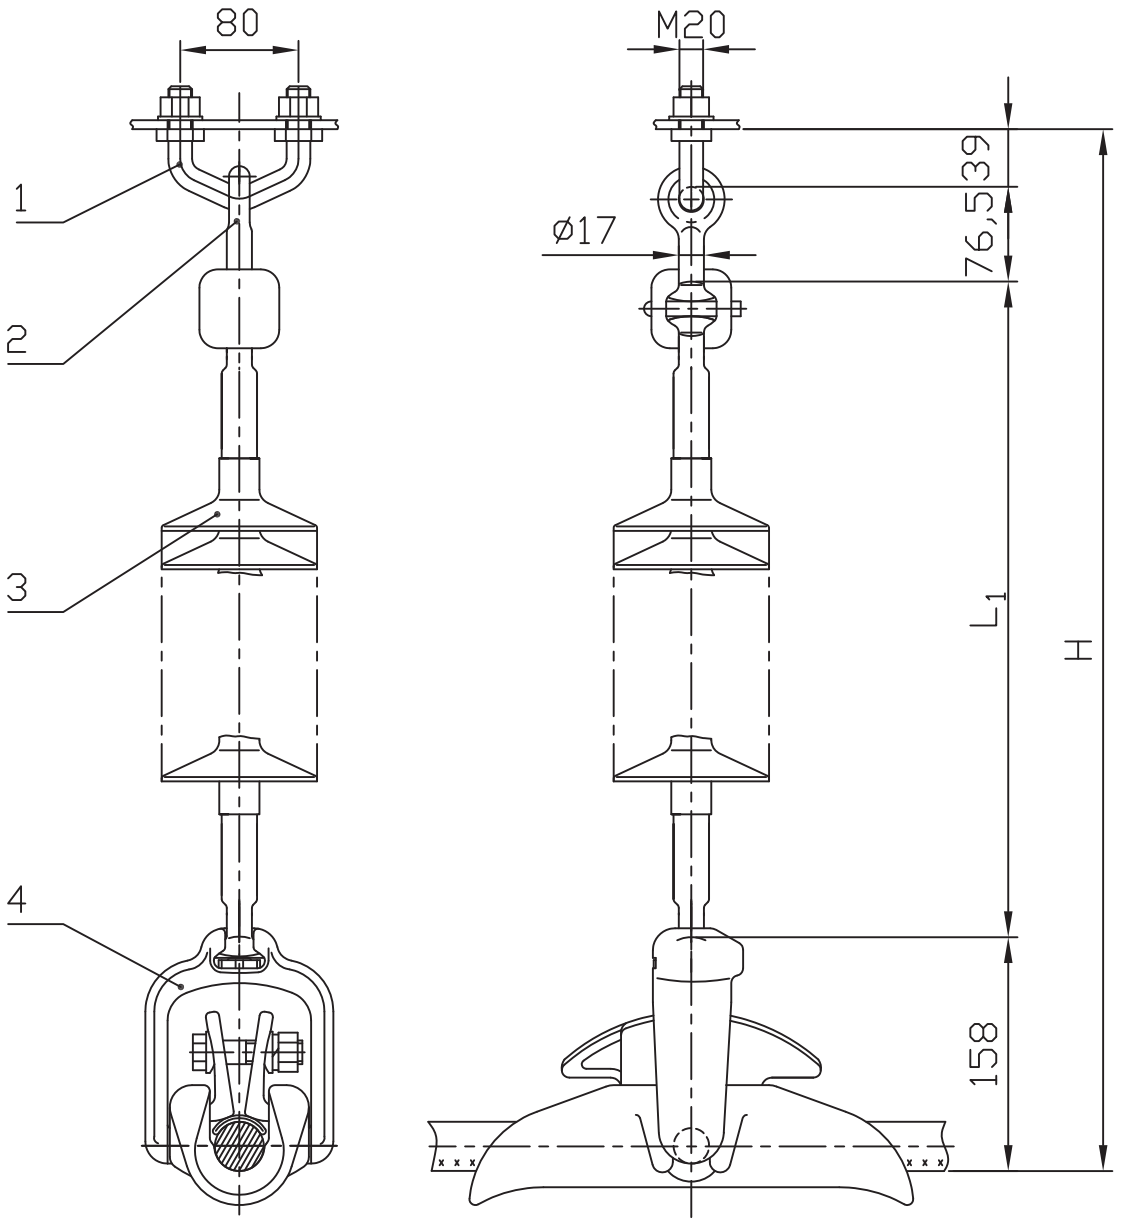

Поз.	Обозначение	Наименование	Кол.	Масса ед. кг	Прим.
1	КГП-16-3	Узел крепления	1	0,81	
2	СРС-7-16	Серьга специальная	1	0,32	
3		Изолятор исп. ГП	1	См. табл.	
4	ПГН-5-3	Зажим поддерживающ.	1	5,3	
Масса арматуры, кг				6,43	
Масса изолирующей подвески, кг				См. табл.	

Напряжение ВЛ, кВ	Провод по ГОСТ 839-80		Изолятор, поз.3			Изолирующая подвеска	
	Марка	Диаметр, мм	Тип	L_1, мм	Масса, кг	H, мм	Масса, кг
110	АС240/32, АС240/39, АС240/56	21,6 - 22,4	ЛК70/110	1213	3,5	1486,5	9,93
220	АС300/39, АС300/48, АС300/67, АС400/51, АС400/93, АС500/64	24,0 - 30,6	ЛК70/220	2060	8,0	2333,5	14,43*

* Масса указана с изолятором ЛК-70/220-3-ГП

Утв.	Вигдергауз		
Пров.	Липунцов		
Разраб.	Власкина		

ЭСИП-0008

ЭСС.001 ТМ - т.1


Поддерживающие одноцепные изолирующие с полимерными изоляторами ряда 70 кН подвески проводов к промежуточным металлическим и ж/б опорам 110 кВ, деревянным 110 и 220 кВ, металлическим и ж/б 220 кВ для обводки шлейфа

Стадия	Лист	Листов
Р		1

Филиал ОАО "ФСК ЕЭС" "Электросетьсервис"

Взам. инв. N | Подп. и дата | Инв. N подл.

Формат А3

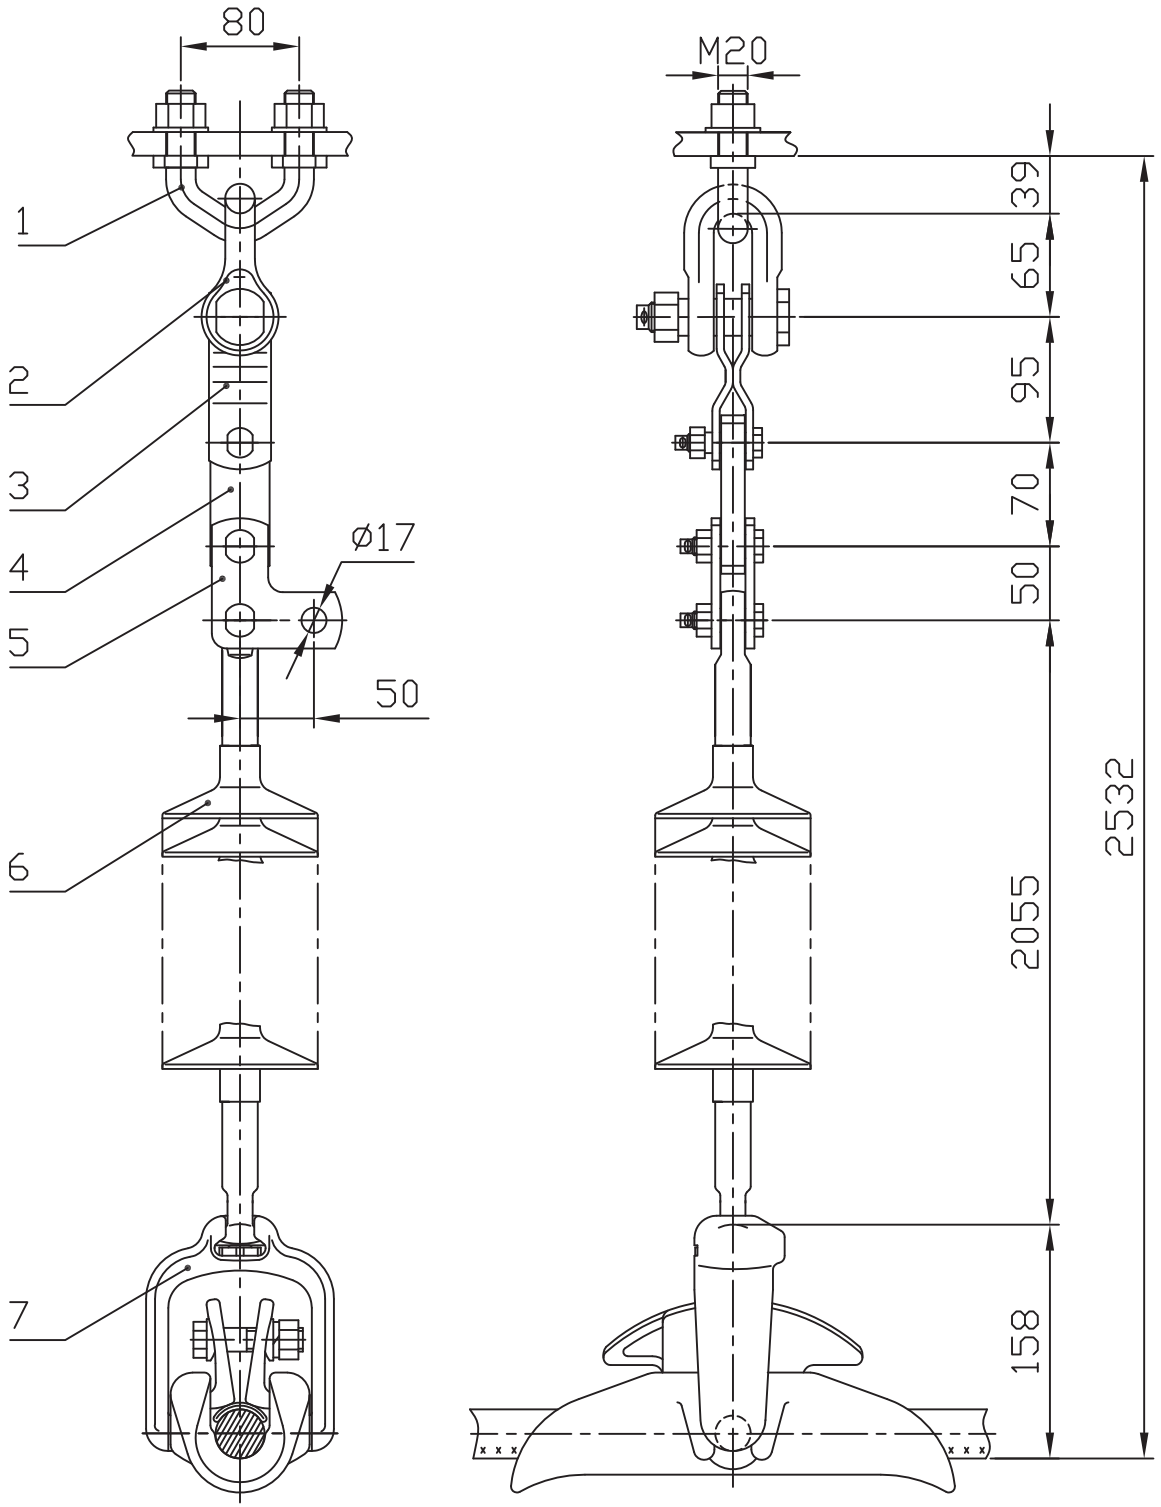

Поз.	Обозначение	Наименование	Кол.	Масса ед. кг	Прим.
1	КГП-16-3	Узел крепления	1	0,81	
2	СК-120-1Б	Скоба	1	0,92	
3	ПРТ12/7-2	Звено пром. переходное	1	0,7	
4	ПР-7-6	Звено пром. прямое	1	0,44	
5	ПТМ-7-3А	Звено пром. монтажное	1	0,63	
6	ЛК 70/220-	Изолятор исп. СП	1	8,0	
7	ПГН-5-3	Зажим поддерживающ.	1	5,3	
Масса арматуры, кг				8,8	
Масса изолирующей подвески, кг				16,8*	

* Масса указана с изолятором ЛК70/220-3-СП


Взам. инв. N

Подп. и дата

Инв. N подл.

		ЭСИП-0009	
		ЭСС.001 ТМ - т.1	
Утв.	Вигдергауз	Поддерживающие одноцепные изолирующие с полимерными изоляторами ряда 70 кН подвески проводов АС240/32 - АС500/64 к промежуточным металлическим опорам ВЛ 220 кВ	Стадия: Р; Лист: ; Листов: 1
Пров.	Липунцов		Филиал ОАО "ФСК ЕЭС" "Электросетьсервис"
Разраб.	Власкина		

Формат А3

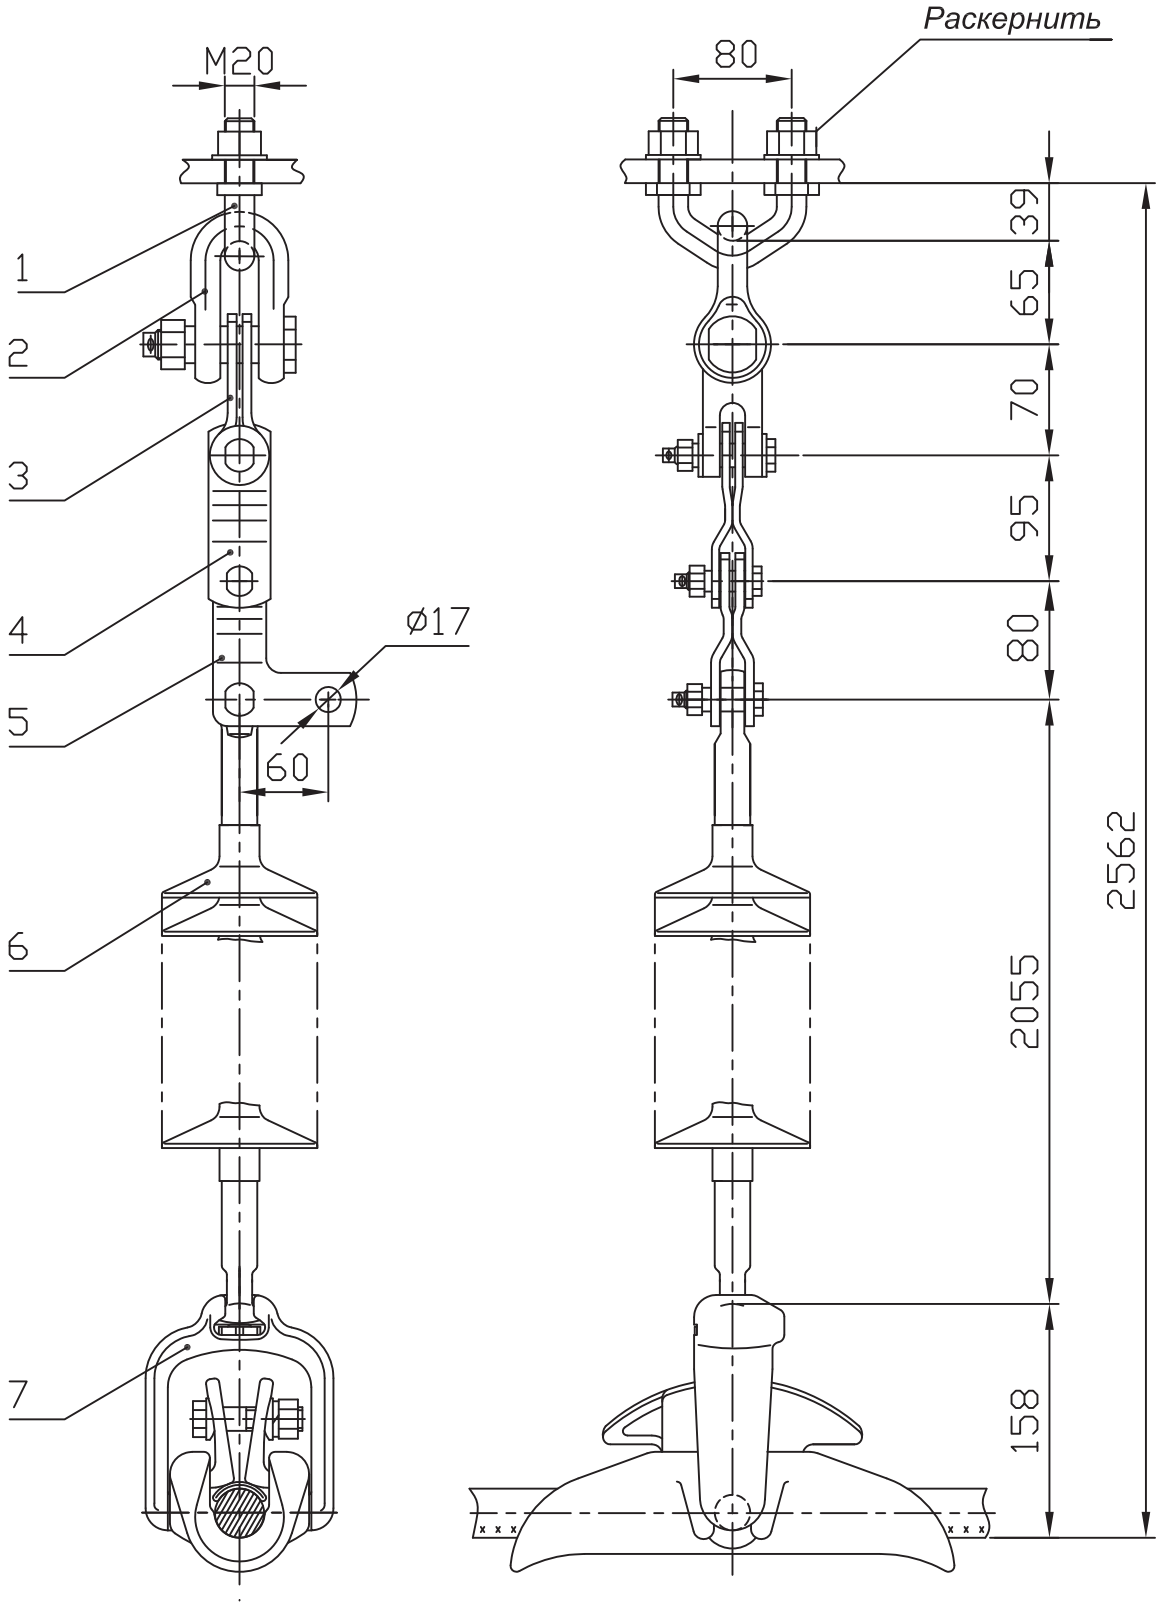

Поз.	Обозначение	Наименование	Кол.	Масса ед. кг	Прим.
1	КГП-16-3	Узел крепления	1	0,81	
2	СК-120-1Б	Узел крепления	1	0,92	
3	СКТ-12-1	Скоба трехлапчатая	1	0,93	
4	ПРТ-12/7-2	Звено пром. переходное	1	0,7	
5	ПТМ-7-2	Звено пром. монтажное	1	0,7	
6	ЛК 70/220-	Изолятор исп. СП	1	8,0	
7	ПГН-5-3	Зажим поддерживающ.	1	5,3	
Масса арматуры, кг				9,36	
Масса изолирующей подвески, кг				17,4*	

* Масса указана с изолятором ЛК70/220-3-СП

Взам. инв. N

Подп. и дата


Инв. N подл.

				ЭСИП-0010
				ЭСС.001 ТМ - т.1
Утв.	Вигдергауз			Поддерживающие одноцепные изолирующие с полимерными изоляторами ряда 70 кН подвески проводов АС240/32 - АС500/64 к промежуточным металлическим и ж/б опорам ВЛ 220 кВ
Пров.	Липунцов			
Разраб.	Власкина			

Стадия	Лист	Листов
Р		1

Филиал ОАО "ФСК ЕЭС" "Электросетьсервис"

Формат А3

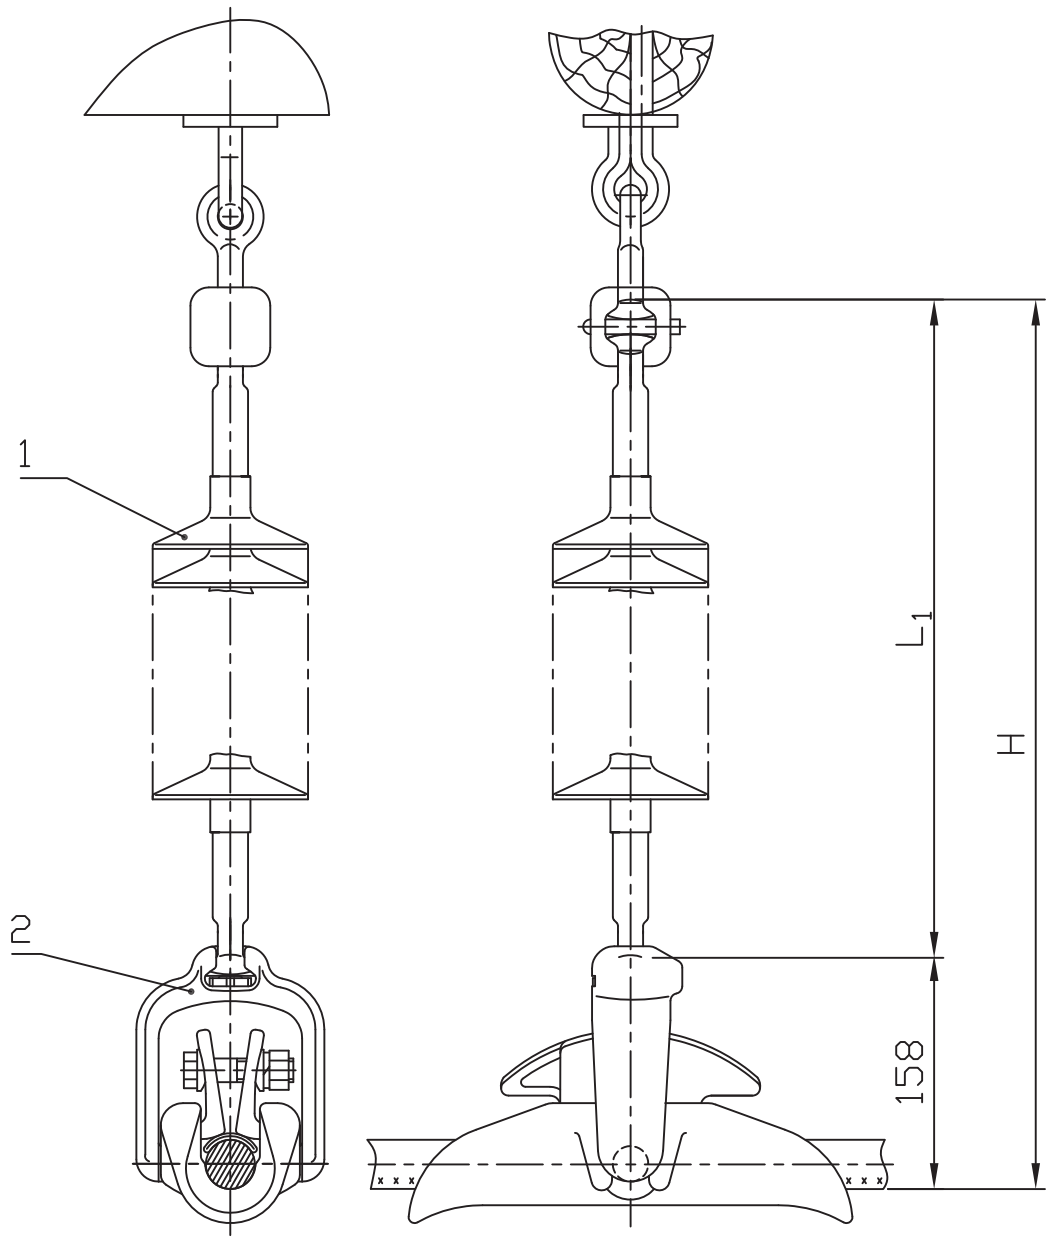

Поз.	Обозначение	Наименование	Кол.	Масса ед. кг	Прим.
1		Изолятор исп. ГП	1	См. табл.	
2	ПГН-5-3	Зажим поддерживающ.	1	5,3	
Масса арматуры, кг				5,3	
Масса изолирующей подвески, кг				См. талб.	


Напряжение ВЛ, кВ	Провод по ГОСТ 839-80		Изолятор, поз.1			Изолирующая подвеска	
	Марка	Диаметр, мм	Тип	L1, мм	Масса, кг	H, мм	Масса, кг
110	АС240/32, АС240/39, АС240/56	21,6 - 22,4	ЛК70/110	1213	3,5	1371	8,8
220	АС300/39, АС300/48, АС300/67, АС400/51, АС400/93, АС500/64	24,0 - 30,6	ЛК70/220	2060	8,0	2218	13,3*

* Масса указана с изолятором ЛК-70/220-3-ГП

				ЭСИП-0011		
				ЭСС.001 ТМ - т.1		
Утв.	Вигдергауз			Поддерживающие одноцепные изолирующие с полимерными изоляторами ряда 70 кН подвески проводов к промежуточным деревянным опорам ВЛ 110, 220 кВ	Стадия	Лист	Листов
					Р		1
Пров.	Липунцов				Филиал ОАО "ФСК ЕЭС" "Электросетьсервис"		
Разраб.	Власкина						

Взам. инв. N | Подп. и дата | Инв. N подл.

Формат А3

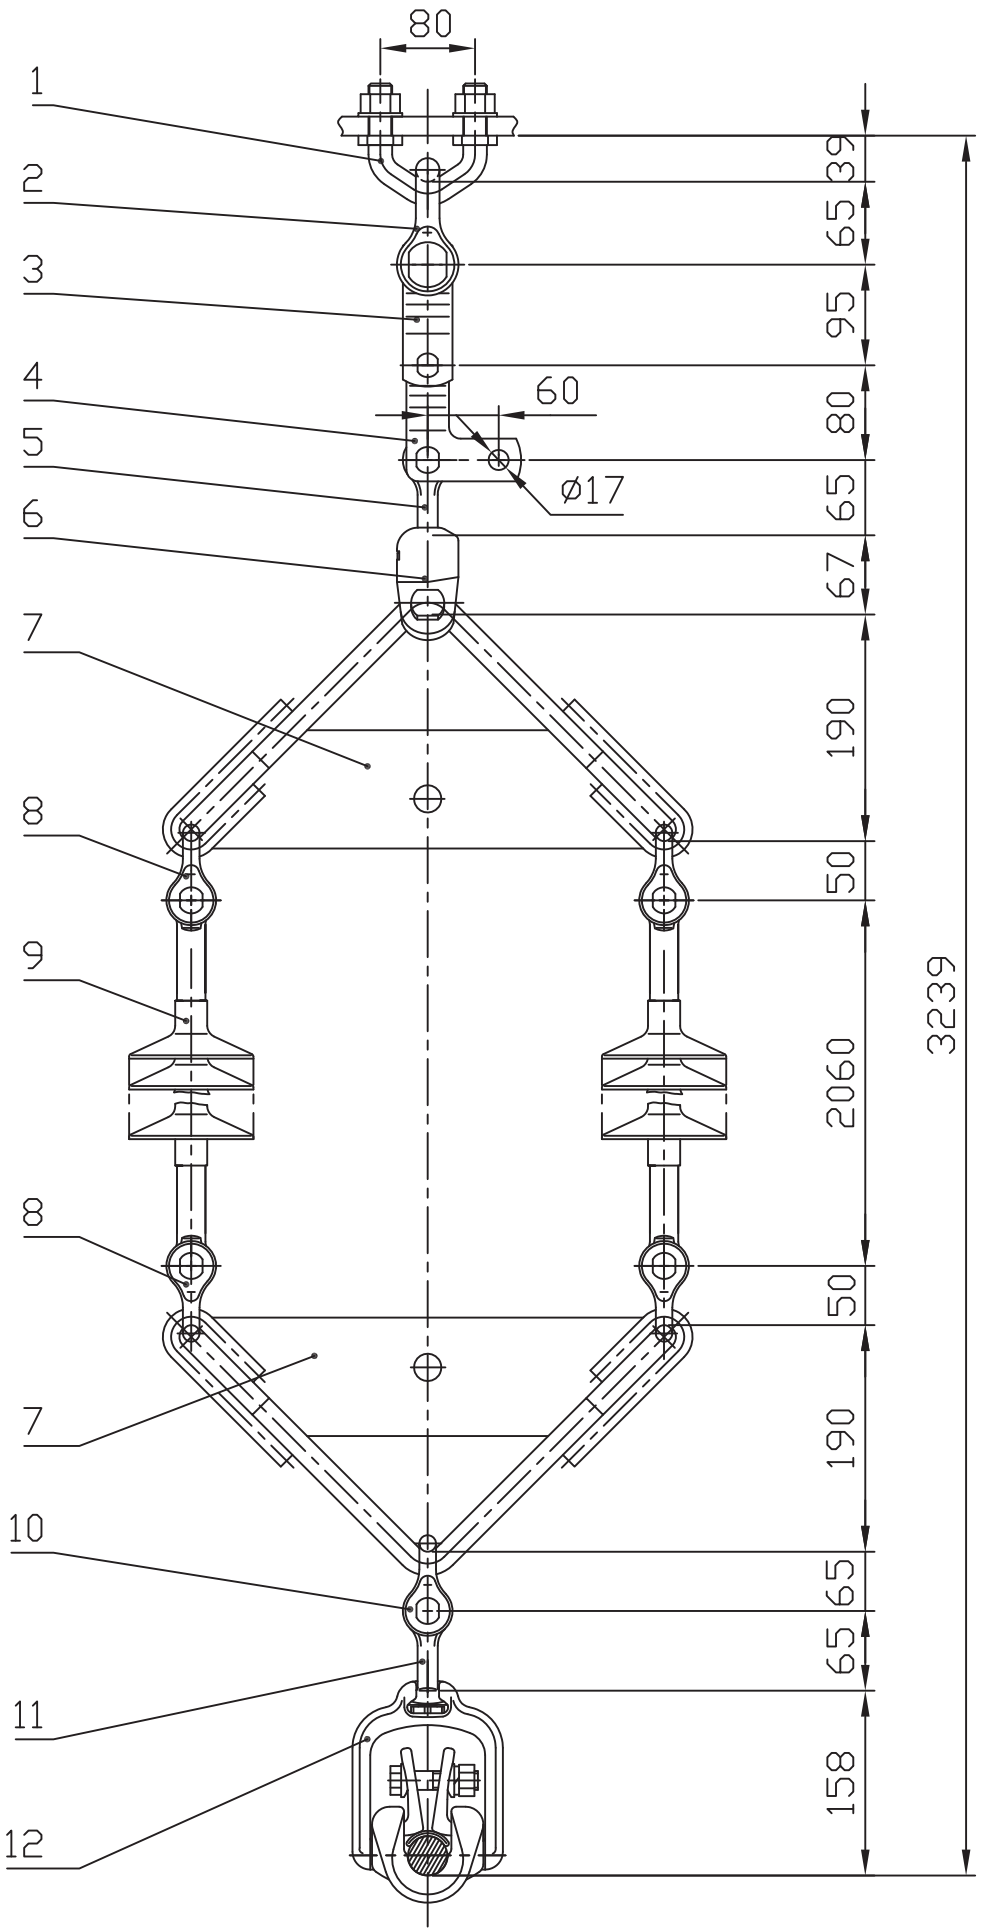


Поз.	Обозначение	Наименование	Кол.	Масса ед. кг	Прим.
1	КГП-16-3	Узел крепления	1	0,81	
2	СК-120-1Б	Скоба	1	0,92	
3	ПРТ12/7-2	Звено промеж. переходное	1	0,7	
4	ПТМ-7-2	Звено промеж. монтажное	1	0,7	
5	СР-7-16	Серьга	1	0,3	
6	УСК-7-16	Ушко спец. укороченое	1	1,2	
7	2КУ-12-1	Коромысло	2	4,75	
8	СК-70-1Б	Скоба	4	0,38	
9	ЛК 70/220-	Изолятор исп.СС	2	8,0	
10	СК-120-1Б	Скоба	1	0,92	
11	СР-12-16	Серьга	1	0,41	
12	ПГН-5-3	Зажим поддерживающ.	1	5,3	
Масса арматуры, кг				22,3	
Масса изолирующей подвески, кг				38,3*	

* Масса указана с изолятором ЛК 70/220-3-СС

		ЭСИП-0012	
		ЭСС.001 ТМ - т.1	
Утв.	Вигдергауз	Поддерживающие двухцепные изолирующие с полимерными изоляторами ряда 70 кН подвески проводов АС240/32 - АС500/64 к промежуточным металлическим опорам ВЛ 220 кВ	Стадия: Р; Лист: ; Листов: 1
Пров.	Липунцов		Филиал ОАО "ФСК ЕЭС" "Электросетьсервис"
Разраб.	Власкина		

Взам. инв. N | Подп. и дата | Инв. N подл.

Формат А3

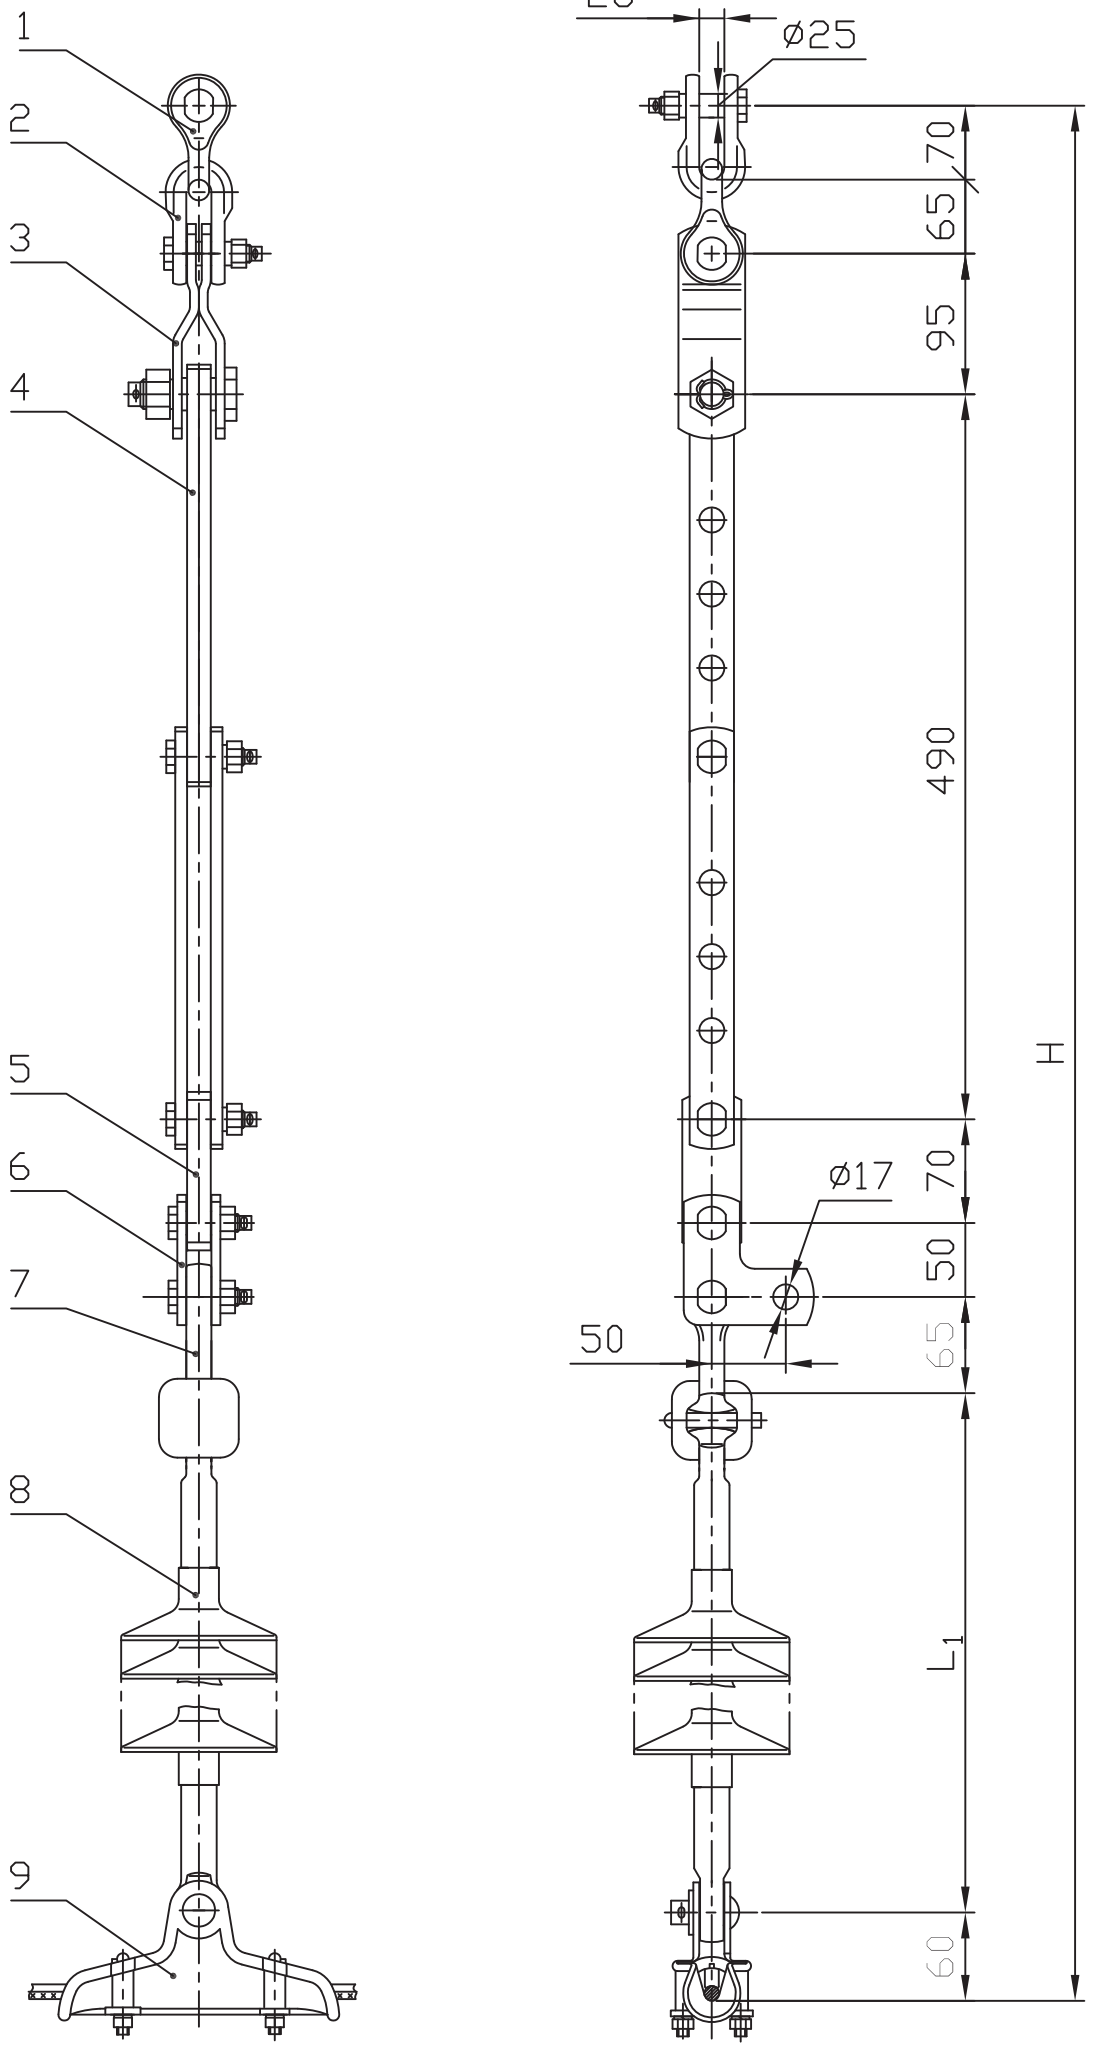

Поз.	Обозначение	Наименование	Кол.	Масса ед. кг	Прим.
1	СК-16-1А	Скоба	1	1,22	
2	СК-120-1Б	Скоба	1	0,92	
3	ПРТ-12/7-2	Звено пром. переходное	1	0,7	
4	ПРР-7-1	Звено пром. регулируемое	1	1,91	
5	ПР-7-6	Звено пром. прямое	1	0,44	
6	ПТМ-7-3А	Звено пром. монтажное	1	0,63	
7		Изолятор исп. ГС	1	См. табл.	
8	ПГ-25/6-12	Зажим поддерживающ.	1	1,01	
9	СР-7-16	Серьга	1	0,3	
Масса арматуры, кг				7,13	
Масса изолирующей подвески, кг				См. табл.	

Напряжение ВЛ, кВ	Изолятор, поз. 7			Изолирующая подвеска	
	Тип	L1, мм	Масса, кг	H, мм	Масса, кг
35	ЛК70/35	513	1,5	1478	8,6
110	ЛК70/110	1213	3,5	2178	10,6

Взам. инв. N

Подп. и дата

Инв. N подл.

Утв.	Вигдергауз		
Пров.	Липунцов		
Разраб.	Власкина		

ЭСИП-0013


ЭСС.001 ТМ - т.1


Поддерживающие одноцепные изолирующие с полимерными изоляторами ряда 70 кН подвески провода АС70/11 для оттяжки шлейфа на соседнюю стойку ВЛ 35, 110 кВ

Стадия	Лист	Листов
Р		1

Филиал ОАО "ФСК ЕЭС" "Электросетьсервис"

Формат А3

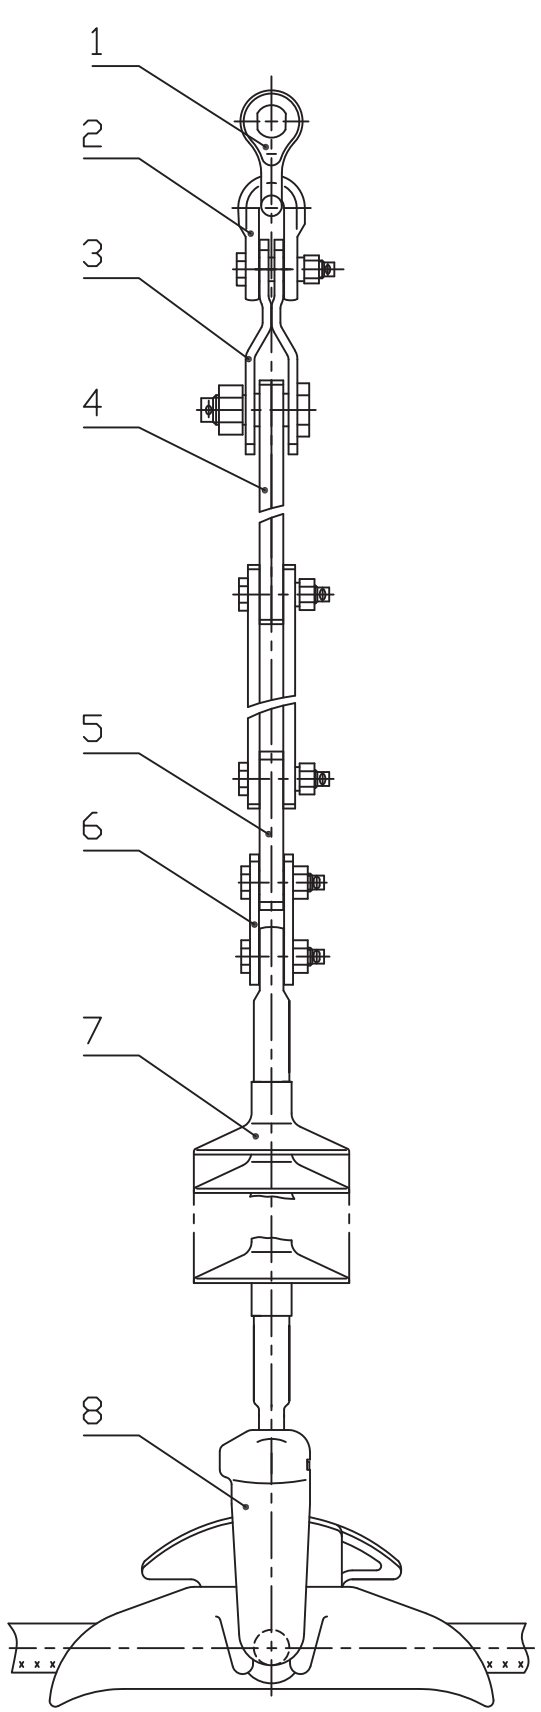

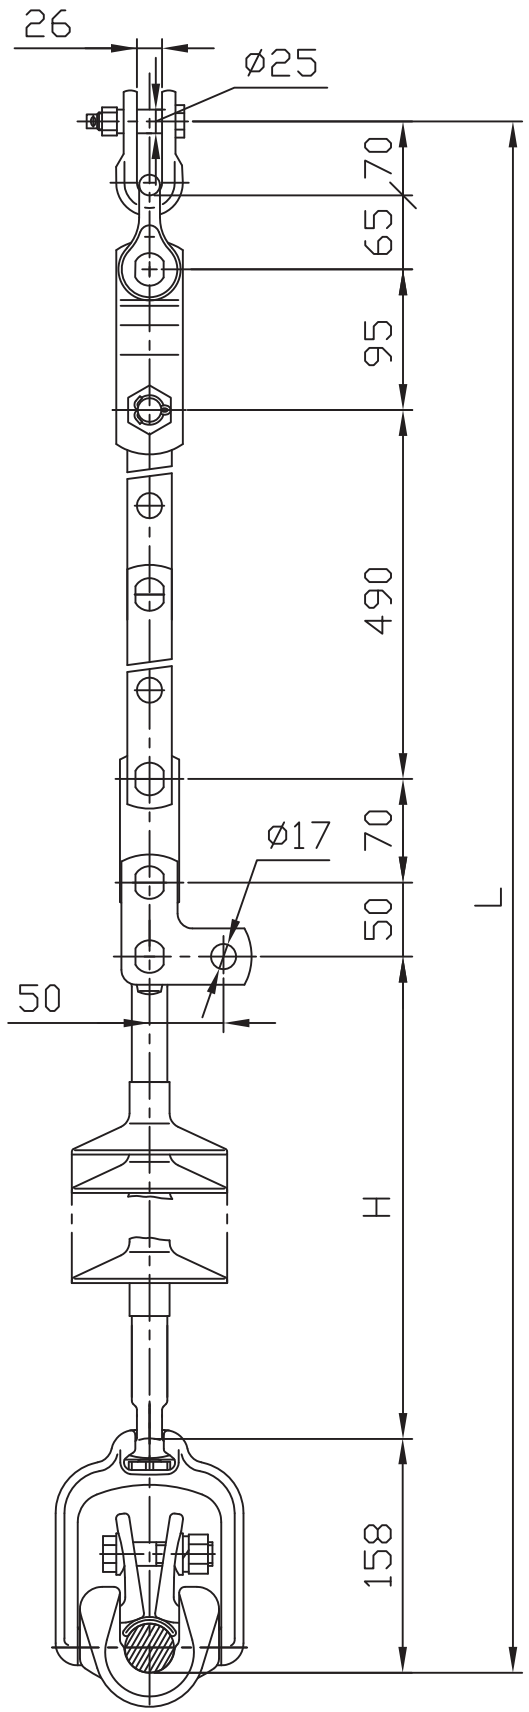

Поз.	Обозначение	Наименование	Кол.	Масса ед. кг	Прим.
1	СК-16-1А	Скоба	1	1,22	
2	СК-120-1Б	Скоба	1	0,92	
3	ПРТ-12/7-2	Звено пром. переходное	1	0,7	
4	ПРР-7-1	Звено пром. регулируемое	1	1,91	
5	ПР-7-6	Звено пром. прямое	1	0,44	
6	ПТМ-7-3А	Звено пром. монтажное	1	0,63	
7		Изолятор исп. СП	1	См. табл.	
8	ПГН-5-3	Зажим поддерживающ.	1	5,3	
Масса арматуры, кг				11,12	
Масса изолирующей подвески, кг				См. табл.	

* Масса указана с изолятором ЛК 70/220-3-СП

Напряжение ВЛ, кВ	Изолятор, поз. 7			Изолирующая подвеска	
	Тип	L1, мм	Масса, кг	H, мм	Масса, кг
110	ЛК70/110	1213	3,5	2211	14,6
220	ЛК70/220	2060	8,0	3058	19,1*

Утв.	Вигдергауз		
Пров.	Липунцов		
Разраб.	Власкина		

ЭСИП-0014

ЭСС.001 ТМ - т.1

Поддерживающие одноцепные изолирующие с полимерными изоляторами ряда 70 кН подвески провода АС240/32 - АС240/39 для оттяжки шлейфа на соседнюю стальную и ж/б стойку ВЛ 110,220 кВ

Стадия	Лист	Листов
Р		1


Филиал ОАО "ФСК ЕЭС" "Электросетьсервис"

Взам. инв. N

Подп. и дата

Инв. N подл.

Формат А3

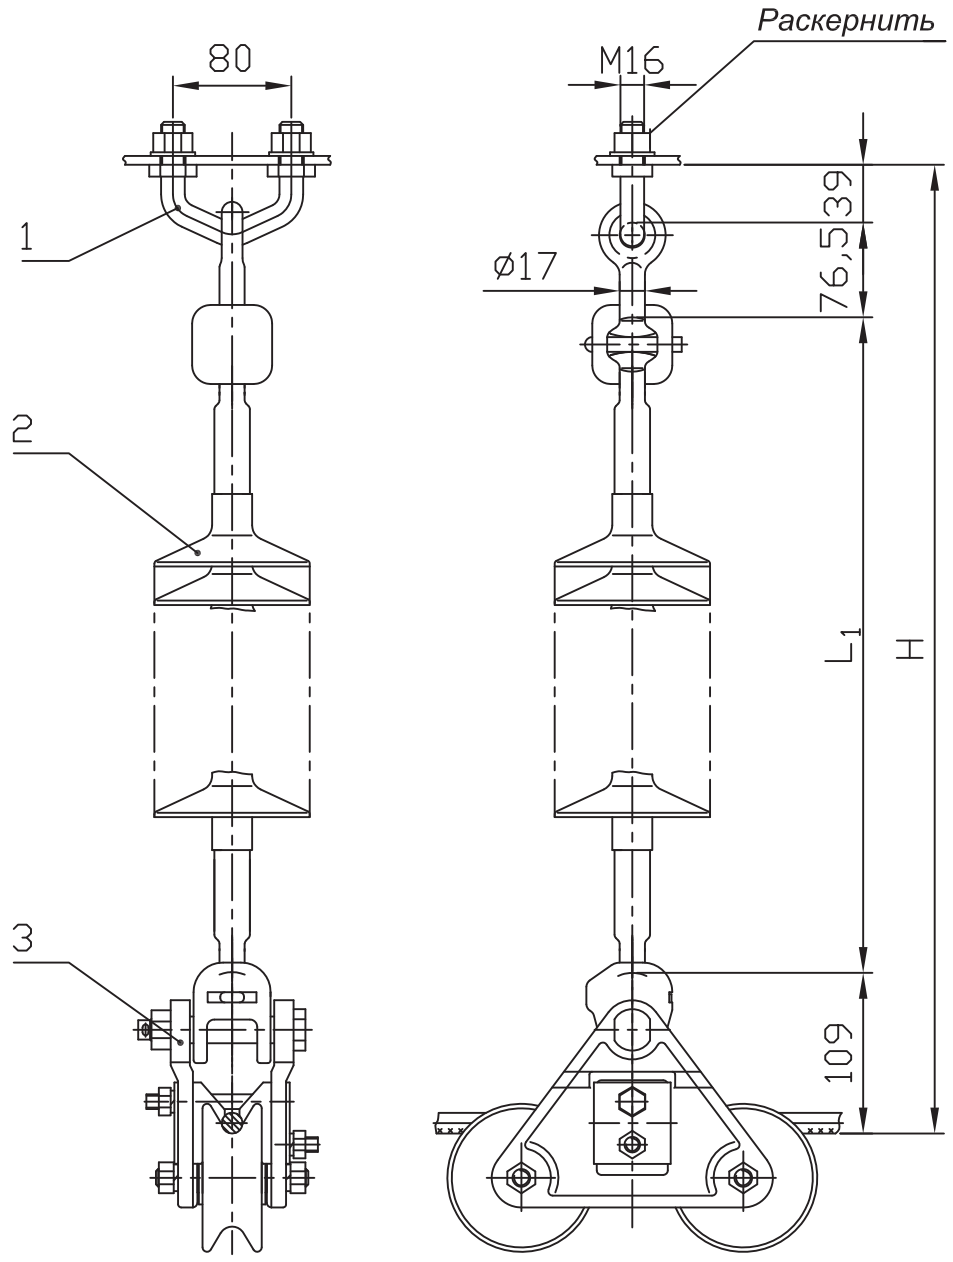


Поз.	Обозначение	Наименование	Кол.	Масса ед. кг	Прим.
1	КГП-7-2В	Узел крепления	1	0,7	
2		Изолятор исп. ГП	1	См. табл.	
3	ПГУ-2-1	Зажим поддерживающ.	1	3,1	
Масса арматуры, кг				3,8	
Масса изолирующей подвески, кг				См табл.	

Напряжение ВЛ, кВ	Провод по ГОСТ 839-80		Зажим, поз.3 комплектуется плашками	Изолятор, поз.2			Изолирующая подвеска	
	Марка	Диаметр, мм		Тип	L1, мм	Масса, кг	H, мм	Масса, кг
35	АС70/11	11,4 - 13,5	ПГУ-2-1-0-2А	ЛК70/35	513	1,5	737,5	5,3
	АС95/16							
	АС120/19	15,2 - 21,6	ПГУ-2-1-0-2Б					
110	АС150/24			ЛК70/110	1213	3,5	1437,5	7,3
	АС185/29							
	АС240/32							
	АС240/39							

		ЭСИП-0015	
		ЭСС.001 ТМ - т.1	
Утв.	Вигдергауз	Поддерживающие одноцепные изолирующие с полимерными изоляторами ряда 70 кН подвески проводов к металлическим и ж/б промежуточно-угловым опорам ВЛ 35, 110 кВ	Стадия: Р; Лист: ; Листов: 1
Пров.	Липунцов		Филиал ОАО "ФСК ЕЭС" "Электросетьсервис"
Разраб.	Власкина		

Взам. инв. N | Подп. и дата | Инв. N подл.

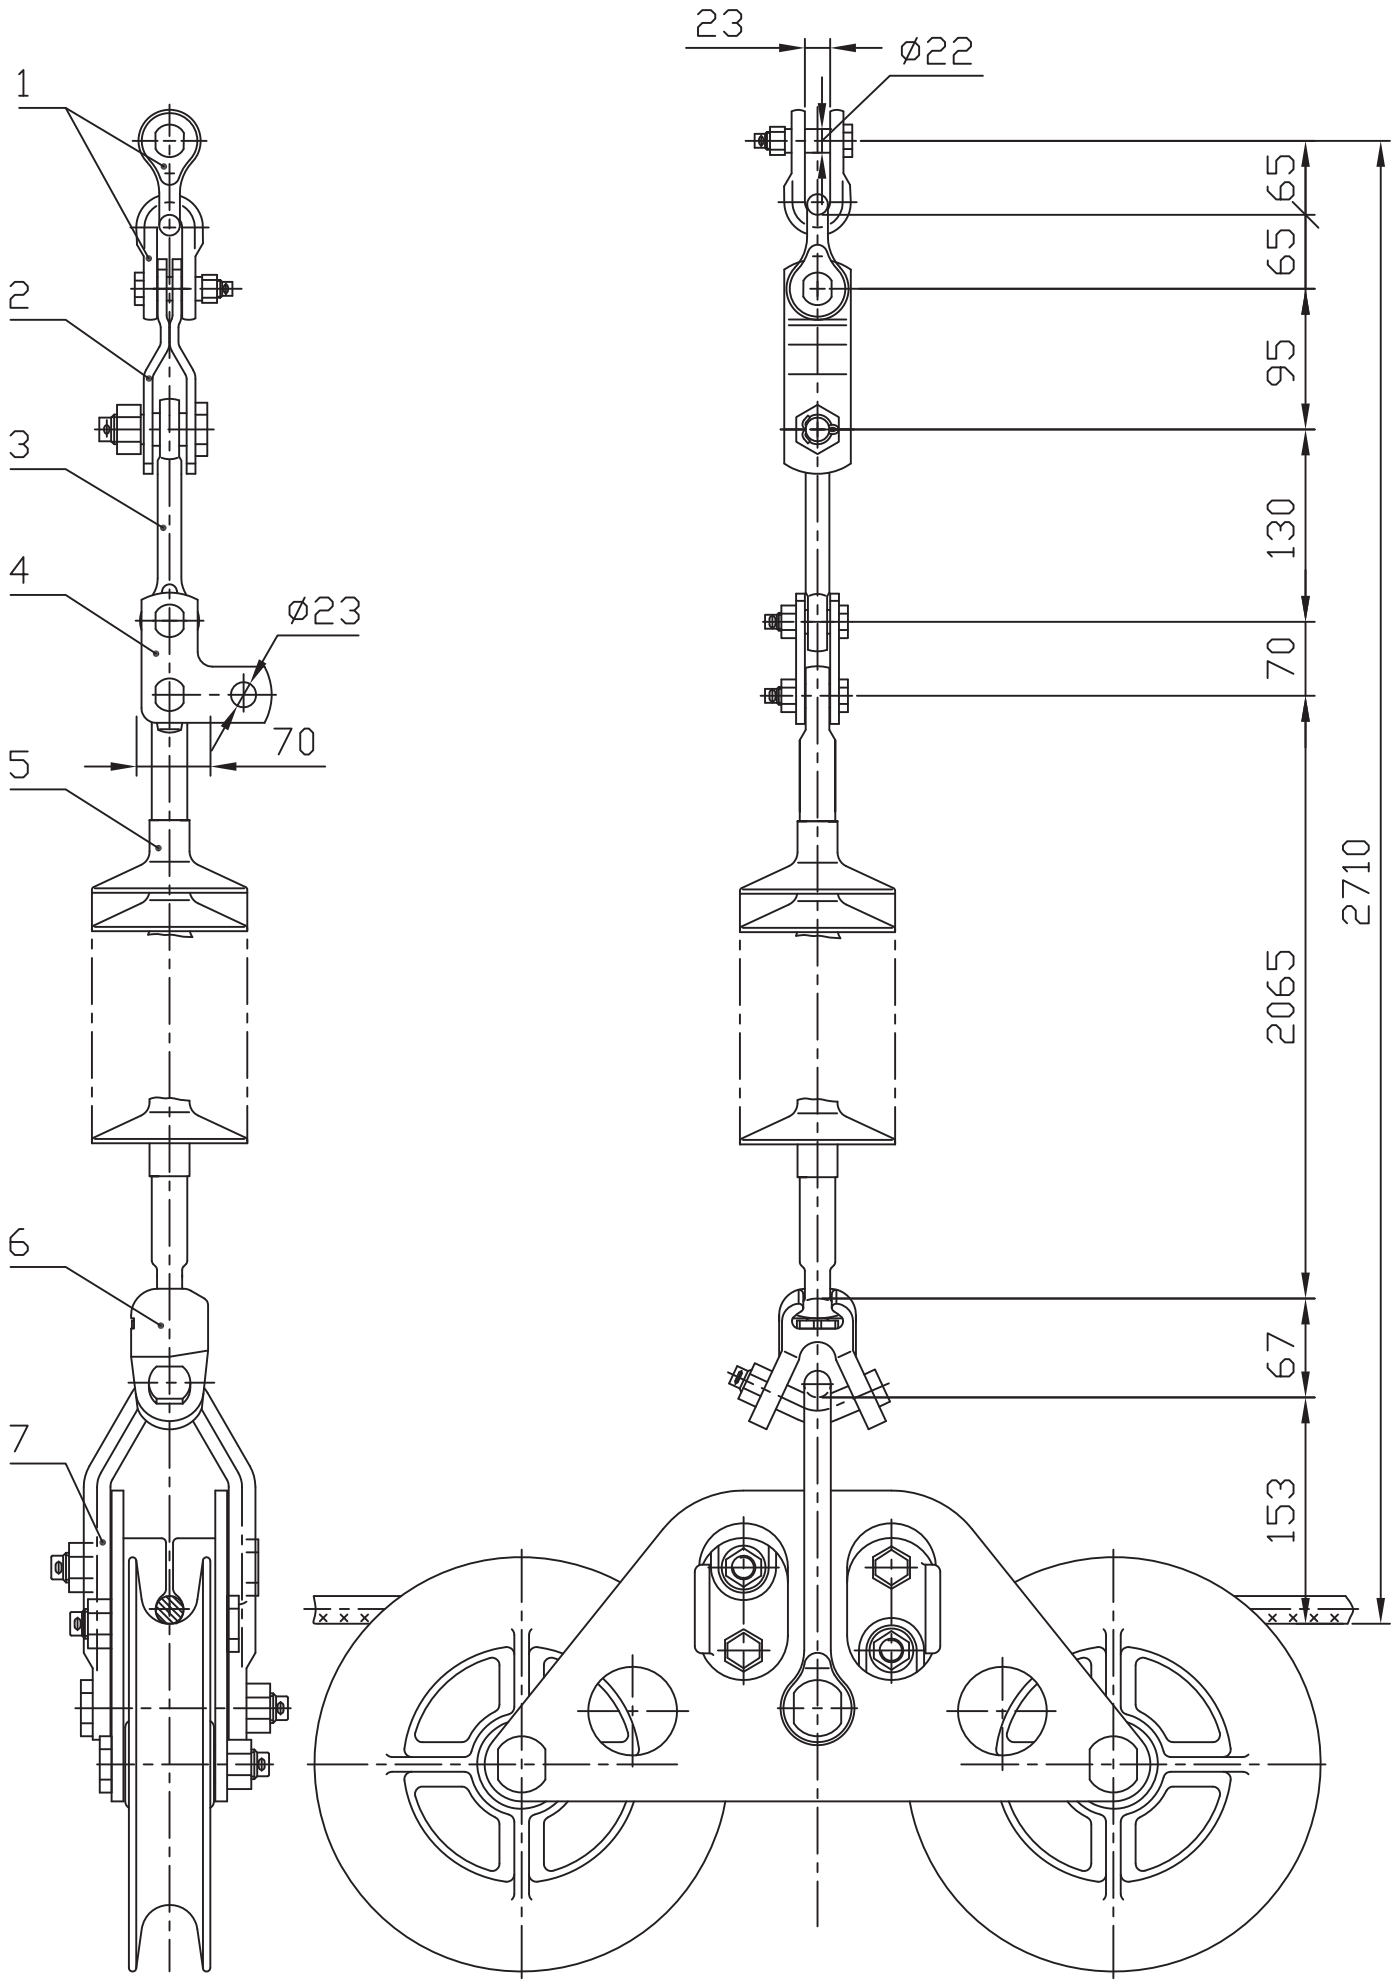

Поз.	Обозначение	Наименование	Кол.	Масса ед. кг	Прим.
1	СК-120-1Б	Скоба	2	0,92	
2	ПРТ-12/7-2	Звено переходное	1	0,7	
3	ПРВ-7-1	Звено пром. вывернутое	1	0,43	
4	ПТМ-7-3А	Звено пром. монтажное	1	0,63	
5	ЛК 70/220-	Изолятор исп. СП	1	8,0	
6	УСК-7-16	Ушко спец. укороченное	1	1,2	
7	ПГУ-5-1	Зажим поддерживающ.	1	13,8	
Масса арматуры, кг				18,6	
Масса изолирующей подвески, кг				26,6*	

* Масса указана с изолятором ЛК 70/220-3-СП

Взам. инв. N

Подп. и дата

Инв. N подл.

Утв.	Вигдергауз		
Пров.	Липунцов		
Разраб.	Власкина		

ЭСИП-0016


ЭСС.001 ТМ - т.1


Поддерживающие одноцепные изолирующие с полимерными изоляторами ряда 70 кН подвески проводов АС240/32 - АС500/64 к промежуточно-угловым опорам ВЛ 220 кВ

Стадия	Лист	Листов
Р		1

Филиал ОАО "ФСК ЕЭС" "Электросетьсервис"

Формат А3

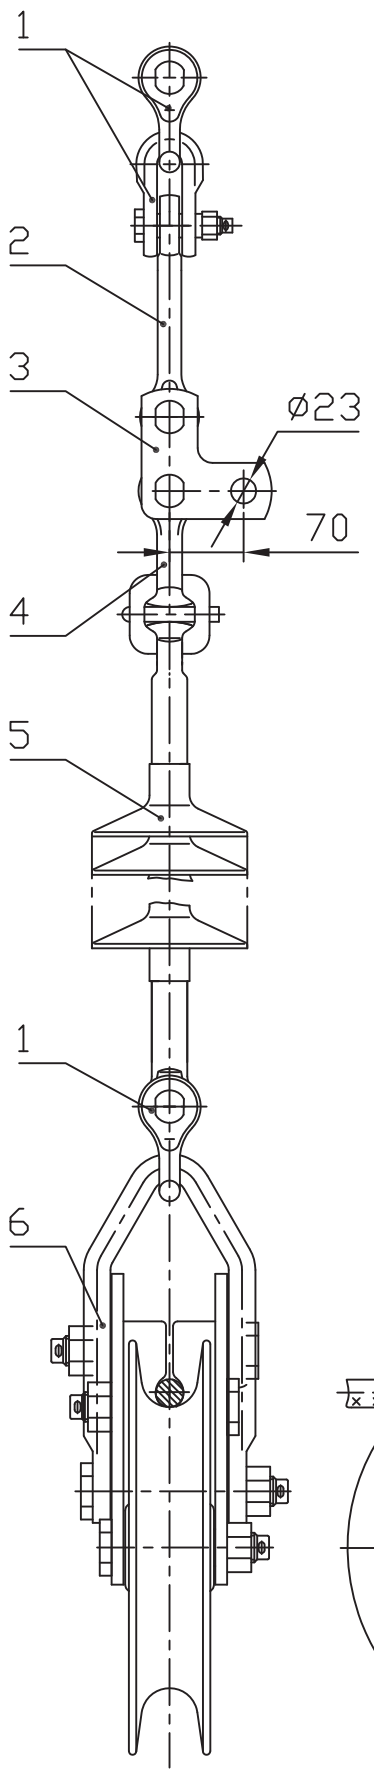

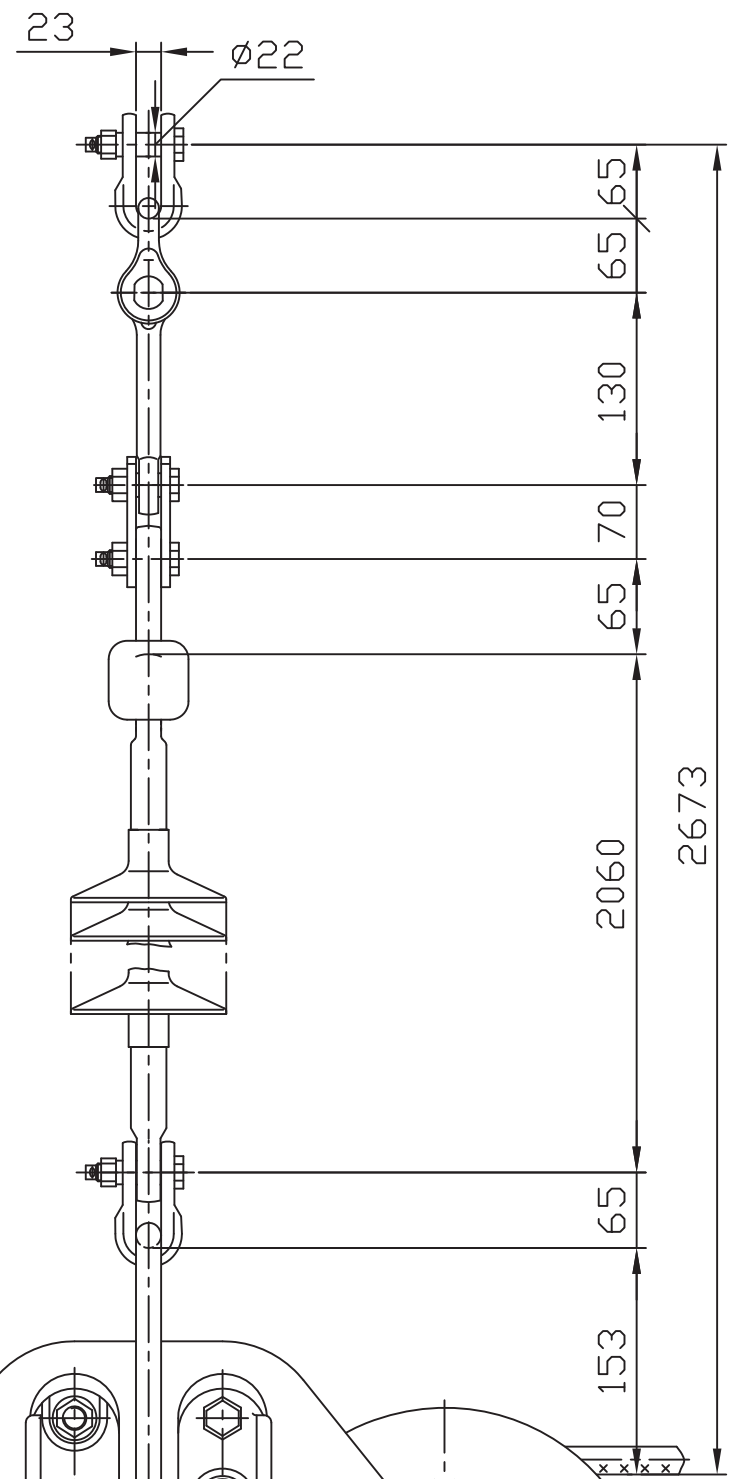

Поз.	Обозначение	Наименование	Кол.	Масса ед. кг	Прим.
1	СК-120-1Б	Скоба	3	0,92	
2	ПРВ-12-1	Звено пром. вывернутое	1	0,74	
3	ПТМ-12-3А	Звено пром. монтажное	1	1,7	
4	СР-12-16	Серьга	1	0,41	
5	ЛК 120/220-	Изолятор исп. ГС	1	8,0	
6	ПГУ-5-1	Зажим поддерживающ.	1	13,8	
Масса арматуры, кг				19,41	
Масса изолирующей подвески, кг				27,41*	

* Масса указана с изолятором ЛК 120/220-3-ГС


Взам. инв. N


Подп. и дата

Инв. N подл.

Утв.	Вигдергауз	ЭСИП-0017	
		ЭСС.001 ТМ - т.1	
Пров.	Липунцов	Поддерживающие одноцепные изолирующие с полимерными изоляторами ряда 120 кН подвески проводов АС240/32 - АС500/64 к промежуточно-угловым опорам ВЛ 220 кВ	Стадия: Р; Лист: ; Листов: 1
Разраб.	Власкина		Филиал ОАО "ФСК ЕЭС" "Электросетьсервис"

Формат А3

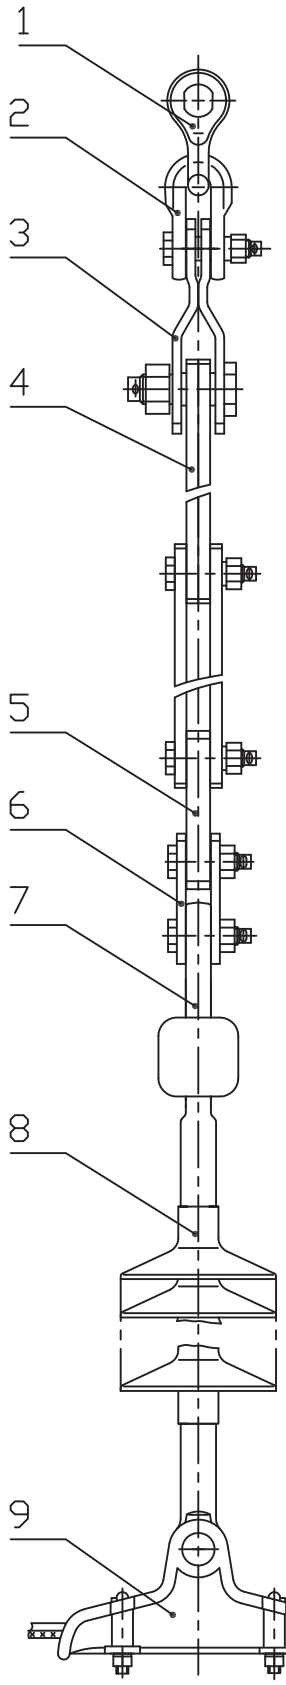

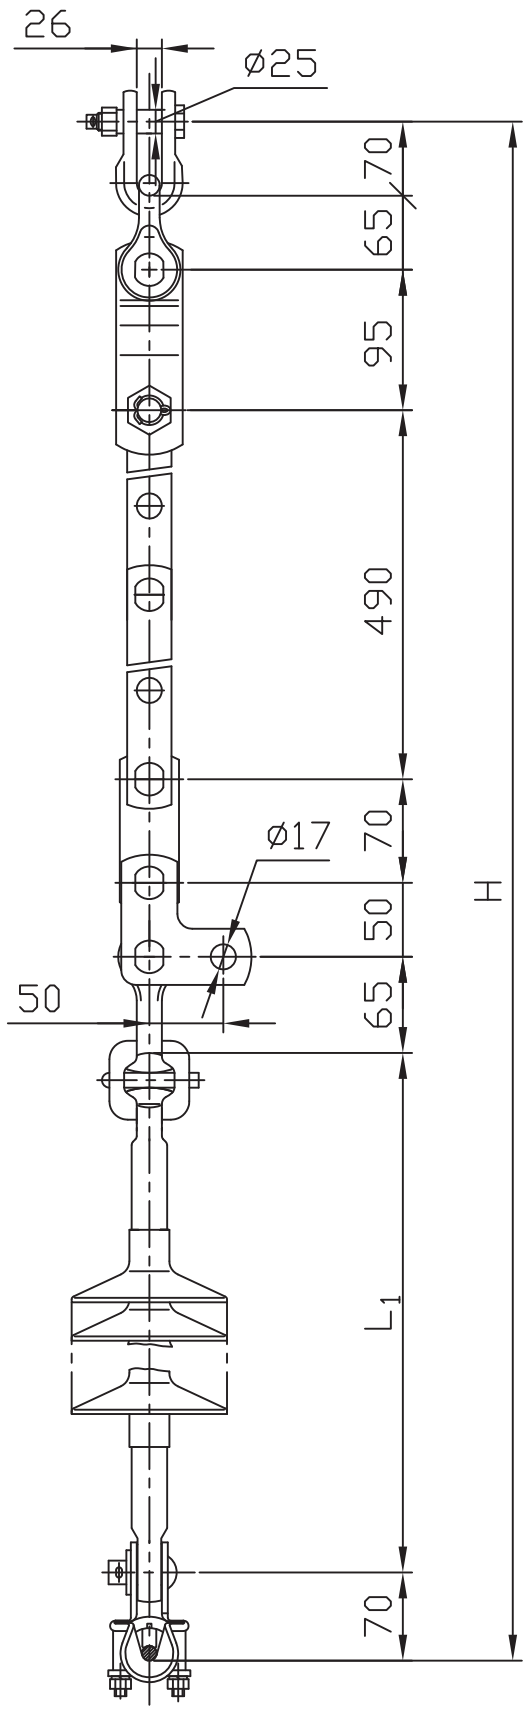

Поз.	Обозначение	Наименование	Кол.	Масса ед. кг	Прим.
1	СК-16-1А	Скоба	1	1,22	
2	СК-120-1Б	Скоба	1	0,92	
3	ПРТ-12/7-2	Звено пром. переходное	1	0,7	
4	ПРР-7-1	Звено пром. регулируемое	1	1,91	
5	ПР-7-6	Звено пром. прямое	1	0,44	
6	ПТМ-7-3А	Звено пром. монтажное	1	0,63	
7	СР-7-16	Серьга	1	0,3	
8		Изолятор исп. ГС	1	См. табл.	
9	ПГ-30/12-20	Зажим поддерживающ.	1	1,07	
Масса арматуры, кг				7,19	
Масса изолирующей подвески, кг				См. табл.	

Напряжение ВЛ, кВ	Провод по ГОСТ 839-80		Изолятор, поз.8			Изолирующая подвеска	
	Марка	Диаметр, мм	Тип	L1, мм	Масса, кг	H, мм	Масса, кг
35	АС95/16, АС120/19, АС150/24	13,5 - 17,5	ЛК70/35	513	1,5	1488	8,7
110	АС185/29	18,8	ЛК70/110	1213	3,5	2188	10,7


Взам. инв. N


Подп. и дата

Инв. N подл.

				ЭСИП-0018
				ЭСС.001 ТМ - т.1
Утв.	Вигдергауз			Поддерживающие одноцепные изолирующие с полимерными изоляторами ряда 70 кН подвески провода АС95/16 - АС185/29 для оттяжки шлейфа на соседнюю стальную и ж/б стойку ВЛ 35, 110 кВ
Пров.	Липунцов			Стадия: Р; Лист: ; Листов: 1
Разраб.	Власкина			Филиал ОАО "ФСК ЕЭС" "Электросетьсервис"

Формат А3

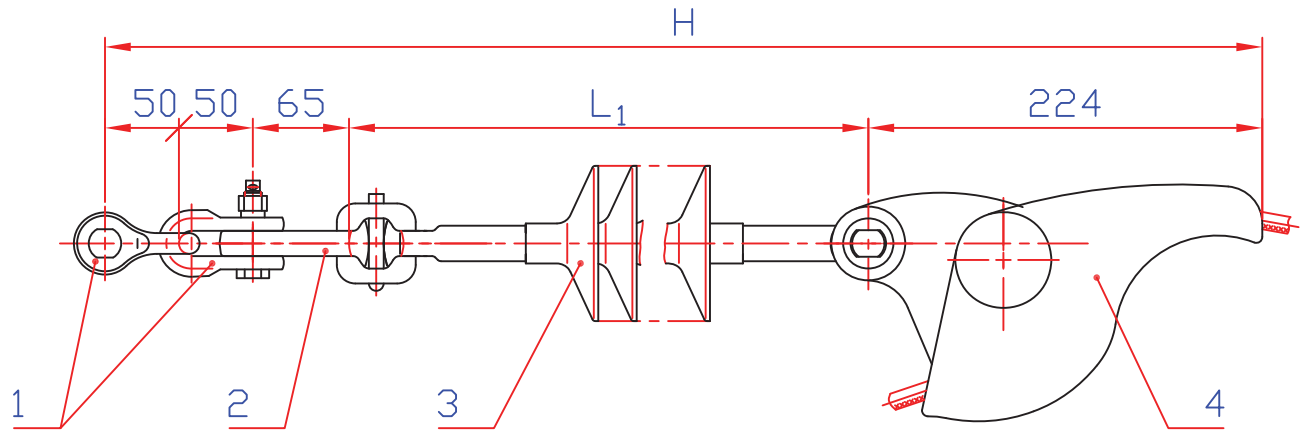

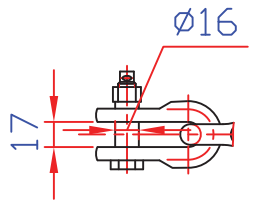

Поз.	Обозначение	Наименование	Кол.	Масса ед. кг	Прим.
1	СК-70-1Б	Скоба	2	0,38	
2	СР-7-16	Серьга	1	0,3	
3		Изолятор исп. ГС	1	См. табл.	
4	НЗ-60/11-17	Зажим натяжной	1	1,5	
Масса арматуры, кг				2,56	
Масса изолирующей подвески, кг				См. табл.	

Напряжение ВЛ, кВ	Изолятор, поз.3			Изолирующая подвеска	
	Тип	L_1, мм	Масса, кг	H, мм	Масса, кг
35	ЛК70/35	513	1,5	902	4,1
110	ЛК70/110	1213	3,5	1602	6,1


Взам. инв. N


Подп. и дата

Инв. N подл.

				ЭСИП-0019	
				ЭСС.001 ТМ - т.1	
Утв.	Вигдергауз			Натяжные одноцепные изолирующие с полимерными изоляторами ряда 70 кН подвески проводов АС70/11 - АС150/24 к а/у металлическим, ж/б и деревянным опорам ВЛ 35, 110 кВ	Стадия: Р; Лист: ; Листов: 1
Пров.	Липунцов				Филиал ОАО "ФСК ЕЭС" "Электросетьсервис"
Разраб.	Власкина				

Формат А3

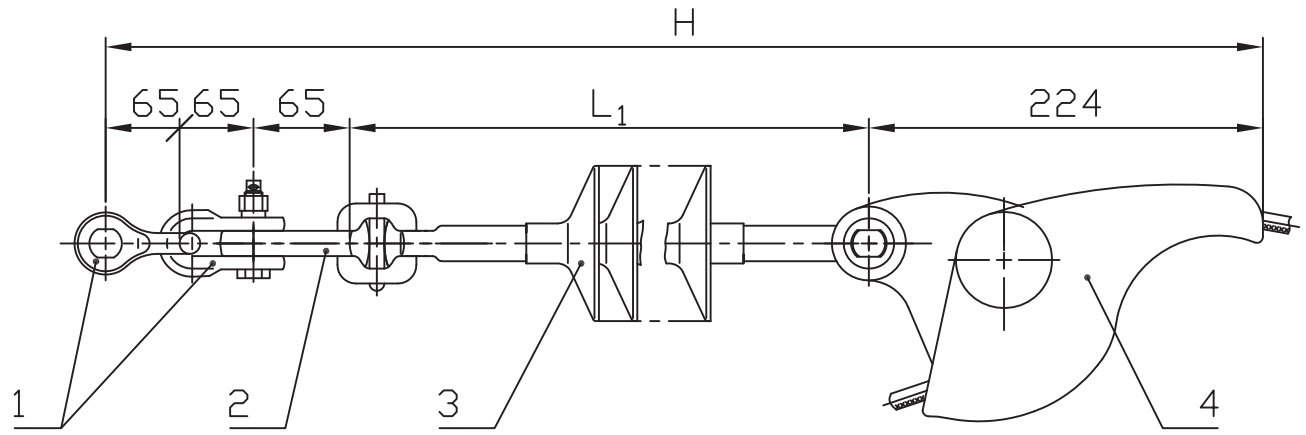

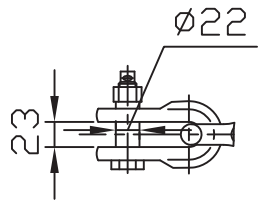

Поз.	Обозначение	Наименование	Кол.	Масса ед. кг	Прим.
1	СК-120-1Б	Скоба	2	0,92	
2	СР-12-16	Серьга	1	0,41	
3		Изолятор исп. ГС	1	См. табл.	
4	НЗ-60/11-17	Зажим натяжной	1	1,5	
Масса арматуры, кг				3,75	
Масса изолирующей подвески, кг				См. табл.	

Напряжение ВЛ, кВ	Изолятор, поз.3			Изолирующая подвеска	
	Тип	L1, мм	Масса, кг	H, мм	Масса, кг
35	ЛК70/35	513	1,5	932	5,3
110	ЛК70/110	1213	3,5	1632	7,3


Взам. инв. N


Подп. и дата

Инв. N подл.

				ЭСИП-0020	
				ЭСС.001 ТМ - т.1	
Утв.	Вигдергауз			Натяжные одноцепные изолирующие с полимерными изоляторами ряда 70 кН подвески проводов АС70/11 - АС150/24 к а/у металлическим и ж/б опорам ВЛ 35, 110 кВ	Стадия: Р; Лист: ; Листов: 1
Пров.	Липунцов				Филиал ОАО "ФСК ЕЭС" "Электросетьсервис"
Разраб.	Власкина				

Формат А3

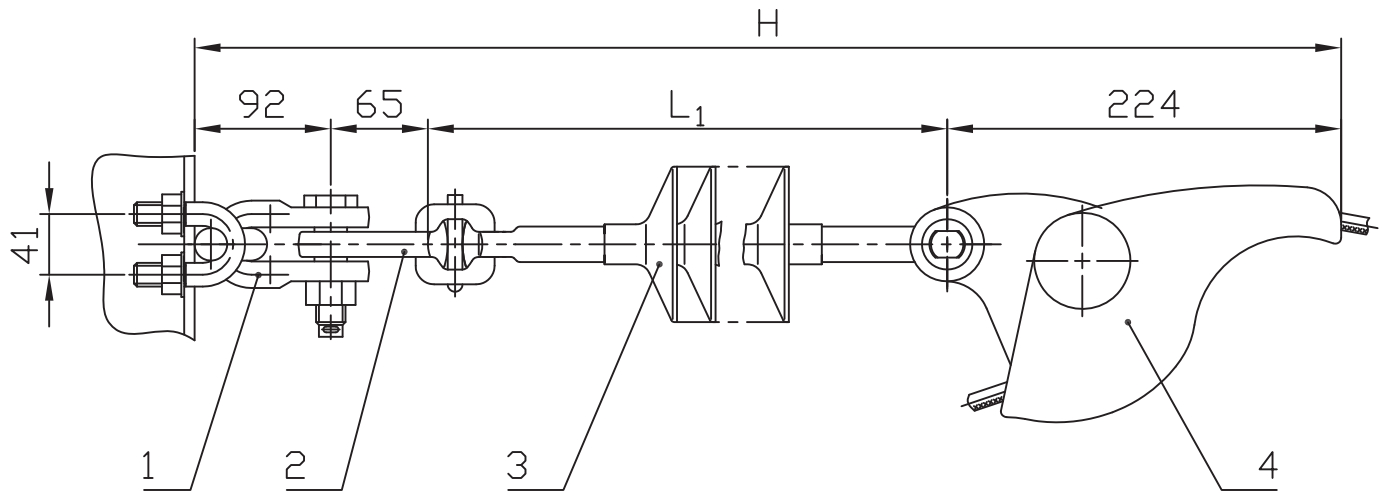

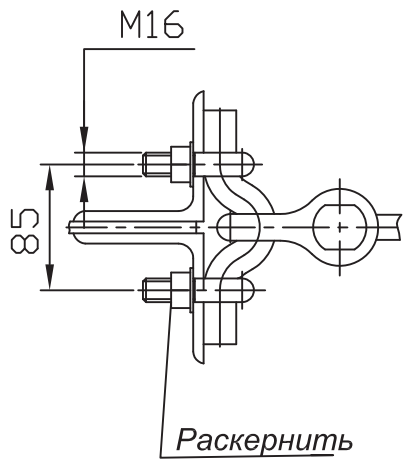

Поз.	Обозначение	Наименование	Кол.	Масса ед. кг	Прим.
1	КГ-12-1	Узел крепления	1	2,15	
2	СР-12-16	Серьга	1	0,41	
3		Изолятор исп. ГС	1	См. табл.	
4	НЗ-60/11-17	Зажим натяжной	1	1,5	
Масса арматуры, кг				4,06	
Масса изолирующей подвески, кг				См. табл.	

Напряжение ВЛ, кВ	Изолятор, поз.3			Изолирующая подвеска	
	Тип	L1, мм	Масса, кг	H, мм	Масса, кг
35	ЛК70/35	513	1,5	894	5,6
110	ЛК70/110	1213	3,5	1594	7,6


Взам. инв. N

Подп. и дата

Инв. N подл.

				ЭСИП-0021	
				ЭСС.001 ТМ - т.1	
Утв.	Вигдергауз			Натяжные одноцепные изолирующие с полимерными изоляторами ряда 70 кН подвески проводов АС70/11 - АС150/24 к а/у металлическим и ж/б опорам ВЛ 35, 110 кВ	Стадия: Р; Лист: ; Листов: 1
Пров.	Липунцов				Филиал ОАО "ФСК ЕЭС" "Электросетьсервис"
Разраб.	Власкина				

Формат А3

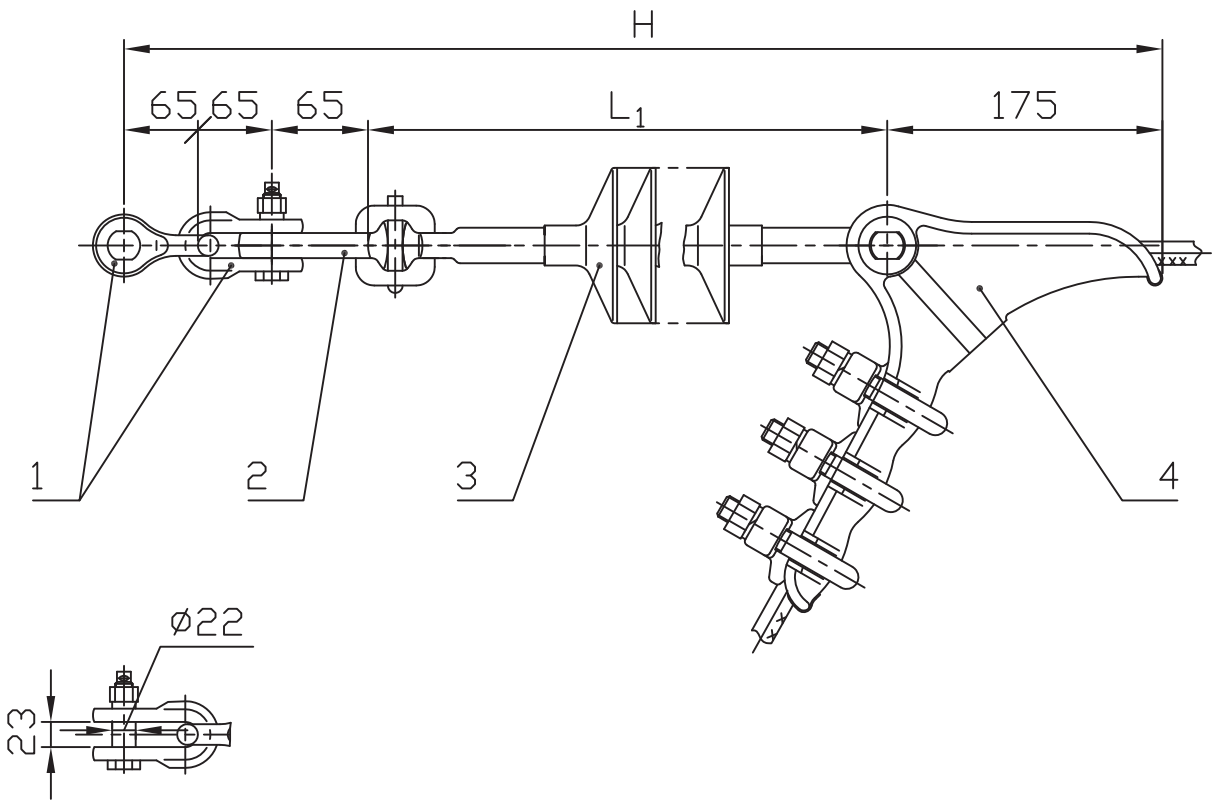

Поз.	Обозначение	Наименование	Кол.	Масса ед. кг	Прим.
1	СК-120-1Б	Скоба	2	0,92	
2	СР-12-16	Серьга	1	0,41	
3		Изолятор исп. ГС	1	См. табл.	
4	НБ-90/15-22	Зажим натяжной	1	2,84	
Масса арматуры, кг				5,09	
Масса изолирующей подвески, кг				См. табл.	

Напряжение ВЛ, кВ	Изолятор, поз.3			Изолирующая подвеска	
	Тип	L1, мм	Масса, кг	H, мм	Масса, кг
110	ЛК120/110	1213	3,5	1583	8,6
220	ЛК120/220	2070	8,0	2440	13,1*

* Масса указана с изолятором ЛК 120/220-3-ГС


Взам. инв. N


Подп. и дата

Инв. N подл.

				ЭСИП-0022	
				ЭСС.001 ТМ - т.1	
Утв.	Вигдергауз			Натяжные одноцепные изолирующие с полимерными изоляторами ряда 120 кН подвески проводов АС185/29 - АС240/39 к а/у металлическим, ж/б опорам 110 кВ и деревянным опорам ВЛ 110, 220 кВ	Стадия: Р; Лист: ; Листов: 1
Пров.	Липунцов				Филиал ОАО "ФСК ЕЭС" "Электросетьсервис"
Разраб.	Власкина				

Формат А3

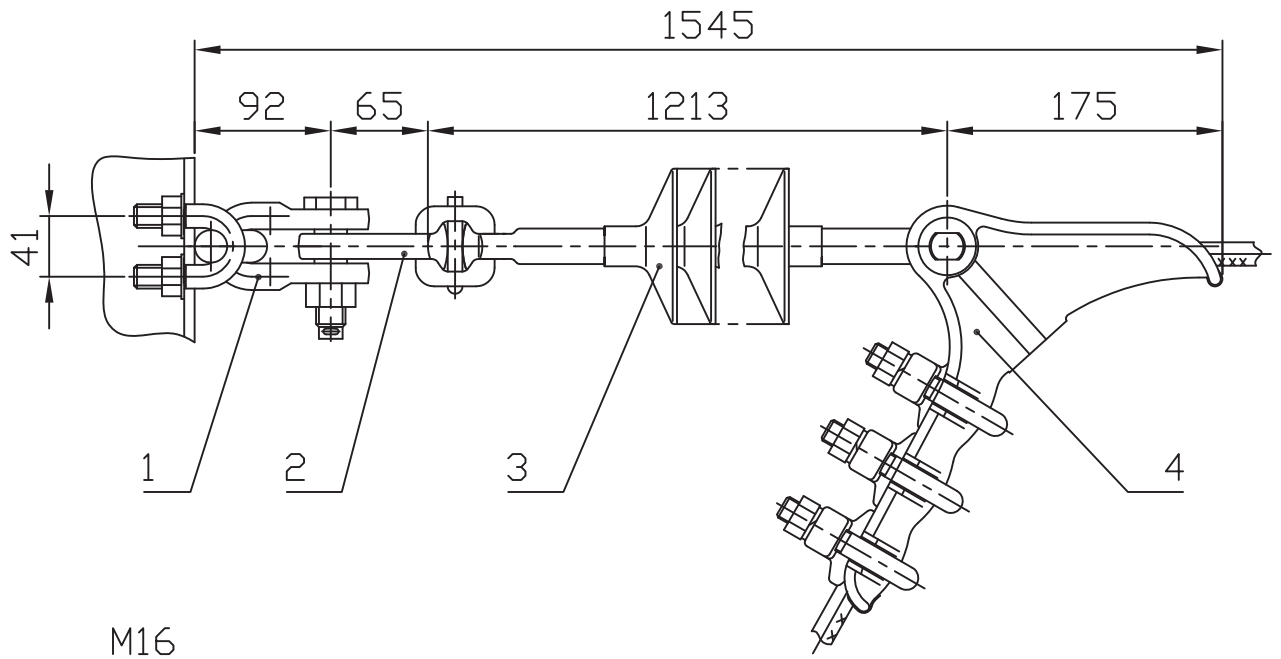

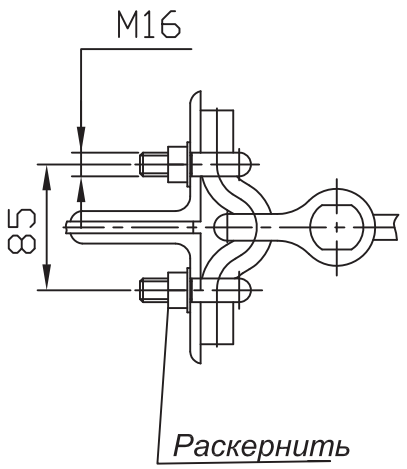

Поз.	Обозначение	Наименование	Кол.	Масса ед. кг	Прим.
1	КГ-12-1	Узел крепления	1	2,15	
2	СР-12-16	Серьга	1	0,41	
3	ЛК 120/110-	Изолятор исп. ГС	1	3,5	
4	НБ-90/15-22	Зажим натяжной	1	2,84	
Масса арматуры, кг				5,4	
Масса изолирующей подвески, кг				8,9	


Взам. инв. N


Подп. и дата

Инв. N подл.


				ЭСИП-0023		
				ЭСС.001 ТМ - т.1		
Утв.	Вигдергауз			Натяжные одноцепные изолирующие с полимерными изоляторами ряда 120 кН подвески проводов АС185/29 - АС240/39 к а/у металлическим и ж/б опорам ВЛ 110 кВ	Стадия	Лист	Листов
					Р		1
Пров.	Липунцов				Филиал ОАО "ФСК ЕЭС" "Электросетьсервис"		
Разраб.	Власкина						

Формат А3

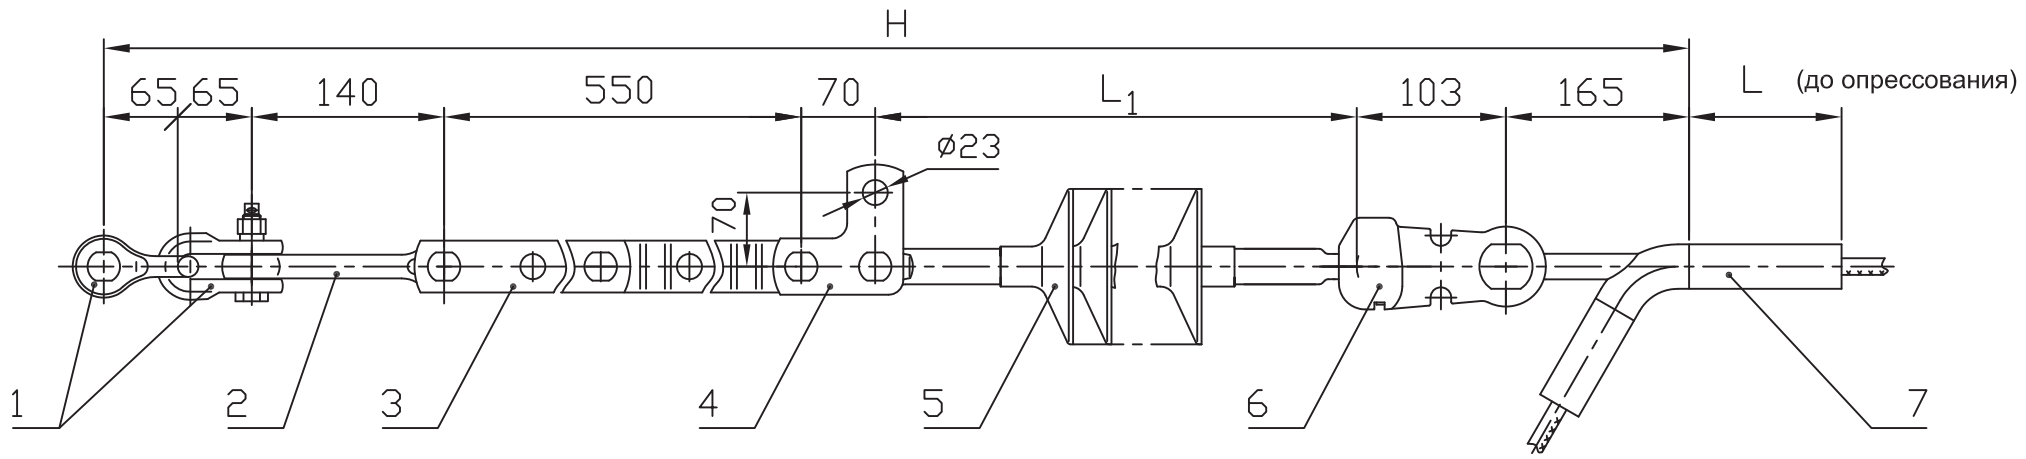

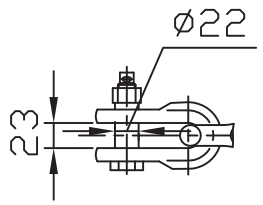

Вариант

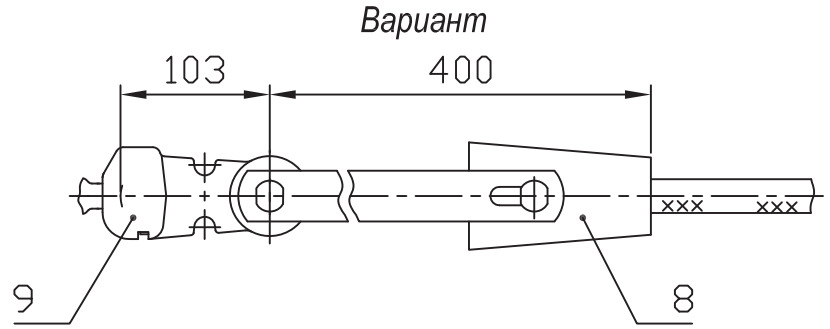

При заказе натяжного клинового зажима типа НК-300-1 следует указывать марку провода.
Ушко У2-12-16 (поз.6) заменить на У1-12-16 (поз.9)

Поз.	Обозначение	Наименование	Кол.	Масса ед. кг	Прим.
1	СК-120-1Б	Скоба	2	0,92	
2	ПРВ-12-1	Звено вывернутое	1	0,74	
3	ПРР-12-1	Звено регулируемое	1	3,69	
4	ПТМ-12-3А	Звено монтажное	1	1,7	
5		Изолятор исп. СП	1	См. табл.1	
6	У2-12-16	Ушко	1	1,54	
7	См. табл.	Зажим натяжной	1	См. табл.2	
8	НК-300-1	Зажим клиновой	1	5,1	
9	У1-12-16	Ушко однолапчатое	1	1,05	
Масса арматуры, кг				см. табл. 2	
Масса изолирующей подвески, кг				см. табл. 1	

Таблица 1

Напряжение ВЛ, кВ	Изолятор, поз.5			Изолирующая подвеска	
	Тип	L1, мм	Масса, кг	H, мм	Масса, кг
110	ЛК120/110	1200	4,0	2358	15,1
220	ЛК120/220	2060	8,0	3218	19,5

Таблица 2

Напряжение ВЛ, кВ	Провод по ГОСТ 839-80		Зажим, поз.7			Масса армат., кг
	Марка	Диаметр, мм	Обозначение	L, мм	Масса, кг	
110	АС240/32	21,6	НАС-240-1Б	160	1,63	11,14
	АС240/39		НАС-240-2Б		1,60	11,11
220	АС240/56	22,4	НАС-330-1Б	175	1,99	11,50
	АС300/39	24,0				

Взам. инв. N | Подп. и дата | Инв. N подл.

ЭСИП-0024

ЭСС.001 ТМ - т.1


Утв.	Вигдергауз	
Пров.	Липунцов	
Разраб.	Власкина	


Натяжные одноцепные изолирующие с полимерными изоляторами ряда 120 кН подвески проводов АС240/32 - АС300/39 к а/у деревянным опорам ВЛ 110, 220 кВ

Стадия	Лист	Листов
Р		1


Филиал ОАО "ФСК ЕЭС" "Электросетьсервис"

Формат А3

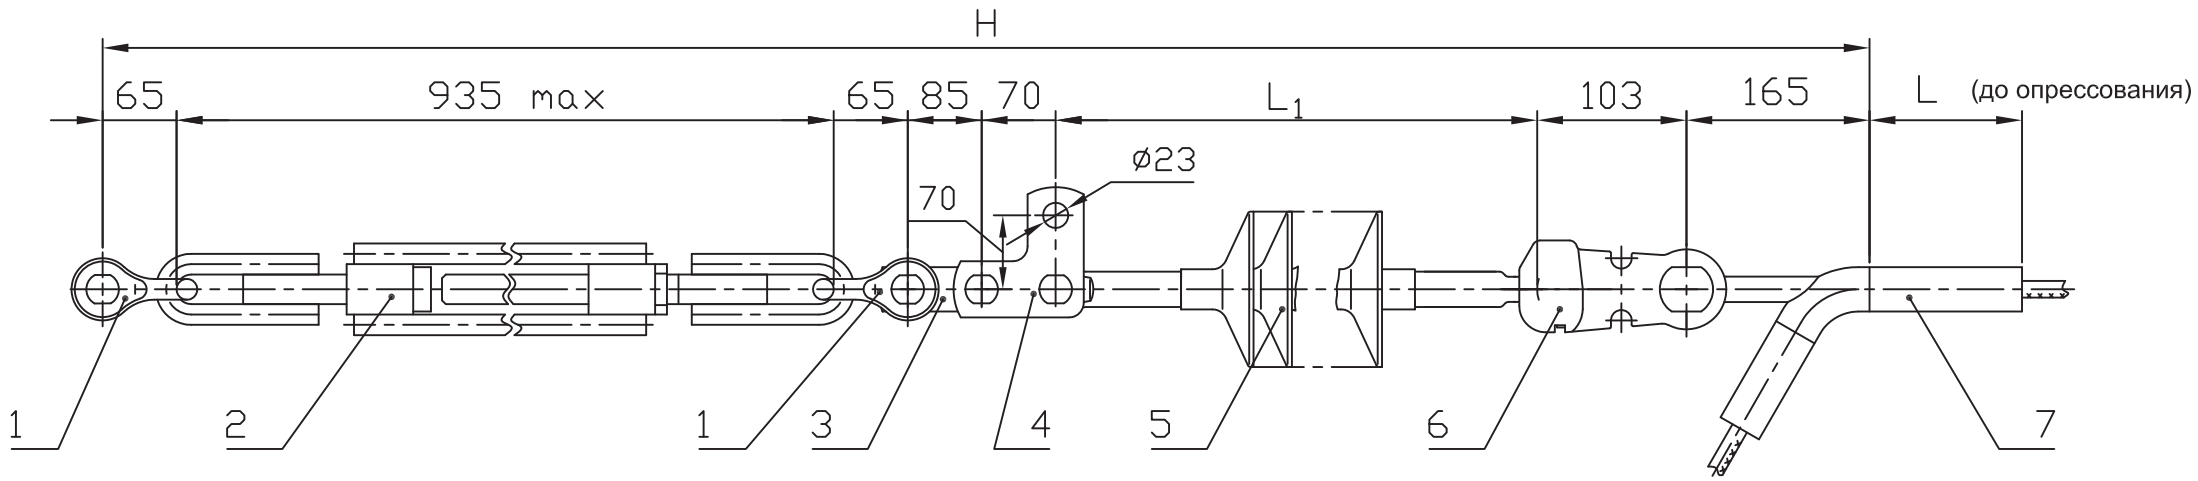

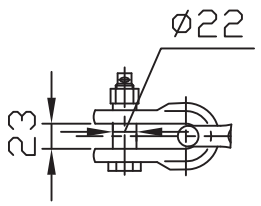

Вариант

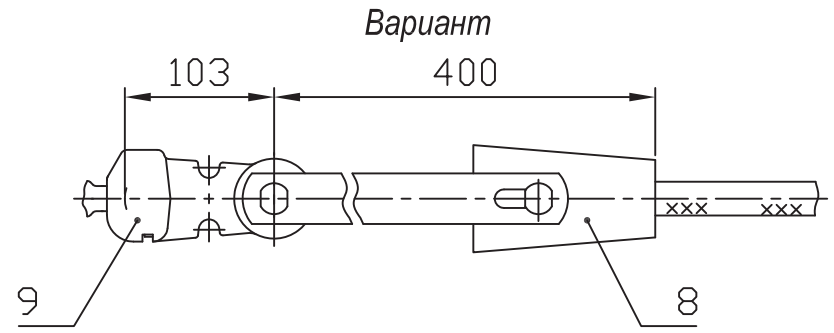

При заказе натяжного клинового зажима типа НК-300-1 следует указывать марку провода.
Ушко У2-12-16 (поз.6) заменить на У1-12-16 (поз.9)

Поз.	Обозначение	Наименование	Кол.	Масса ед. кг	Прим.
1	СК-120-1Б	Скоба	2	0,92	
2	ПТР-12-1	Талреп	1	5,67	
3	ПР-12-1	Звено прямое	1	0,94	
4	ПТМ-12-3А	Звено монтажное	1	1,7	
5		Изолятор исп. СП	1	См. табл.1	
6	У2-12-16	Ушко двухлапчатое	1	1,54	
7	См. табл.	Зажим натяжной	1	См. табл.2	
8	НК-300-1	Зажим клиновой	1	5,1	
9	У1-12-16	Ушко однолапчатое	1	1,05	
Масса арматуры, кг				см. табл. 2	
Масса изолирующей подвески, кг				см. табл. 1	

Таблица 1

Напряжение ВЛ, кВ	Изолятор, поз.5			Изолирующая подвеска	
	Тип	L1, мм	Масса, кг	H, мм	Масса, кг
110	ЛК120/110	1200	4,0	2688	17,7
220	ЛК120/220	2060	8,0	3548	21,7

Таблица 2

Напряжение ВЛ, кВ	Провод по ГОСТ 839-80		Зажим, поз.7			Масса армат., кг
	Марка	Диаметр, мм	Обозначение	L, мм	Масса, кг	
110	АС240/32	21,6	НАС-240-1Б	160	1,63	13,32
	АС240/39		НАС-240-2Б		1,60	13,29
220	АС240/56	22,4	НАС-330-1Б	175	1,99	13,68
	АС300/39	24,0				


Взам. инв. N | Подп. и дата | Инв. N подл.


			ЭСИП-0025
			ЭСС.001 ТМ - т.1
Утв.	Вигдергауз		Натяжные одноцепные изолирующие с полимерными изоляторами ряда 120 кН подвески проводов АС240/32 - АС300/39 к а/у деревянным опорам ВЛ 110, 220 кВ
Пров.	Липунцов		
Разраб.	Власкина		

Стадия	Лист	Листов
Р		1


Филиал ОАО "ФСК ЕЭС" "Электросетьсервис"

Формат А3

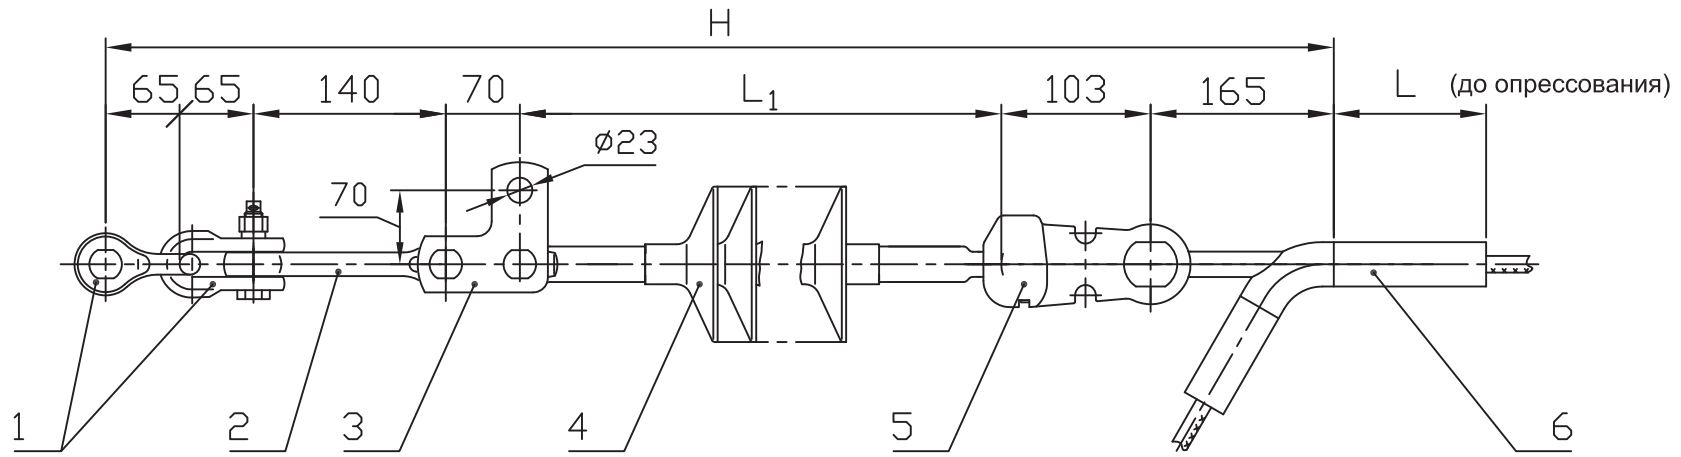

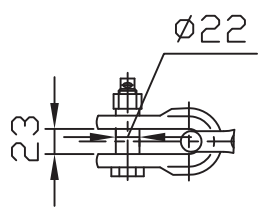

Вариант

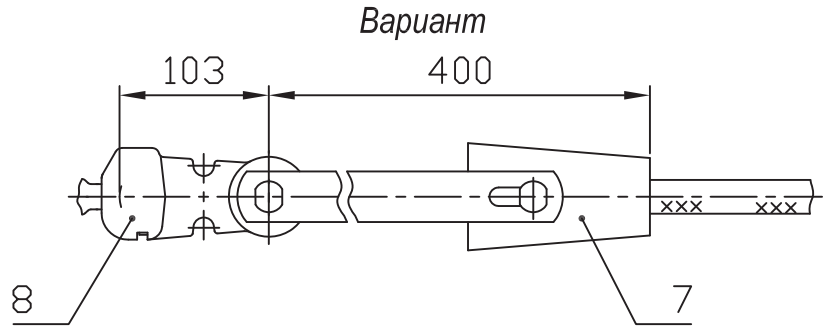

При заказе натяжного клинового зажима типа НК-300-1 следует указывать марку провода.
Ушко У2-12-16 (поз.5) заменить на У1-12-16 (поз.8)

Таблица 1

Напряжение ВЛ, кВ	Изолятор, поз.4			Изолирующая подвеска	
	Тип	L1, мм	Масса, кг	H, мм	Масса, кг
110	ЛК120/110	1200	4,0	1808	11,8
220	ЛК120/220	2060	8,0	2668	15,8

Таблица 2


Напряжение ВЛ, кВ	Провод по ГОСТ 839-80		Зажим, поз.6			Масса армат., кг
	Марка	Диаметр, мм	Обозначение	L, мм	Масса, кг	
110	АС240/32	21,6	НАС-240-1Б	160	1,63	7,45
	АС240/39		НАС-240-2Б		1,60	7,42
220	АС240/56	22,4	НАС-330-1Б	175	1,99	7,81
	АС300/39	24,0				


Поз.	Обозначение	Наименование	Кол.	Масса ед. кг	Прим.
1	СК-120-1Б	Скоба	2	0,92	
2	ПРВ-12-1	Звено вывернутое	1	0,74	
3	ПТМ-12-3А	Звено монтажное	1	1,7	
4		Изолятор исп. СП	1	См. табл.1	
5	У2-12-16	Ушко	1	1,54	
6	См. табл.	Зажим натяжной	1	См. табл.2	
7	НК-300-1	Зажим клиновой	1	5,1	
8	У1-12-16	Ушко однолапчатое	1	1,05	
Масса арматуры, кг				см. табл. 2	
Масса изолирующей подвески, кг				см. табл. 1	

Утв.	Вигдергауз	ЭСИП-0026	
		ЭСС.001 ТМ - т.1	
Пров.	Липунцов	Натяжные одноцепные изолирующие с полимерными изоляторами ряда 120 кН подвески проводов АС240/32 - АС300/39 к а/у деревянным опорам ВЛ 110, 220 кВ	Стадия: Р; Лист: ; Листов: 1
Разраб.	Власкина		Филиал ОАО "ФСК ЕЭС" "Электросетьсервис"


Взам. инв. N | Подп. и дата | Инв. N подл.

Формат А3

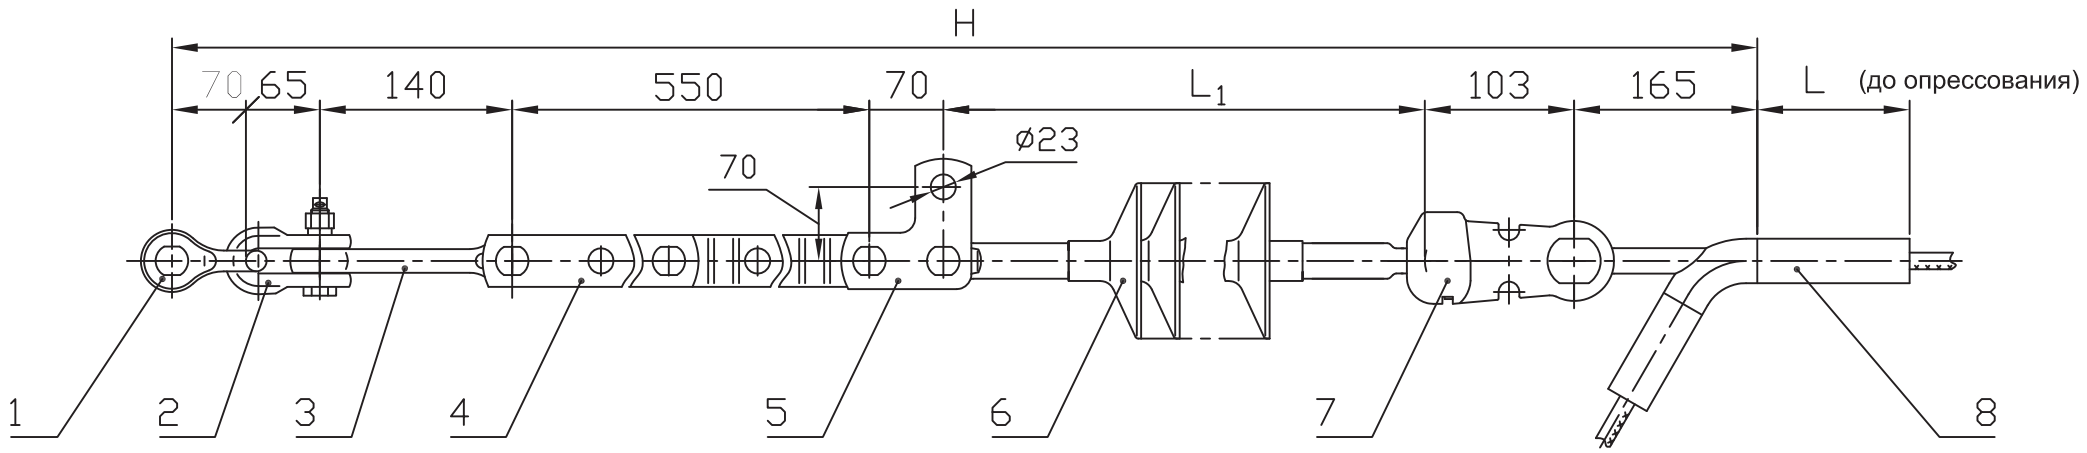

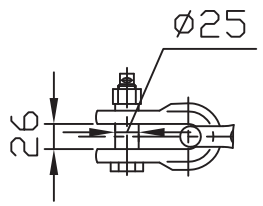

Вариант

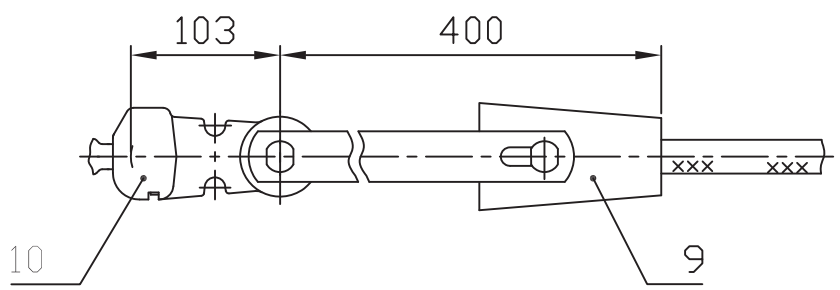

При заказе натяжного клинового зажима типа НК-300-1 следует указывать марку провода. Ушко У2-12-16 (поз.7) заменить на У1-12-16 (поз.10)

Поз.	Обозначение	Наименование	Кол.	Масса ед. кг	Прим.
1	СК-16-1А	Скоба	1	1,22	
2	СК-120-1Б	Скоба	1	0,92	
3	ПРВ-12-1	Звено вывернутое	1	0,74	
4	ПРР-12-1	Звено регулируемое	1	3,69	
5	ПТМ-12-3А	Звено монтажное	1	1,7	
6		Изолятор исп. СП	1	См. табл.1	
7	У2-12-16	Ушко	1	1,54	
8	См. табл.	Зажим натяжной	1	См. табл.2	
9	НК-300-1	Зажим клиновой	1	5,1	
10	У1-12-16	Ушко однолапчатое	1	1,05	
Масса арматуры, кг				см. табл. 2	
Масса изолирующей подвески, кг				см. табл. 1	

Таблица 1

Напряжение ВЛ, кВ	Изолятор, поз.6			Изолирующая подвеска	
	Тип	L1, мм	Масса, кг	H, мм	Масса, кг
110	ЛК120/110	1200	4,0	2363	15,5
220	ЛК120/220	2060	8,0	3223	19,8


Таблица 2


Напряжение ВЛ, кВ	Провод по ГОСТ 839-80		Зажим, поз.8			Масса армат., кг
	Марка	Диаметр, мм	Обозначение	L, мм	Масса, кг	
110	АС240/32	21,6	НАС-240-1Б	160	1,63	11,44
	АС240/39		НАС-240-2Б		1,60	11,41
220	АС240/56	22,4	НАС-330-1Б	175	1,99	11,80
	АС300/39	24,0				
	АС300/48	24,1				

				ЭСИП-0027	
				ЭСС.001 ТМ - т.1	
Утв.	Вигдергауз			Натяжные одноцепные изолирующие с полимерными изоляторами ряда 120 кН подвески проводов АС240/32 - АС300/48 к а/у стальным, ж/б опорам ВЛ 220 кВ и деревянным опорам ВЛ 110, 220 кВ	Стадия: Р; Лист: ; Листов: 1
Пров.	Липунцов				Филиал ОАО "ФСК ЕЭС" "Электросетьсервис"
Разраб.	Власкина				


Формат А3

Взам. инв. N | Подп. и дата | Инв. N подл.

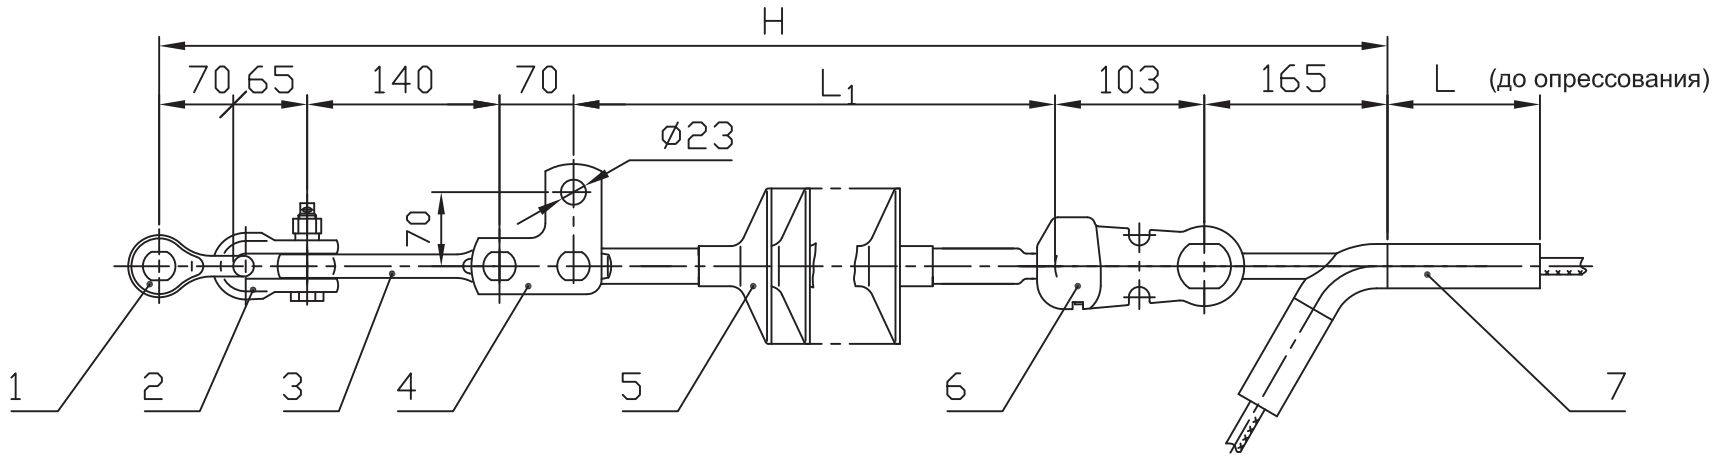

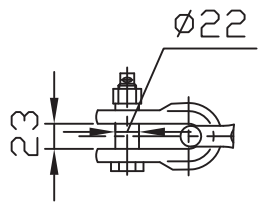

Вариант

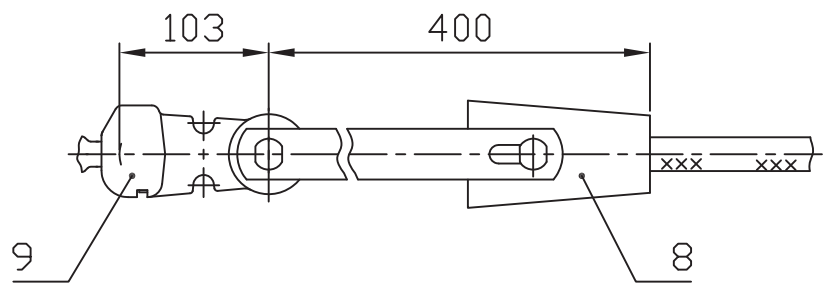

При заказе натяжного клинового зажима типа НК-300-1 следует указывать марку провода.
Ушко У2-12-16 (поз.6) заменить на У1-12-16 (поз.9)

Таблица 1

Напряжение ВЛ, кВ	Изолятор, поз.5			Изолирующая подвеска	
	Тип	L1, мм	Масса, кг	H, мм	Масса, кг
110	ЛК120/110	1200	4,0	1813	12,1
220	ЛК120/220	2060	8,0	2673	16,1

Таблица 2

Напряжение ВЛ, кВ	Провод по ГОСТ 839-80		Зажим, поз.7			Масса армат., кг
	Марка	Диаметр, мм	Обозначение	L, мм	Масса, кг	
110	АС240/32	21,6	НАС-240-1Б	160	1,63	7,75
	АС240/39		НАС-240-2Б		1,60	7,72
220	АС240/56	22,4	НАС-330-1Б	175	1,99	8,11
	АС300/39	24,0				
	АС300/48	24,1				

Поз.	Обозначение	Наименование	Кол.	Масса ед. кг	Прим.
1	СК-16-1А	Скоба	1	1,22	
2	СК-120-1Б	Скоба	1	0,92	
3	ПРВ-12-1	Звено вывернутое	1	0,74	
4	ПТМ-12-3А	Звено монтажное	1	1,7	
5		Изолятор исп. СП	1	См. табл.1	
6	У2-12-16	Ушко	1	1,54	
7	См. табл.	Зажим натяжной	1	См. табл.2	
8	НК-300-1	Зажим клиновой	1	5,1	
9	У1-12-16	Ушко однолапчатое	1	1,05	
Масса арматуры, кг				см. табл. 2	
Масса изолирующей подвески, кг				см. табл. 1	

Утв.	Вигдергауз		
Пров.	Липунцов		
Разраб.	Власкина		

ЭСИП-0028

ЭСС.001 ТМ - т.1


Натяжные одноцепные изолирующие с полимерными изоляторами ряда 120 кН подвески проводов АС240/32 - АС300/48 к а/у металлическим и ж/б опорам ВЛ220 кВ и деревянным опорам ВЛ 110, 220 кВ


Стадия	Лист	Листов
Р		1

Филиал ОАО "ФСК ЕЭС" "Электросетьсервис"


Взам. инв. N | Подп. и дата | Инв. N подл.

Формат А3

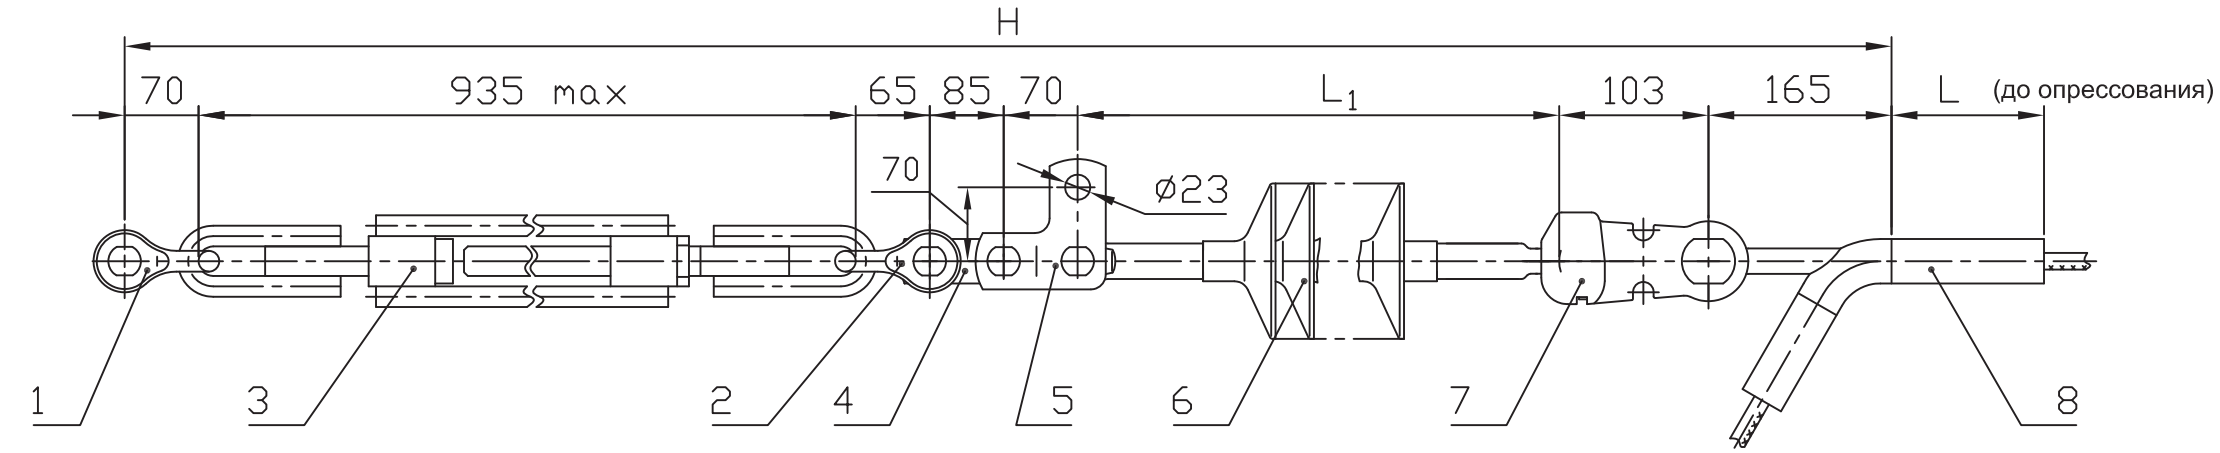

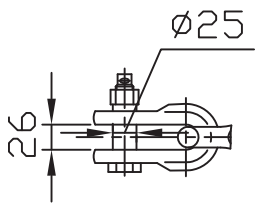

Вариант

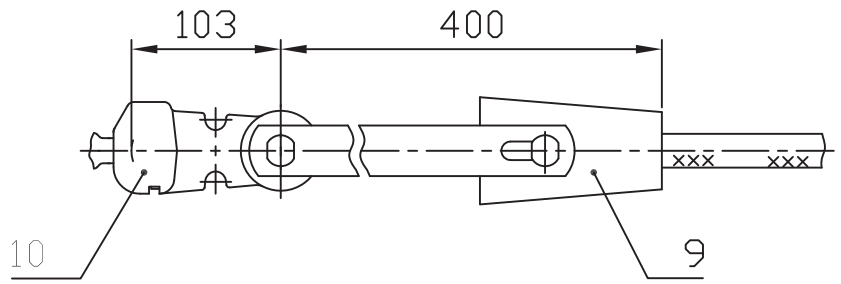

При заказе натяжного клинового зажима типа НК-300-1 следует указывать марку провода.
Ушко У2-12-16 (поз.7) заменить на У1-12-16 (поз.10)

Таблица 1

Напряжение ВЛ, кВ	Изолятор, поз.6			Изолирующая подвеска	
	Тип	L1, мм	Масса, кг	H, мм	Масса, кг
110	ЛК120/110	1200	4,0	2693	18,0
220	ЛК120/220	2060	8,0	3553	22,0

Таблица 2

Напряжение ВЛ, кВ	Провод по ГОСТ 839-80		Зажим, поз.8			Масса армат., кг
	Марка	Диаметр, мм	Обозначение	L, мм	Масса, кг	
110	АС240/32	21,6	НАС-240-1Б	160	1,63	13,62
	АС240/39		НАС-240-2Б		1,60	13,59
220	АС240/56	22,4	НАС-330-1Б	175	1,99	13,98
	АС300/39	24,0				
	АС300/48	24,1				

Поз.	Обозначение	Наименование	Кол.	Масса ед. кг	Прим.
1	СК-16-1А	Скоба	1	1,22	
2	СК-120-1Б	Скоба	1	0,92	
3	ПТР-12-1	Талреп	1	5,67	
4	ПР-12-1	Звено прямое	1	0,94	
5	ПТМ-12-3А	Звено монтажное	1	1,7	
6		Изолятор исп. СП	1	См. табл.1	
7	У2-12-16	Ушко двухлапчатое	1	1,54	
8	См. табл.	Зажим натяжной	1	См. табл.2	
9	НК-300-1	Зажим клиновой	1	5,1	
10	У1-12-16	Ушко однолапчатое	1	1,05	
Масса арматуры, кг				см. табл. 2	
Масса изолирующей подвески, кг				см. табл. 1	

ЭСИП-0029

ЭСС.001 ТМ - т.1

Утв.	Вигдергауз		
Пров.	Липунцов		
Разраб.	Власкина		


Натяжные одноцепные изолирующие с полимерными изоляторами ряда 120 кН подвески проводов АС240/32 - АС300/48 к а/у металлич., ж/б опорам ВЛ 220 кВ и деревянным опорам ВЛ 110, 220 кВ


Стадия	Лист	Листов
Р		1

Филиал ОАО "ФСК ЕЭС" "Электросетьсервис"


Взам. инв. N | Подп. и дата | Инв. N подл.

Формат А3

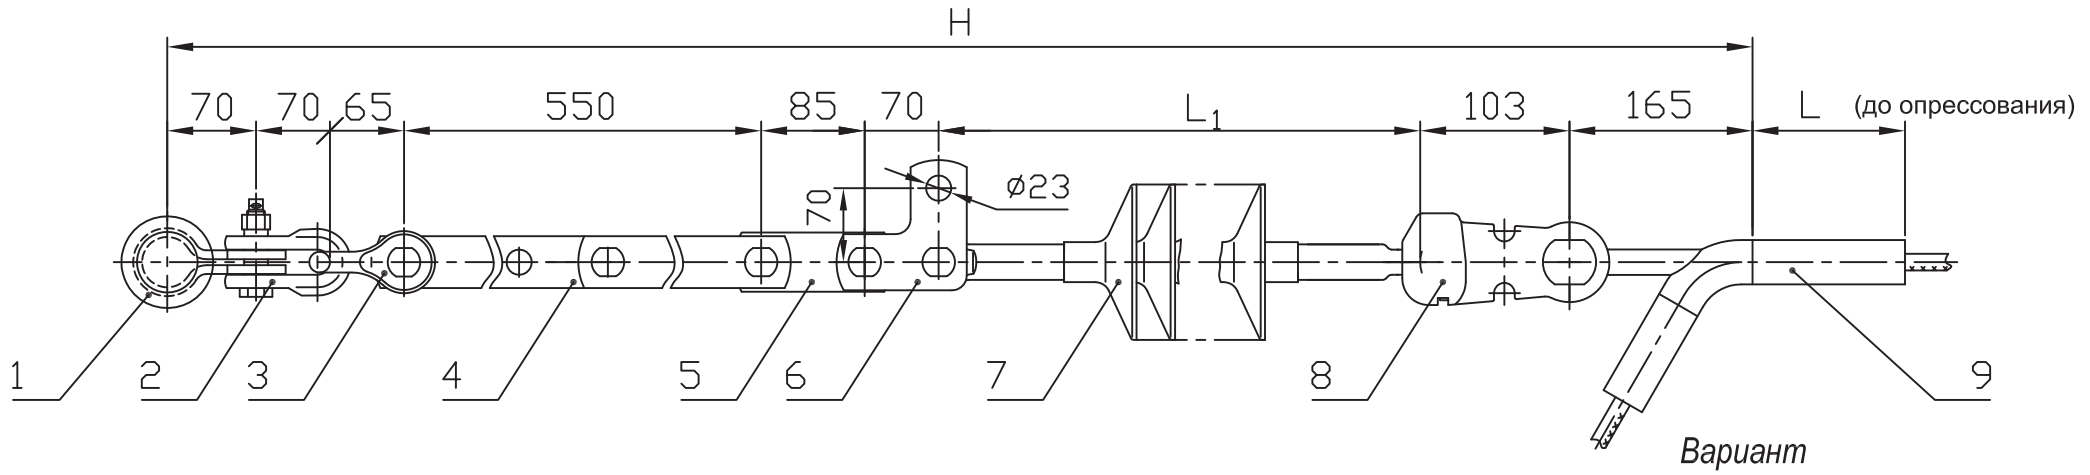

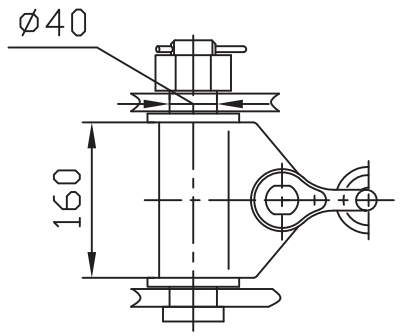

Вариант

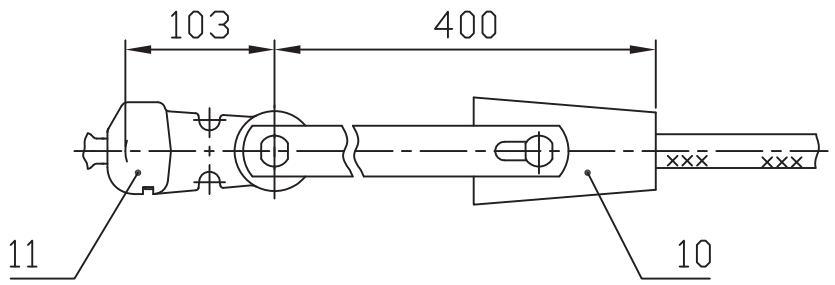

При заказе натяжного клинового зажима типа НК-300-1 следует указывать марку провода.
Ушко У2-12-16 (поз.8) заменить на У1-12-16 (поз.11)

Поз.	Обозначение	Наименование	Кол.	Масса ед. кг	Прим.
1	КГН-16-5	Узел крепления	1	5,23	
2	СК-16-1А	Скоба	1	1,22	
3	СК-120-1Б	Скоба	1	0,92	
4	ПРР-12-1	Звено регулируемое	1	3,69	
5	ПР-12-6	Звено прямое	1	0,94	
6	ПТМ-12-3А	Звено монтажное	1	1,7	
7		Изолятор исп. СП	1	См. табл.1	
8	У2-12-16	Ушко двухлапчатое	1	1,54	
9	См. табл.	Зажим натяжной	1	См. табл.2	
10	НК-300-1	Зажим клиновой	1	5,1	
11	У1-12-16	Ушко однолапчатое	1	1,05	
Масса арматуры, кг				см. табл. 2	
Масса изолирующей подвески, кг				см. табл. 1	

Таблица 1

Напряжение ВЛ, кВ	Изолятор, поз.7			Изолирующая подвеска	
	Тип	L1, мм	Масса, кг	Н, мм	Масса, кг
110	ЛК120/110	1200	4,0	2378	21,2
220	ЛК120/220	2060	8,0	3238	25,2

Таблица 2

Провод по ГОСТ 839-80		Зажим, поз.9			Масса армат., кг
Марка	Диаметр, мм	Обозначение	L, мм	Масса, кг	
АС240/32	21,6	НАС-240-1Б	160	1,63	16,87
АС240/39		НАС-240-2Б		1,60	16,84
АС300/39	24,0	НАС-330-1Б	175	1,99	17,23

Утв.	Вигдергауз		
Пров.	Липунцов		
Разраб.	Власкина		

ЭСИП-0030

ЭСС.001 ТМ - т.1


Натяжные одноцепные изолирующие с полимерными изоляторами ряда 120 кН подвески проводов АС240/32 - АС300/39 к а/у металлическим опорам ВЛ 110, 220 кВ


Стадия	Лист	Листов
Р		1

Филиал ОАО "ФСК ЕЭС" "Электросетьсервис"


Взам. инв. N | Подп. и дата | Инв. N подл.

Формат А3

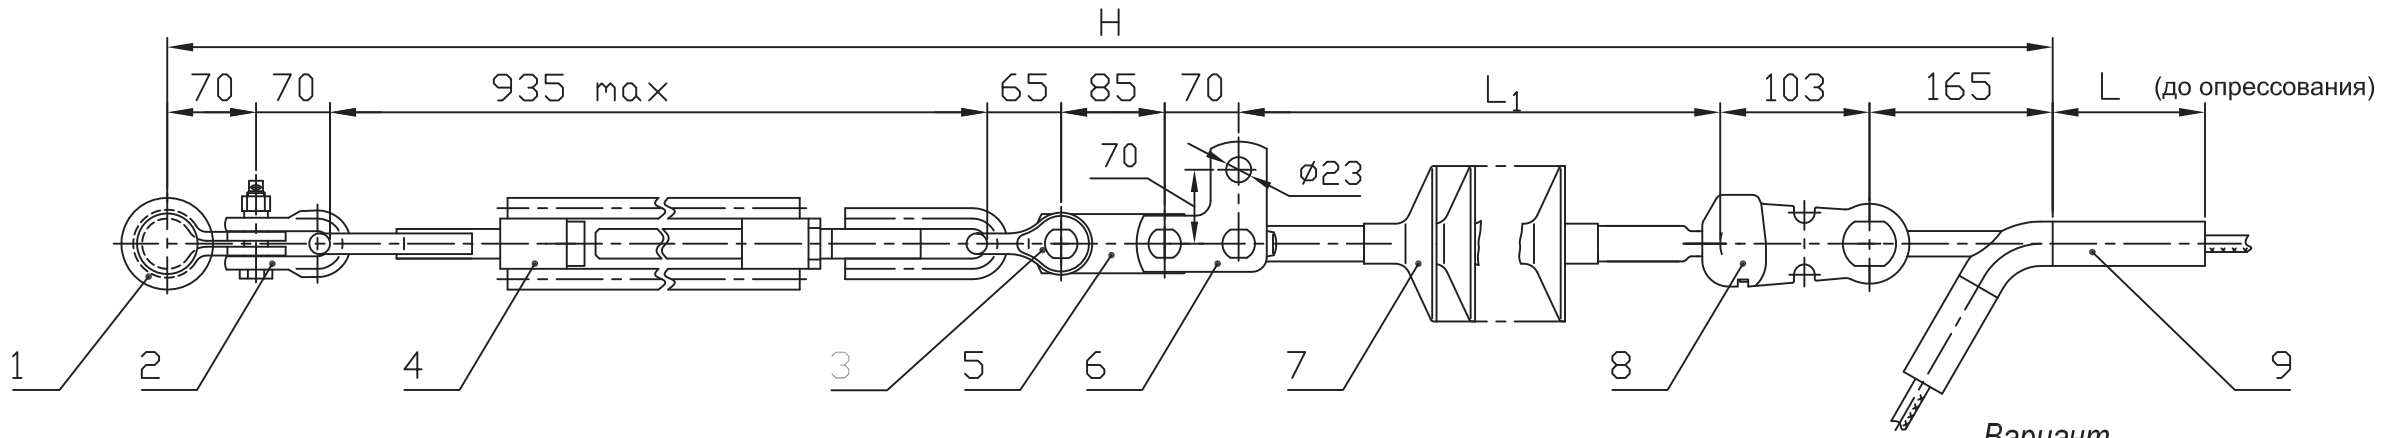

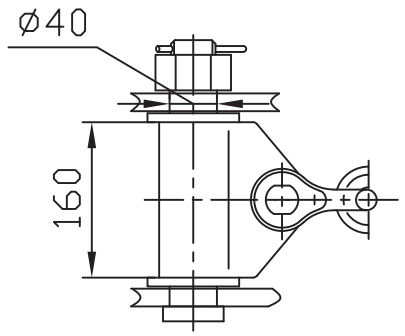

Вариант

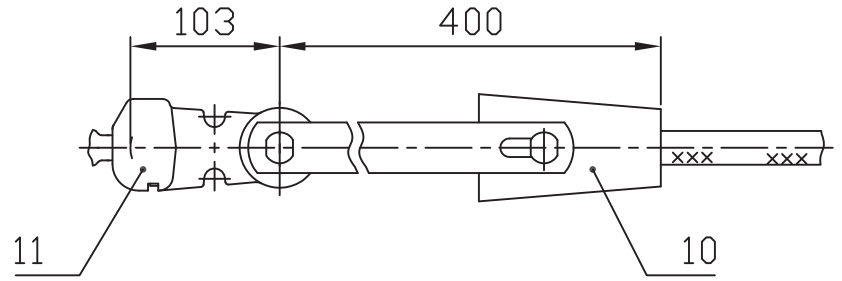

При заказе натяжного клинового зажима типа НК-300-1 следует указывать марку провода.
Ушко У2-12-16 (поз.8) заменить на У1-12-16 (поз.11)

Поз.	Обозначение	Наименование	Кол.	Масса ед. кг	Прим.
1	КГН-16-5	Узел крепления	1	5,23	
2	СК-16-1А	Скоба	1	1,22	
3	СК-120-1Б	Скоба	1	0,92	
4	ПТР-12-1	Талреп	1	5,67	
5	ПР-12-6	Звено прямое	1	0,94	
6	ПТМ-12-3А	Звено монтажное	1	1,7	
7		Изолятор исп. СП	1	См. табл.1	
8	У2-12-16	Ушко двухлапчатое	1	1,54	
9	См. табл.	Зажим натяжной	1	См. табл.2	
10	НК-300-1	Зажим клиновой	1	5,1	
11	У1-12-16	Ушко однолапчатое	1	1,05	
Масса арматуры, кг				см. табл. 2	
Масса изолирующей подвески, кг				см. табл. 1	

Таблица 1

Напряжение ВЛ, кВ	Изолятор, поз.7			Изолирующая подвеска	
	Тип	L1, мм	Масса, кг	Н, мм	Масса, кг
110	ЛК120/110	1200	4,0	2763	23,2
220	ЛК120/220	2060	8,0	3623	27,2

Таблица 2

Провод по ГОСТ 839-80		Зажим, поз.9			Масса армат., кг
Марка	Диаметр, мм	Обозначение	L, мм	Масса, кг	
АС240/32	21,6	НАС-240-1Б	160	1,63	18,83
АС240/39		НАС-240-2Б		1,60	18,8
АС300/39	24,0	НАС-330-1Б	175	1,99	19,2

Утв.	Вигдергауз		
Пров.	Липунцов		
Разраб.	Власкина		

ЭСИП-0031

ЭСС.001 ТМ - т.1


Натяжные одноцепные изолирующие с полимерными изоляторами ряда 120 кН подвески проводов АС240/32 - АС300/39 к а/у металлическим опорам ВЛ 110, 220 кВ


Стадия	Лист	Листов
Р		1

Филиал ОАО "ФСК ЕЭС" "Электросетьсервис"


Формат А3

Взам. инв. N | Подп. и дата | Инв. N подл.

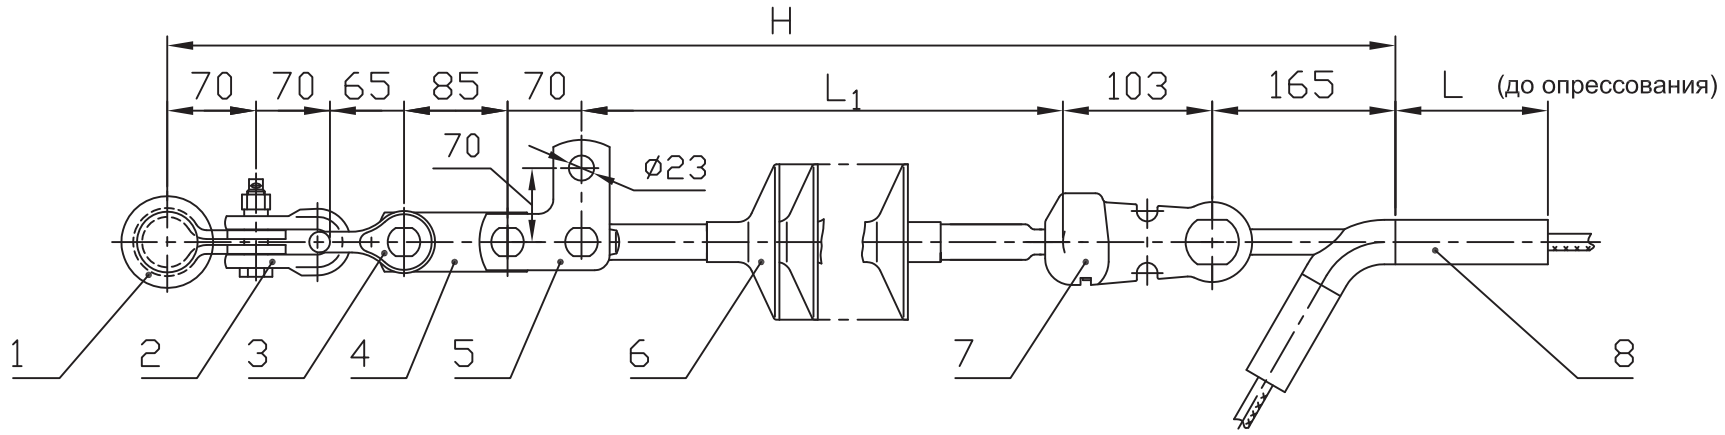

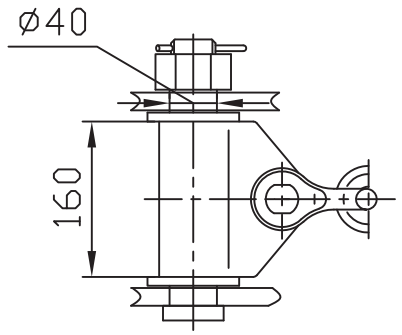

Вариант

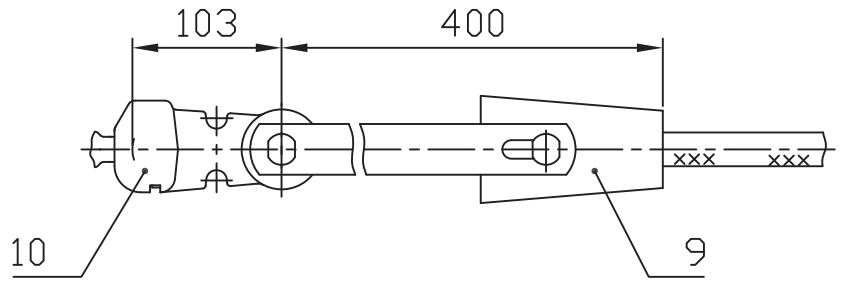

При заказе натяжного клинового зажима типа НК-300-1 следует указывать марку провода.
Ушко У2-12-16 (поз.7) заменить на У1-12-16 (поз.10)

Поз.	Обозначение	Наименование	Кол.	Масса ед. кг	Прим.
1	КГН-16-5	Узел крепления	1	5,23	
2	СК-16-1А	Скоба	1	1,22	
3	СК-120-1Б	Скоба	1	0,92	
4	ПР-12-6	Звено прямое	1	0,94	
5	ПТМ-12-3А	Звено монтажное	1	1,7	
6		Изолятор исп. СП	1	См. табл.1	
7	У2-12-16	Ушко двухлапчатое	1	1,54	
8	См. табл.	Зажим натяжной	1	См. табл.2	
9	НК-300-1	Зажим клиновой	1	5,1	
10	У1-12-16	Ушко однолапчатое	1	1,05	
Масса арматуры, кг				см. табл. 2	
Масса изолирующей подвески, кг				см. табл. 1	

Таблица 1

Напряжение ВЛ, кВ	Изолятор, поз.6			Изолирующая подвеска	
	Тип	L1, мм	Масса, кг	H, мм	Масса, кг
110	ЛК120/110	1200	4,0	1828	17,6
220	ЛК120/220	2060	8,0	2688	21,6

Таблица 2

Провод по ГОСТ 839-80		Зажим, поз.8			Масса армат., кг
Марка	Диаметр, мм	Обозначение	L, мм	Масса, кг	
АС240/32	21,6	НАС-240-1Б	160	1,63	13,18
АС240/39		НАС-240-2Б		1,60	13,15
АС300/39	24,0	НАС-330-1Б	175	1,99	13,54

Утв.	Вигдергауз		
Пров.	Липунцов		
Разраб.	Власкина		

ЭСИП-0032

ЭСС.001 ТМ - т.1


Натяжные одноцепные изолирующие с полимерными изоляторами ряда 120 кН подвески проводов АС240/32 - АС300/39 к а/у металлическим опорам ВЛ 110, 220 кВ


Стадия	Лист	Листов
Р		1

Филиал ОАО "ФСК ЕЭС" "Электросетьсервис"


Формат А3

Взам. инв. N | Подп. и дата | Инв. N подл.

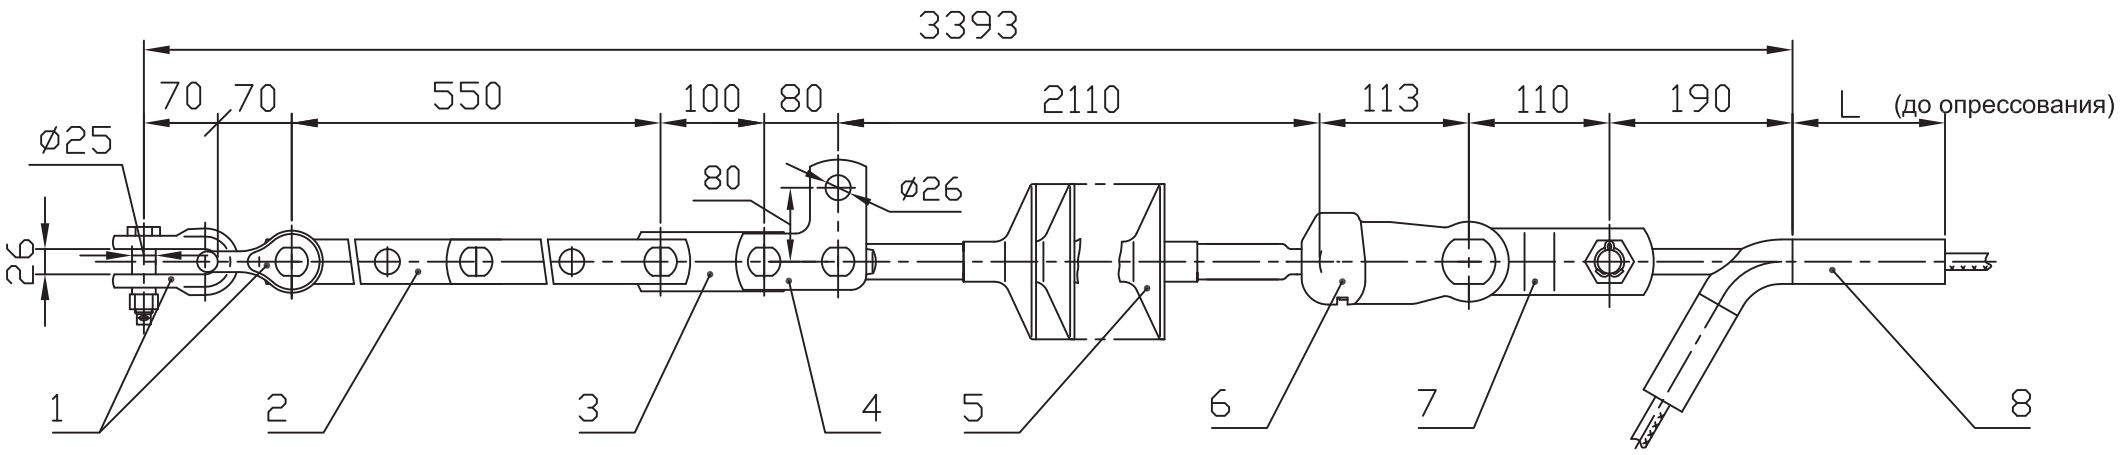

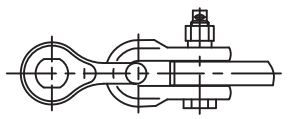

Вариант

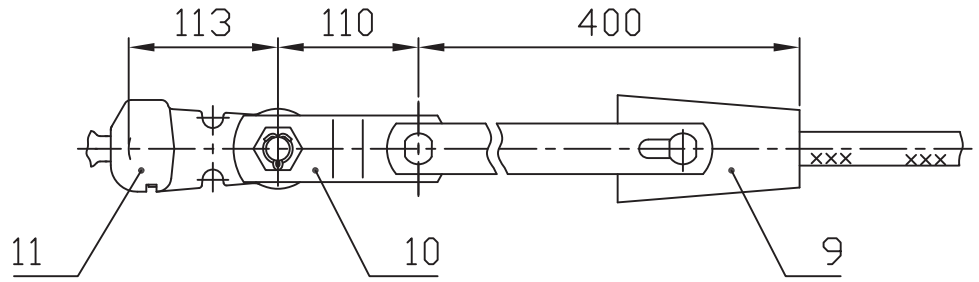


При заказе натяжного клинового зажима типа НК-300-1 следует указывать марку провода. Ушко У2-16-20 (поз.6) заменить на У1-16-20 (поз.11), а звено ПРТ-16/12-2 (поз. 7) на ПРТ-12/16-2 (поз.10).

Провод по ГОСТ 839-80		Зажим, поз.8			Масса армат., кг
Марка	Диаметр, мм	Обозначение	L, мм	Масса, кг	
АС240/56	22,4	НАС-330-1Б	175	1,99	16,80
АС300/39	24,0				
АС330/43	25,2	НАС-330-3Б	200	2,16	16,97


Поз.	Обозначение	Наименование	Кол.	Масса ед. кг	Прим.
1	СК-16-1А	Скоба	2	1,22	
2	ПРР-16-1	Звено регулируемое	1	5,00	
3	ПР-16-6	Звено прямое	1	1,36	
4	ПТМ-16-3А	Звено монтажное	1	2,34	
5	ЛК 160/220-	Изолятор исп. СП	1	9,0	
6	У2-16-20	Ушко двухлапчатое	1	2,17	
7	ПРТ-16/12-2	Звено переходное	1	1,5	
8	См. табл.	Зажим натяжной	1	См. табл.	
9	НК-300-1	Зажим клиновой	1	5,1	
10	ПРТ-12/16-2	Звено переходное	1	1,6	
11	У1-16-20	Ушко однолапчатое	1	1,6	
Масса арматуры, кг				см. табл.	
Масса изолирующей подвески, кг				26,0	

			ЭСИП-0033
			ЭСС.001 ТМ - т.1
Утв.	Вигдергауз		Натяжные одноцепные изолирующие с полимерными изоляторами ряда 160 кН подвески проводов АС240/56 - АС330/43 к а/у ж/б опорам ВЛ 220 кВ
Пров.	Липунцов		Стадия: Р; Лист: ; Листов: 1
Разраб.	Власкина		Филиал ОАО "ФСК ЕЭС" "Электросетьсервис"

Взам. инв. N | Подп. и дата | Инв. N подл.

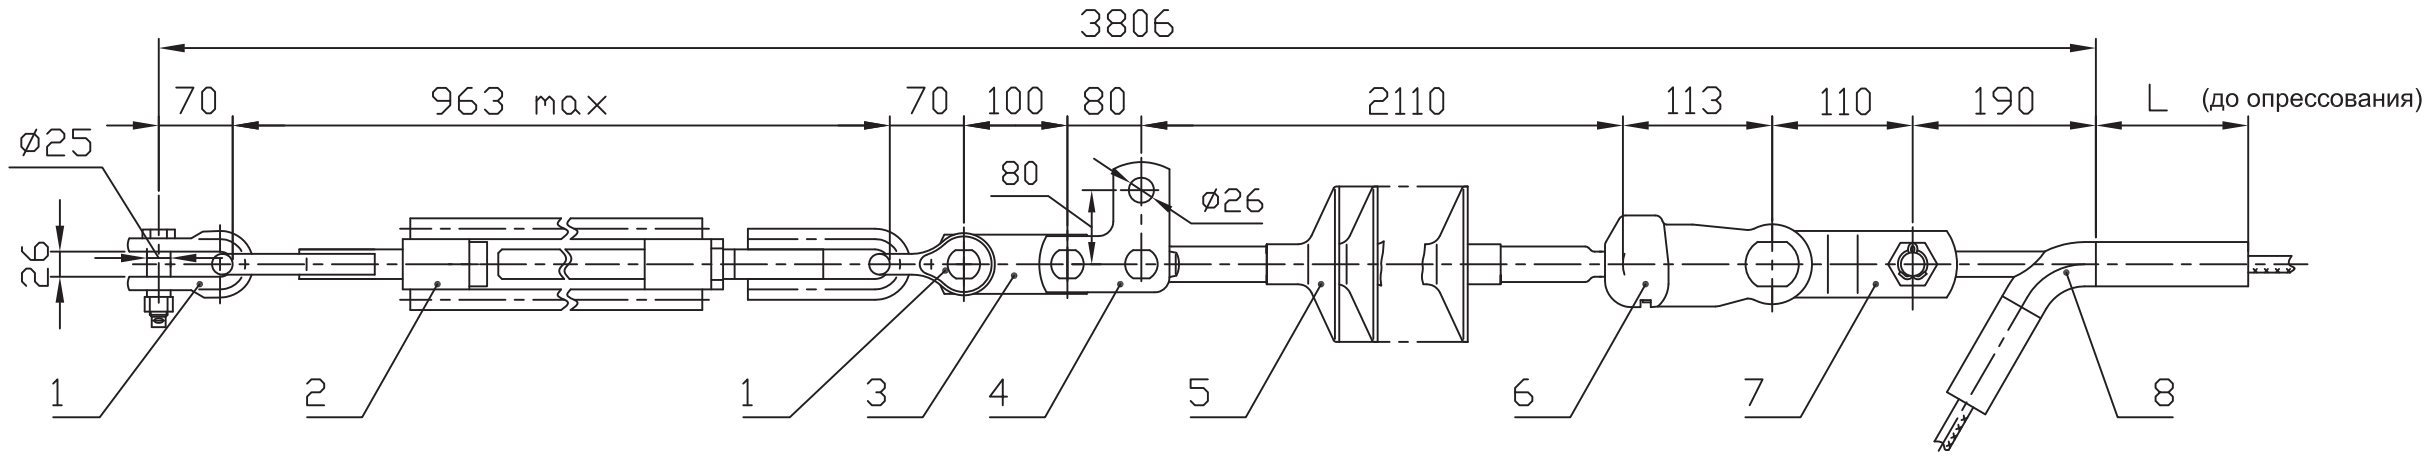

Вариант

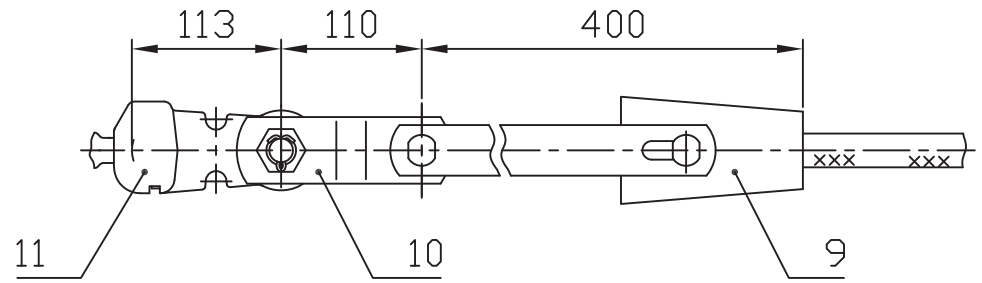

При заказе натяжного клинового зажима типа НК-300-1 следует указывать марку провода. Ушко У2-16-20 (поз.6) заменить на У1-16-20 (поз.11), а звено ПРТ-16/12-2 (поз. 7) на ПРТ-12/16-2 (поз.10).

Провод по ГОСТ 839-80		Зажим, поз.8			Масса армат., кг
Марка	Диаметр, мм	Обозначение	L, мм	Масса, кг	
АС240/56	22,4	НАС-330-1Б	175	1,99	19,0
АС300/39	24,0				
АС330/43	25,2	НАС-330-3Б	200	2,16	19,17

Поз.	Обозначение	Наименование	Кол.	Масса ед. кг	Прим.
1	СК-16-1А	Скоба	2	1,22	
2	ПТР-16-1	Звено регулируемое	1	7,2	
3	ПР-16-6	Звено прямое	1	1,36	
4	ПТМ-16-3А	Звено монтажное	1	2,34	
5	ЛК 160/220-	Изолятор исп. СП	1	9,0	
6	У2-16-20	Ушко двухлапчатое	1	2,17	
7	ПРТ-16/12-2	Звено переходное	1	1,5	
8	См. табл.	Зажим натяжной	1	См. табл.	
9	НК-300-1	Зажим клиновой	1	5,1	
10	ПРТ-12/16-2	Звено переходное	1	1,6	
11	У1-16-20	Ушко однолапчатое	1	1,6	
Масса арматуры, кг				см. табл.	
Масса изолирующей подвески, кг				28,2	


Взам. инв. N


Подп. и дата

Инв. N подл.


			ЭСИП-0034
			ЭСС.001 ТМ - т.1
Утв.	Вигдергауз		Натяжные одноцепные изолирующие с полимерными изоляторами ряда 160 кН подвески проводов АС240/56 - АС330/43 к а/у ж/б опорам ВЛ 220 кВ
Пров.	Липунцов		Стадия: Р; Лист: ; Листов: 1
Разраб.	Власкина		Филиал ОАО "ФСК ЕЭС" "Электросетьсервис"

Формат А3

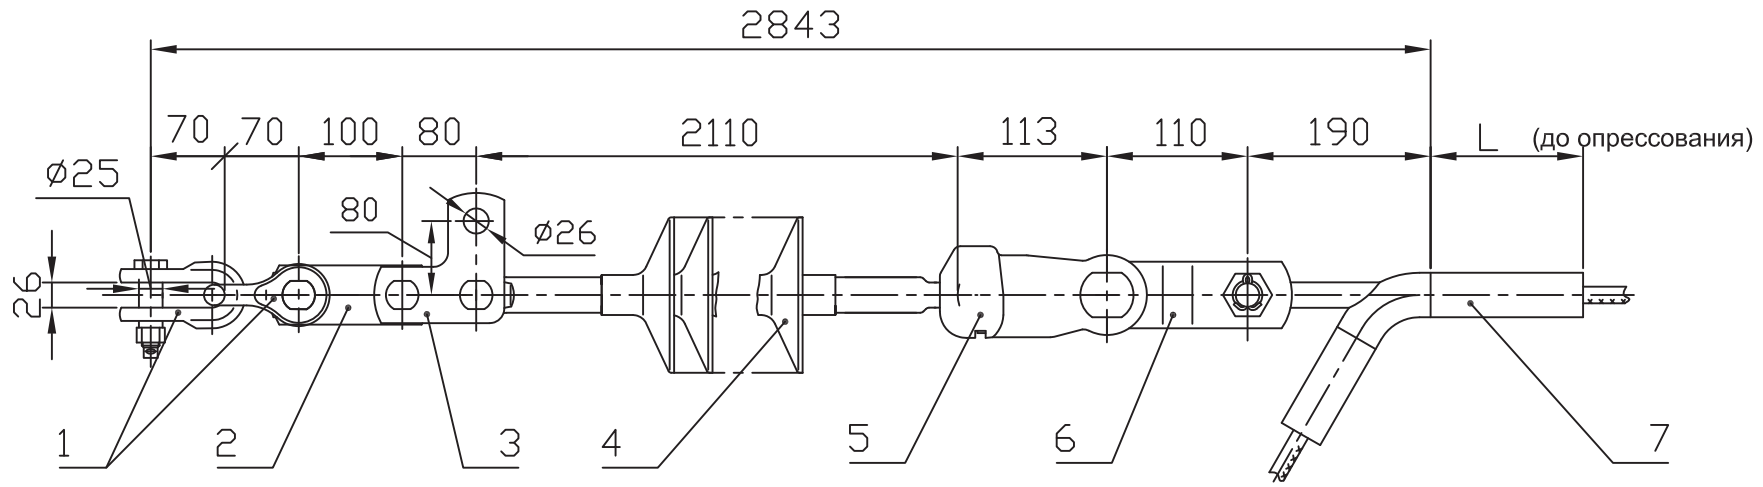

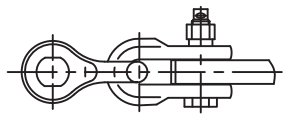

Вариант

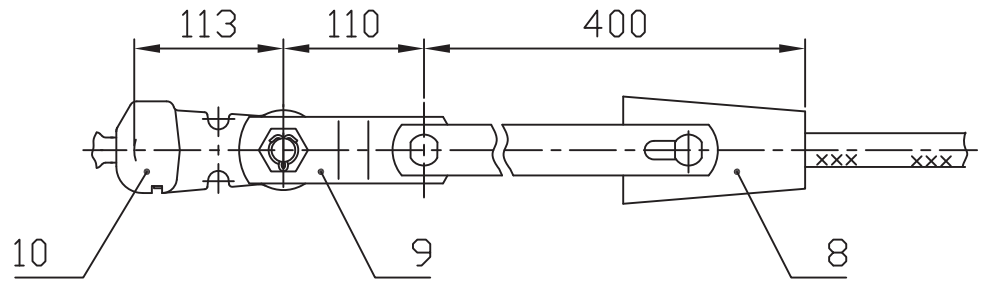

При заказе натяжного клинового зажима типа НК-300-1 следует указывать марку провода. Ушко У2-16-20 (поз.5) заменить на У1-16-20 (поз.10), а звено ПРТ-16/12-2 (поз. 6) на ПРТ-12/16-2 (поз.9).

Провод по ГОСТ 839-80		Зажим, поз.7			Масса армат., кг
Марка	Диаметр, мм	Обозначение	L, мм	Масса, кг	
АС240/56	22,4	НАС-330-1Б	175	1,99	11,80
АС300/39	24,0				
АС330/43	25,2	НАС-330-3Б	200	2,16	11,97

Поз.	Обозначение	Наименование	Кол.	Масса ед. кг	Прим.
1	СК-16-1А	Скоба	2	1,22	
2	ПР-16-6	Звено прямое	1	1,36	
3	ПТМ-16-3А	Звено монтажное	1	2,34	
4	ЛК 160/220-	Изолятор исп. СП	1	9,0	
5	У2-16-20	Ушко двухлапчатое	1	2,17	
6	ПРТ-16/12-2	Звено переходное	1	1,5	
7	См. табл.	Зажим натяжной	1	См. табл.	
8	НК-300-1	Зажим клиновой	1	5,1	
9	ПРТ-12/16-2	Звено переходное	1	1,6	
10	У1-16-20	Ушко однолапчатое	1	1,05	
Масса арматуры, кг				см. табл.	
Масса изолирующей подвески, кг				21,0	

Взам. инв. N

Подп. и дата

Инв. N подл.

ЭСИП-0035

ЭСС.001 ТМ - т.1


Утв.	Вигдергауз		
Пров.	Липунцов		
Разраб.	Власкина		


Натяжные одноцепные изолирующие с полимерными изоляторами ряда 160 кН подвески проводов АС240/56, АС300/39 и АС330/43 к а/у ж/б опорам ВЛ 220 кВ

Стадия	Лист	Листов
Р		1


Филиал ОАО "ФСК ЕЭС" "Электросетьсервис"

Формат А3

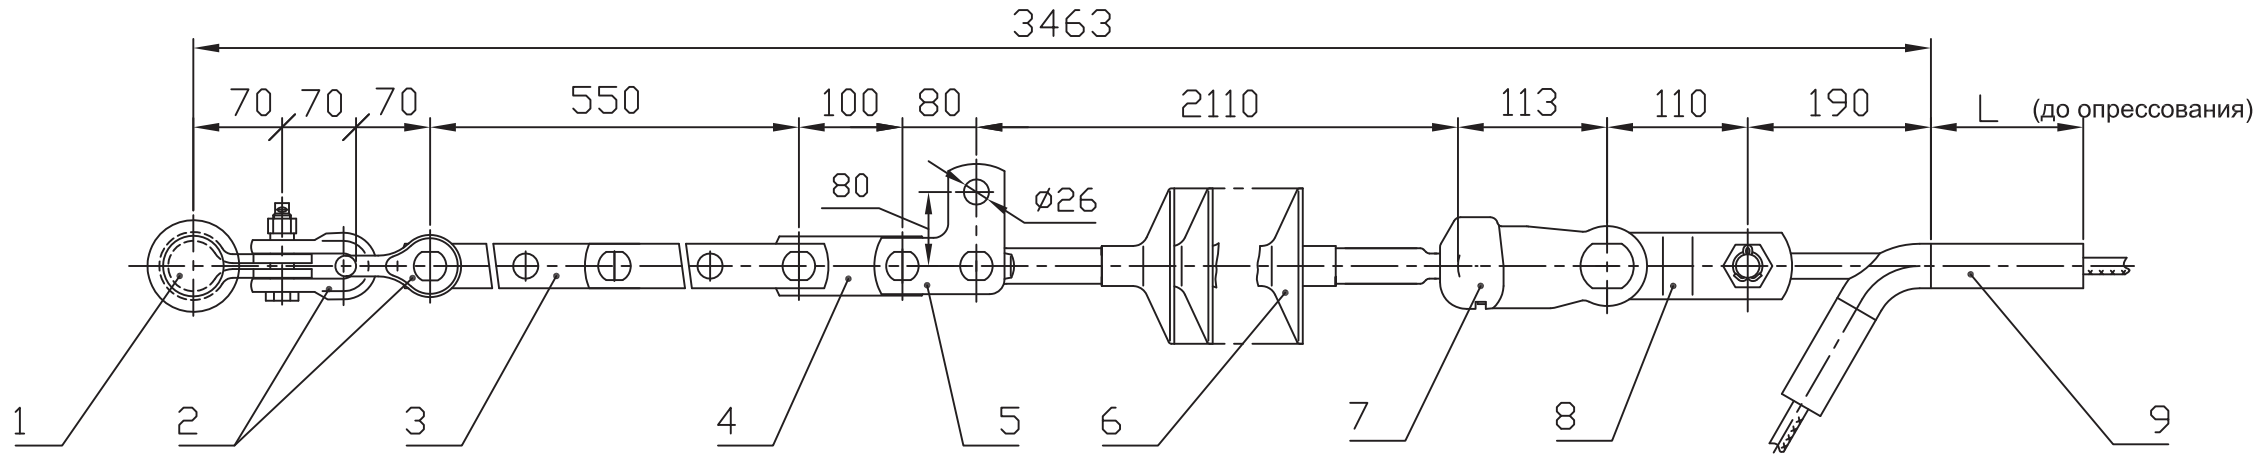

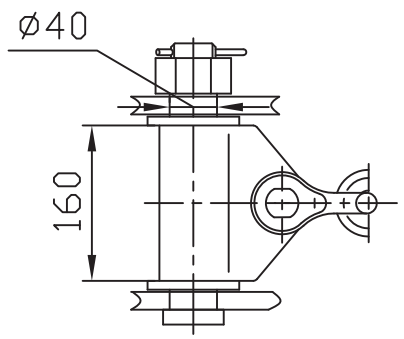

Вариант

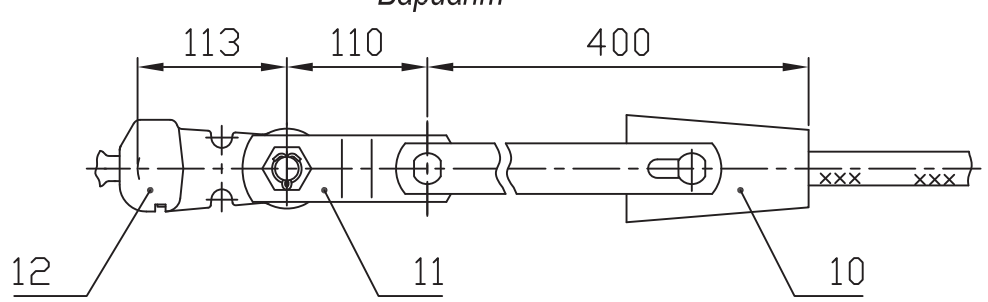

При заказе натяжного клинового зажима типа НК-300-1 следует указывать марку провода. Ушко У2-16-20 (поз.7) заменить на У1-16-20 (поз.12), а звено ПРТ-16/12-2 (поз. 8) на ПРТ-12/16-2 (поз.11).

Провод по ГОСТ 839-80		Зажим, поз.9			Масса армат., кг
Марка	Диаметр, мм	Обозначение	L, мм	Масса, кг	
АС240/56	22,4	НАС-330-1Б	175	1,99	22,03
АС300/39	24,0				
АС330/43	25,2	НАС-330-3Б	200	2,16	22,20

Поз.	Обозначение	Наименование	Кол.	Масса ед. кг	Прим.
1	КГН-16-5	Узел крепления	1	5,23	
2	СК-16-1А	Скоба	2	1,22	
3	ПРР-16-1	Звено регулируемое	1	5,00	
4	ПР-16-6	Звено прямое	1	1,36	
5	ПТМ-16-3А	Звено монтажное	1	2,34	
6	ЛК 160/220-	Изолятор исп. СП	1	9,0	
7	У2-16-20	Ушко двухлапчатое	1	2,17	
8	ПРТ-16/12-2	Звено переходное	1	1,5	
9	См. табл.	Зажим натяжной	1	См. табл.	
10	НК-300-1	Зажим клиновой	1	5,1	
11	ПРТ-12/16-2	Звено переходное	1	1,6	
12	У1-16-20	Ушко однолапчатое	1	1,6	
Масса арматуры, кг				см. табл.	
Масса изолирующей подвески, кг				31,2	

Утв.	Вигдергауз		
Пров.	Липунцов		
Разраб.	Власкина		

ЭСИП-0036

ЭСС.001 ТМ - т.1

Натяжные одноцепные изолирующие с полимерными изоляторами ряда 160 кН подвески проводов АС240/56, АС300/39 и АС330/43 к а/у металлическим опорам ВЛ 220 кВ

Стадия	Лист	Листов
Р		1


Филиал ОАО "ФСК ЕЭС" "Электросетьсервис"


Взам. инв. N

Подп. и дата


Инв. N подл.

Формат А3

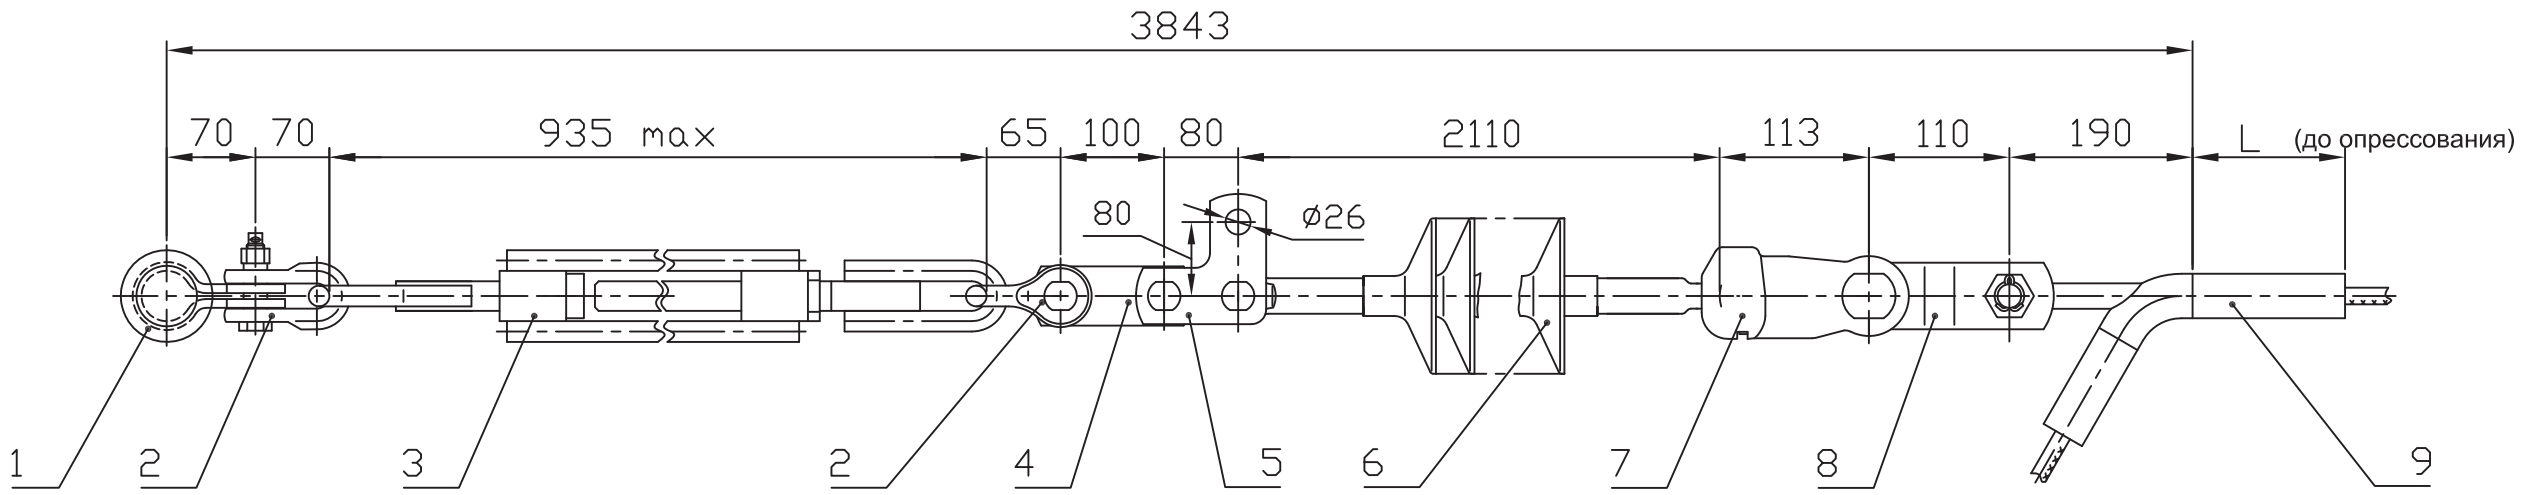

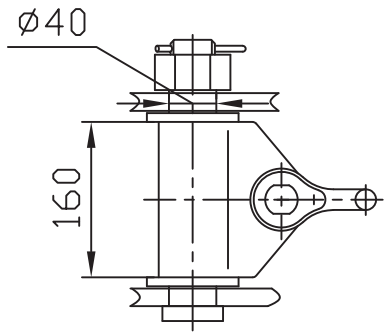

Вариант

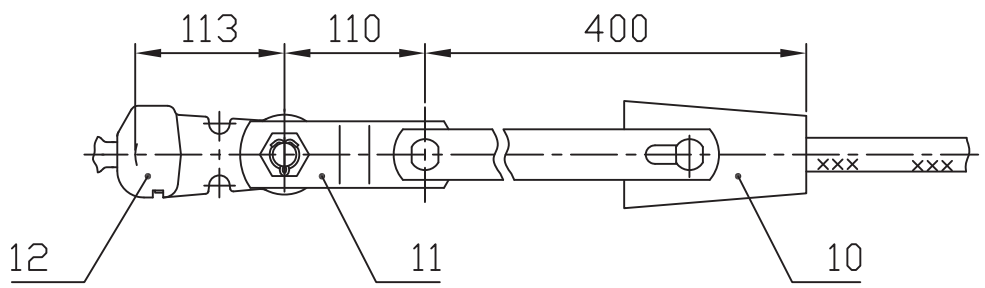

При заказе натяжного клинового зажима типа НК-300-1 следует указывать марку провода. Ушко У2-16-20 (поз.7) заменить на У1-16-20 (поз.12), а звено ПРТ-16/12-2 (поз. 8) на ПРТ-12/16-2 (поз.11).

Провод по ГОСТ 839-80		Зажим, поз.9			Масса армат., кг
Марка	Диаметр, мм	Обозначение	L, мм	Масса, кг	
АС240/56	22,4	НАС-330-1Б	175	1,99	24,21
АС300/39	24,0				
АС330/43	25,2	НАС-330-3Б	200	2,16	24,38

Поз.	Обозначение	Наименование	Кол.	Масса ед. кг	Прим.
1	КГН-16-5	Узел крепления	1	5,23	
2	СК-16-1А	Скоба	2	1,22	
3	ПТР-16-1	Талреп	1	7,18	
4	ПР-16-6	Звено прямое	1	1,36	
5	ПТМ-16-3А	Звено монтажное	1	2,34	
6	ЛК 160/220-	Изолятор исп. СП	1	9,0	
7	У2-16-20	Ушко двухлапчатое	1	2,17	
8	ПРТ-16/12-2	Звено переходное	1	1,5	
9	См. табл.	Зажим натяжной	1	См. табл.	
10	НК-300-1	Зажим клиновой	1	5,1	
11	ПРТ-12/16-2	Звено переходное	1	1,6	
12	У1-16-20	Ушко однолапчатое	1	1,6	
Масса арматуры, кг				см. табл.	
Масса изолирующей подвески, кг				33,4	

ЭСИП-0037

ЭСС.001 ТМ - т.1


Утв.	Вигдергауз	Натяжные одноцепные изолирующие с полимерными изоляторами ряда 160 кН подвески проводов АС240/56, АС300/39 и АС330/43 к а/у металлическим опорам ВЛ 220 кВ	
Пров.	Липунцов		
Разраб.	Власкина		


Стадия	Лист	Листов
Р		1

Филиал ОАО "ФСК ЕЭС" "Электросетьсервис"


Взам. инв. N | Подп. и дата | Инв. N подл.

Формат А3

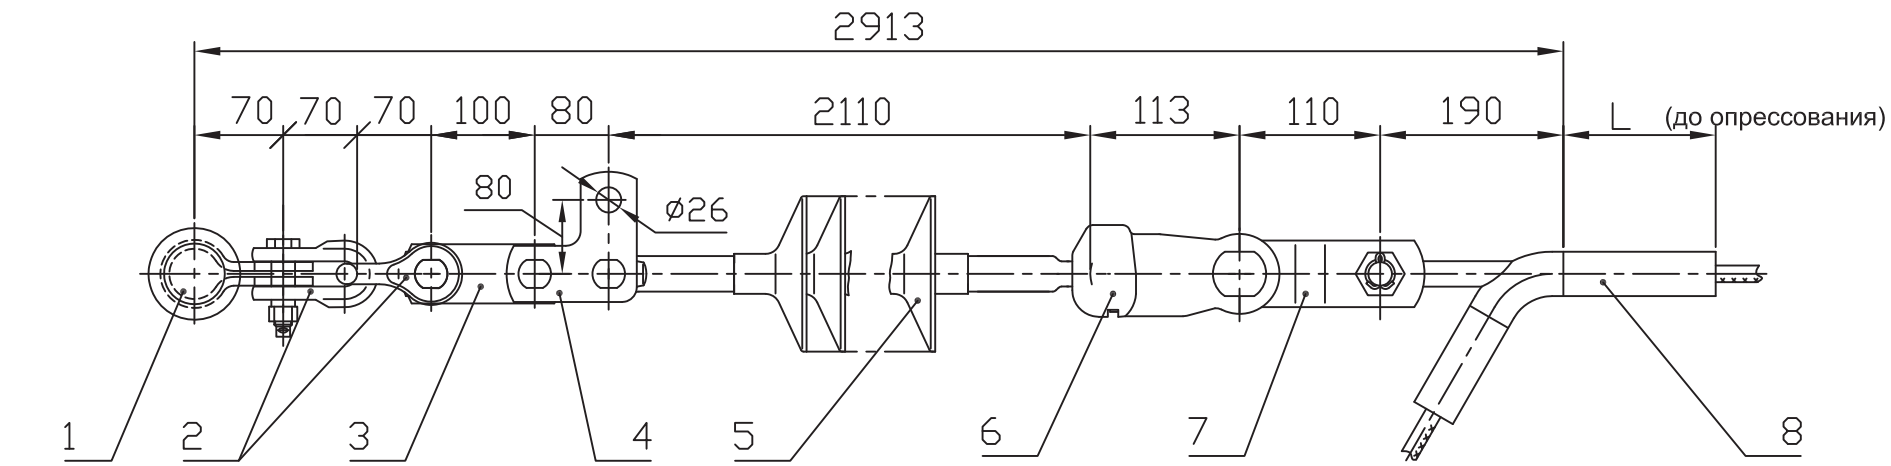

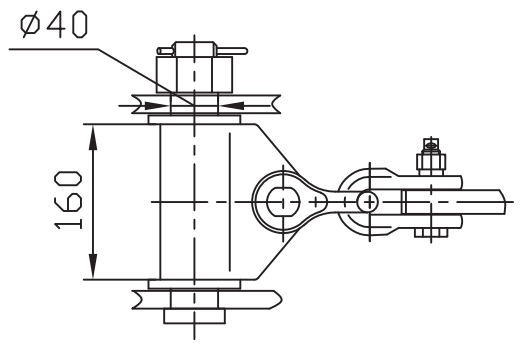

Вариант

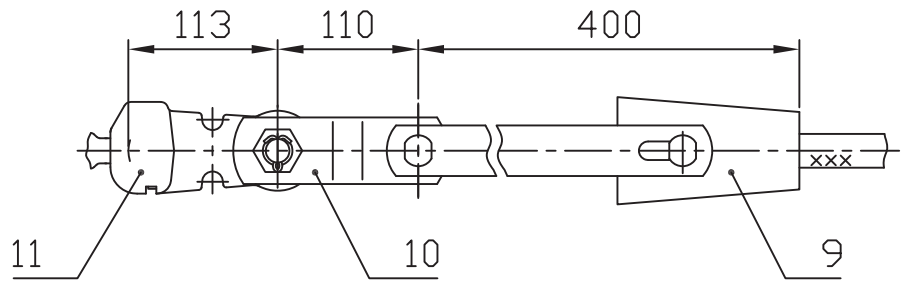

При заказе натяжного клинового зажима типа НК-300-1 следует указывать марку провода. Ушко У2-16-20 (поз.7) заменить на У1-16-20 (поз.12), а звено ПРТ-16/12-2 (поз. 8) на ПРТ-12/16-2 (поз.11).


Провод по ГОСТ 839-80		Зажим, поз.8			Масса армат., кг
Марка	Диаметр, мм	Обозначение	L, мм	Масса, кг	
АС240/56	22,4	НАС-330-1Б	175	1,99	17,03
АС300/39	24,0				
АС330/43	25,2	НАС-330-3Б	200	2,16	17,20


Поз.	Обозначение	Наименование	Кол.	Масса ед. кг	Прим.
1	КГН-16-5	Узел крепления	1	5,23	
2	СК-16-1А	Скоба	2	1,22	
3	ПР-16-6	Звено прямое	1	1,36	
4	ПТМ-16-3А	Звено монтажное	1	2,34	
5	ЛК 160/220-	Изолятор исп. СП	1	9,0	
6	У2-16-20	Ушко двухлапчатое	1	2,17	
7	ПРТ-16/12-2	Звено переходное	1	1,5	
8	См. табл.	Зажим натяжной	1	См. табл.	
9	НК-300-1	Зажим клиновой	1	5,1	
10	ПРТ-12/16-2	Звено переходное	1	1,6	
11	У1-16-20	Ушко однолапчатое	1	1,6	
Масса арматуры, кг				см. табл.	
Масса изолирующей подвески, кг				26,2	

		ЭСИП-0038	
		ЭСС.001 ТМ - т.1	
Утв.	Вигдергауз	Натяжные одноцепные изолирующие с полимерными изоляторами ряда 160 кН подвески проводов АС240/56, АС300/39 и АС330/43 к а/у металлическим опорам ВЛ 220 кВ	Стадия: Р; Лист: ; Листов: 1
Пров.	Липунцов		Филиал ОАО "ФСК ЕЭС" "Электросетьсервис"
Разраб.	Власкина		


Взам. инв. N | Подп. и дата | Инв. N подл.

Формат А3

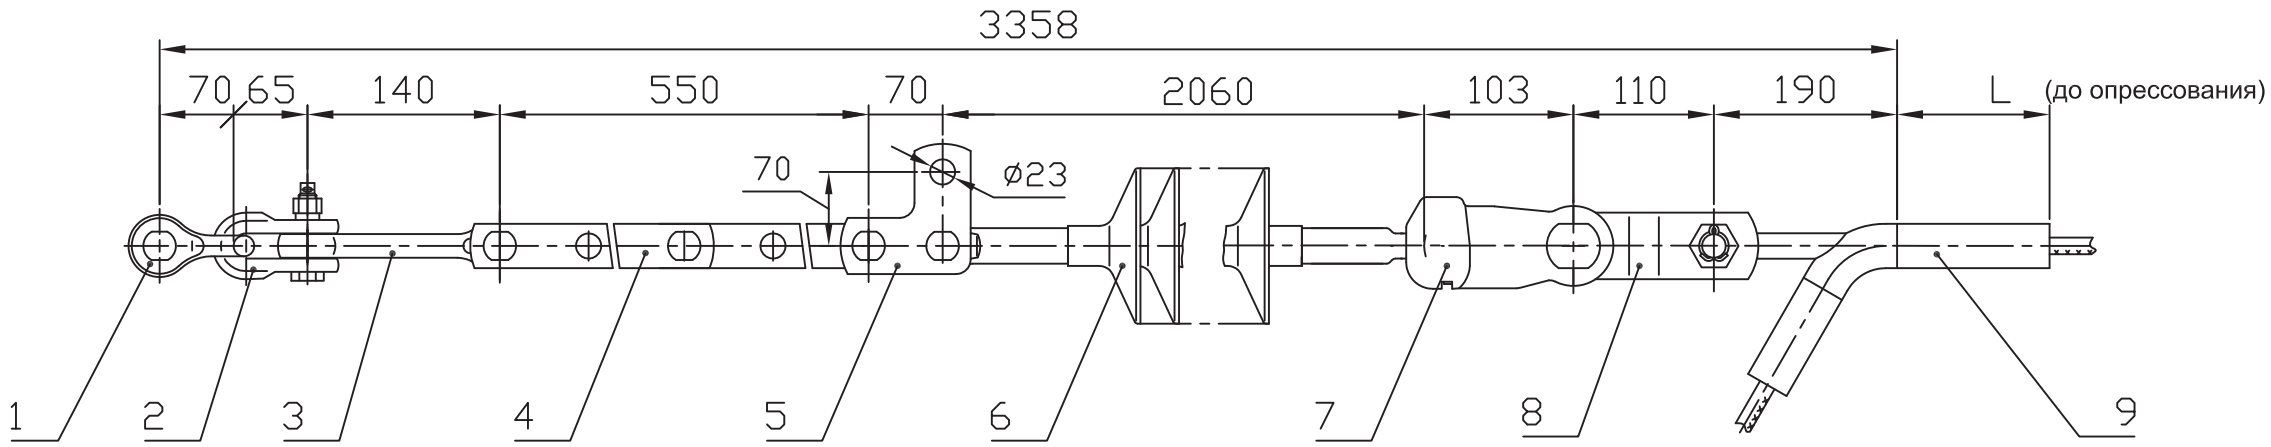

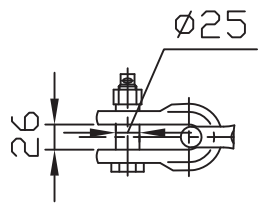

Вариант

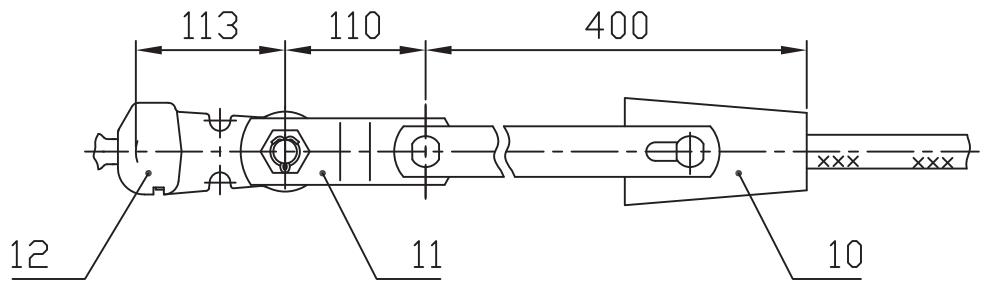

При заказе натяжного клинового зажима типа НК-400-1 следует указывать марку провода. Ушко У2-16-20 (поз.7) заменить на У1-16-20 (поз.12), а звено ПРТ-16/12-2 (поз. 8) на ПРТ-12/16-2 (поз.11).

Провод по ГОСТ 839-80		Зажим, поз.9			Масса армат., кг
Марка	Диаметр, мм	Обозначение	L, мм	Масса, кг	
АС300/67	24,5	НАС-300-1Б	165	2,41	13,82
АС400/51	27,5	НАС-450-1Б	210	2,78	14,19

Поз.	Обозначение	Наименование	Кол.	Масса ед. кг	Прим.
1	СК-16-1А	Скоба	1	1,22	
2	СК-120-1Б	Скоба	1	0,92	
3	ПРВ-12-1	Звено вывернутое	1	0,74	
4	ПРР-12-1	Звено регулируемое	1	3,69	
5	ПТМ-12-3А	Звено монтажное	1	1,7	
6	ЛК 120/220-	Изолятор исп.СП	1	9,0	
7	У2-12-16	Ушко двухлапчатое	1	1,54	
8	ПРТ-12/16-2	Звено переходное	1	1,6	
9	См. табл.	Зажим натяжной	1	См. табл.	
10	НК-400-1	Зажим клиновой	1	5,2	
11	ПРТ-16/12-2	Звено переходное	1	1,5	
12	У1-12-16	Ушко однолапчатое	1	1,05	
Масса арматуры, кг				см. табл.	
Масса изолирующей подвески, кг				23,2	

Взам. инв. N

Подп. и дата

Инв. N подл.

Утв.	Вигдергауз		
Пров.	Липунцов		
Разраб.	Власкина		

ЭСИП-0039


ЭСС.001 ТМ - т.1


Натяжные одноцепные изолирующие с полимерными изоляторами ряда 120 кН подвески проводов АС300/67, АС400/51 к а/у деревянным опорам ВЛ 220 кВ


Стадия	Лист	Листов
Р		1

Филиал ОАО "ФСК ЕЭС" "Электросетьсервис"

Формат А3

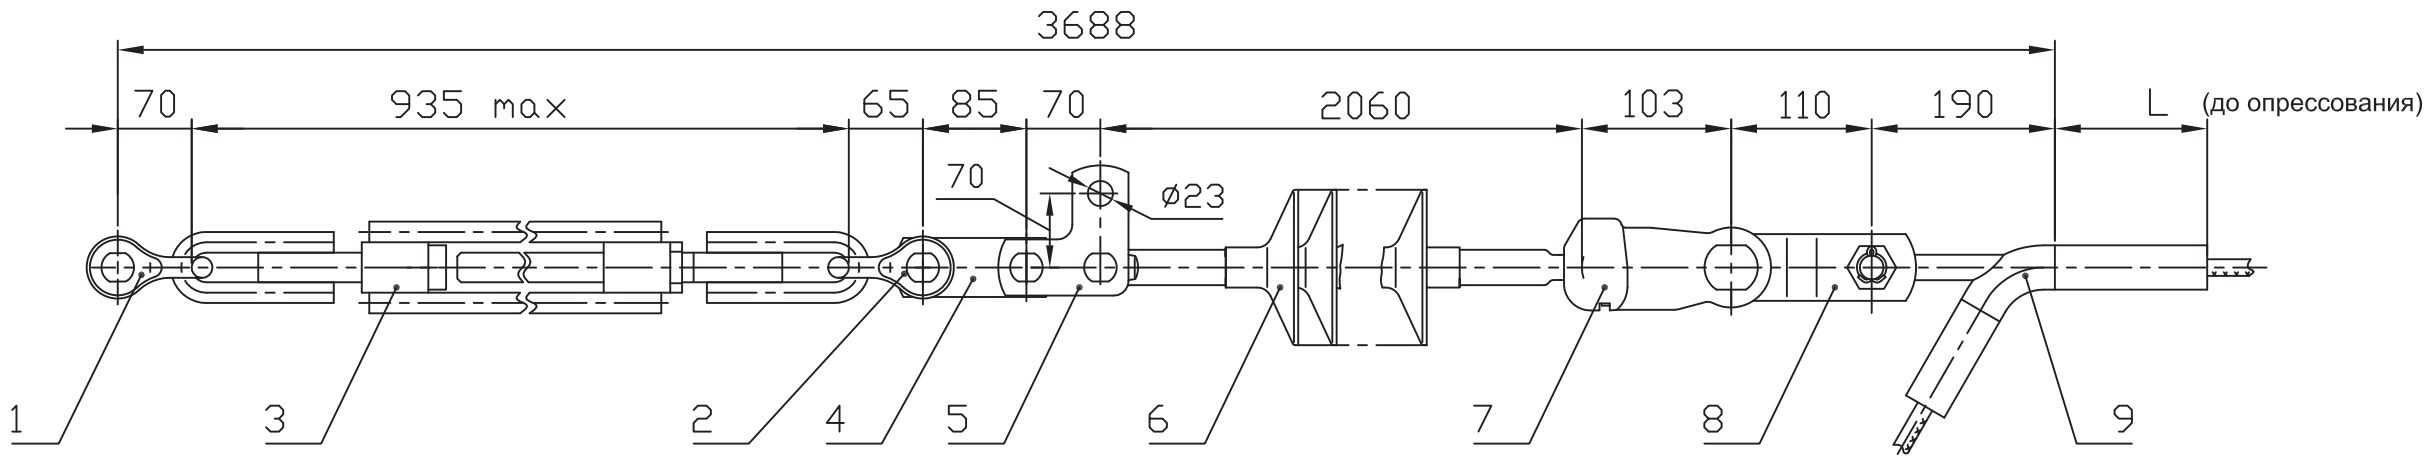

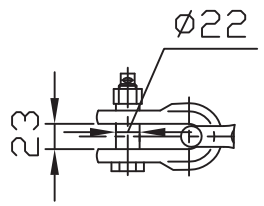

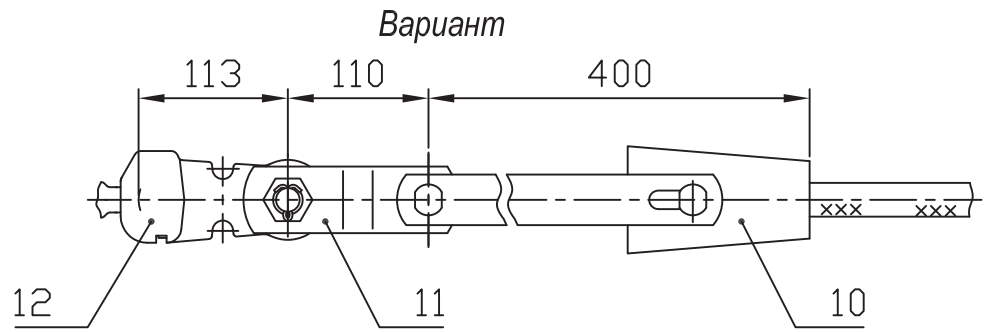

При заказе натяжного клинового зажима типа НК-400-1 следует указывать марку провода. Ушко У2-16-20 (поз.7) заменить на У1-16-20 (поз.12), а звено ПРТ-16/12-2 (поз. 8) на ПРТ-12/16-2 (поз.11).

Провод по ГОСТ 839-80		Зажим, поз.9			Масса армат., кг
Марка	Диаметр, мм	Обозначение	L, мм	Масса, кг	
АС300/67	24,5	НАС-300-1Б	165	2,41	16,4
АС400/51	27,5	НАС-450-1Б	210	2,78	16,8

Поз.	Обозначение	Наименование	Кол.	Масса ед. кг	Прим.
1	СК-16-1А	Скоба	1	1,22	
2	СК-120-1Б	Скоба	1	0,92	
3	ПТР-12-1	Талреп	1	5,67	
4	ПР-12-6	Звено прямое	1	1,36	
5	ПТМ-12-3А	Звено монтажное	1	1,7	
6	ЛК 120/220-	Изолятор исп. СП	1	8,0	
7	У2-12-16	Ушко двухлапчатое	1	1,54	
8	ПРТ-12/16-2	Звено переходное	1	1,6	
9	См. табл.	Зажим натяжной	1	См. табл.	
10	НК-400-1	Зажим клиновой	1	5,2	
11	ПРТ-16/12-2	Звено переходное	1	1,5	
12	У1-12-16	Ушко однолапчатое	1	1,05	
Масса арматуры, кг				см. табл.	
Масса изолирующей подвески, кг				24,8	

Взам. инв. N

Подп. и дата

Инв. N подл.

ЭСИП-0040

ЭСС.001 ТМ - т.1


Утв.	Вигдергауз
Пров.	Липунцов
Разраб.	Власкина


Натяжные одноцепные изолирующие с полимерными изоляторами ряда 120 кН подвески проводов АС300/67,АС400/51 к а/у деревянным опорам ВЛ 220 кВ

Стадия	Лист	Листов
Р		1


Филиал ОАО "ФСК ЕЭС" "Электросетьсервис"

Формат А3

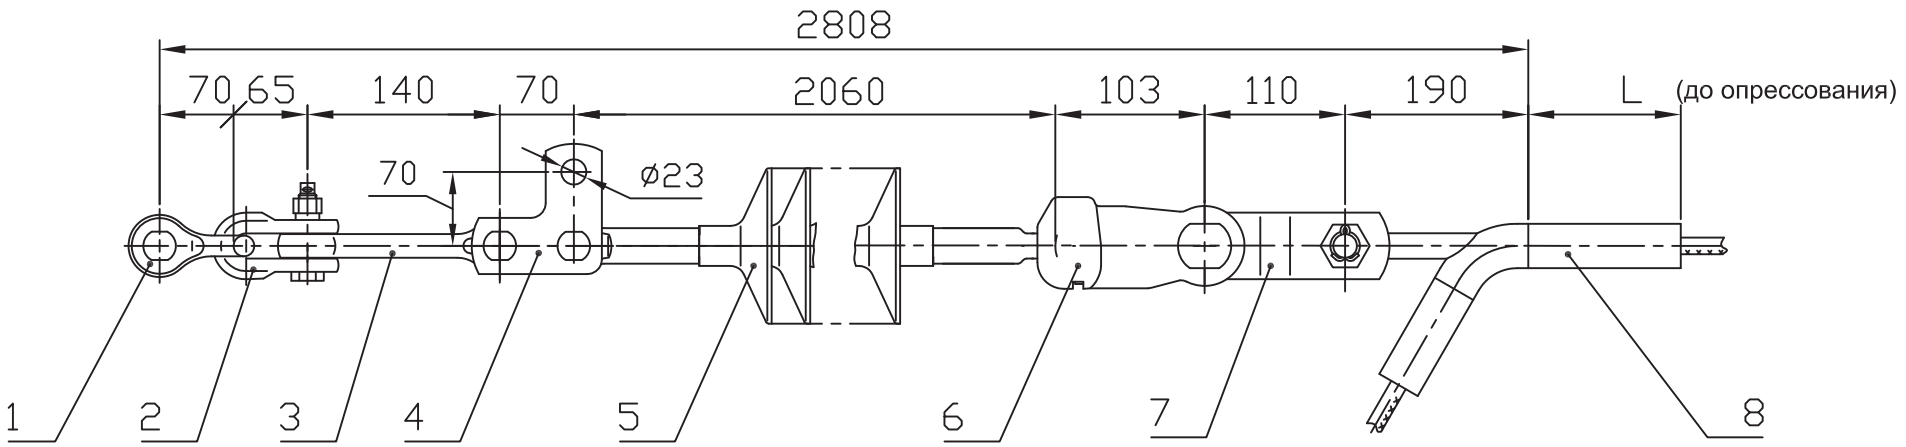

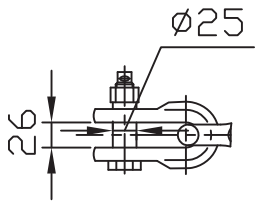

Вариант

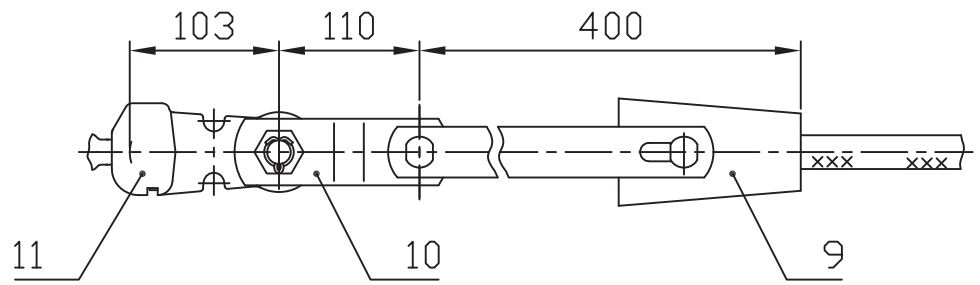

При заказе натяжного клинового зажима типа НК-400-1 следует указывать марку провода.
Ушко У2-16-20 (поз.6) заменить на У1-16-20 (поз.11), а звено ПРТ-12/16-2 (поз.7) на ПРТ-16/12-2 (поз.10).

Провод по ГОСТ 839-80		Зажим, поз.8			Масса армат., кг
Марка	Диаметр, мм	Обозначение	L, мм	Масса, кг	
АС300/67	24,5	НАС-300-1Б	165	2,41	10,13
АС400/51	27,5	НАС-450-1Б	210	2,78	10,50

Поз.	Обозначение	Наименование	Кол.	Масса ед. кг	Прим.
1	СК-16-1А	Скоба	1	1,22	
2	СК-120-1Б	Скоба	1	0,92	
3	ПРВ-12-1	Звено вывернутое	1	0,74	
4	ПТМ-12-3А	Звено монтажное	1	1,7	
5	ЛК 120/220-	Изолятор исп. СП	1	8,0	
6	У2-12-16	Ушко двухлапчатое	1	1,54	
7	ПРТ-12/16-2	Звено переходное	1	1,6	
8	См. табл.	Зажим натяжной	1	См. табл.	
9	НК-400-1	Зажим клиновой	1	5,2	
10	ПРТ-16/12-2	Звено переходное	1	1,5	
11	У1-12-16	Ушко однолапчатое	1	1,05	
Масса арматуры, кг				см. табл.	
Масса изолирующей подвески, кг				18,5	

Взам. инв. N | Подп. и дата | Инв. N подл.

Утв.	Вигдергауз		
Пров.	Липунцов		
Разраб.	Власкина		

ЭСИП-0041


ЭСС.001 ТМ - т.1


Натяжные одноцепные изолирующие с полимерными изоляторами ряда 120 кН подвески проводов АС300/67, АС400/51 к а/у деревянным опорам ВЛ 220 кВ


Стадия	Лист	Листов
Р		1

Филиал ОАО "ФСК ЕЭС" "Электросетьсервис"

Формат А3

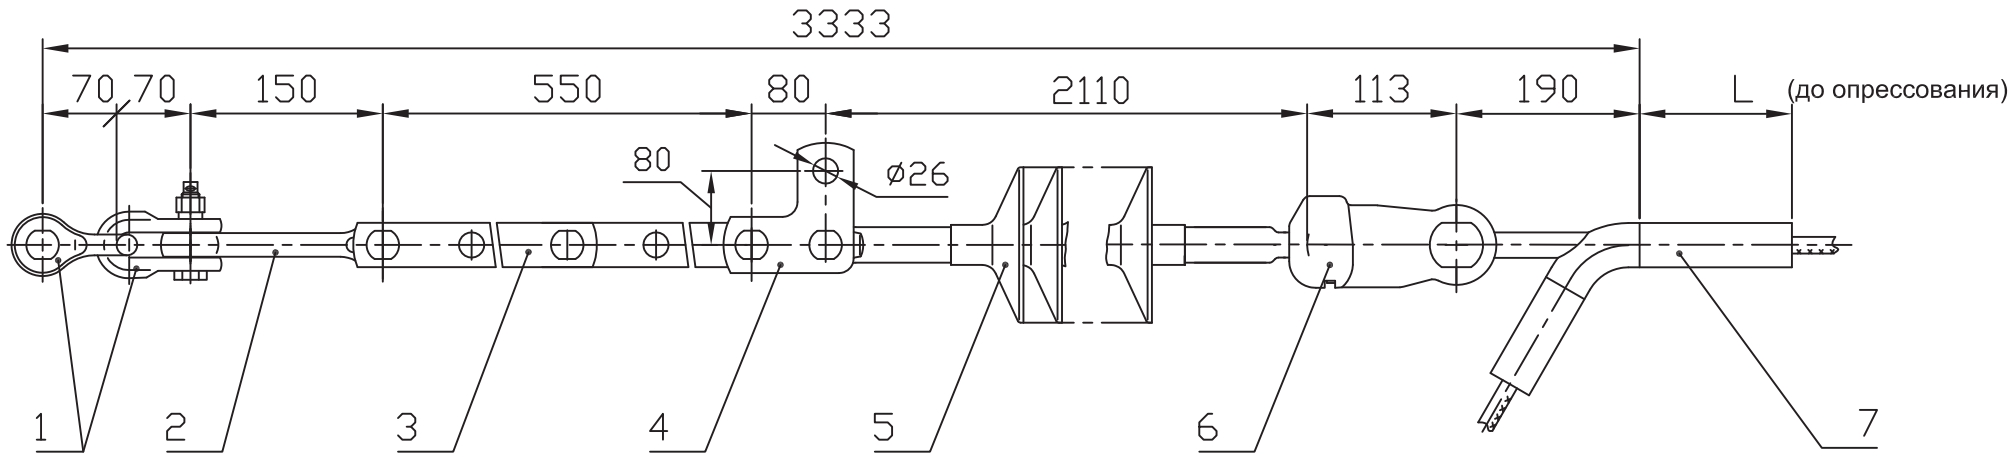

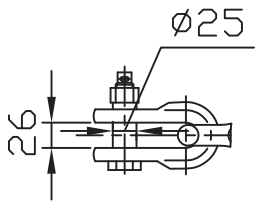

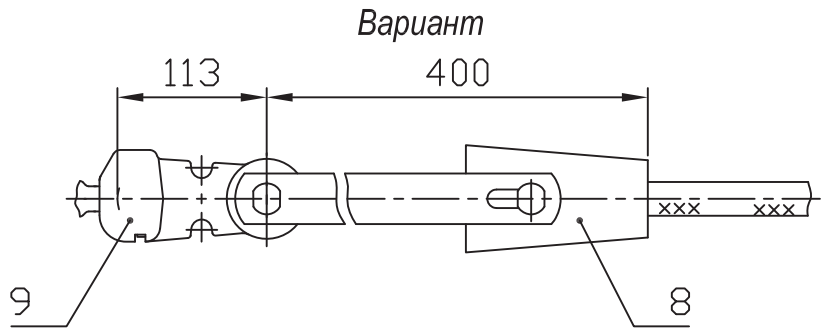

При заказе натяжного клинового зажима типа НК-400-1 следует указывать марку провода.
Ушко У2-16-20 (поз.6) заменить на У1-16-20 (поз.9)

Провод по ГОСТ 839-80		Зажим, поз.7			Масса армат., кг
Марка	Диаметр, мм	Обозначение	L, мм	Масса, кг	
АС300/67	24,5	НАС-300-1Б	165	2,41	15,27
АС400/51	27,5	НАС-450-1Б	210	2,78	15,64

Поз.	Обозначение	Наименование	Кол.	Масса ед. кг	Прим.
1	СК-16-1А	Скоба	2	1,22	
2	ПРВ-16-1	Звено вывернутое	1	0,91	
3	ПРР-16-1	Звено регулируемое	1	5,0	
4	ПТМ-16-3А	Звено монтажное	1	2,34	
5	ЛК 160/220-	Изолятор исп. СП	1	9,0	
6	У2-16-20	Ушко двухлапчатое	1	2,17	
7	См. табл.	Зажим натяжной	1	См. табл.	
8	НК-400-1	Зажим клиновой	1	5,2	
9	У1-16-20	Ушко однолапчатое	1	1,6	
Масса арматуры, кг				см. табл.	
Масса изолирующей подвески, кг				24,6	

Утв.	Вигдергауз		
Пров.	Липунцов		
Разраб.	Власкина		

ЭСИП-0042

ЭСС.001 ТМ - т.1

Натяжные одноцепные изолирующие с полимерными изоляторами ряда 160 кН подвески проводов АС300/67, АС400/51 к а/у деревянным опорам ВЛ 220 кВ

Стадия	Лист	Листов
Р		1


Филиал ОАО "ФСК ЕЭС" "Электросетьсервис"


Взам. инв. N


Подп. и дата

Инв. N подл.

Формат А3

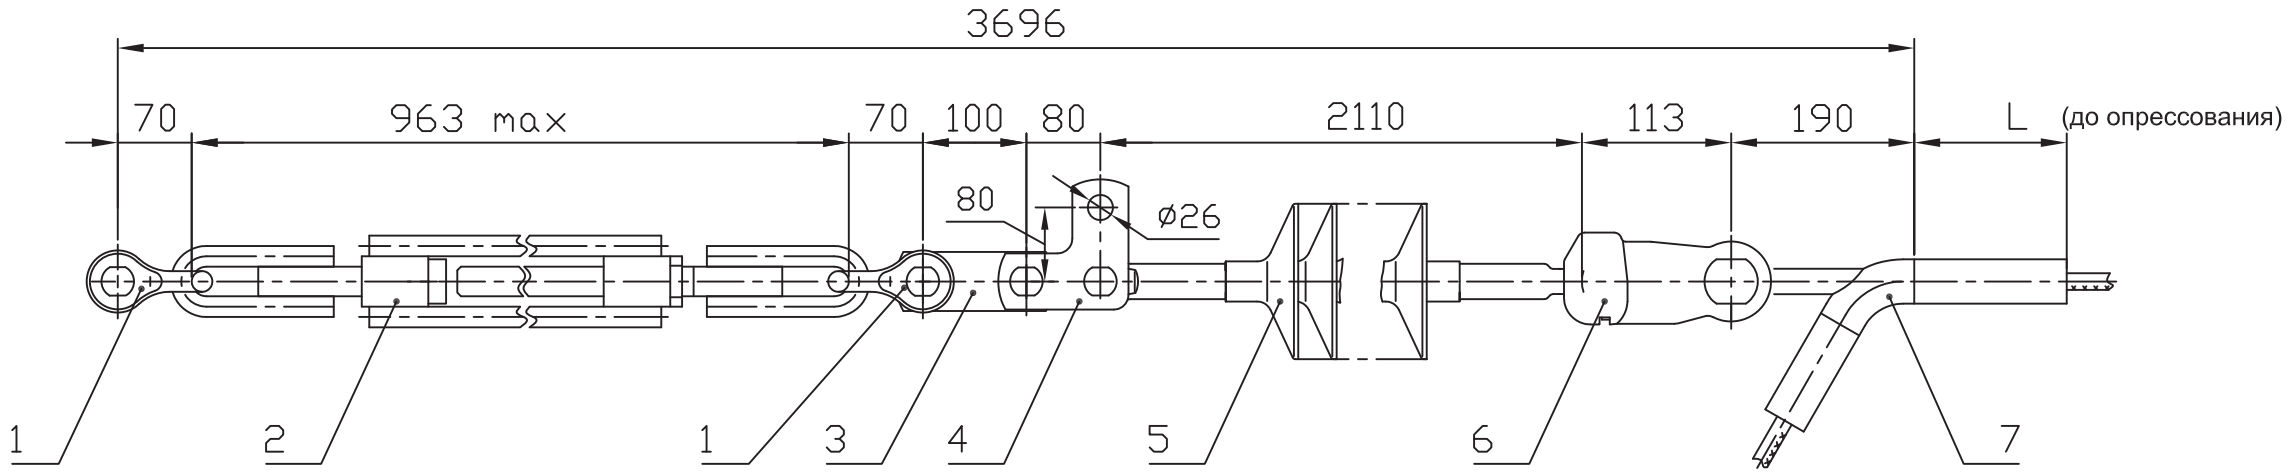

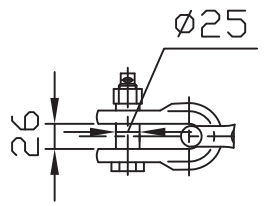

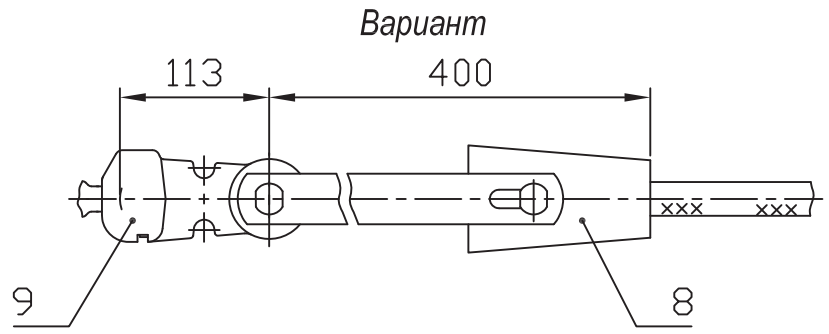

При заказе натяжного клинового зажима типа НК-400-1 следует указывать марку провода.
Ушко У2-16-20 (поз.6) заменить на У1-16-20 (поз.9)

Поз.	Обозначение	Наименование	Кол.	Масса ед. кг	Прим.
1	СК-16-1А	Скоба	2	1,22	
2	ПТР-16-1	Талреп	1	5,67	
3	ПР-16-6	Звено прямое	1	1,36	
4	ПТМ-16-3А	Звено монтажное	1	1,7	
5	ЛК 160/220-	Изолятор исп. СП	1	9,0	
6	У2-16-20	Ушко двухлапчатое	1	1,54	
7	См. табл.	Зажим натяжной	1	См. табл.	
8	НК-400-1	Зажим клиновой	1	5,2	
9	У1-16-20	Ушко однолапчатое	1	1,6	
Масса арматуры, кг				см. табл.	
Масса изолирующей подвески, кг				24,5	

Провод по ГОСТ 839-80		Зажим, поз.7			Масса армат., кг
Марка	Диаметр, мм	Обозначение	L, мм	Масса, кг	
АС300/67	24,5	НАС-300-1Б	165	2,41	15,1
АС400/51	27,5	НАС-450-1Б	210	2,78	15,5


Взам. инв. N


Подп. и дата


Инв. N подл.

		ЭСИП-0043	
		ЭСС.001 ТМ - т.1	
Утв.	Вигдергауз	Натяжные одноцепные изолирующие с полимерными изоляторами ряда 160 кН подвески проводов АС300/67,АС400/51 к а/у деревянным опорам ВЛ 220 кВ	Стадия: Р; Лист: ; Листов: 1
Пров.	Липунцов		Филиал ОАО "ФСК ЕЭС" "Электросетьсервис"
Разраб.	Власкина		

Формат А3

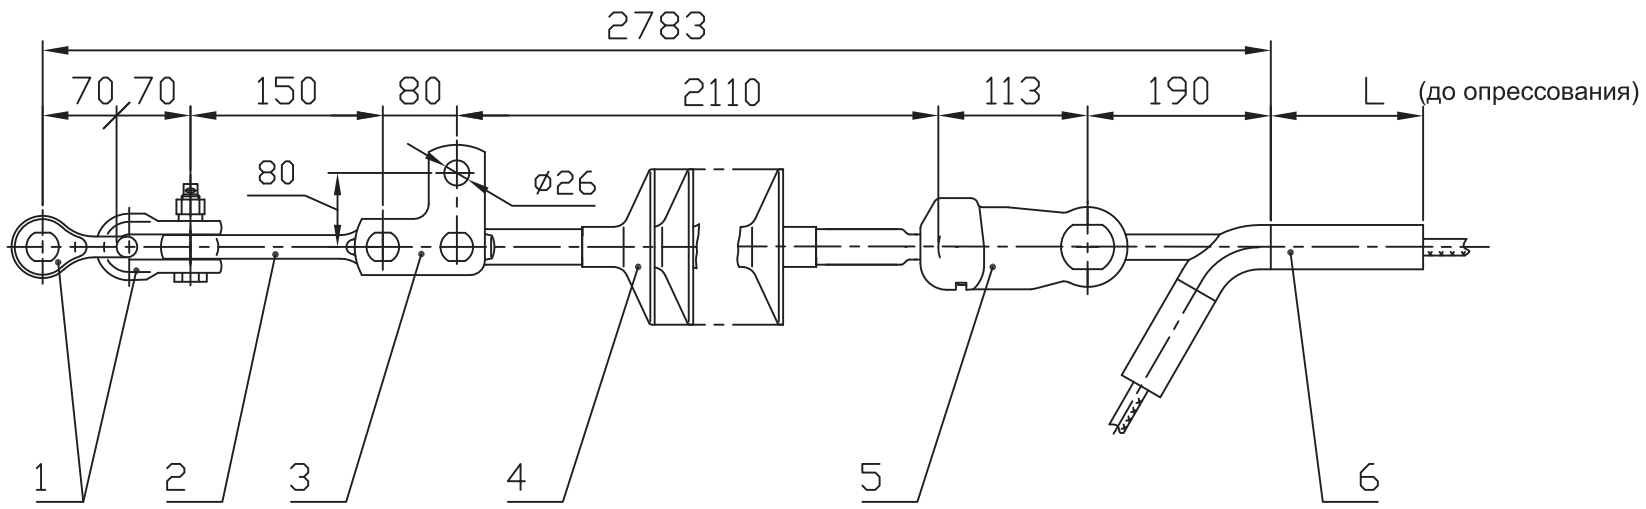

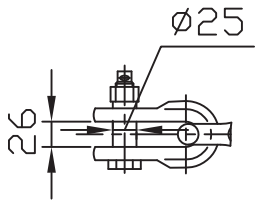

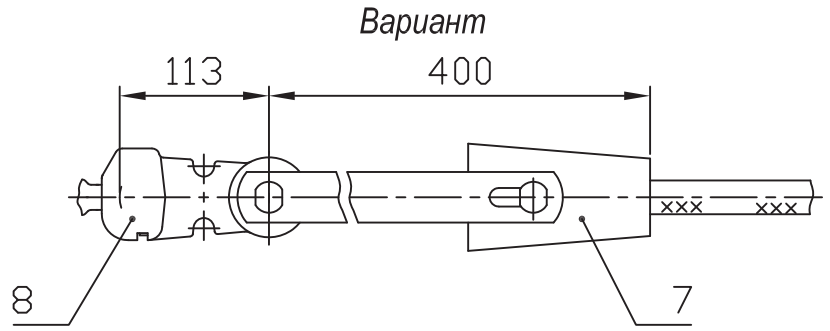

При заказе натяжного клинового зажима типа НК-400-1 следует указывать марку провода.
Ушко У2-16-20 (поз.5) заменить на У1-16-20 (поз.8)

Поз.	Обозначение	Наименование	Кол.	Масса ед. кг	Прим.
1	СК-16-1А	Скоба	2	1,22	
2	ПРВ-16-1	Звено вывернутое	1	0,91	
3	ПТМ-16-3А	Звено монтажное	1	2,34	
4	ЛК160/220-	Изолятор исп. СП	1	9,0	
5	У2-16-20	Ушко двухлапчатое	1	2,17	
6	См. табл.	Зажим натяжной	1	См. табл.	
7	НК-400-1	Зажим клиновой	1	5,2	
8	У1-16-20	Ушко однолапчатое	1	1,6	
Масса арматуры, кг				см. табл.	
Масса изолирующей подвески, кг				19,6	

Провод по ГОСТ 839-80		Зажим, поз.6			Масса армат., кг
Марка	Диаметр, мм	Обозначение	L, мм	Масса, кг	
АС300/67	24,5	НАС-300-1Б	165	2,41	10,27
АС400/51	27,5	НАС-450-1Б	210	2,78	10,64

Утв.	Вигдергауз		
Пров.	Липунцов		
Разраб.	Власкина		

ЭСИП-0044

ЭСС.001 ТМ - т.1

Натяжные одноцепные изолирующие с полимерными изоляторами ряда 160 кН подвески проводов АС300/67, АС400/51 к а/у деревянным опорам ВЛ 220 кВ

Стадия	Лист	Листов
Р		1


Филиал ОАО "ФСК ЕЭС" "Электросетьсервис"


Взам. инв. N

Подп. и дата


Инв. N подл.

Формат А3

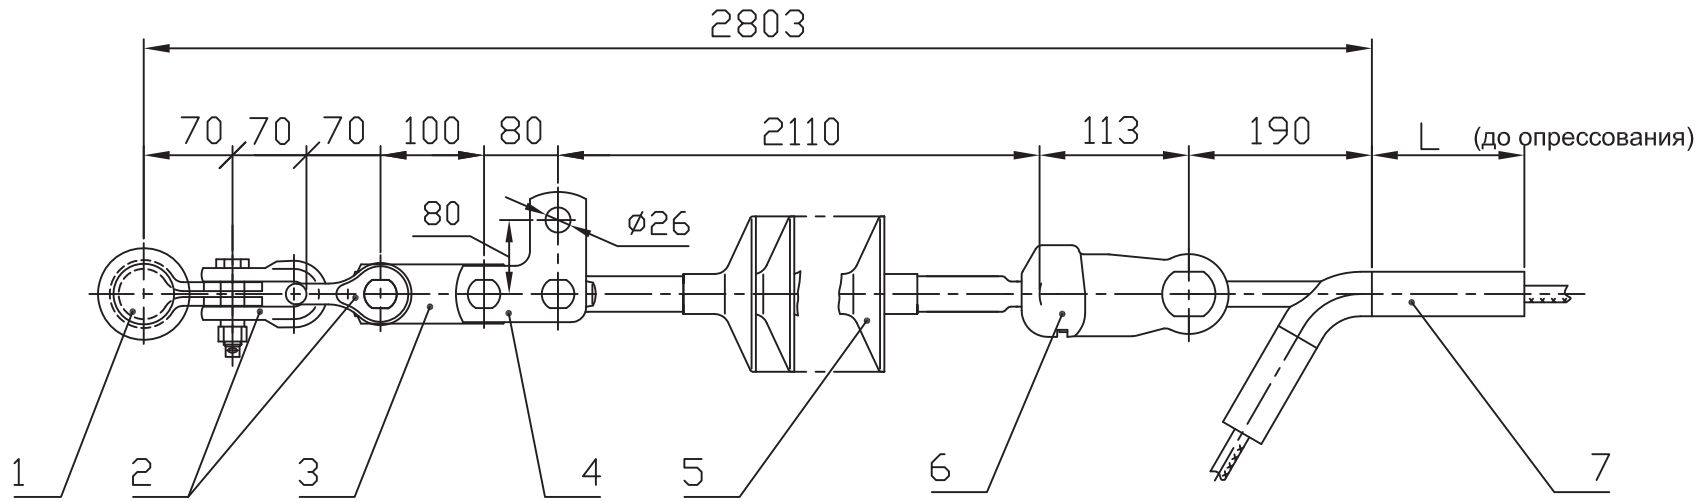

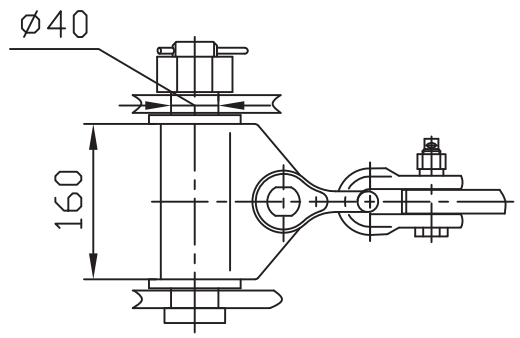

Вариант

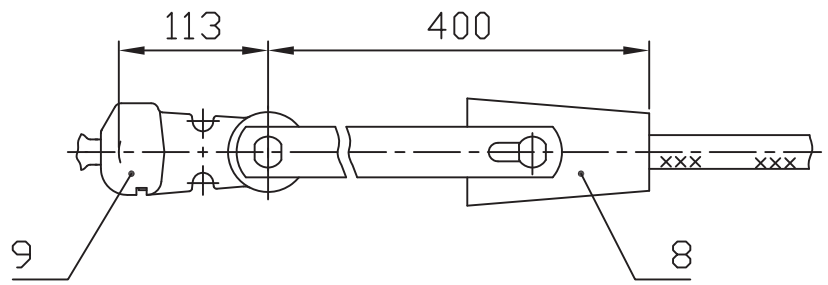

При заказе натяжного клинового зажима типа НК-400-1 следует указывать марку провода.
Ушко У2-16-20 (поз.6) заменить на У1-16-20 (поз.9)


Поз.	Обозначение	Наименование	Кол.	Масса ед. кг	Прим.
1	КГН-16-5	Узел крепления	1	5,23	
2	СК-16-1А	Скоба	2	1,22	
3	ПР-16-6	Звено прямое	1	1,36	
4	ПТМ-16-3А	Звено монтажное	1	2,34	
5	ЛК 160/220-	Изолятор исп. СП	1	9,0	
6	У2-16-20	Ушко двухлапчатое	1	2,17	
7	См. табл.	Зажим натяжной	1	См. табл.	
8	НК-400-1	Зажим клиновой	1	5,2	
9	У1-16-20	Ушко однолапчатое	1	1,6	
Масса арматуры, кг				см. табл.	
Масса изолирующей подвески, кг				25,3	


Провод по ГОСТ 839-80		Зажим, поз.7			Масса армат., кг
Марка	Диаметр, мм	Обозначение	L, мм	Масса, кг	
АС300/67	24,5	НАС-300-1Б	165	2,41	15,95
АС400/51	27,5	НАС-450-1Б	210	2,78	16,32


		ЭСИП-0045	
		ЭСС.001 ТМ - т.1	
Утв.	Вигдергауз	Натяжные одноцепные изолирующие с полимерными изоляторами ряда 160 кН подвески проводов АС300/67, АС400/51 к а/у металлическим опорам ВЛ 220 кВ	Стадия: Р; Лист: ; Листов: 1
Пров.	Липунцов		Филиал ОАО "ФСК ЕЭС" "Электросетьсервис"
Разраб.	Власкина		

Взам. инв. N | Подп. и дата | Инв. N подл.

Формат А3

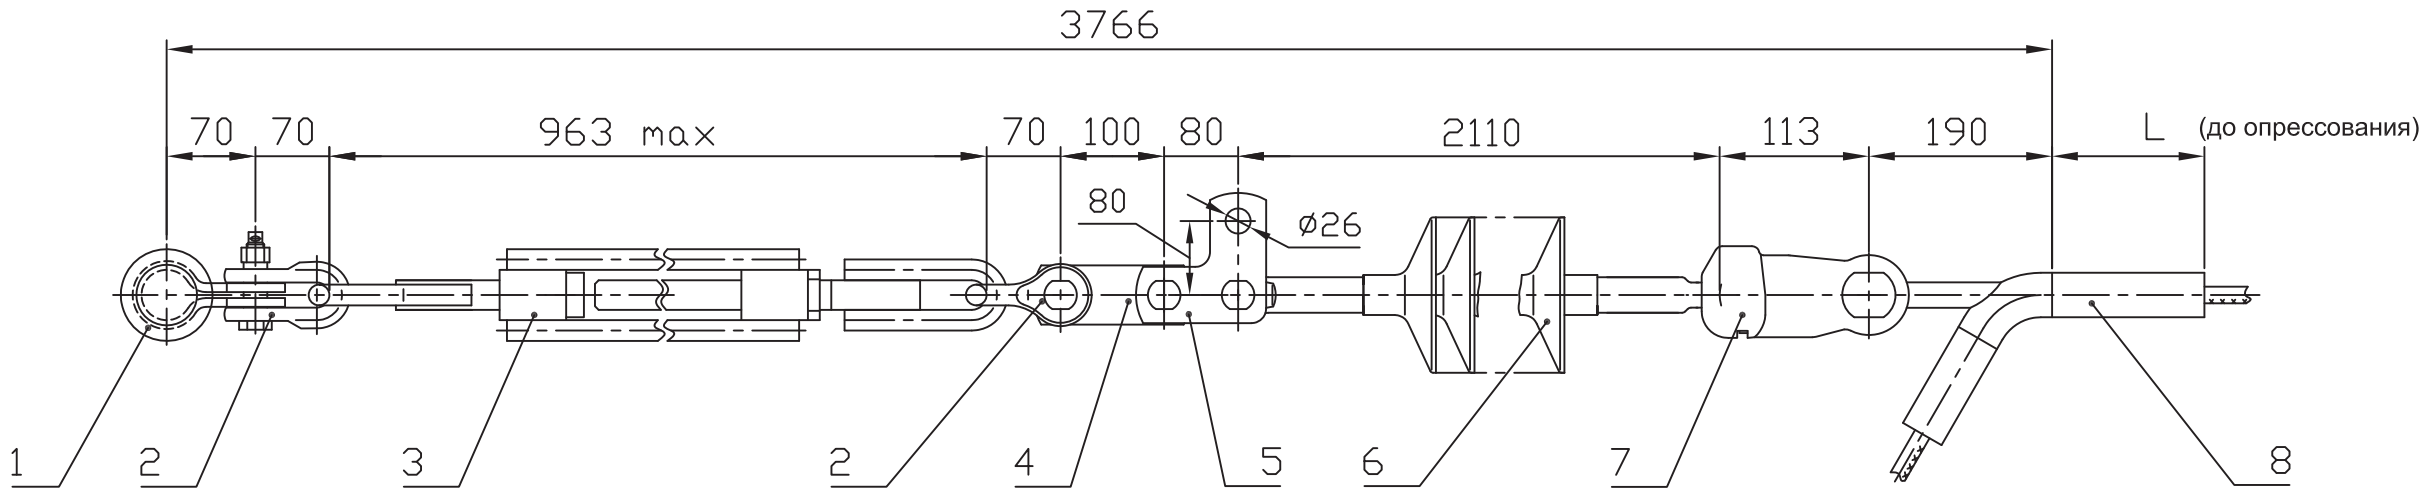

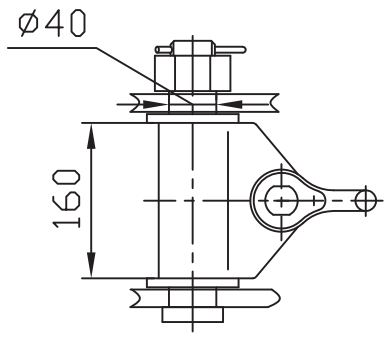

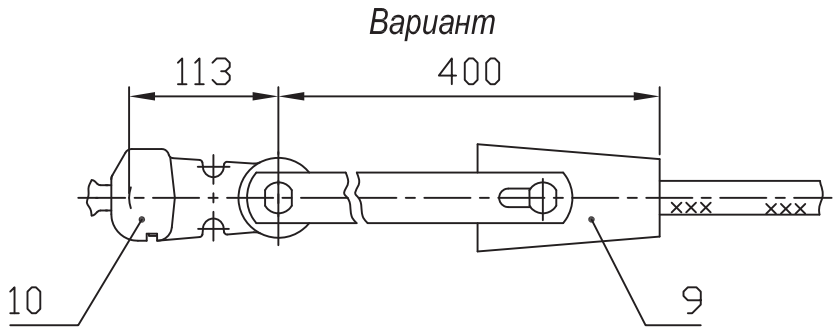

При заказе натяжного клинового зажима типа НК-400-1 следует указывать марку провода.
Ушко У2-16-20 (поз.7) заменить на У1-16-20 (поз.10)

Провод по ГОСТ 839-80		Зажим, поз.8			Масса армат., кг
Марка	Диаметр, мм	Обозначение	L, мм	Масса, кг	
АС300/67	24,5	НАС-300-1Б	165	2,41	23,13
АС400/51	27,5	НАС-450-1Б	210	2,78	23,50

Поз.	Обозначение	Наименование	Кол.	Масса ед. кг	Прим.
1	КГН-16-5	Узел крепления	1	5,23	
2	СК-16-1А	Скоба	2	1,22	
3	ПТР-16-1	Талреп	1	7,18	
4	ПР-16-6	Звено прямое	1	1,36	
5	ПТМ-16-3А	Звено монтажное	1	2,34	
6	ЛК 160/220-	Изолятор исп. СП	1	9,0	
7	У2-16-20	Ушко двухлапчатое	1	2,17	
8	См. табл.	Зажим натяжной	1	См. табл.	
9	НК-400-1	Зажим клиновой	1	5,2	
10	У1-16-20	Ушко однолапчатое	1	1,6	
Масса арматуры, кг				см. табл.	
Масса изолирующей подвески, кг				32,5	


Взам. инв. N


Подп. и дата


Инв. N подл.

		ЭСИП-0046	
		ЭСС.001 ТМ - т.1	
Утв.	Вигдергауз	Натяжные одноцепные изолирующие с полимерными изоляторами ряда 160 кН подвески проводов АС300/67, АС400/51 к а/у металлическим опорам ВЛ 220 кВ	Стадия: Р; Лист: ; Листов: 1
Пров.	Липунцов		Филиал ОАО "ФСК ЕЭС" "Электросетьсервис"
Разраб.	Власкина		

Формат А3

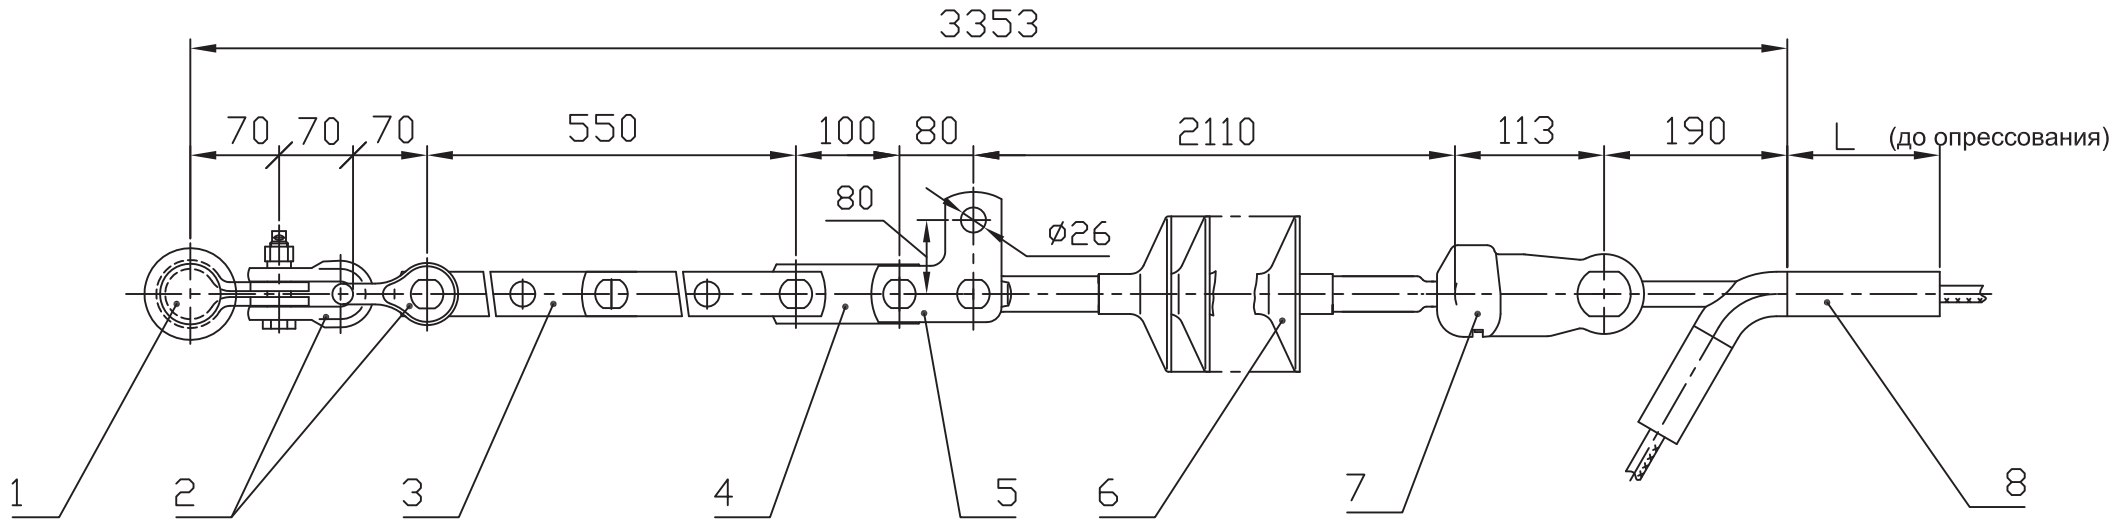

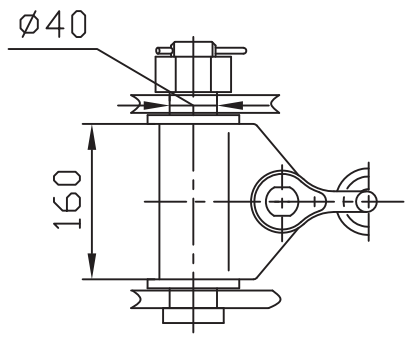

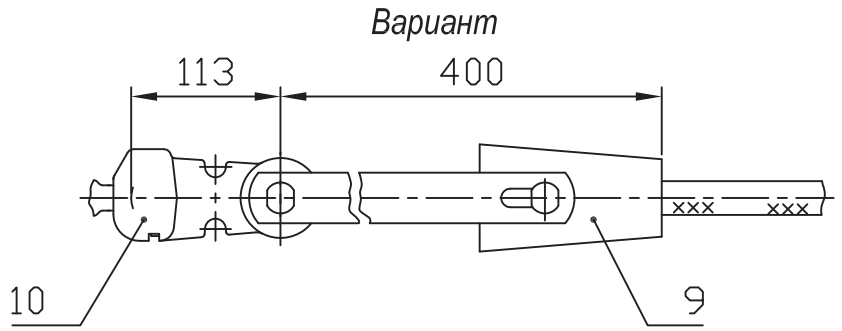

При заказе натяжного клинового зажима типа НК-400-1 следует указывать марку провода.
Ушко У2-16-20 (поз.7) заменить на У1-16-20 (поз.10)

Провод по ГОСТ 839-80		Зажим, поз.8			Масса армат., кг
Марка	Диаметр, мм	Обозначение	L, мм	Масса, кг	
АС300/67	24,5	НАС-300-1Б	165	2,41	20,95
АС400/51	27,5	НАС-450-1Б	210	2,78	21,32

Поз.	Обозначение	Наименование	Кол.	Масса ед. кг	Прим.
1	КГН-16-5	Узел крепления	1	5,23	
2	СК-16-1А	Скоба	2	1,22	
3	ПРР-16-1	Звено регулируемое	1	5,00	
4	ПР-16-6	Звено прямое	1	1,36	
5	ПТМ-16-3А	Звено монтажное	1	2,34	
6	ЛК 160/220-	Изолятор исп. СП	1	9,0	
7	У2-16-20	Ушко двухлапчатое	1	2,17	
8	См. табл.	Зажим натяжной	1	См. табл.	
9	НК-400-1	Зажим клиновой	1	5,2	
10	У1-16-20	Ушко однолапчатое	1	1,6	
Масса арматуры, кг				см. табл.	
Масса изолирующей подвески, кг				30,3	


			ЭСИП-0047
			ЭСС.001 ТМ - т.1
Утв.	Вигдергауз		Натяжные одноцепные изолирующие с полимерными изоляторми ряда 160 кН подвески проводов АС300/67, АС400/51 к а/у металлическим опорам ВЛ 220 кВ
Пров.	Липунцов		
Разраб.	Власкина		


Стадия	Лист	Листов
Р		1


Филиал ОАО "ФСК ЕЭС" "Электросетьсервис"

Взам. инв. N | Подп. и дата | Инв. N подл.

Формат А3

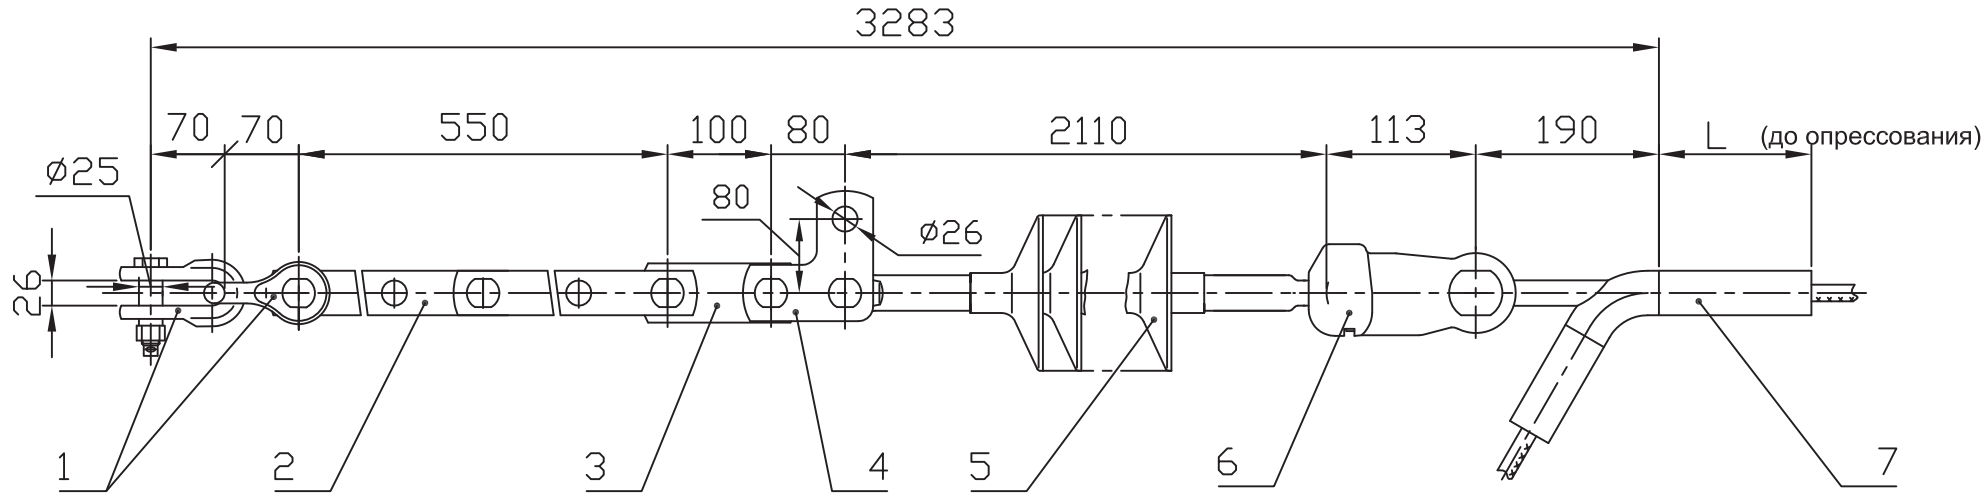

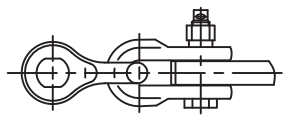

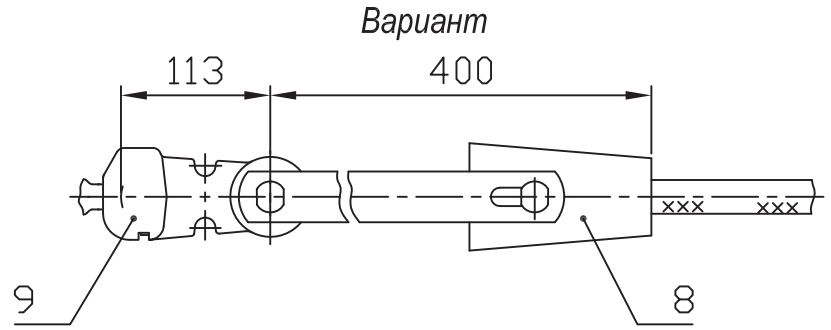

При заказе натяжного клинового зажима типа НК-400-1 следует указывать марку провода.
Ушко У2-16-20 (поз.6) заменить на У1-16-20 (поз.9)

Провод по ГОСТ 839-80		Зажим, поз.7			Масса армат., кг
Марка	Диаметр, мм	Обозначение	L, мм	Масса, кг	
АС300/67	24,5	НАС-300-1Б	165	2,41	15,72
АС400/51	27,5	НАС-450-1Б	210	2,78	16,06

Поз.	Обозначение	Наименование	Кол.	Масса ед. кг	Прим.
1	СК-16-1А	Скоба	2	1,22	
2	ПРР-16-1	Звено регулируемое	1	5,00	
3	ПР-16-6	Звено прямое	1	1,36	
4	ПТМ-16-3А	Звено монтажное	1	2,34	
5	ЛК 160/220-	Изолятор исп. СП	1	9,0	
6	У2-16-20	Ушко двухлапчатое	1	2,17	
7	См. табл.	Зажим натяжной	1	См. табл.	
8	НК-400-1	Зажим клиновой	1	5,2	
9	У1-16-20	Ушко однолапчатое	1	1,6	
Масса арматуры, кг				см. таблицу	
Масса изолирующей подвески, кг				25,1	


Взам. инв. N

Подп. и дата


Инв. N подл.

			ЭСИП-0048
			ЭСС.001 ТМ - т.1
Утв.	Вигдергауз		Натяжные одноцепные изолирующие с полимерными изоляторами ряда 160 кН подвески проводов АС300/67, АС400/51 к а/у ж/б опорам ВЛ 220 кВ
Пров.	Липунцов		Стадия: Р; Лист: ; Листов: 1
Разраб.	Власкина		Филиал ОАО "ФСК ЕЭС" "Электросетьсервис"

Формат А3

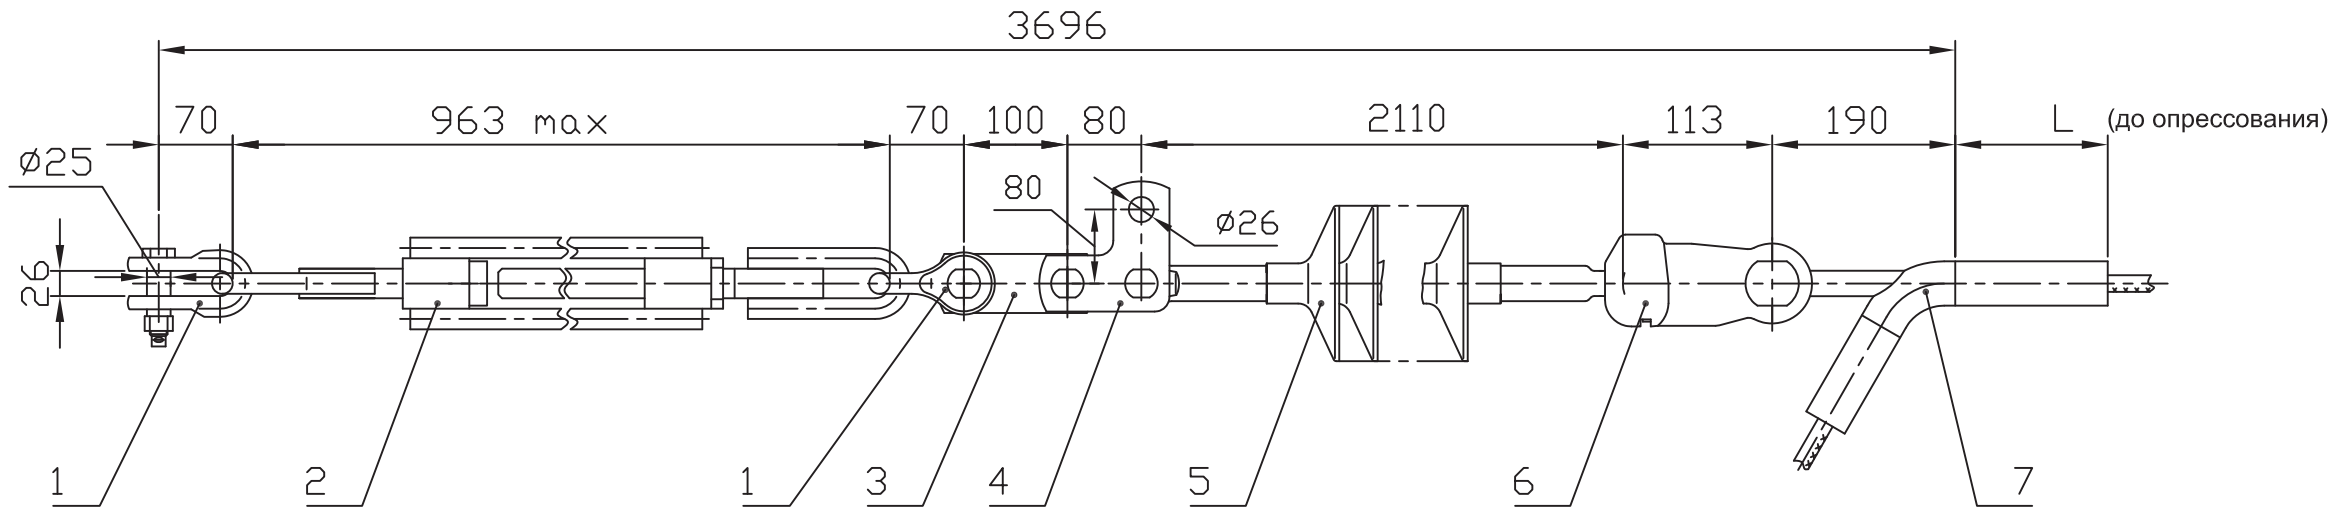

Вариант

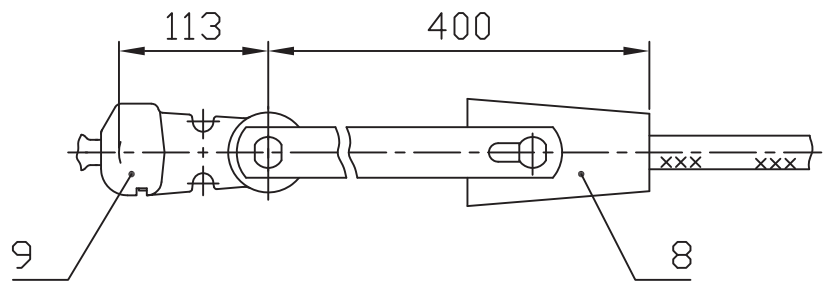

При заказе натяжного клинового зажима типа НК-400-1 следует указывать марку провода.
Ушко У2-16-20 (поз.6) заменить на У1-16-20 (поз.9)

Поз.	Обозначение	Наименование	Кол.	Масса ед. кг	Прим.
1	СК-16-1А	Скоба	2	1,22	
2	ПТР-16-1	Звено регулируемое	1	7,18	
3	ПР-16-6	Звено прямое	1	1,36	
4	ПТМ-16-3А	Звено монтажное	1	2,34	
5	ЛК 160/220-	Изолятор исп. СП	1	9,0	
6	У2-16-20	Ушко двухлапчатое	1	2,17	
7	См. табл.	Зажим натяжной	1	См. табл.	
8	НК-400-1	Зажим клиновой	1	5,2	
9	У1-16-20	Ушко однолапчатое	1	1,6	
Масса арматуры, кг				см. табл.	
Масса изолирующей подвески, кг				27,3	

Провод по ГОСТ 839-80		Зажим, поз.7			Масса армат., кг
Марка	Диаметр, мм	Обозначение	L, мм	Масса, кг	
АС300/67	24,5	НАС-300-1Б	165	2,41	17,90
АС400/51	27,5	НАС-450-1Б	210	2,78	18,27


Взам. инв. N


Подп. и дата


Инв. N подл.

		ЭСИП-0049	
		ЭСС.001 ТМ - т.1	
Утв.	Вигдергауз	Натяжные одноцепные изолирующие с полимерными изоляторами ряда 160 кН подвески проводов АС300/67, АС450/51 к а/у ж/б опорам ВЛ 220 кВ	Стадия: Р; Лист: ; Листов: 1
Пров.	Липунцов		Филиал ОАО "ФСК ЕЭС" "Электросетьсервис"
Разраб.	Власкина		

Формат А3

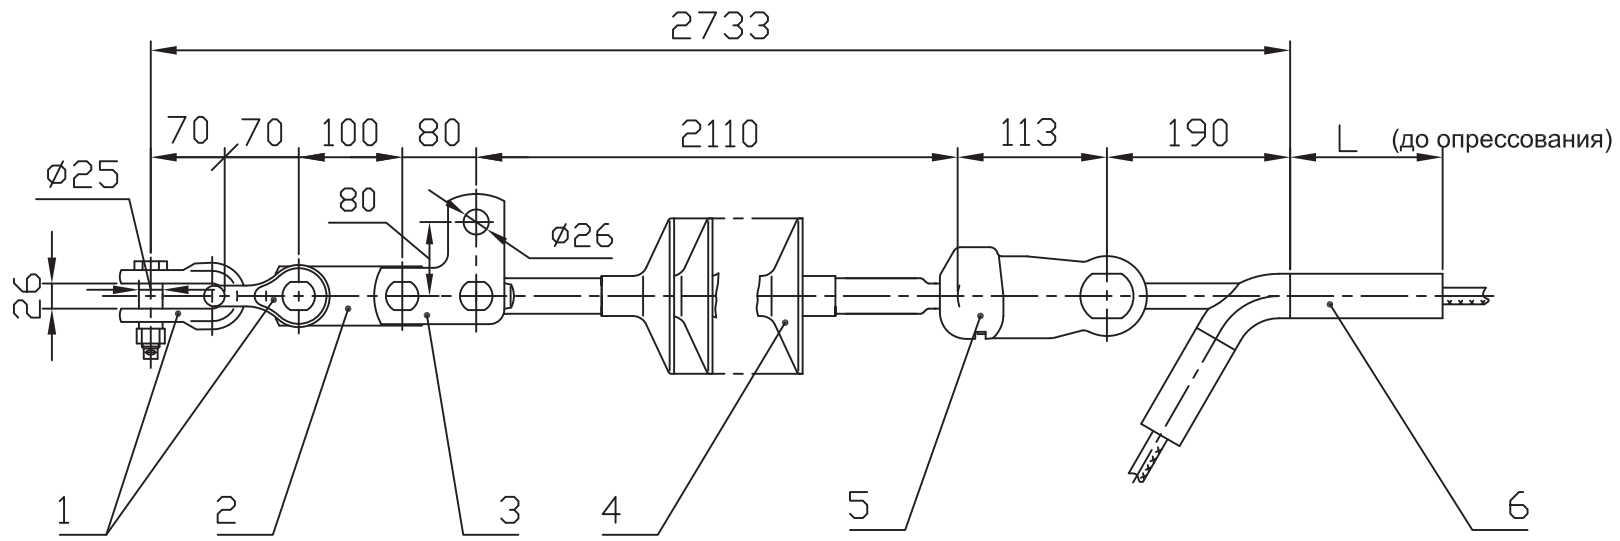

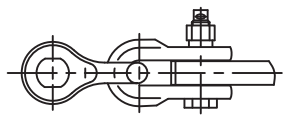

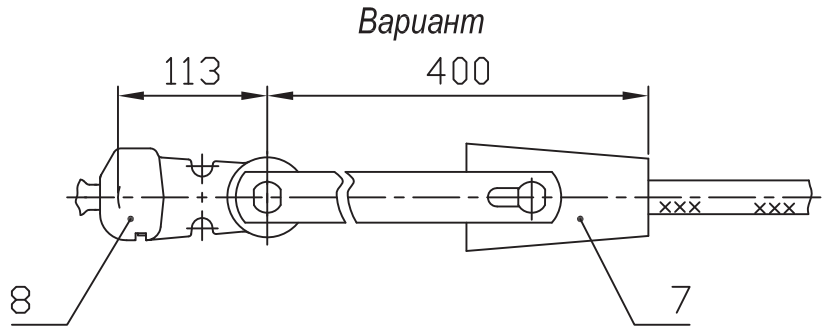


При заказе натяжного клинового зажима типа НК-400-1 следует указывать марку провода.
Ушко У2-16-20 (поз.5) заменить на У1-16-20 (поз.8)


Поз.	Обозначение	Наименование	Кол.	Масса ед. кг	Прим.
1	СК-16-1А	Скоба	2	1,22	
2	ПР-16-6	Звено прямое	1	1,36	
3	ПТМ-16-3А	Звено монтажное	1	2,34	
4	ЛК 160/220-	Изолятор исп. СП	1	9,0	
5	У2-16-20	Ушко двухлапчатое	1	2,17	
6	См. табл.	Зажим натяжной	1	См. табл.	
7	НК-400-1	Зажим клиновой	1	5,2	
8	У1-16-20	Ушко однолапчатое	1	1,6	
Масса арматуры, кг				см. табл.	
Масса изолирующей подвески, кг				20,1	

Провод по ГОСТ 839-80		Зажим, поз.6			Масса армат., кг
Марка	Диаметр, мм	Обозначение	L, мм	Масса, кг	
АС300/67	24,5	НАС-300-1Б	165	2,41	10,72
АС400/51	27,5	НАС-450-1Б	210	2,78	11,09


		ЭСИП-0050	
		ЭСС.001 ТМ - т.1	
Утв.	Вигдергауз	Натяжные одноцепные изолирующие с полимерными изоляторами ряда 160 кН подвески проводов АС300/67, АС400/51 к а/у ж/б опорам ВЛ 220 кВ	Стадия: Р; Лист: ; Листов: 1
Пров.	Липунцов		Филиал ОАО "ФСК ЕЭС" "Электросетьсервис"
Разраб.	Власкина		

Взам. инв. N | Подп. и дата | Инв. N подл.

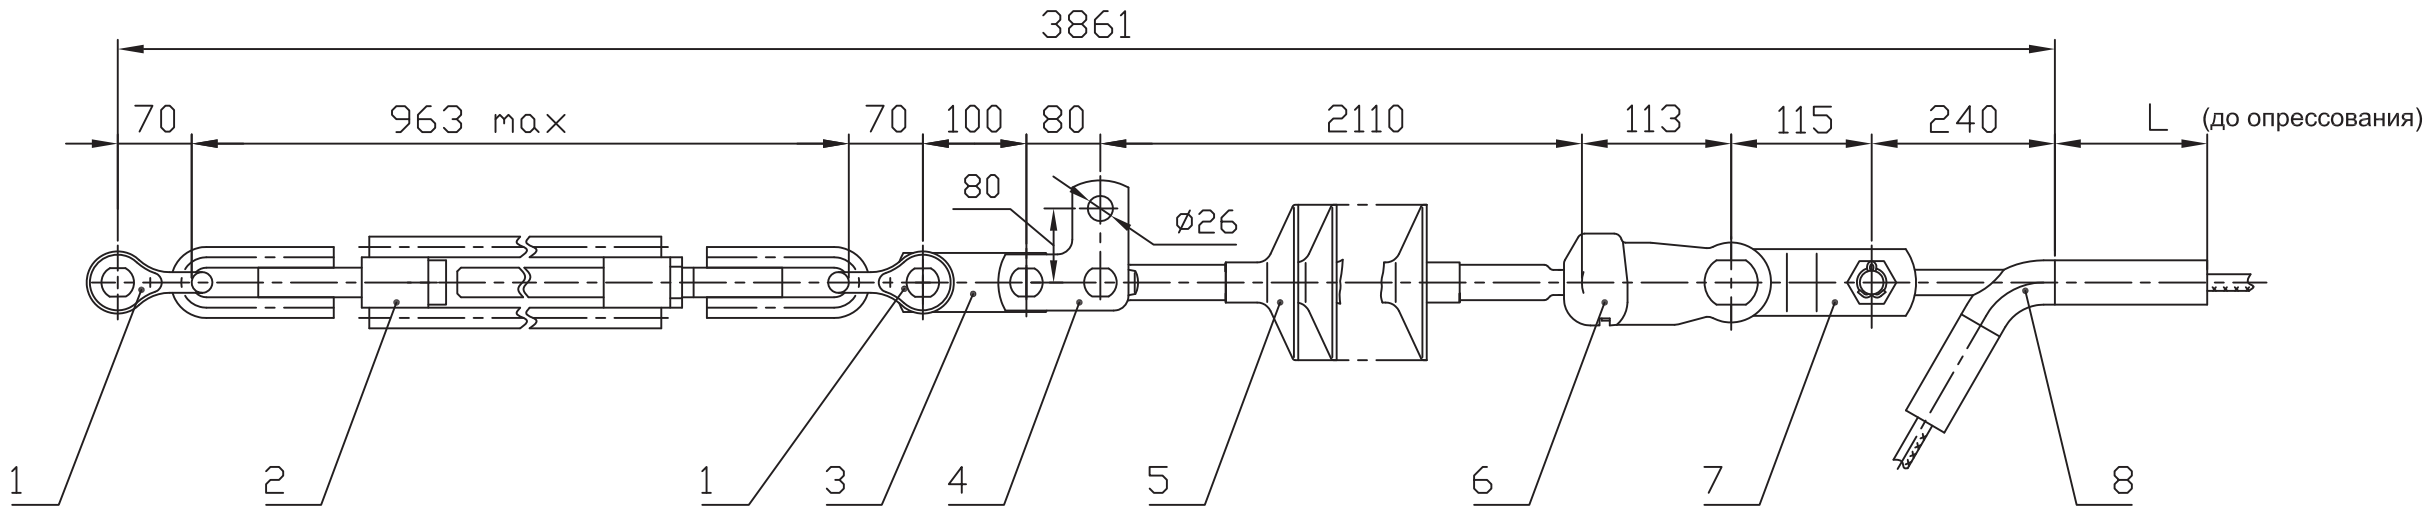

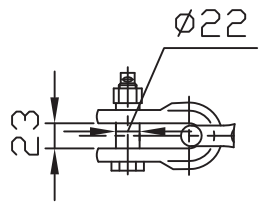

Вариант

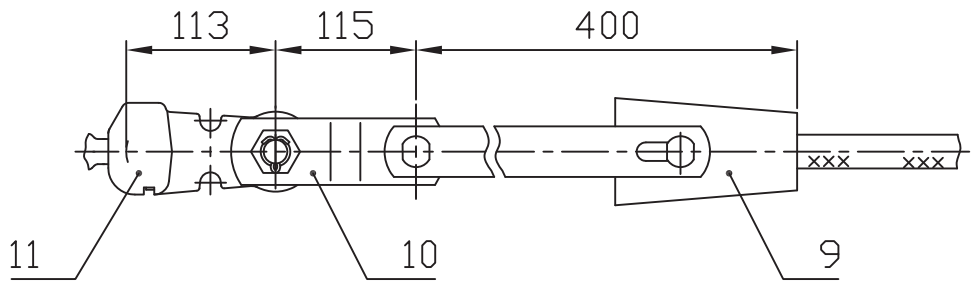

При заказе натяжного клинового зажима типа НК-500-1 следует указывать марку провода.
Ушко У2-16-20 (поз.6) заменить на У1-16-20 (поз.11), а звено ПРТ-16/21-2 (поз.7) на ПРТ-21/16-2 (поз.10).

Провод по ГОСТ 839-80		Зажим, поз.8			Масса армат., кг
Марка	Диаметр, мм	Обозначение	L, мм	Масса, кг	
АС400/93	29,1	НАС-600-2Б	225	3,99	21,38
АС500/64	30,6	НАС-600-1Б	240	4,65	22,04

Поз.	Обозначение	Наименование	Кол.	Масса ед. кг	Прим.
1	СК-16-1А	Скоба	2	1,22	
2	ПТР-16-1	Талреп	1	7,18	
3	ПР-16-6	Звено прямое	1	1,36	
4	ПТМ-16-3А	Звено монтажное	1	2,34	
5	ЛК 160/220-	Изолятор исп. СП	1	9,0	
6	У2-16-20	Ушко двухлапчатое	1	2,17	
7	ПРТ-16/21-2	Звено переходное	1	1,9	
8	См. табл.	Зажим натяжной	1	См. табл.	
9	НК-500-1	Зажим клиновой	1	5,2	
10	ПРТ-21/16-2	Звено переходное	1	1,8	
11	У1-16-20	Ушко однолапчатое	1	1,6	
Масса арматуры, кг				см. табл.	
Масса изолирующей подвески, кг				31,0	

Утв.	Вигдергауз		
Пров.	Липунцов		
Разраб.	Власкина		

ЭСИП-0051

ЭСС.001 ТМ - т.1

Натяжные одноцепные изолирующие с полимерными изоляторами ряда 160 кН подвески проводов АС400/93,АС500/64 к а/у деревянным опорам ВЛ 220 кВ

Стадия	Лист	Листов
Р		1


Филиал ОАО "ФСК ЕЭС" "Электросетьсервис"


Взам. инв. N

Подп. и дата


Инв. N подл.

Формат А3

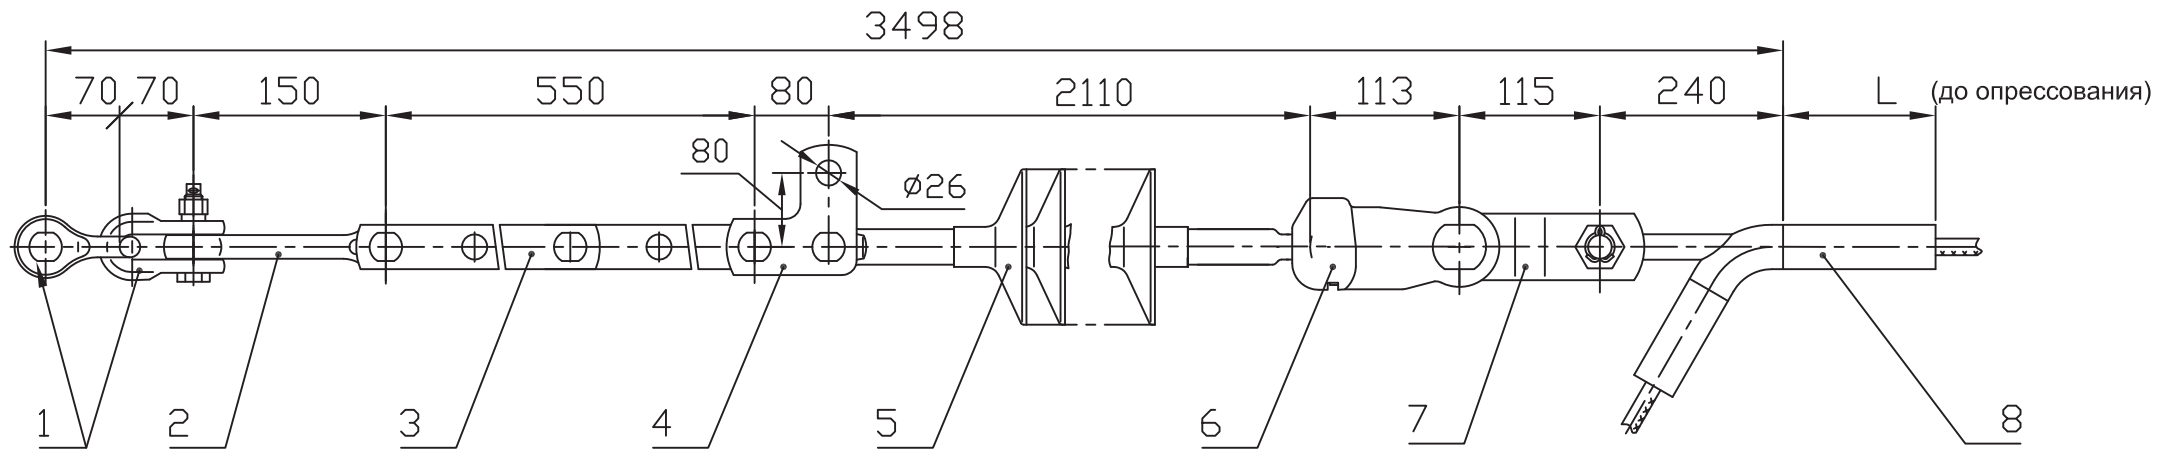

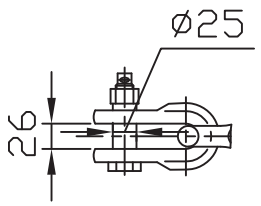

Вариант

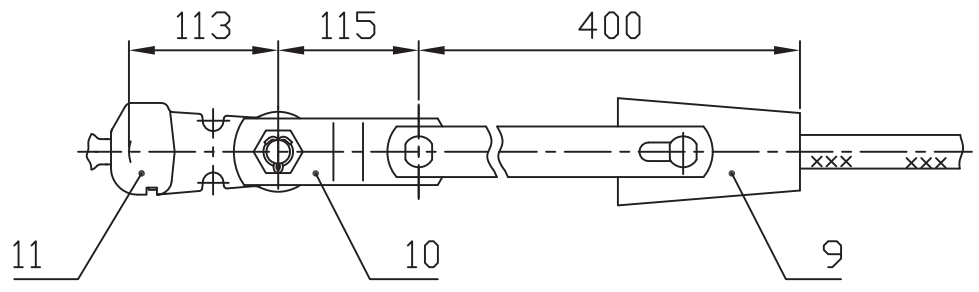

При заказе натяжного клинового зажима типа НК-500-1 следует указывать марку провода.
Ушко У2-16-20 (поз.6) заменить на У1-16-20 (поз.11), а звено ПРТ-16/ 21-2 (поз.7) на ПРТ-21/16-2 (поз.10).

Провод по ГОСТ 839-80		Зажим, поз.8			Масса армат., кг
Марка	Диаметр, мм	Обозначение	L, мм	Масса, кг	
АС400/93	29,1	НАС-600-2Б	225	3,99	18,75
АС500/64	30,6	НАС-600-1Б	240	4,65	19,40

Поз.	Обозначение	Наименование	Кол.	Масса ед. кг	Прим.
1	СК-16-1А	Скоба	2	1,22	
2	ПРВ-16-1	Звено вывернутое	1	0,91	
3	ПРР-16-1	Звено регулируемое	1	5,0	
4	ПТМ-16-3А	Звено монтажное	1	2,34	
5	ЛК 160/220-	Изолятор исп. СП	1	9,0	
6	У2-16-20	Ушко двухлапчатое	1	2,17	
7	ПРТ-16/21-2	Звено переходное	1	1,9	
8	См. табл.	Зажим натяжной	1	См. табл.	
9	НК-500-1	Зажим клиновой	1	5,2	
10	ПРТ-21/16-2	Звено переходное	1	1,8	
11	У1-16-20	Ушко однолапчатое	1	1,6	
Масса арматуры, кг				см. табл.	
Масса изолирующей подвески, кг				28,4	

ЭСИП-0052

ЭСС.001 ТМ - т.1

Утв.	Вигдергауз	
Пров.	Липунцов	
Разраб.	Власкина	

Натяжные одноцепные изолирующие с полимерными изоляторами ряда 160 кН подвески проводов АС400/93, АС50/64 к а/у деревянным опорам ВЛ 220 кВ

Стадия	Лист	Листов
Р		1


Филиал ОАО "ФСК ЕЭС" "Электросетьсервис"


Взам. инв. N

Подп. и дата


Инв. N подл.

Формат А3

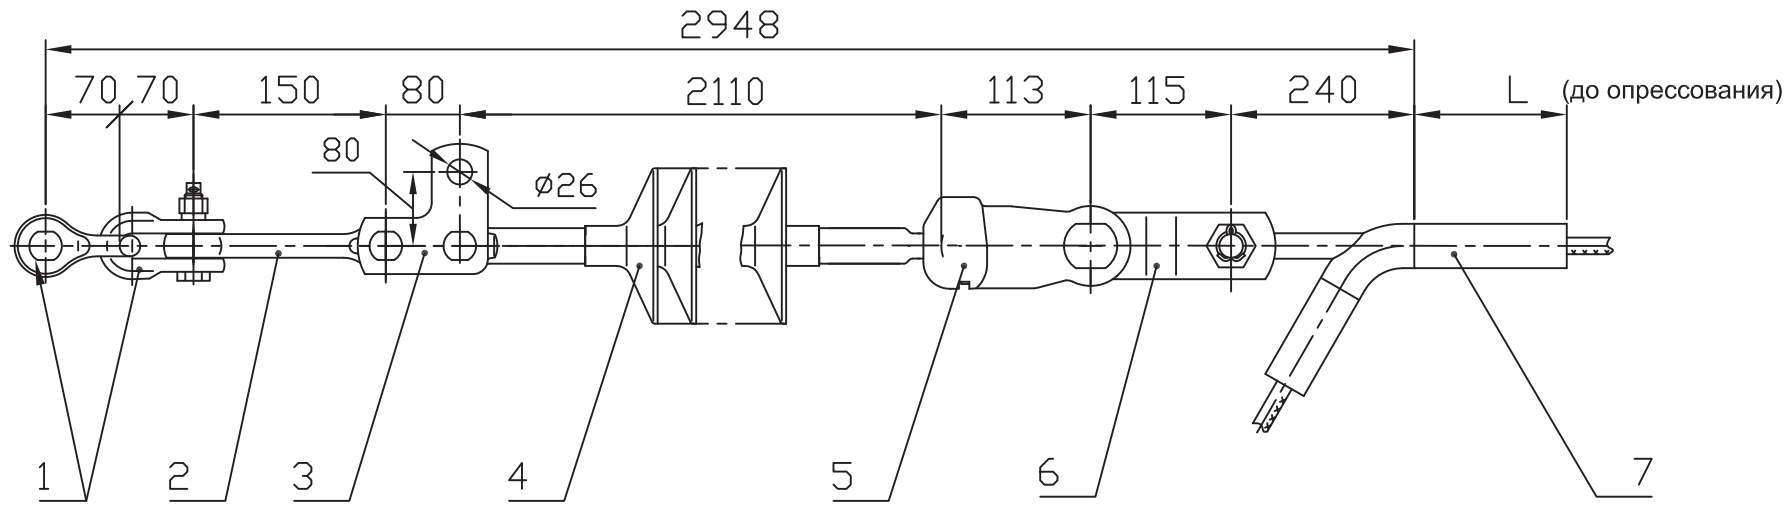

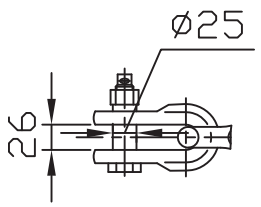

Вариант

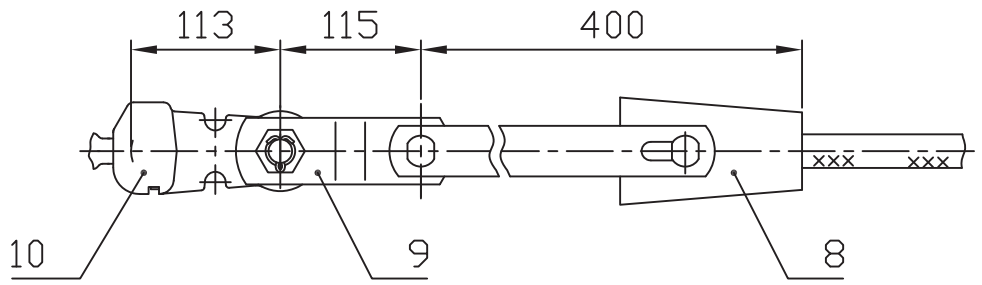

При заказе натяжного клинового зажима типа НК-500-1 следует указывать марку провода.
Ушко У2-16-20 (поз.5) заменить на У1-16-20 (поз.10), а звено ПРТ-16/ 21-2 (поз.6) на ПРТ-21/16-2 (поз.9).

Провод по ГОСТ 839-80		Зажим, поз.7			Масса армат., кг
Марка	Диаметр, мм	Обозначение	L, мм	Масса, кг	
АС400/93	29,1	НАС-600-2Б	225	3,99	13,75
АС500/64	30,6	НАС-600-1Б	240	4,65	14,41

Поз.	Обозначение	Наименование	Кол.	Масса ед. кг	Прим.
1	СК-16-1А	Скоба	2	1,22	
2	ПРВ-16-1	Звено вывернутое	1	0,91	
3	ПТМ-16-3А	Звено монтажное	1	2,34	
4	ЛК 160/220-	Изолятор исп. СП	1	9,0	
5	У2-16-20	Ушко двухлапчатое	1	2,17	
6	ПРТ-16/21-2	Звено переходное	1	1,9	
7	См. табл.	Зажим натяжной	1	См. табл.	
8	НК-500-1	Зажим клиновой	1	5,4	
9	ПРТ-21/16-2	Звено переходное	1	1,8	
10	У1-16-20	Ушко однолапчатое	1	1,6	
Масса арматуры, кг				см. табл.	
Масса изолирующей подвески, кг				23,4	

Утв.	Вигдергауз		
Пров.	Липунцов		
Разраб.	Власкина		

ЭСИП-0053

ЭСС.001 ТМ - т.1


Натяжные одноцепные изолирующие с полимерными изоляторами ряда 160 кН подвески проводов АС400/93, АС500/64 к а/у деревянным опорам ВЛ 220 кВ


Стадия	Лист	Листов
Р		1

Филиал ОАО "ФСК ЕЭС" "Электросетьсервис"


Взам. инв. N | Подп. и дата | Инв. N подл.

Формат А3

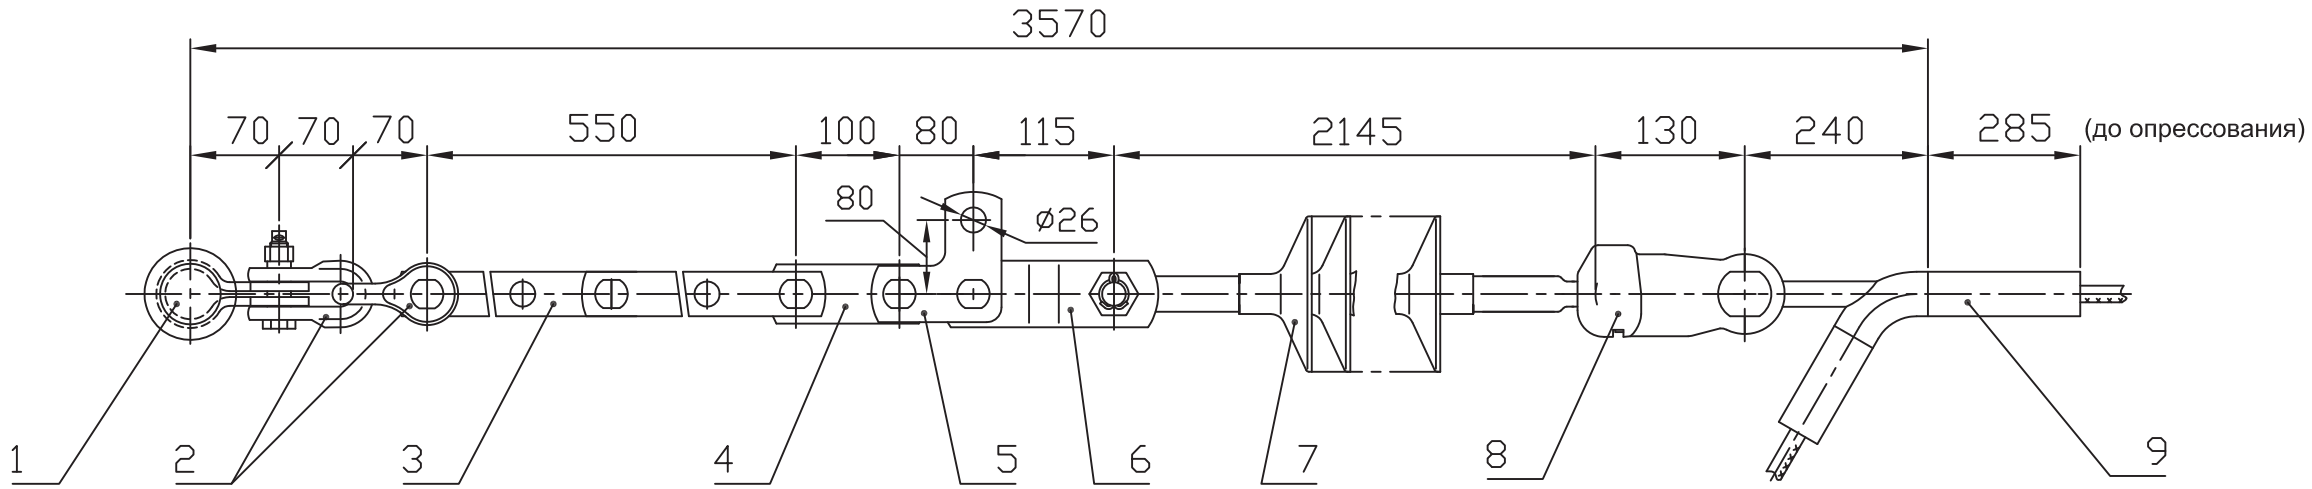

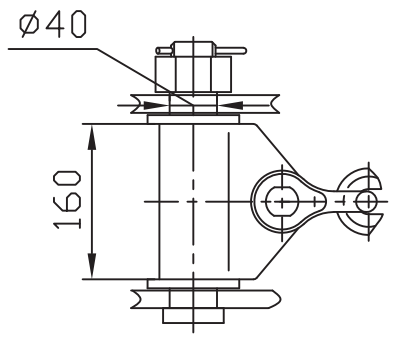

Вариант

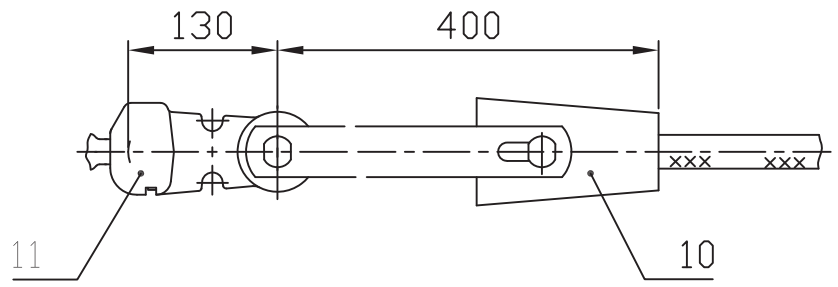

При заказе натяжного клинового зажима типа НК-500-1 следует указывать марку провода.
Ушко У2-21-20 (поз.8) заменить на У1-21-20 (поз.11)

Провод по ГОСТ 839-80		Зажим, поз.9			Масса армат., кг
Марка	Диаметр, мм	Обозначение	L, мм	Масса, кг	
АС400/93	29,1	НАС-600-2Б	225	3,99	25,84
АС500/64	30,6	НАС-600-1Б	240	4,65	26,50

Поз.	Обозначение	Наименование	Кол.	Масса ед. кг	Прим.
1	КГН-16-5	Узел крепления	1	5,23	
2	СК-16-1А	Скоба	2	1,22	
3	ПРР-16-1	Звено регулируемое	1	5,00	
4	ПР-16-6	Звено прямое	1	1,36	
5	ПТМ-16-3А	Звено монтажное	1	2,34	
6	ПРТ-16/21-2	Звено переходное	1	1,9	
7	ЛК 210/220-	Изолятор исп. СП	1	11,0	
8	У2-21-20	Ушко двухлапчатое	1	3,58	
9	См. табл.	Зажим натяжной	1	См. табл.	
10	НК-500-1	Зажим клиновой	1	5,4	
11	У1-21-20	Ушко однолапчатое	1	2,23	
Масса арматуры, кг				см. табл.	
Масса изолирующей подвески, кг				37,5	


			ЭСИП-0054
			ЭСС.001 ТМ - т.1
Утв.	Вигдергауз		Натяжные одноцепные изолирующие с полимерными изоляторами ряда 210 кН подвески проводов АС400/93, АС500/64 к а/у стальным опорам ВЛ 220 кВ
Пров.	Липунцов		
Разраб.	Власкина		


Стадия	Лист	Листов
Р		1

Филиал ОАО "ФСК ЕЭС" "Электросетьсервис"


Взам. инв. N | Подп. и дата | Инв. N подл.

Формат А3

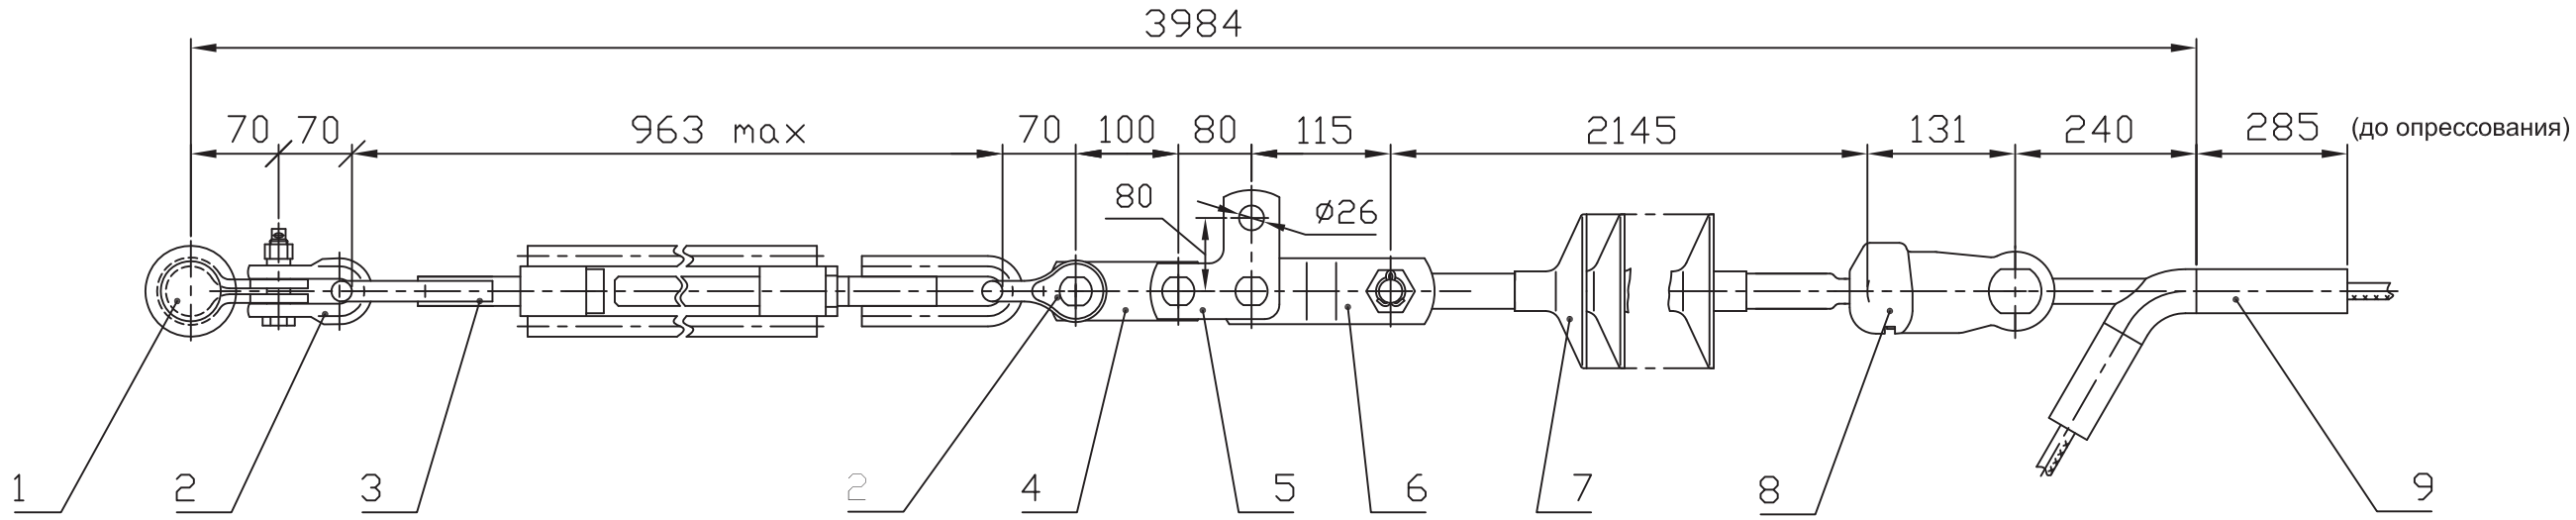

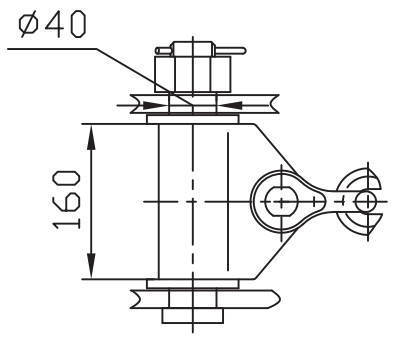

Вариант

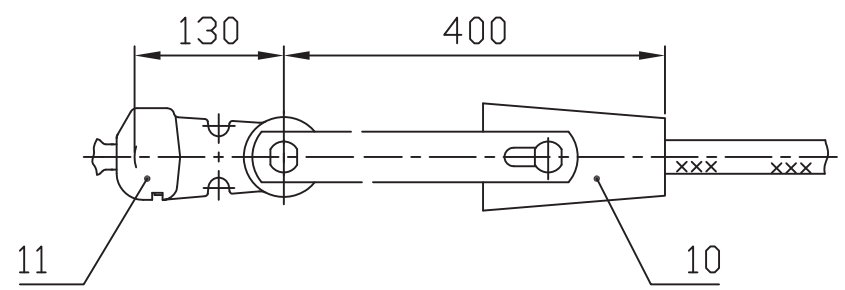

При заказе натяжного клинового зажима типа НК-500-1 следует указывать марку провода.
Ушко У2-21-20 (поз.8) заменить на У1-21-20 (поз.11)


Провод по ГОСТ 839-80		Зажим, поз.9			Масса армат., кг
Марка	Диаметр, мм	Обозначение	L, мм	Масса, кг	
АС400/93	29,1	НАС-600-2Б	225	3,99	28,03
АС500/64	30,6	НАС-600-1Б	240	4,65	28,68


Поз.	Обозначение	Наименование	Кол.	Масса ед. кг	Прим.
1	КГН-16-5	Узел крепления	1	5,23	
2	СК-16-1А	Скоба	2	1,22	
3	ПТР-16-1	Звено регулируемое	1	7,18	
4	ПР-16-6	Звено прямое	1	1,36	
5	ПТМ-16-3А	Звено монтажное	1	2,34	
6	ПРТ-16/21-2	Звено переходное	1	1,9	
7	ЛК 210/220-	Изолятор исп. СП	1	11,0	
8	У2-21-20	Ушко двухлапчатое	1	3,58	
9	См. табл.	Зажим натяжной	1	См. табл.	
10	НК-500-1	Зажим клиновой	1	5,4	
11	У1-21-20	Ушко однолапчатое	1	2,23	
Масса арматуры, кг				см. табл.	
Масса изолирующей подвески, кг				39,7	

Утв.	Вигдергауз	ЭСИП-0055	
		ЭСС.001 ТМ - т.1	
Пров.	Липунцов	Натяжные одноцепные изолирующие с полимерными изоляторами ряда 210 кН подвески проводов АС400/93, АС500/64 к а/у стальным опорам ВЛ 220 кВ	Стадия: Р; Лист: ; Листов: 1
Разраб.	Власкина		Филиал ОАО "ФСК ЕЭС" "Электросетьсервис"


Взам. инв. N | Подп. и дата | Инв. N подл.

Формат А3

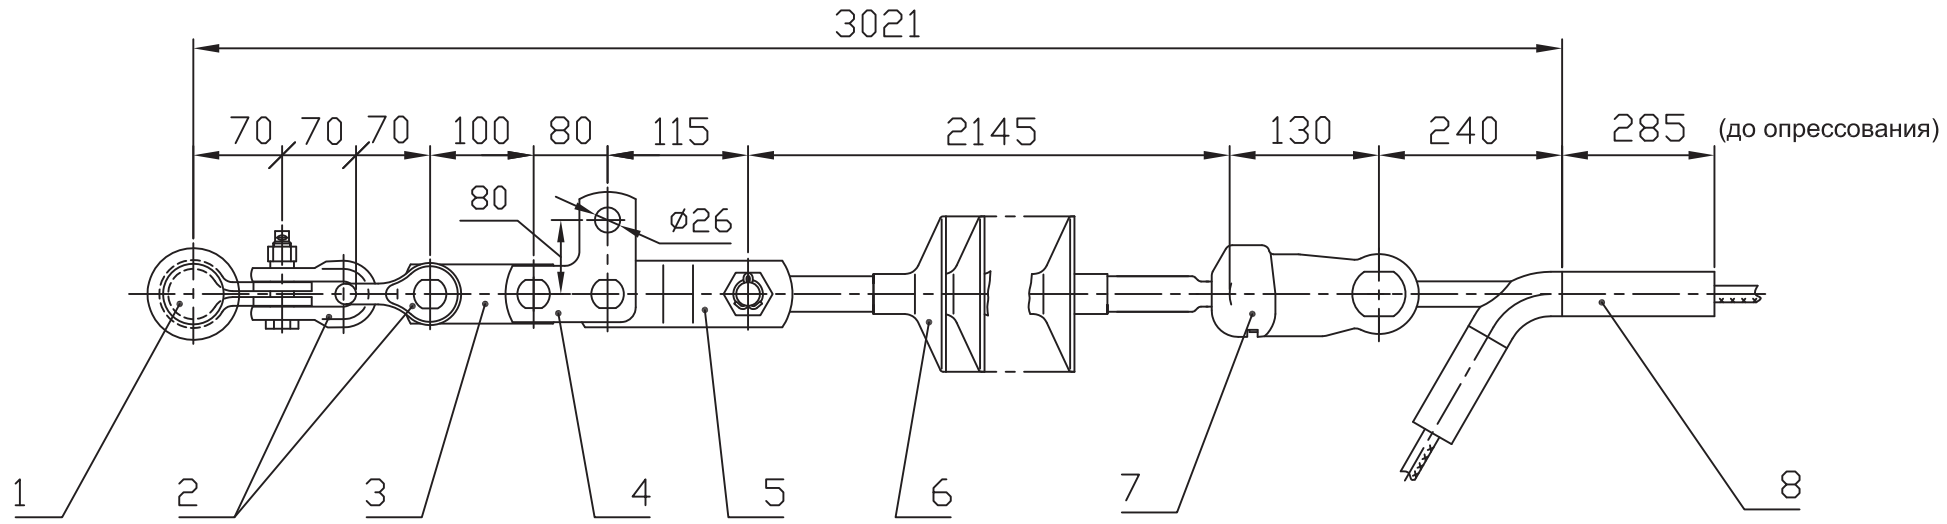

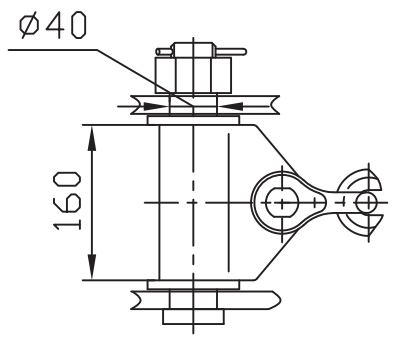

Вариант

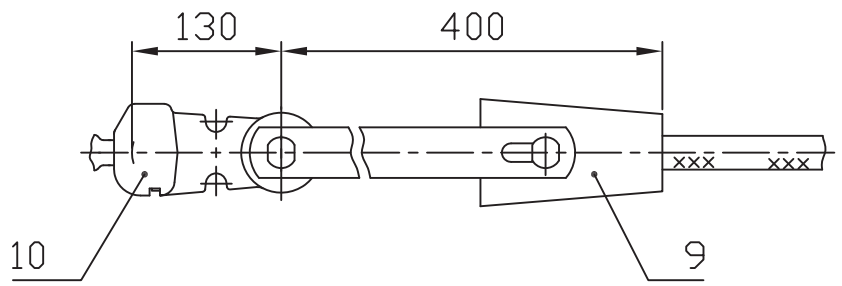


При заказе натяжного клинового зажима типа НК-500-1 следует указывать марку провода.
Ушко У2-21-20 (поз.7) заменить на У1-21-20 (поз.10)


Провод по ГОСТ 839-80		Зажим, поз.8			Масса армат., кг
Марка	Диаметр, мм	Обозначение	L, мм	Масса, кг	
АС400/93	29,1	НАС-600-2Б	225	3,99	20,84
АС500/64	30,6	НАС-600-1Б	240	4,65	21,50

Поз.	Обозначение	Наименование	Кол.	Масса ед. кг	Прим.
1	КГН-16-5	Узел крепления	1	5,23	
2	СК-16-1А	Скоба	2	1,22	
3	ПР-16-6	Звено прямое	1	1,36	
4	ПТМ-16-3А	Звено монтажное	1	2,34	
5	ПРТ-16/21-2	Звено переходное	1	1,9	
6	ЛК 210/220-	Изолятор исп. СП	1	11,0	
7	У2-21-20	Ушко двухлапчатое	1	3,58	
8	См. табл.	Зажим натяжной	1	См. табл.	
10	НК-500-1	Зажим клиновой	1	5,4	
11	У1-21-20	Ушко однолапчатое	1	2,23	
Масса арматуры, кг				см. табл.	
Масса изолирующей подвески, кг				32,5	

Утв.	Вигдергауз	ЭСИП-0056	
		ЭСС.001 ТМ - т.1	
Пров.	Липунцов	Натяжные одноцепные изолирующие с полимерными изоляторами ряда 210 кН подвески проводов АС400/93, АС500/64 к а/у стальным опорам ВЛ 220 кВ	Стадия: Р; Лист: ; Листов: 1
Разраб.	Власкина		Филиал ОАО "ФСК ЕЭС" "Электросетьсервис"

Взам. инв. N | Подп. и дата | Инв. N подл.

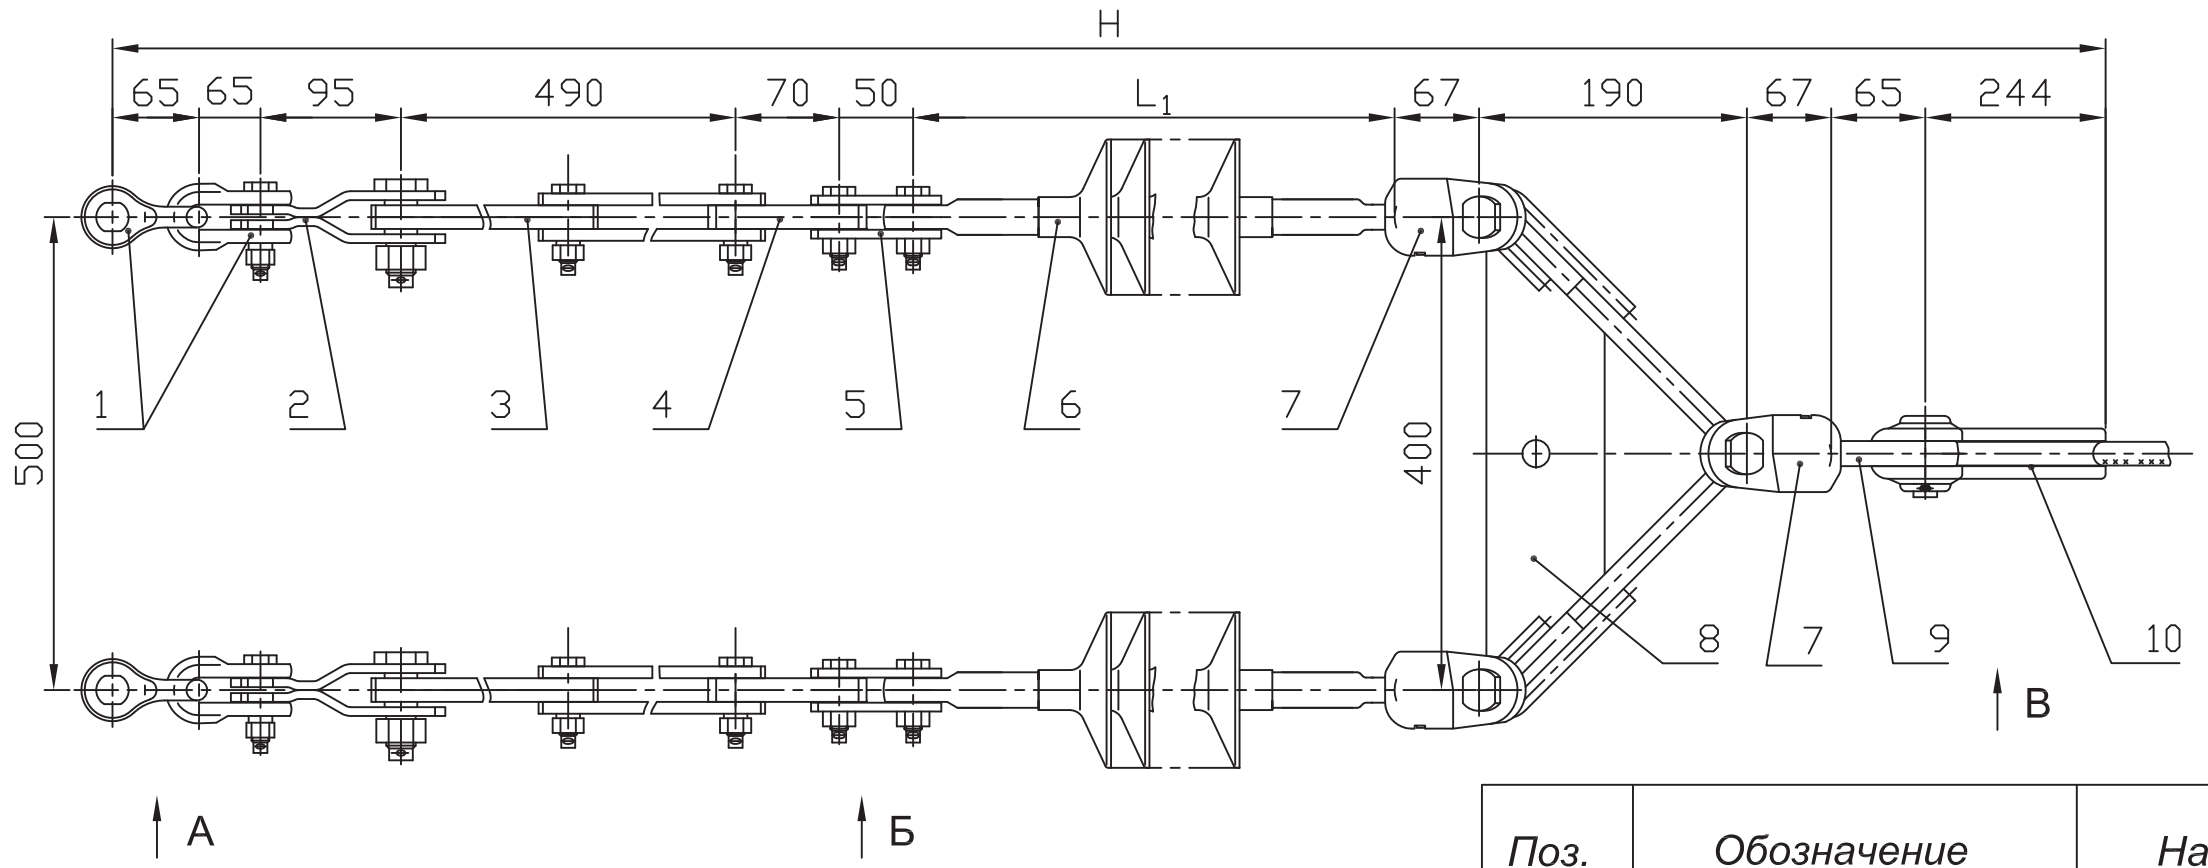

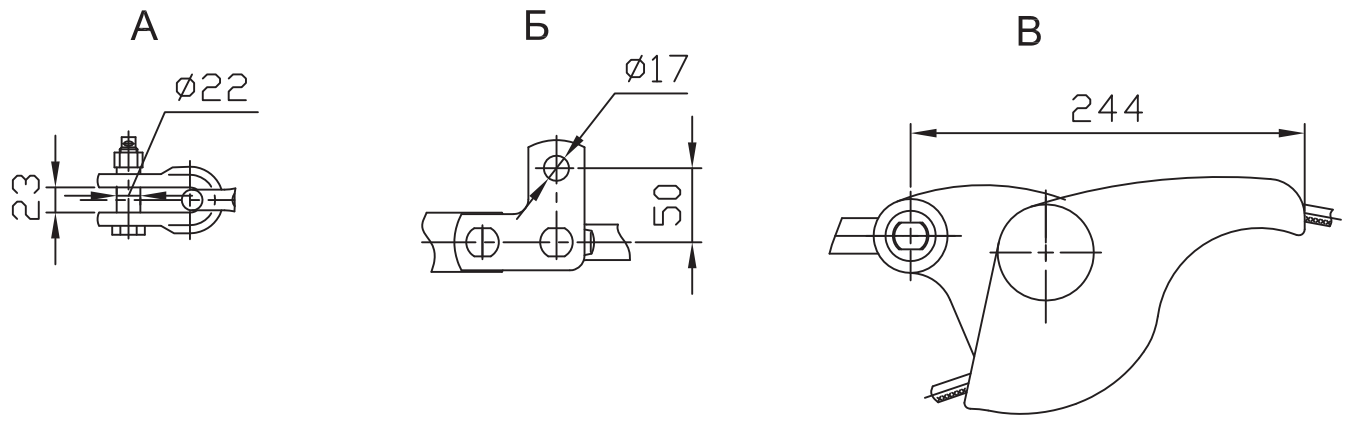

Напряжение ВЛ, кВ	Изолятор, поз.6		Изолирующая подвеска	
	L1, мм	Масса, кг	H, мм	Масса, кг
35	475	1,5	1943	24,2
110	1175	3,0	2643	27,2

Поз.	Обозначение	Наименование	Кол.	Масса ед. кг	Прим.
1	СК-120-1Б	Скоба	4	0,92	
2	ПРТ-12/7-2	Звено переходное	2	0,7	
3	ПРР-7-1	Звено регулируемое	2	1,91	
4	ПР-7-6	Звено прямое	2	0,44	
5	ПТМ-7-3А	Звено монтажное	2	0,63	
6		Изолятор исп. СП	2	См. табл.	
7	УСК-7-16	Ушко специальное	3	1,2	
8	2КУ-12-1	Коромысло	1	4,75	
9	СР-7-16	Серьга	1	0,3	
10	НЗ-60/11-17	Зажим натяжной	1	1,5	
Масса арматуры, кг				21,2	
Масса изолирующей подвески, кг				см. табл.	


				ЭСИП-0057
				ЭСС.001 ТМ - т.1
Утв.	Вигдергауз			Натяжные двухцепные изолирующие с полимерными изоляторами ряда 70 кН подвески проводов АС70/11 - АС150/24 к а/у металлическим и ж/б опорам ВЛ 35, 110 кВ
Пров.	Липунцов			
Разраб.	Власкина			


Стадия	Лист	Листов
Р		1


Филиал ОАО "ФСК ЕЭС" "Электросетьсервис"


Взам. инв. N | Подп. и дата | Инв. N подл.

Формат А3

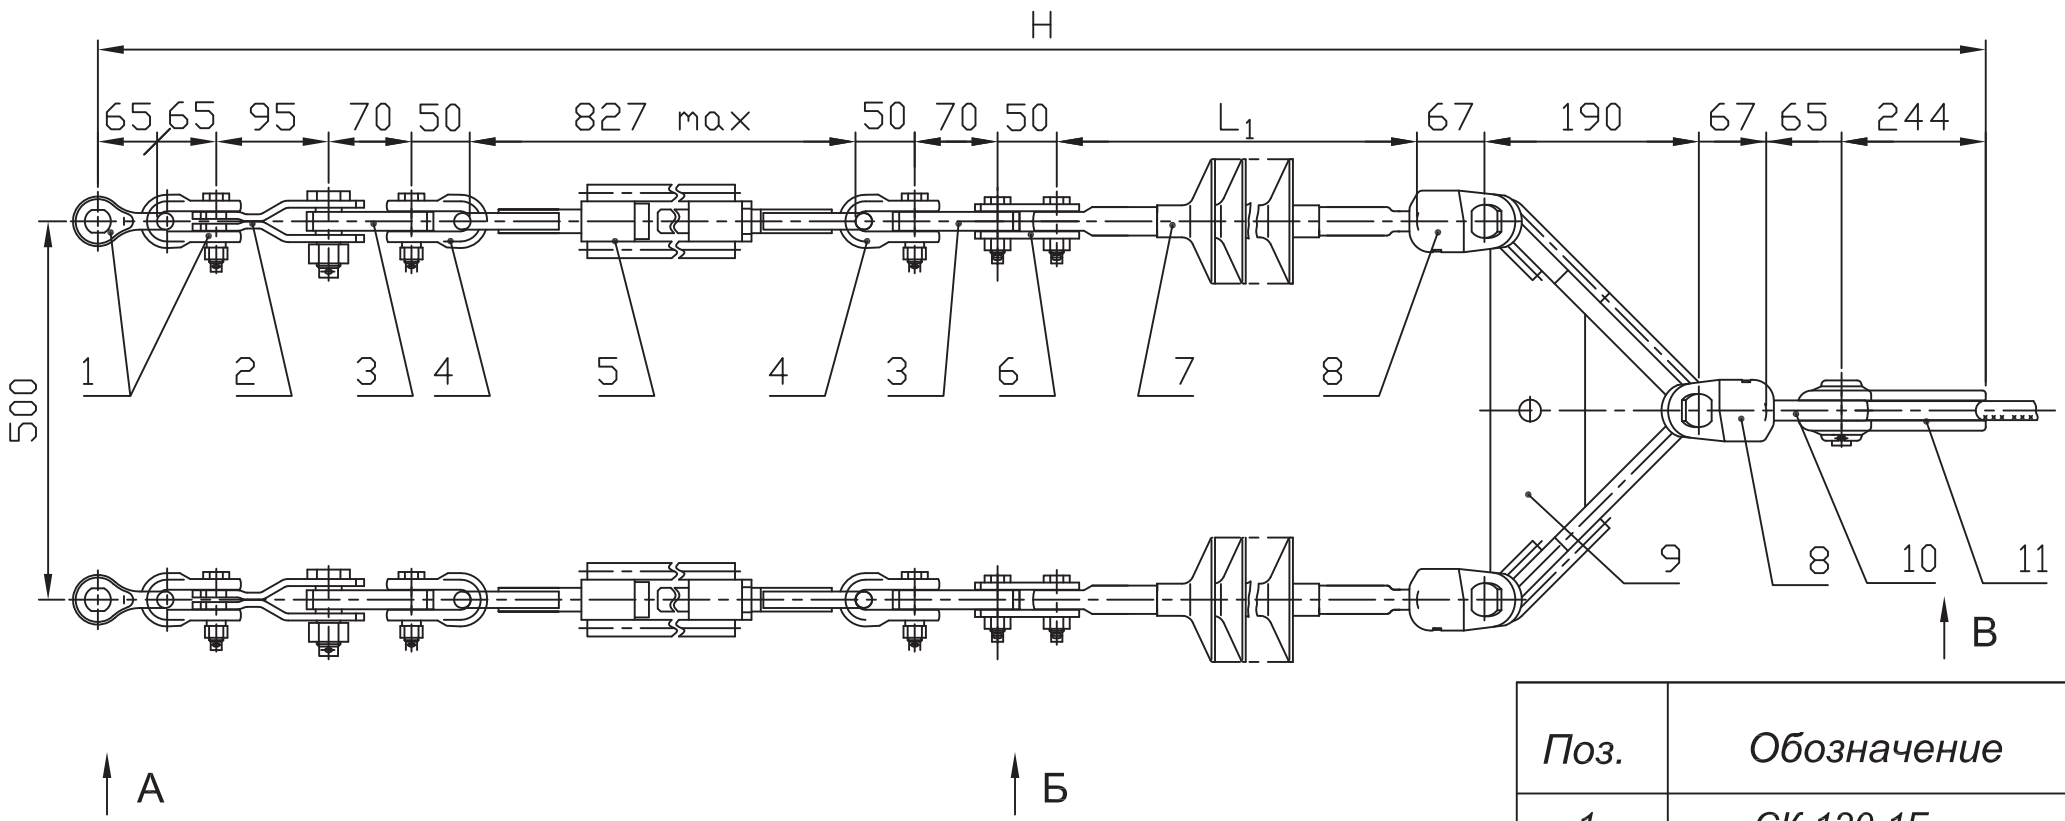

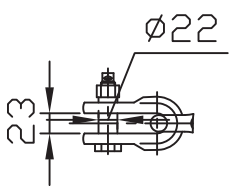

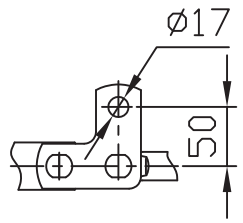

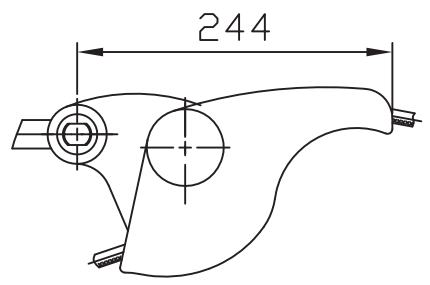

Поз.	Обозначение	Наименование	Кол.	Масса ед. кг	Прим.
1	СК-120-1Б	Скоба	4	0,92	
2	ПРТ-12/7-2	Звено переходное	2	0,7	
3	ПР-7-6	Звено прямое	4	0,44	
4	СК-70-1Б	Скоба	4	0,38	
5	ПТР-7-1	Талреп	2	3,0	
6	ПТМ-7-3А	Звено монтажное	2	0,63	
7		Изолятор исп. СП	2	См. табл.	
8	УСК-7-16	Ушко специальное	3	1,2	
9	2КУ-12-1	Коромысло	1	4,75	
10	СР-7-16	Серьга	1	0,3	
11	НЗ-60/11-17	Зажим натяжной	1	1,5	
Масса арматуры, кг				25,8	
Масса изолирующей подвески, кг				см. табл.	

Напряжение ВЛ, кВ	Изолятор, поз.6		Изолирующая подвеска	
	L1, мм	Масса, кг	Н, мм	Масса, кг
35	475	1,5	2450	28,8
110	1175	3,0	3150	31,8

Взам. инв. N

Подп. и дата

Инв. N подл.

Утв.	Вигдергауз		
Пров.	Липунцов		
Разраб.	Власкина		

ЭСИП-0058


ЭСС.001 ТМ - т.1

Натяжные двухцепные изолирующие с полимерными изоляторами ряда 70 кН подвески проводов АС70/11 - АС150/24 к а/у металлическим и ж/б опорам ВЛ 35, 110 кВ


Стадия	Лист	Листов
Р		1

Филиал ОАО "ФСК ЕЭС" "Электросетьсервис"


Формат А3

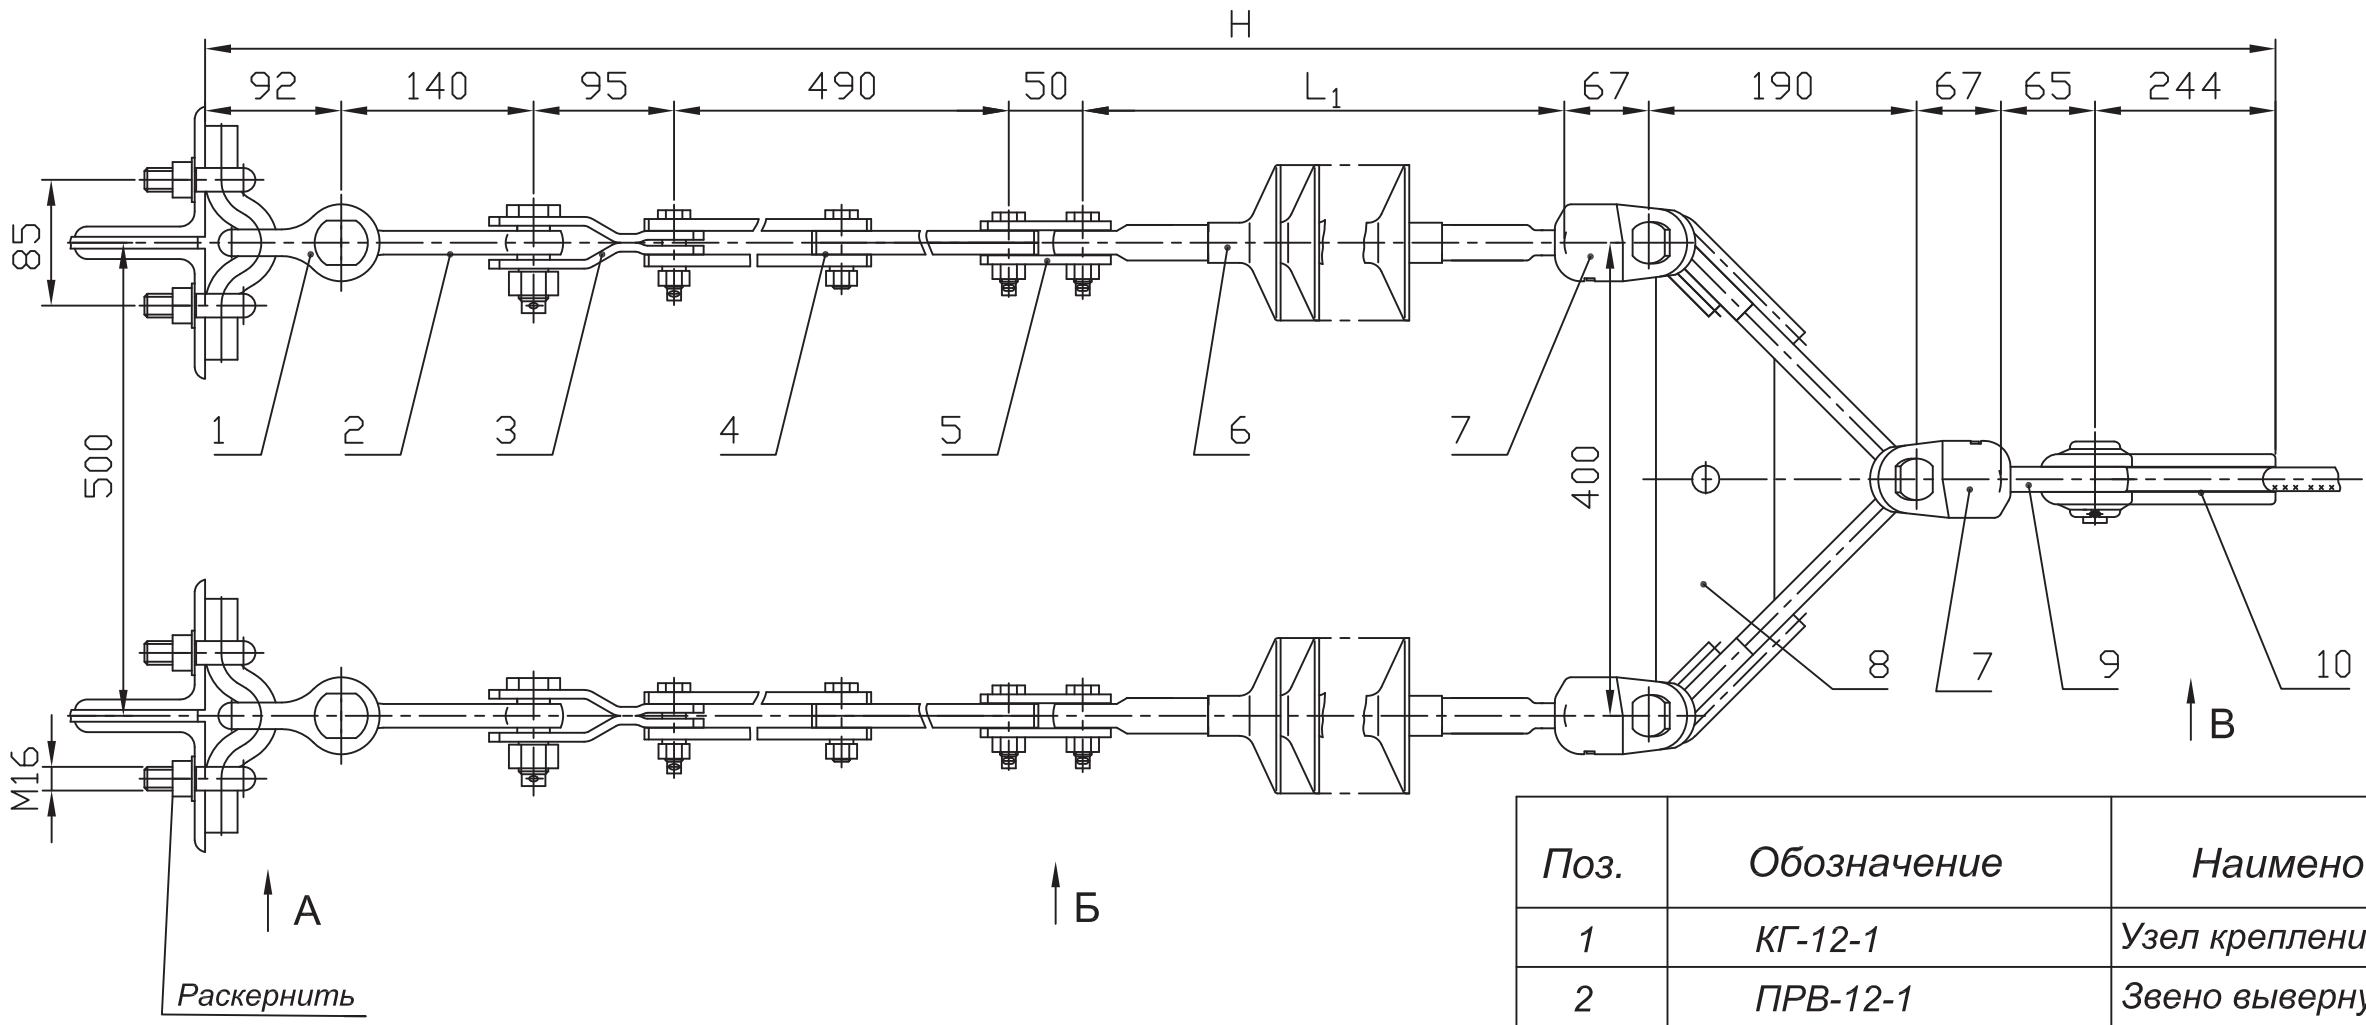


А

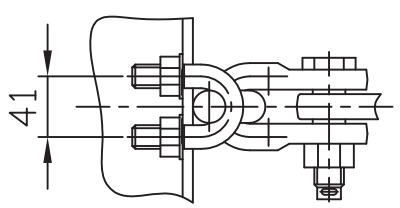

Б

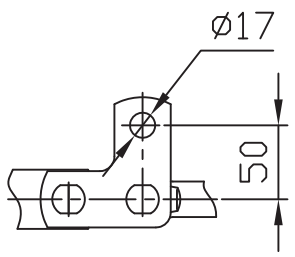

В

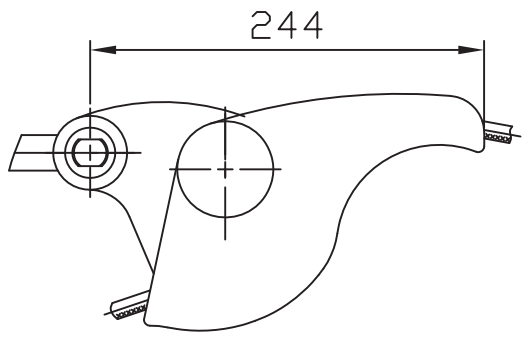

Напряжение ВЛ, кВ	Изолятор, поз.6		Изолирующая подвеска	
	L1, мм	Масса, кг	H, мм	Масса, кг
35	475	1,5	1975	25,2
110	1175	3,0	2675	28,2

Поз.	Обозначение	Наименование	Кол.	Масса ед. кг	Прим.
1	КГ-12-1	Узел крепления	2	2,15	
2	ПРВ-12-1	Звено вывернутое	2	0,43	
3	ПРТ-7/12-2	Звено переходное	2	0,9	
4	ПРР-7-1	Звено регулируемое	2	1,91	
5	ПТМ-7-3А	Звено монтажное	2	0,63	
6		Изолятор исп. СП	2	См. табл.	
7	УСК-7-16	Ушко специальное	3	1,2	
8	2КУ-12-1	Коромысло	1	4,75	
9	СР-7-16	Серьга	1	0,3	
10	НЗ-60/11-17	Зажим натяжной	1	1,5	
Масса арматуры, кг				22,2	
Масса изолирующей подвески, кг				см. табл.	

Утв.	Вигдергауз		
Пров.	Липунцов		
Разраб.	Власкина		

ЭСИП-0059

ЭСС.001 ТМ - т.1

Натяжные двухцепные изолирующие с полимерными изоляторами ряда 70 кН подвески проводов АС70/11 - АС150/24 к а/у металлическим и ж/б опорам ВЛ 35, 110 кВ

Стадия	Лист	Листов
Р		1


Филиал ОАО "ФСК ЕЭС" "Электросетьсервис"

Формат А3


Взам. инв. N

Подп. и дата


Инв. N подл.

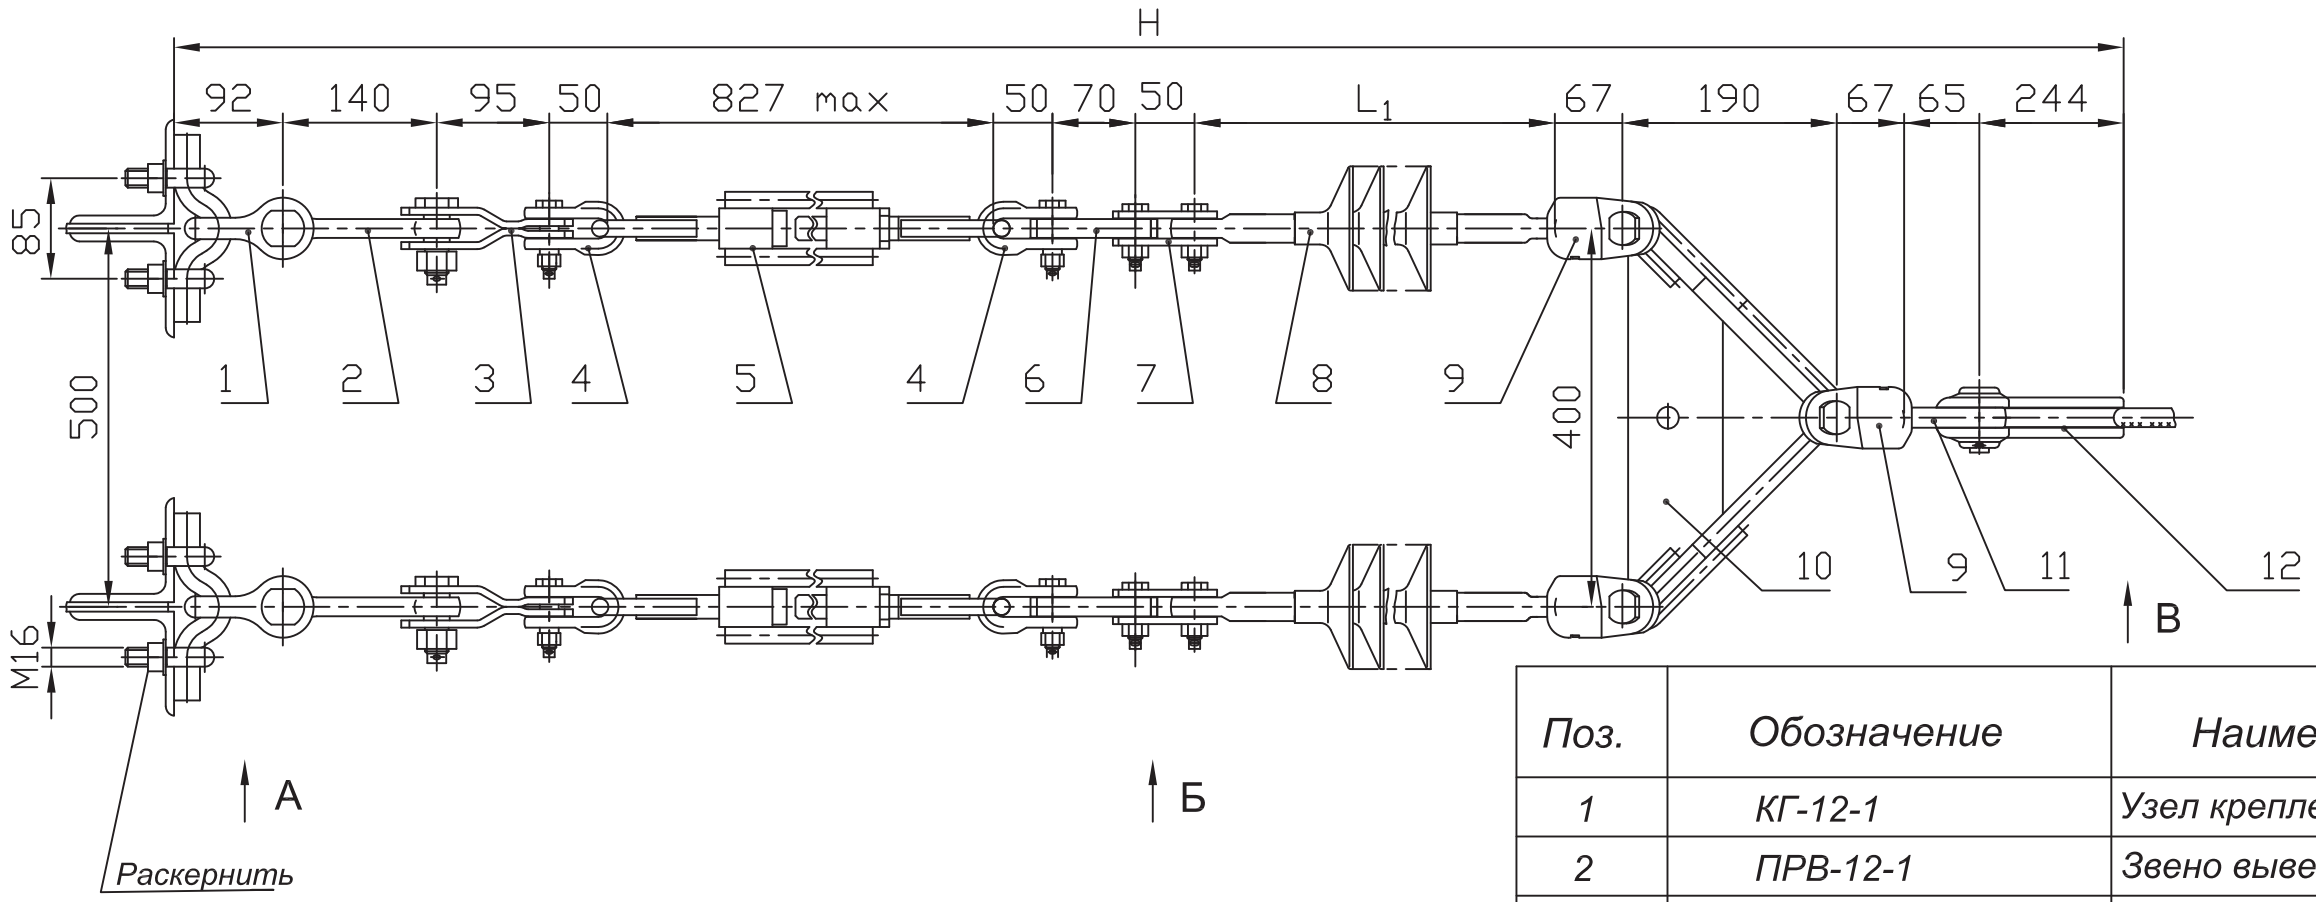


А

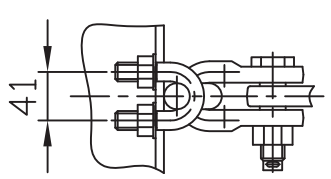

Б

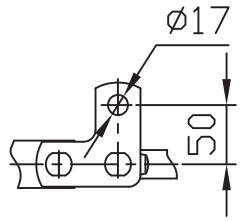

В

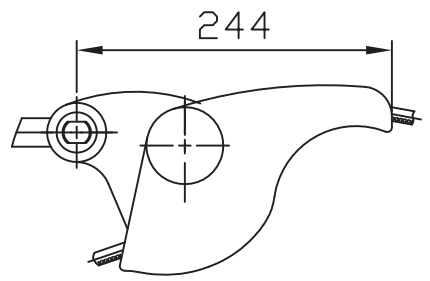

Напряжение ВЛ, кВ	Изолятор, поз.8		Изолирующая подвеска	
	L1, мм	Масса, кг	H, мм	Масса, кг
35	475	1,5	2482	23,8
110	1175	3,0	3182	26,8

Поз.	Обозначение	Наименование	Кол.	Масса ед. кг	Прим.
1	КГ-12-1	Узел крепления	2	2,15	
2	ПРВ-12-1	Звено вывернутое	2	0,43	
3	ПРТ-7/12-2	Звено регулируемое	2	0,9	
4	СК-70-1Б	Скоба	4	0,38	
5	ПТР-7-1	Талреп	2	3,0	
6	ПР-7-6	Звено прямое	2	0,44	
7	ПТМ-7-3А	Звено монтажное	2	0,63	
8		Изолятор исп. СП	2	См. табл.	
9	УСК-7-16	Ушко специальное	3	1,2	
10	2КУ-12-1	Коромысло	1	4,75	
11	СР-7-16	Серьга	1	0,3	
12	НЗ-60/11-17	Зажим натяжной	1	1,5	
Масса арматуры, кг				20,8	
Масса изолирующей подвески, кг				см. табл.	

ЭСИП-0060

ЭСС.001 ТМ - т.1

Утв.	Вигдергауз		
Пров.	Липунцов		
Разраб.	Власкина		

Натяжные двухцепные изолирующие с полимерными изоляторам ряда 70 кН подвески проводов АС70/11 - АС150/24 к а/у металлическим и ж/б опорам ВЛ 35, 110 кВ

Стадия	Лист	Листов
Р		1


Филиал ОАО "ФСК ЕЭС" "Электросетьсервис"

Взам. инв. N


Подп. и дата

Инв. N подл.


Формат А3

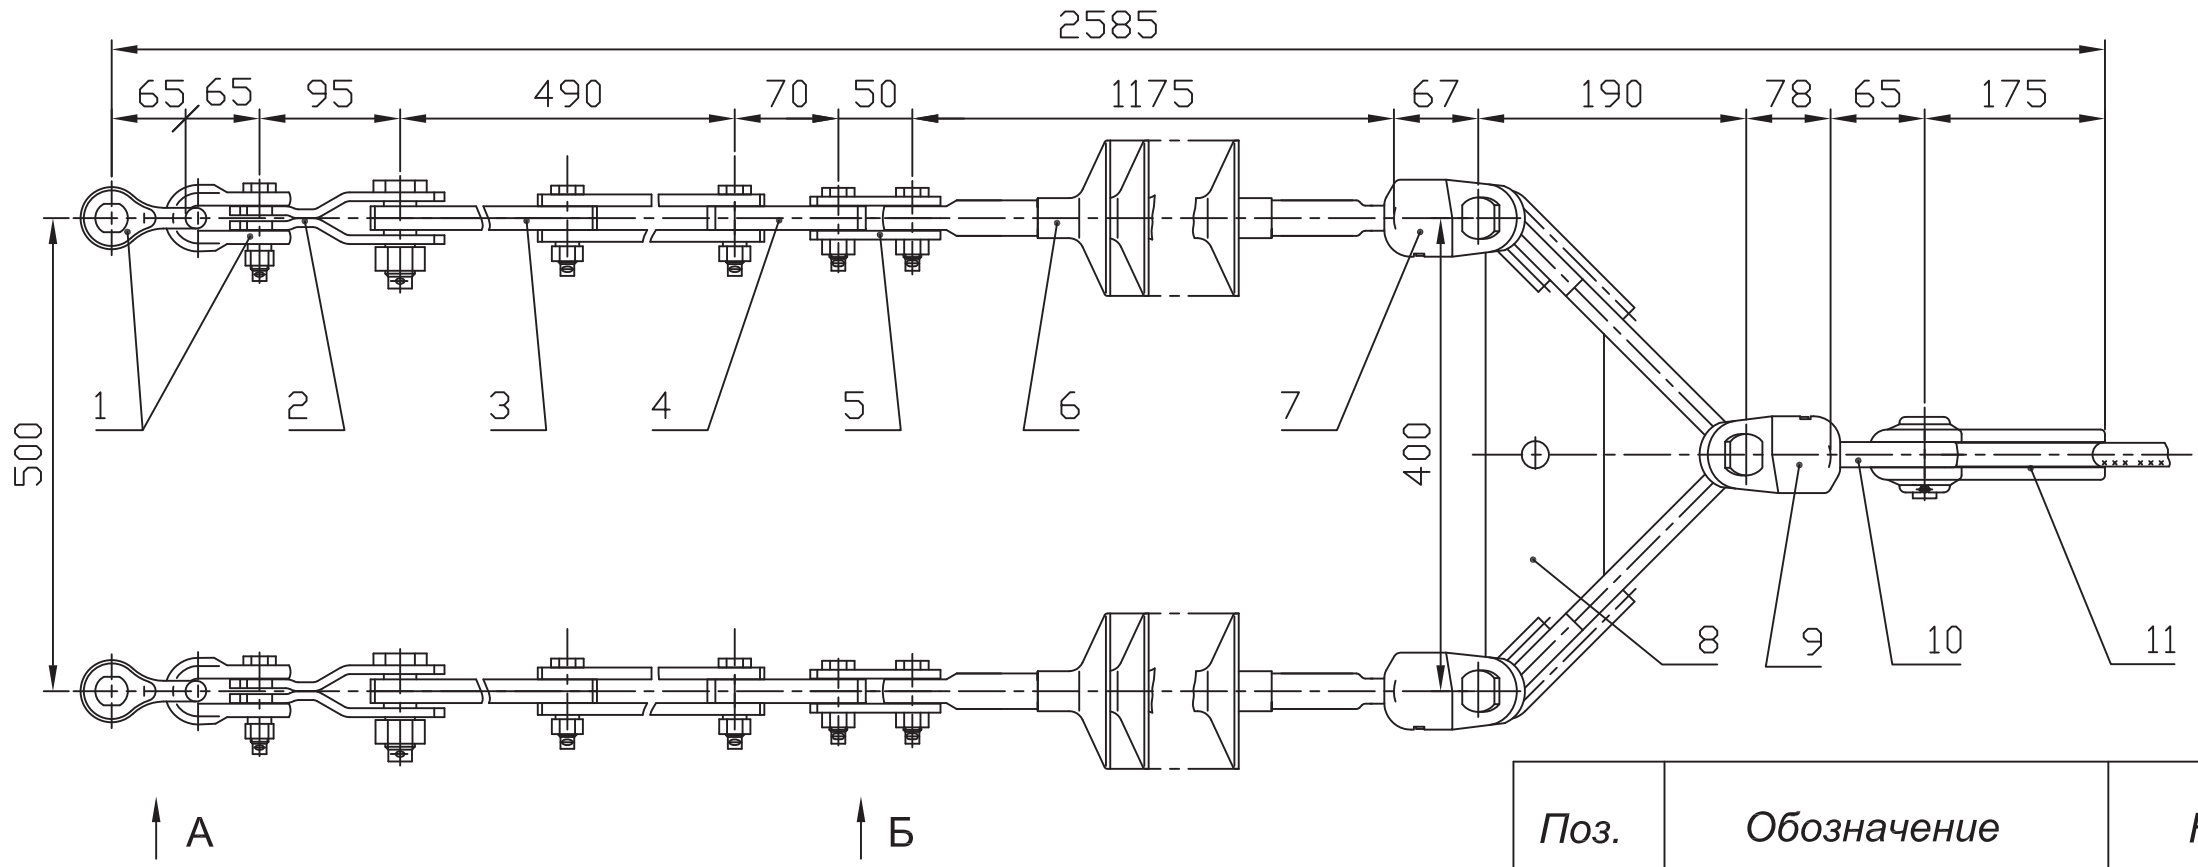

А

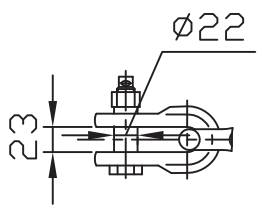

Б

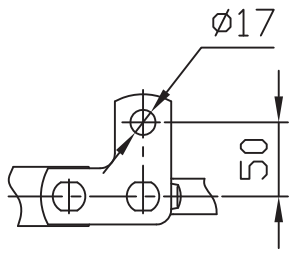

Поз.	Обозначение	Наименование	Кол.	Масса ед. кг	Прим.
1	СК-120-1Б	Скоба	4	0,92	
2	ПРТ-12/7-2	Звено переходное	2	0,7	
3	ПРР-7-1	Звено регулируемое	2	1,91	
4	ПР-7-6	Звено прямое	2	0,44	
5	ПТМ-7-3А	Звено монтажное	2	0,63	
6	ЛК 70/110-	Изолятор исп. СП	2	3,5	
7	УСК-7-16	Ушко специальное	2	1,2	
8	2КУ-12-1	Коромысло	1	4,75	
9	УСК-12-16	Ушко специальное	1	2,07	
10	СР-7-16	Серьга	1	0,41	
11	НБ-90/15-22	Зажим натяжной	1	2,84	
Масса арматуры, кг				23,5	
Масса изолирующей подвески, кг				30,5*	

* Масса указана с изолятором ЛК70/110-3-СП

Взам. инв. N

Подп. и дата

Инв. N подл.

Утв.	Вигдергауз		
Пров.	Липунцов		
Разраб.	Власкина		

ЭСИП-0061


ЭСС.001 ТМ - т.1

Натяжные двухцепные изолирующие с полимерными изоляторами ряда 70 кН подвески проводов АС185/29, АС240/32 и АС240/39 к а/у металлическим и ж/б опорам ВЛ 110 кВ


Стадия	Лист	Листов
Р		1

Филиал ОАО "ФСК ЕЭС" "Электросетьсервис"


Формат А3

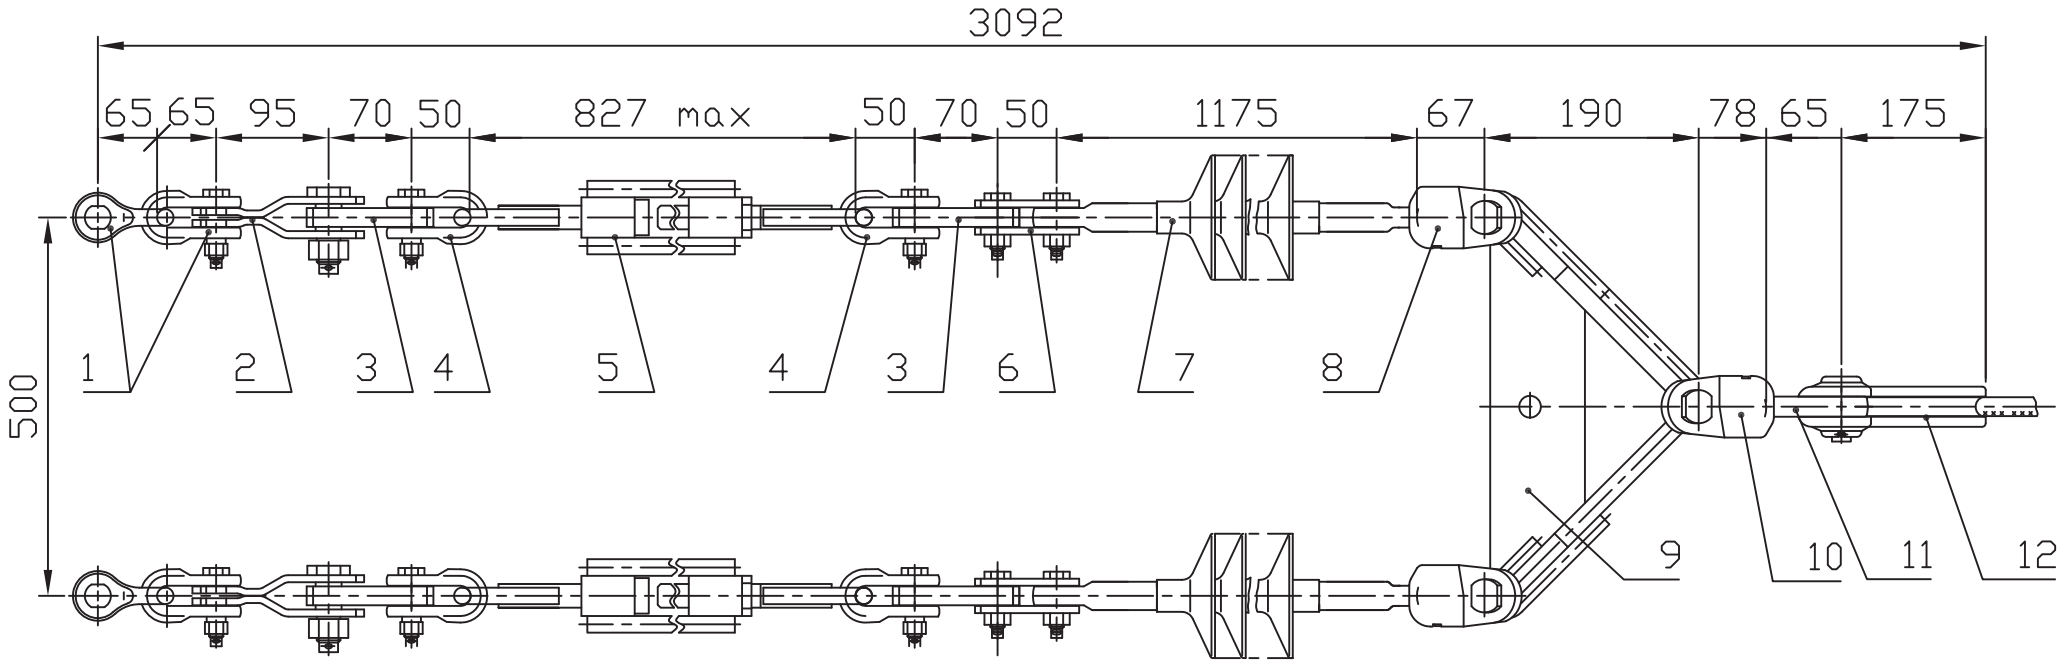

А

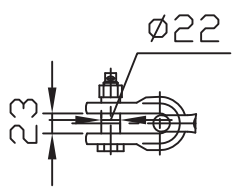

Б

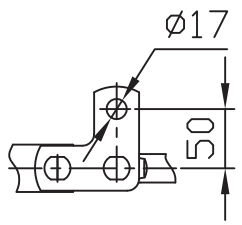


* Масса указана с изолятором ЛК 70/110-3-СП

Поз.	Обозначение	Наименование	Кол.	Масса ед. кг	Прим.
1	СК-120-1Б	Скоба	4	0,92	
2	ПРТ-12/7-2	Звено переходное	2	0,7	
3	ПР-7-6	Звено прямое	4	0,44	
4	СК-70-1Б	Скоба	4	0,38	
5	ПТР-7-1	Талреп	2	3,0	
6	ПТМ-7-3А	Звено монтажное	2	0,63	
7	ЛК 70/110-	Изолятор исп. СП	2	3,5	
8	УСК-7-16	Ушко специальное	2	1,2	
9	2КУ-12-1	Коромысло	1	4,75	
10	УСК-12-16	Ушко специальное	1	2,07	
11	СР-7-16	Серьга	1	0,41	
12	НБ-90/15-22	Зажим натяжной	1	2,84	
Масса арматуры, кг				28,1	
Масса изолирующей подвески, кг				35,1*	


		ЭСИП-0062	
		ЭСС.001 ТМ - т.1	
Утв.	Вигдергауз	Натяжные двухцепные изолирующие с полимерными изоляторами ряда 70 кН подвески проводов АС185/29, АС240/32 и АС240/39 к а/у металлическим и ж/б опорам ВЛ 110 кВ	Стадия: Р; Лист: ; Листов: 1
Пров.	Липунцов		Филиал ОАО "ФСК ЕЭС" "Электросетьсервис"
Разраб.	Власкина		

Взам. инв. N | Подп. и дата | Инв. N подл.


Формат А3

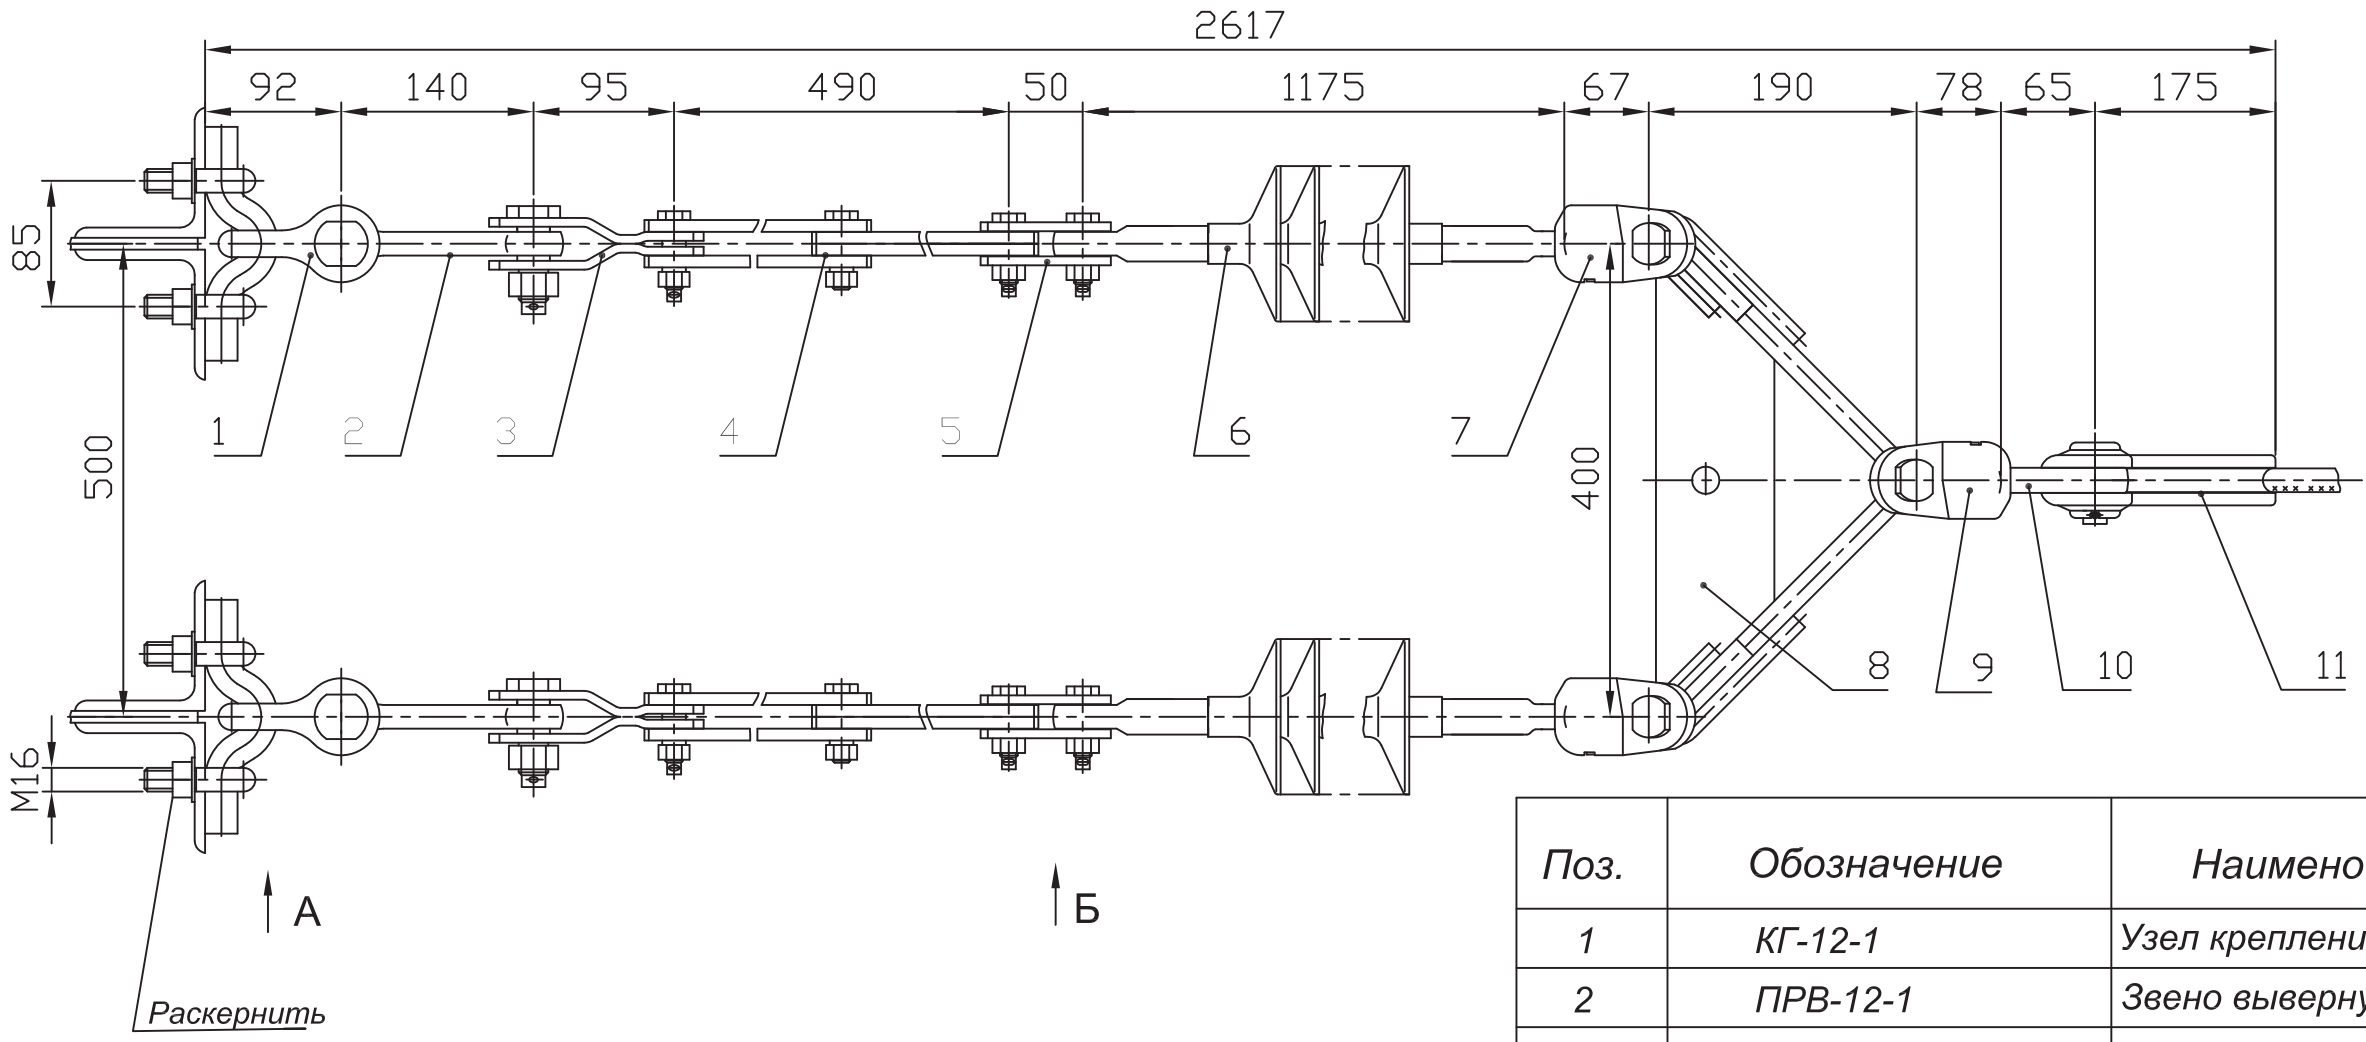

А

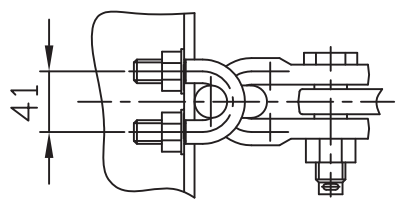

Б

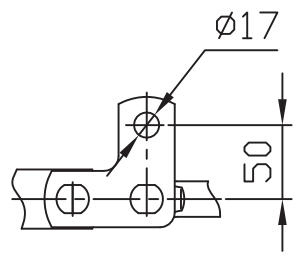

Поз.	Обозначение	Наименование	Кол.	Масса ед. кг	Прим.
1	КГ-12-1	Узел крепления	2	2,15	
2	ПРВ-12-1	Звено вывернутое	2	0,43	
3	ПРТ-7/12-2	Звено переходное	2	0,9	
4	ПРР-7-1	Звено регулируемое	2	1,91	
5	ПТМ-7-3А	Звено монтажное	2	0,63	
6	ЛК 70/110-	Изолятор исп. СП	2	3,5	
7	УСК-7-16	Ушко специальное	2	1,2	
8	2КУ-12-1	Коромысло	1	4,75	
9	УСК-12-16	Ушко специальное	1	2,07	
10	СР-12-16	Серьга	1	0,41	
11	НБ-90/15-22	Зажим натяжной	1	2,84	
Масса арматуры, кг				24,51	
Масса изолирующей подвески, кг				31,51*	

* Масса указана с изолятором ЛК 70/110-3-СП

Взам. инв. N

Подп. и дата


Инв. N подл.

ЭСИП-0063


ЭСС.001 ТМ - т.1

Утв.	Вигдергауз	Натяжные двухцепные изолирующие с полимерными изоляторами ряда 70 кН подвески проводов АС185/29, АС240/32 и АС240/39 к а/у металлическим опорам ВЛ 110 кВ	Стадия: Р; Лист: ; Листов: 1
Пров.	Липунцов		Филиал ОАО "ФСК ЕЭС" "Электросетьсервис"
Разраб.	Власкина		


Формат А3

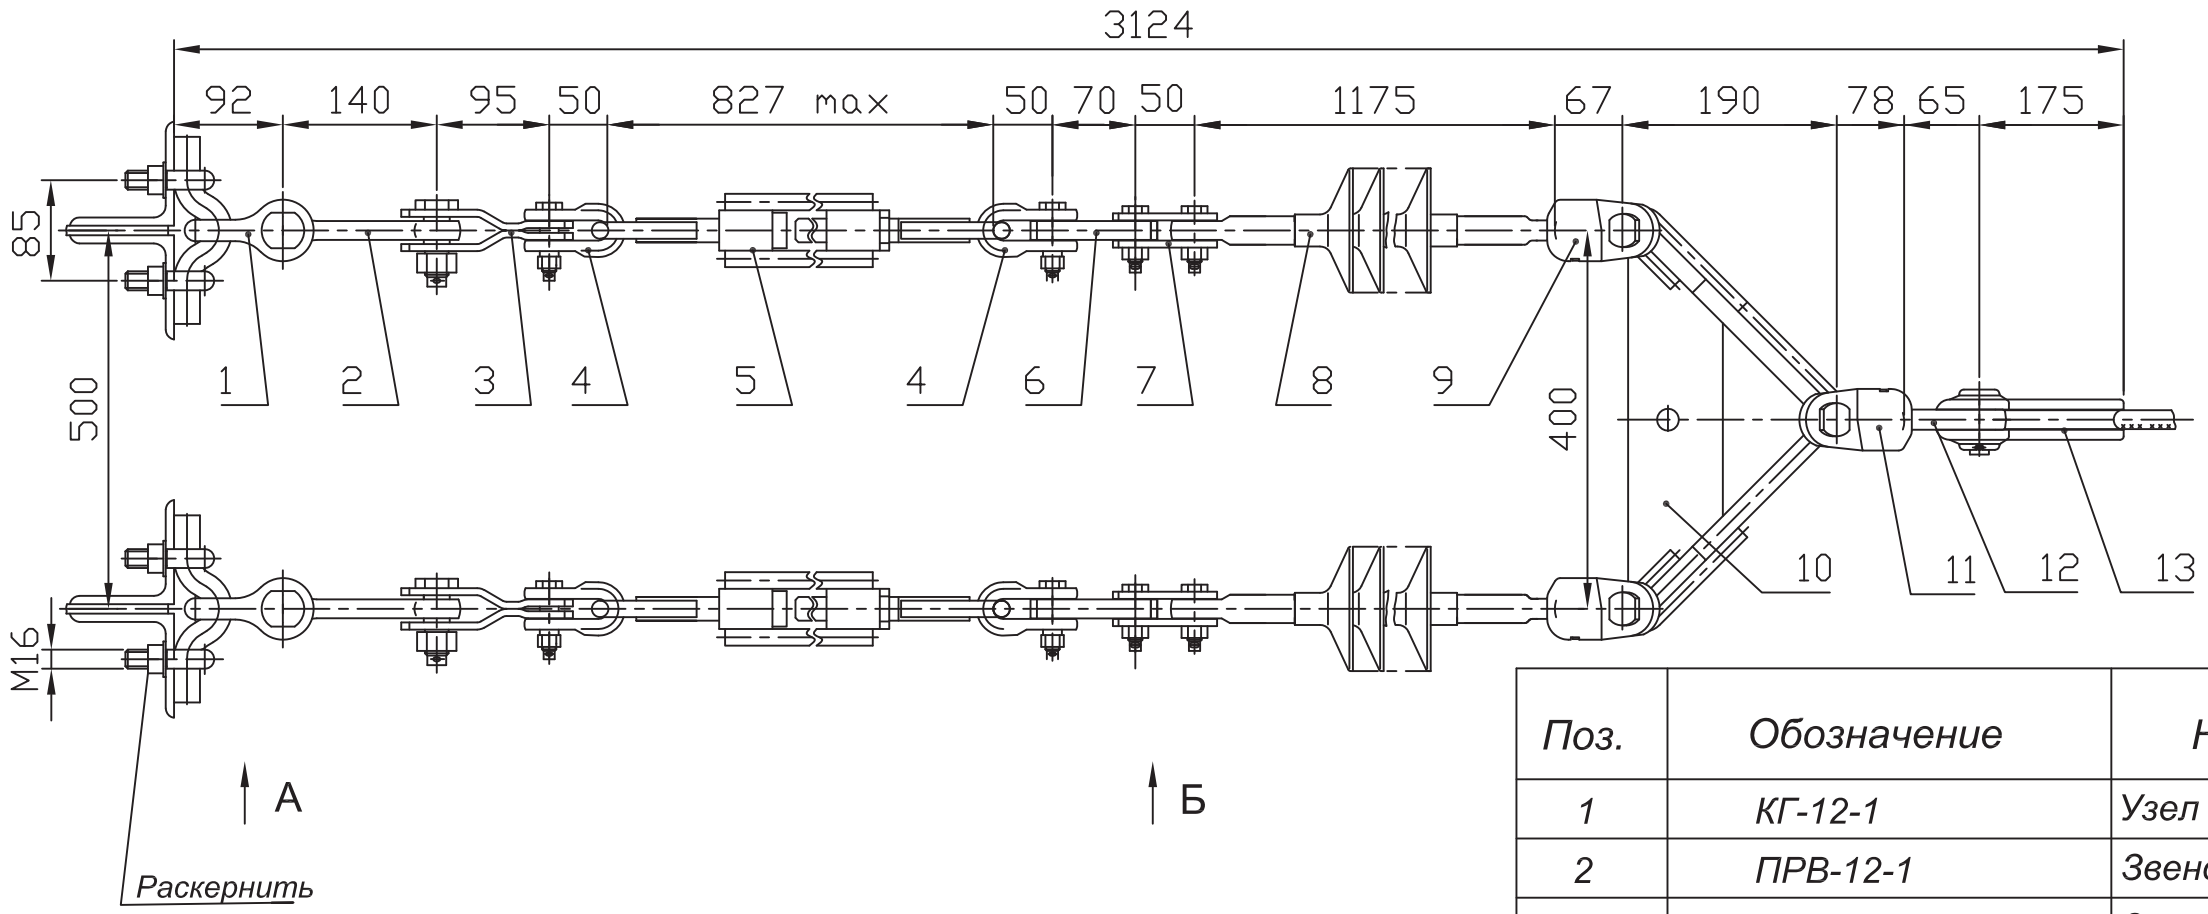

А

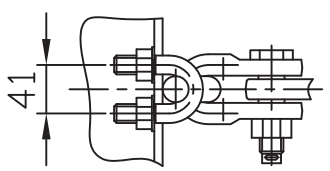

Б

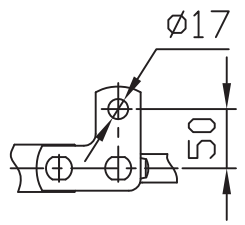

Поз.	Обозначение	Наименование	Кол.	Масса ед. кг	Прим.
1	КГ-12-1	Узел крепления	2	2,15	
2	ПРВ-12-1	Звено вывернутое	2	0,43	
3	ПРТ-7/12-2	Звено регулируемое	2	0,9	
4	СК-70-1Б	Скоба	4	0,38	
5	ПТР-7-1	Талреп	2	3,0	
6	ПР-7-6	Звено прямое	2	0,44	
7	ПТМ-7-3А	Звено монтажное	2	0,63	
8	ЛК 70/110-	Изолятор исп. СП	2	3,5	
9	УСК-7-16	Ушко специальное	2	1,2	
10	2КУ-12-1	Коромысло	1	4,75	
11	УСК-12-16	Ушко специальное	1	2,07	
12	СР-12-16	Серьга	1	0,41	
13	НБ-90/15-22	Зажим натяжной	1	2,84	
Масса арматуры, кг				29,09	
Масса изолирующей подвески, кг				36,1*	

* Масса указана с изолятором ЛК 70/110-4-СП

Взам. инв. N

Подп. и дата

Инв. N подл.

ЭСИП-0064

ЭСС.001 ТМ - т.1


Утв.	Вигдергауз		
Пров.	Липунцов		
Разраб.	Власкина		

Натяжные двухцепные изолирующие с полимерными изоляторами ряда 70 кН подвески проводов АС185/29, АС210/32 и АС240/39 к а/у металлическим опорам ВЛ 110 кВ


Стадия	Лист	Листов
Р		1

Филиал ОАО "ФСК ЕЭС" "Электросетьсервис"

Формат А3

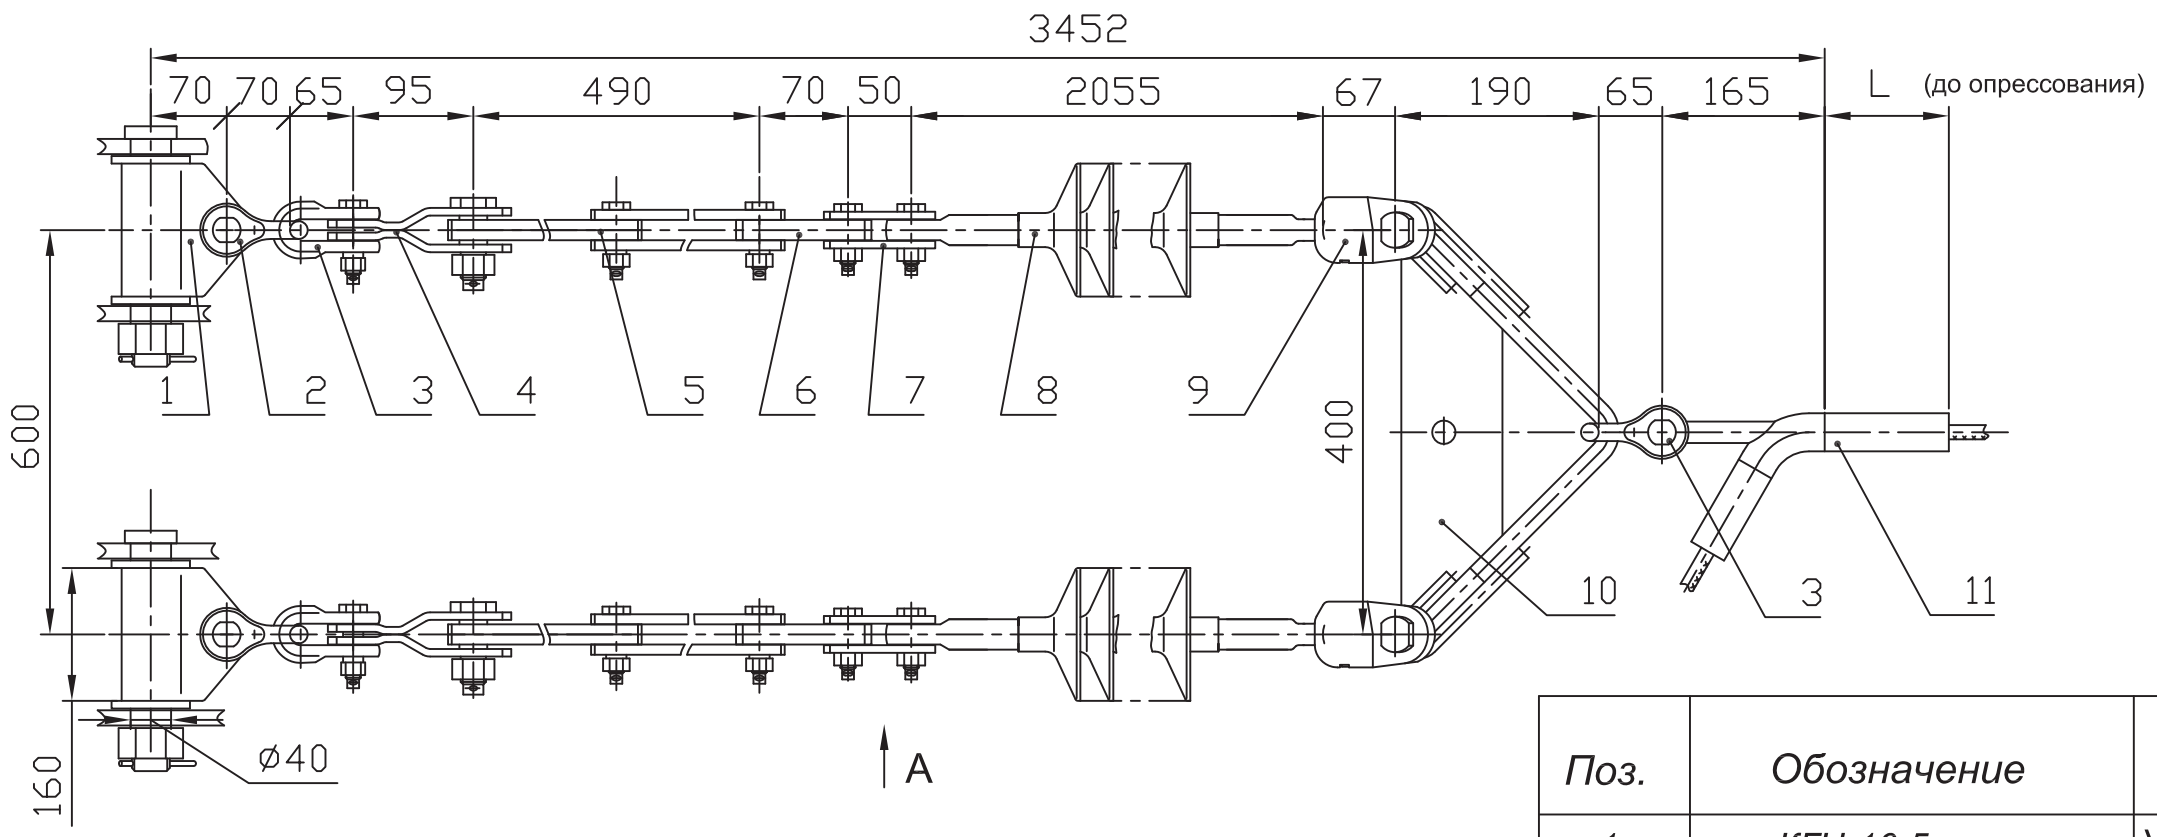

Вариант

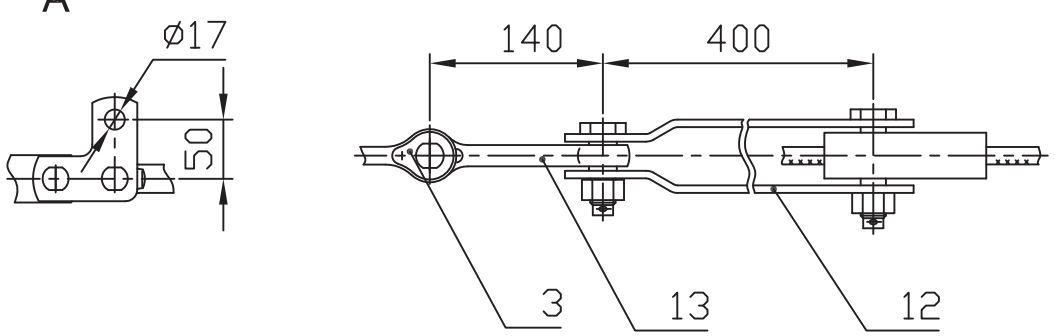

1. *При заказе натяжного клинового зажима типа НК-300-1 следует указывать марку провода. В спецификацию добавляется ПРВ-12-1 (поз.13).*

2. ** Масса указана с зажимом НАС-330-1и изолятором ЛК 70/220-3-СП.*

Провод по ГОСТ 839-80		Зажим, поз.11			Масса армат., кг
Марка	Диаметр, мм	Обозначение	L, мм	Масса, кг	
АС240/32	21,6	НАС-240-1Б	160	1,63	31,8
АС240/39		НАС-240-2Б		1,60	31,8
АС300/39	24,0	НАС-330-1Б	175	1,99	32,2

Поз.	Обозначение	Наименование	Кол.	Масса ед. кг	Прим.
1	КГН-16-5	Узел крепления	2	5,23	
2	СК-16-1А	Скоба	2	1,22	
3	СК-120-1Б	Скоба	3	0,92	
4	ПРТ-12/7-2	Звено переходное	2	0,7	
5	ПРР-7-1	Звено регулируемое	2	1,91	
6	ПР-7-6	Звено прямое	2	0,44	
7	ПТМ-7-3А	Звено монтажное	2	0,63	
8	ЛК 70/220-	Изолятор исп. СП	2	8,0	
9	УСК-7-16	Ушко специальное	2	1,2	
10	2КУ-12-1	Коромысло	1	4,75	
11	См. таблицу	Зажим натяжной	1	См. табл.	
12	НК-300-1	Зажим клиновой	1	5,1	
13	ПРВ-12-1	Звено вывернутое	1	0,43	
Масса арматуры, кг				см. табл.	
Масса изолирующей подвески, кг				48,2*	


ЭСИП-0065

ЭСС.001 ТМ - т.1

Утв.	Вигдергауз			Натяжные двухцепные изолирующие с полимерными изоляторами ряда 70 кН подвески проводов АС240/32 - АС300/39 к а/у металлическим опорам ВЛ 220 кВ	Стадия: Р; Лист: ; Листов: 1
Пров.	Липунцов				Филиал ОАО "ФСК ЕЭС" "Электросетьсервис"
Разраб.	Власкина				


Взам. инв. N | Подп. и дата | Инв. N подл.


Формат А3

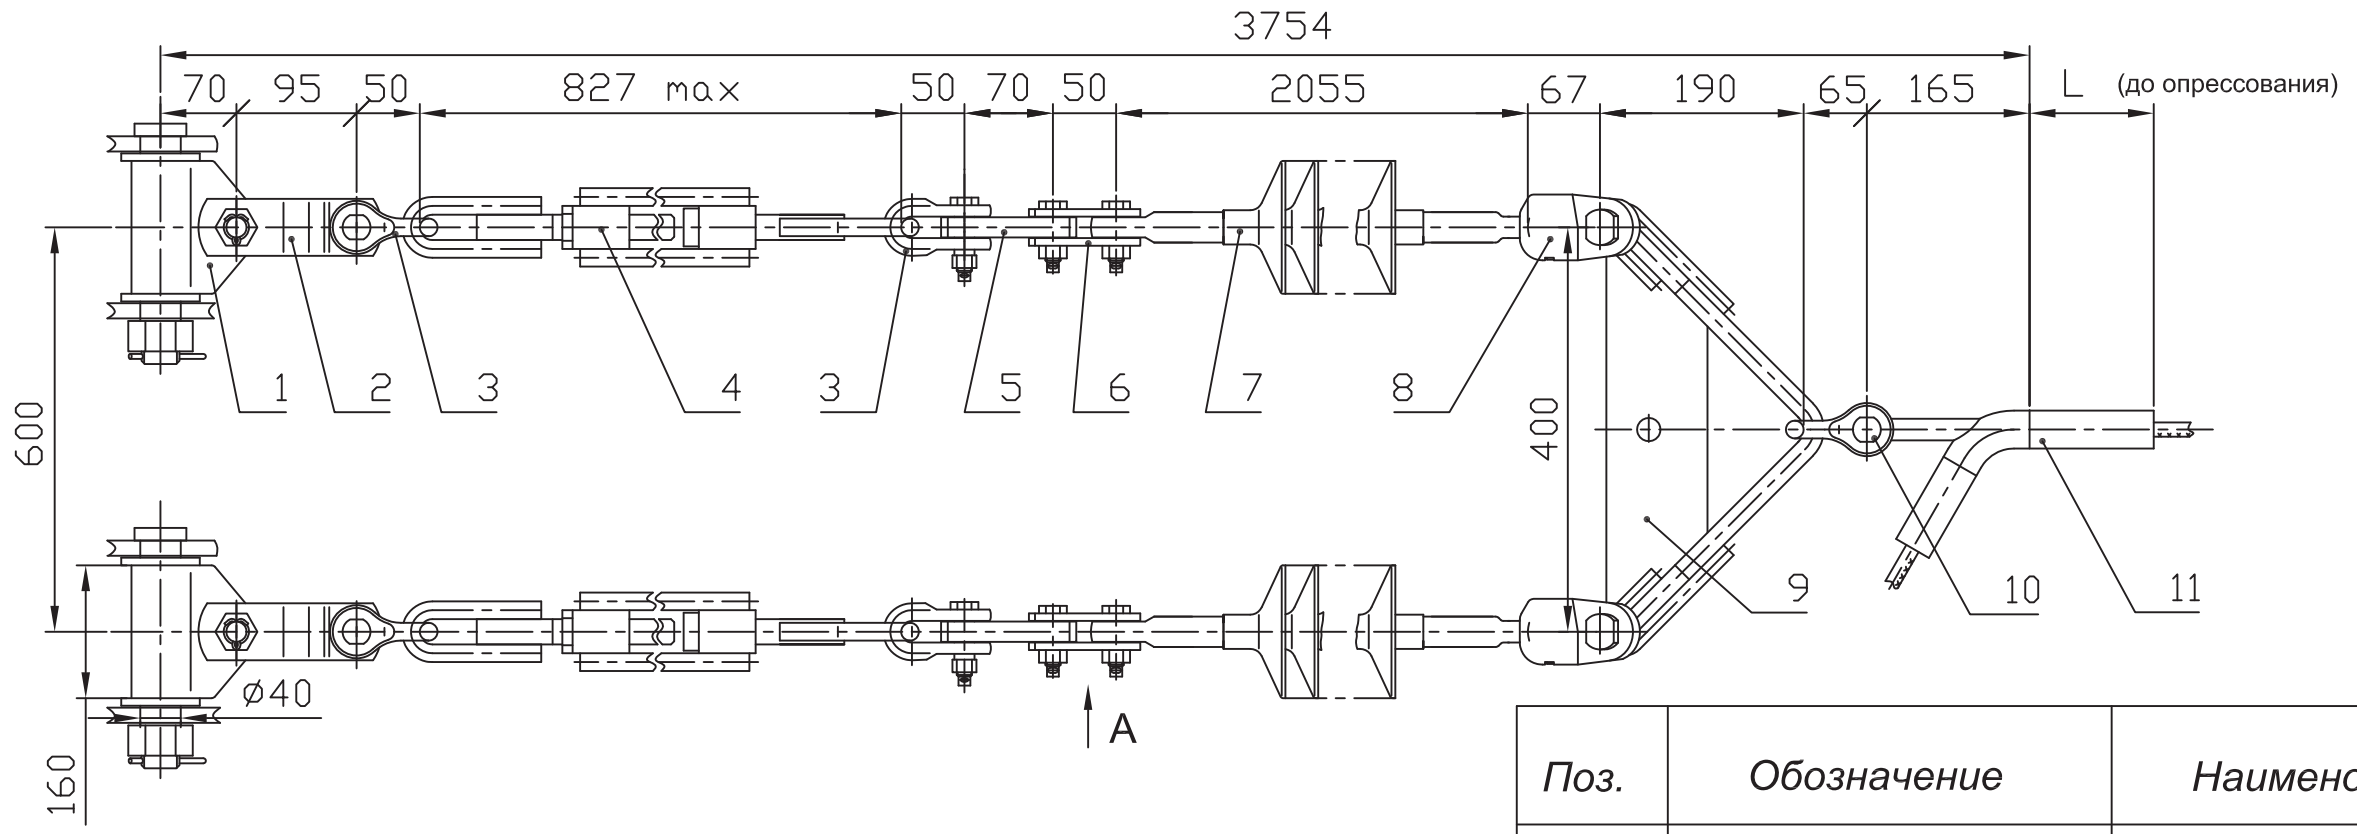

Вариант

A

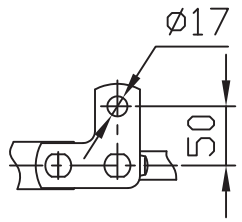

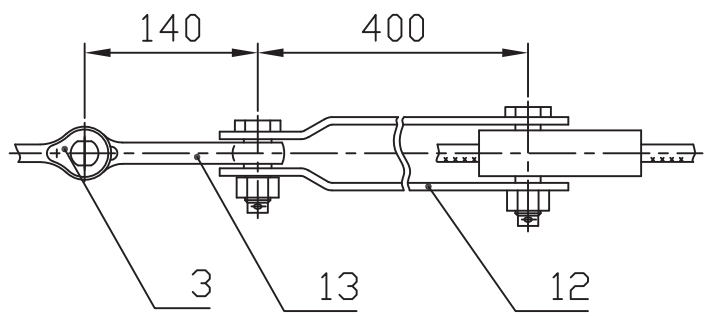

1. При заказе натяжного клинового зажима типа НК-300-1 следует указывать марку провода. В спецификацию добавляется ПРВ-12-1 (поз.13).

2. * Масса указана с зажимом НАС-330-1Б и изолятором ЛК 70/220-3-СП.

Провод по ГОСТ 839-80		Зажим, поз.11			Масса армат., кг
Марка	Диаметр, мм	Обозначение	L, мм	Масса, кг	
АС240/32	21,6	НАС-240-1Б	160	1,63	31,7
АС240/39		НАС-240-2Б		1,60	31,7
АС300/39	24,0	НАС-330-1Б	175	1,99	32,1

Поз.	Обозначение	Наименование	Кол.	Масса ед. кг	Прим.
1	КГН-16-5	Узел крепления	2	5,23	
2	ПРТ-7/16-2	Звено переходное	2	0,96	
3	СК-70-1Б	Скоба	4	0,38	
4	ПТР-7-1	Талреп	2	3,0	
5	ПР-7-6	Звено прямое	2	0,44	
6	ПТМ-7-3А	Звено монтажное	2	0,63	
7	ЛК 70/220-	Изолятор исп. СП	2	8,0	
8	УСК-7-16	Ушко специальное	2	1,2	
9	2КУ-12-1	Коромысло	1	4,75	
10	СК-120-1Б	Скоба	1	0,92	
11	См. таблицу	Зажим натяжной	1	См. табл.	
12	НК-300-1	Зажим клиновой	1	5,1	
13	ПРВ-12-1	Звено вывернутое	1	0,43	
Масса арматуры, кг				См. таблицу	
Масса изолирующей подвески, кг				48,1*	

ЭСИП-0066

ЭСС.001 ТМ - т.1

Утв.	Вигдергауз		
Пров.	Липунцов		
Разраб.	Власкина		


Натяжные двухцепные изолирующие с полимерными изоляторами ряда 70 кН подвески проводов АС240/32 - АС300/39 к а/у металлическим опорам ВЛ 220 кВ


Стадия	Лист	Листов
Р		1

Филиал ОАО "ФСК ЕЭС" "Электросетьсервис"


Формат А3

Взам. инв. N | Подп. и дата | Инв. N подл.

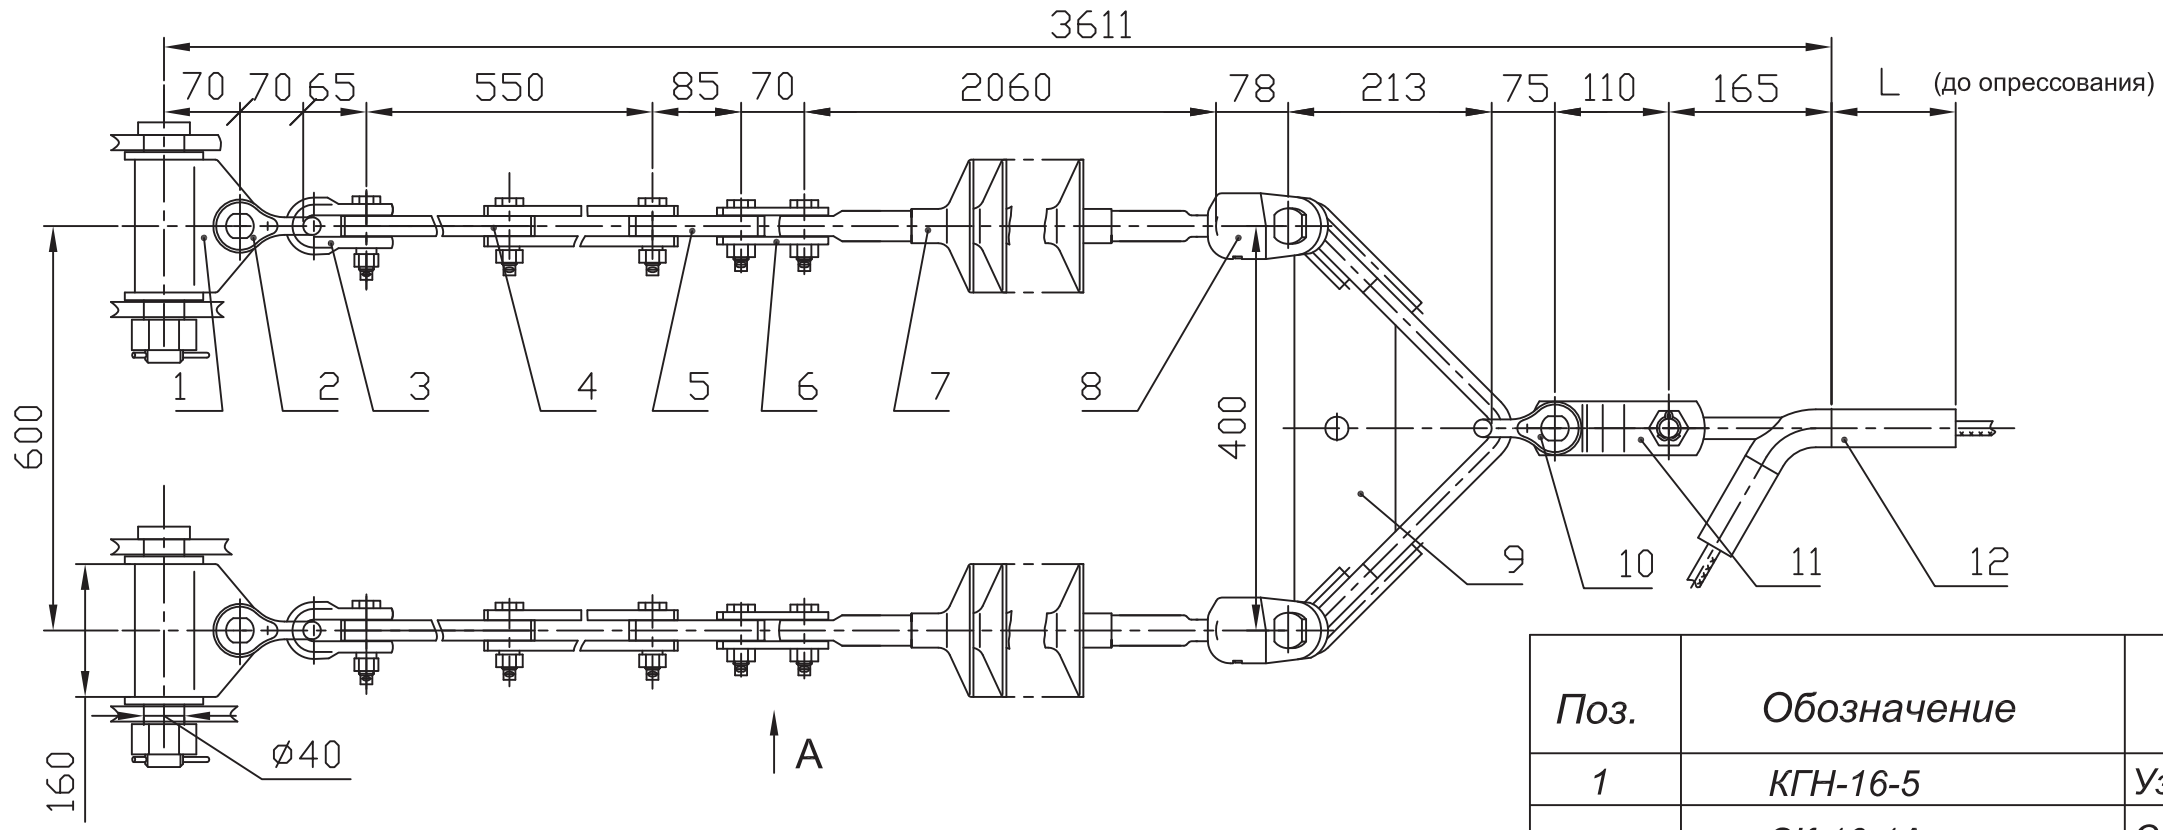

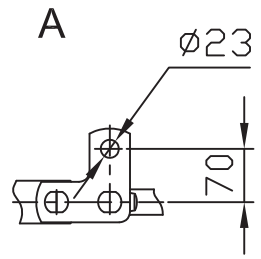

Вариант

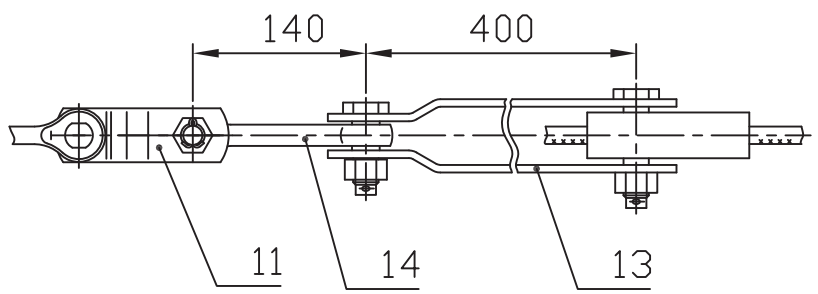

1. *При заказе натяжного клинового зажима типа НК-300-1 (поз.13) следует указывать марку провода. В спецификацию добавляется ПРВ-12-1 (поз.14).*

2. ** Масса указана с зажимом НАС-330-1Б и изолятором ЛК 120/220-3-СП.*

Провод по ГОСТ 839-80		Зажим, поз.12			Масса армат., кг
Марка	Диаметр, мм	Обозначение	L, мм	Масса, кг	
АС240/32	21,6	НАС-240-1Б	160	1,63	44,9
АС240/39		НАС-240-2Б		1,60	44,9
АС300/56	22,4	НАС-330-1Б	175	1,99	45,3
АС300/39	24,0				
АС300/48	24,1				
АС330/43	25,2				

Поз.	Обозначение	Наименование	Кол.	Масса ед. кг	Прим.
1	КГН-16-5	Узел крепления	2	5,23	
2	СК-16-1А	Скоба	2	1,22	
3	СК-120-1Б	Скоба	2	0,92	
4	ПРР-12-1	Звено регулируемое	2	3,69	
5	ПР-12-6	Звено прямое	2	0,94	
6	ПТМ-12-3А	Звено монтажное	2	1,7	
7	ЛК 120/220-	Изолятор исп. СП	2	8,0	
8	УСК-12-16	Ушко специальное	2	2,07	
9	2КУ-30-1	Коромысло	1	8,46	
10	СК-21-1А	Скоба	1	1,82	
11	ПРТ-21/12-2	Звено переходное	1	1,5	
12	См. таблицу	Зажим натяжной	1	См. табл.	
13	НК-300-1	Зажим клиновой	1	5,1	
14	ПРВ-12-1	Звено вывернутое	1	0,43	
Масса арматуры, кг				см. табл.	
Масса изолирующей подвески, кг				61,3*	


ЭСИП-0067

ЭСС.001 ТМ - т.1


Утв.	Вигдергауз	Натяжные двухцепные изолирующие с полимерными изоляторами ряда 120 кН подвески проводов АС240/32 - АС330/43 к а/у металлическим опорам ВЛ 220 кВ	Стадия: Р; Лист; Листов: 1
Пров.	Липунцов		Филиал ОАО "ФСК ЕЭС" "Электросетьсервис"
Разраб.	Власкина		

Взам. инв. N | Подп. и дата | Инв. N подл.

Формат А3

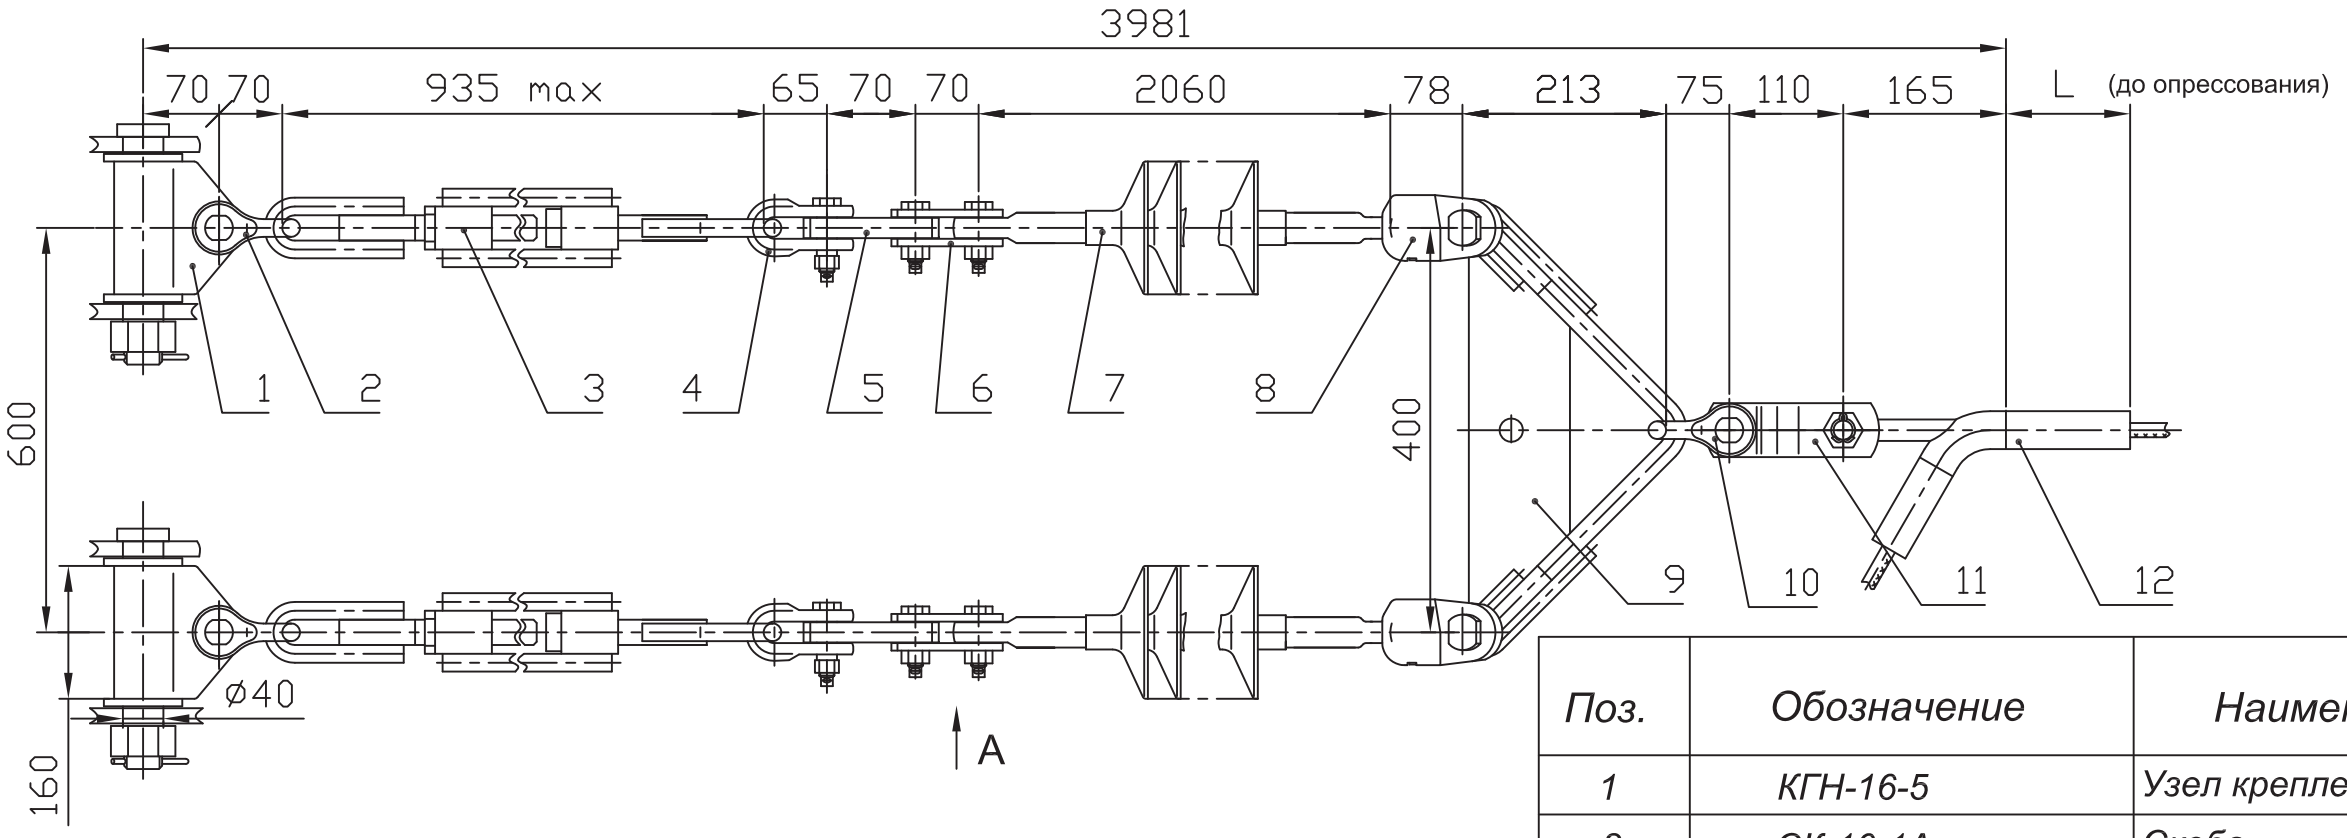

Вариант

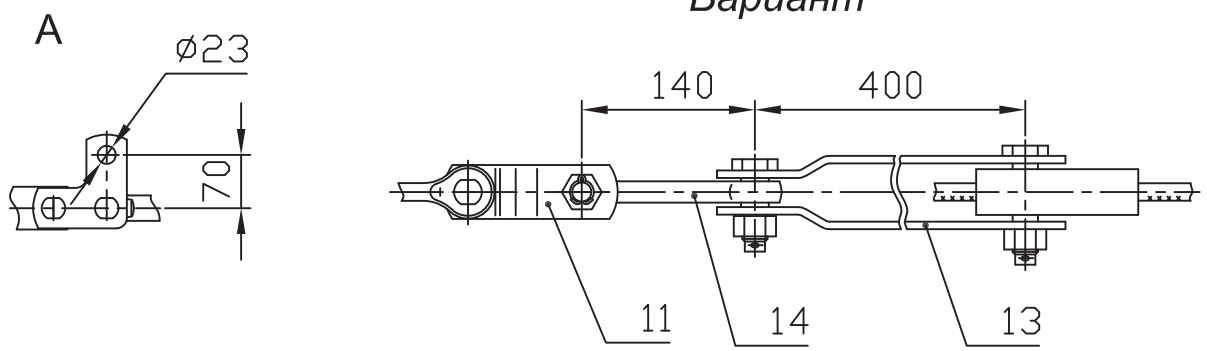

1. *При заказе натяжного клинового зажима типа НК-300-1 (поз.13) следует указывать марку провода. В спецификацию добавляется ПРВ-12-1 (поз.14).*

2. ** Масса указана с зажимом НАС-330-1Б и изолятором ЛК 120/220-3-СП.*


Провод по ГОСТ 839-80		Зажим, поз.12			Масса армат., кг
Марка	Диаметр, мм	Обозначение	L, мм	Масса, кг	
АС240/32	21,6	НАС-240-1Б	160	1,63	48,9
АС240/39		НАС-240-2Б		1,60	48,9
АС300/56	22,4	НАС-330-1Б	175	1,99	49,3
АС300/39	24,0				
АС300/48	24,1				
АС330/43	25,2				


Поз.	Обозначение	Наименование	Кол.	Масса ед. кг	Прим.
1	КГН-16-5	Узел крепления	2	5,23	
2	СК-16-1А	Скоба	2	1,22	
3	ПТР-12-1	Талреп	2	5,67	
4	СК-120-1Б	Скоба	2	0,92	
5	ПР-12-6	Звено прямое	2	0,94	
6	ПТМ-12-3А	Звено монтажное	2	1,7	
7	ЛК 120/220-	Изолятор СП ("А")	2	8,0	
8	УСК-12-16	Ушко специальное	2	2,07	
9	2КУ-30-1	Коромысло	1	8,46	
10	СК-21-1А	Скоба	1	1,82	
11	ПРТ-21/12-2	Звено переходное	1	1,5	
12	См. таблицу	Зажим натяжной	1	См. табл.	
13	НК-300-1	Зажим клиновой	1	5,1	
14	ПРВ-12-1	Звено вывернутое	1	0,43	
Масса арматуры, кг				см. табл.	
Масса изолирующей подвески, кг				65,3*	

		ЭСИП-0068	
		ЭСС.001 ТМ - т.1	
Утв.	Вигдергауз	Натяжные двухцепные изолирующие с полимерными изоляторами ряда 120 кН подвески проводов АС240/32 - АС330/43 к а/у металлическим опорам ВЛ 220 кВ	Стадия: Р; Лист: ; Листов: 1
Пров.	Липунцов		Филиал ОАО "ФСК ЕЭС" "Электросетьсервис"
Разраб.	Власкина		

Взам. инв. N | Подп. и дата | Инв. N подл.

Формат А3

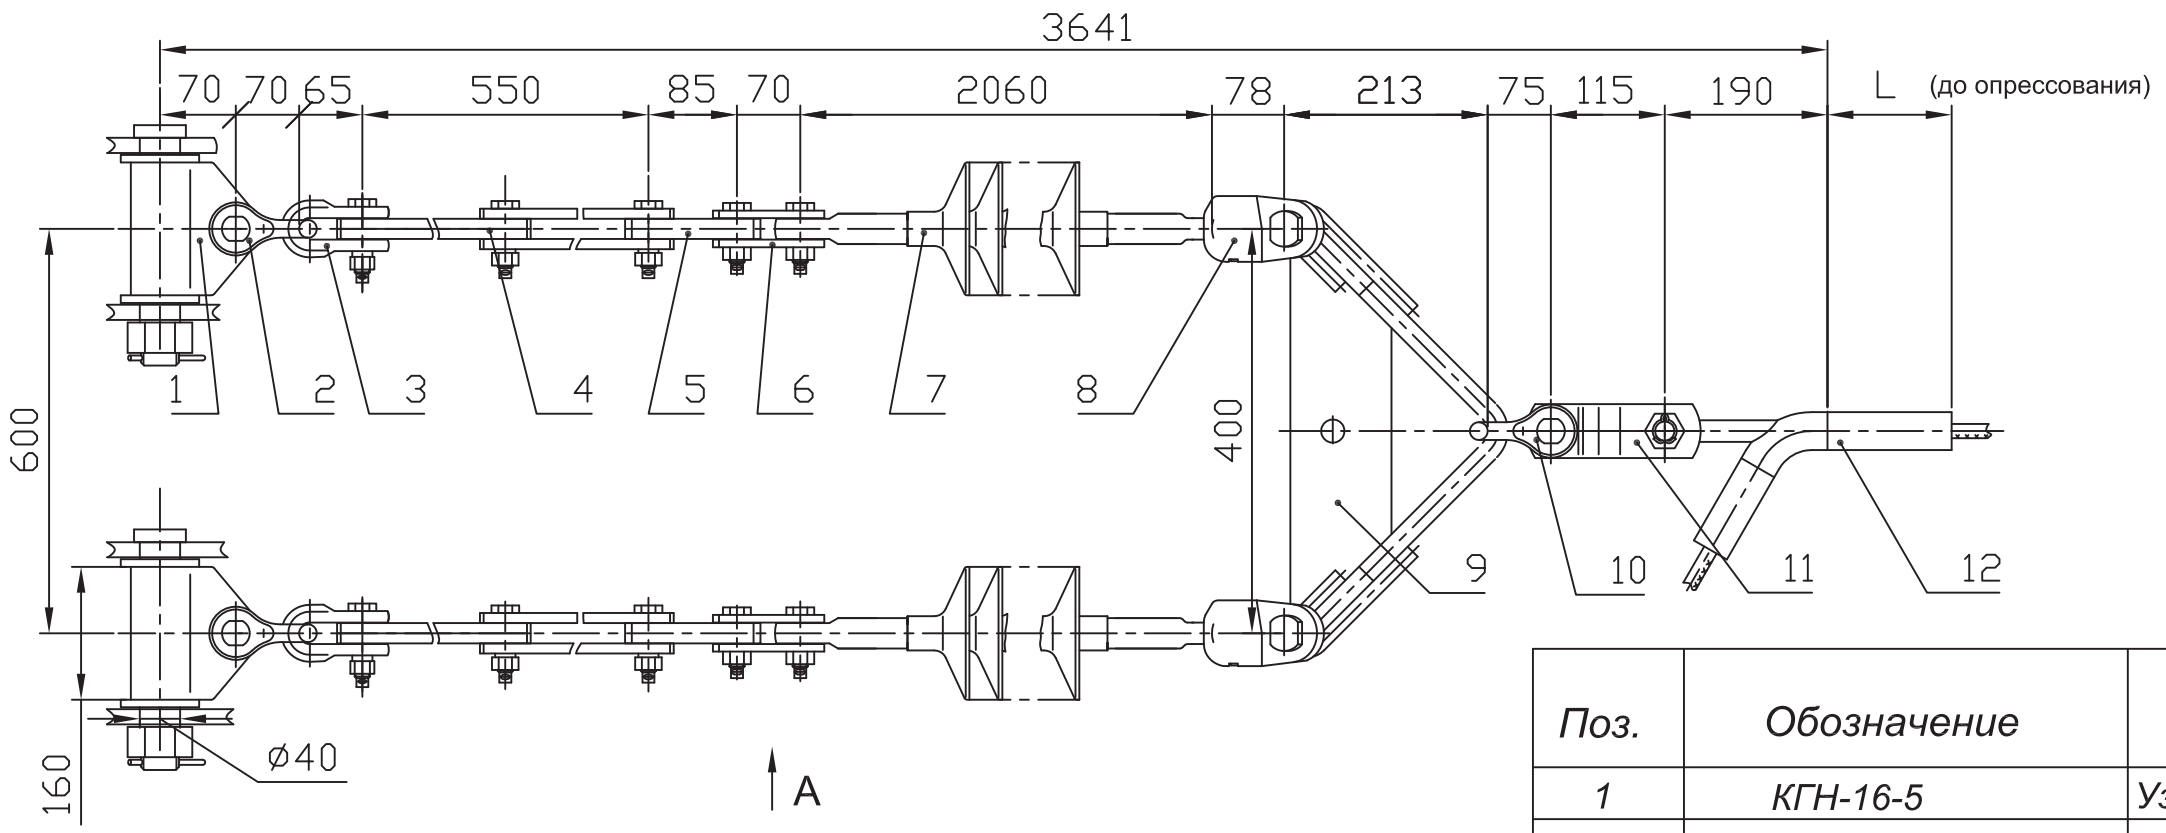

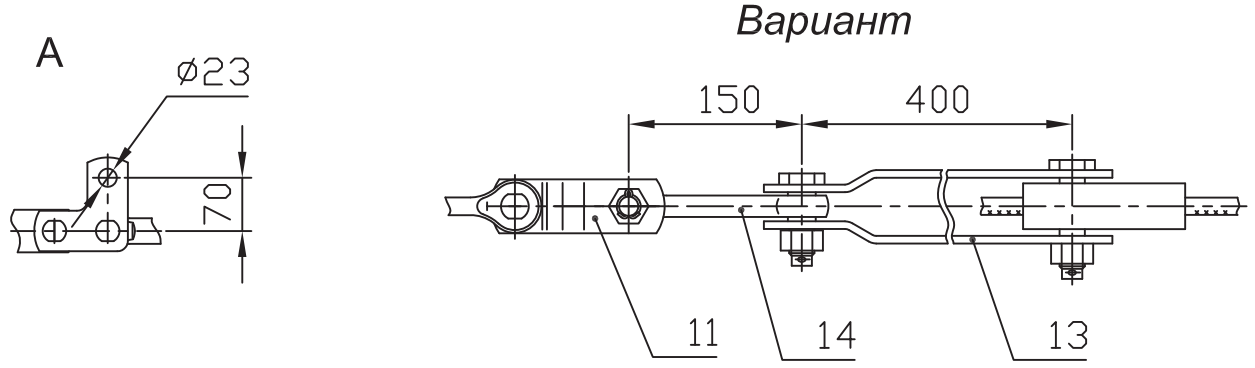

1. *При заказе натяжного клинового зажима типа НК-400-1 (поз.13) следует указывать марку провода. В спецификацию добавляется ПРВ-16-1 (поз.14).*

2. ** Масса указана с зажимом НАС-450-1Б и изолятором ЛК 120/220-3-СП.*


Провод по ГОСТ 839-80		Зажим, поз.12			Масса армат., кг
Марка	Диаметр, мм	Обозначение	L, мм	Масса, кг	
АС300/67	24,5	НАС-300-1Б	165	2,41	46,0
АС400/51	27,5	НАС-450-1Б	210	2,78	46,4

Поз.	Обозначение	Наименование	Кол.	Масса ед. кг	Прим.
1	КГН-16-5	Узел крепления	2	5,23	
2	СК-16-1А	Скоба	2	1,22	
3	СК-120-1Б	Скоба	2	0,92	
4	ПРР-12-1	Звено регулируемое	2	3,69	
5	ПР-12-6	Звено прямое	2	0,94	
6	ПТМ-12-3А	Звено монтажное	2	1,7	
7	ЛК 120/220-	Изолятор исп. СП	2	8,0	
8	УСК-12-16	Ушко специальное	2	2,07	
9	2КУ-30-1	Коромысло	1	8,46	
10	СК-21-1А	Скоба	1	1,82	
11	ПРТ-21/16-2	Звено переходное	1	1,8	
12	См. таблицу	Зажим натяжной	1	См. табл.	
13	НК-400-1	Зажим клиновой	1	5,2	
14	ПРВ-16-1	Звено вывернутое	1	0,91	
Масса арматуры, кг				см. табл.	
Масса изолирующей подвески, кг				62,4*	


Утв.	Вигдергауз	ЭСИП-0069	
		ЭСС.001 ТМ - т.1	
Пров.	Липунцов	Натяжные двухцепные изолирующие с полимерными изоляторами ряда 120 кН подвески проводов АС300/67, АС400/51 к а/у металлическим опорам ВЛ 220 кВ	Стадия: Р; Лист: ; Листов: 1
Разраб.	Власкина		Филиал ОАО "ФСК ЕЭС" "Электросетьсервис"

Взам. инв. N | Подп. и дата | Инв. N подл.

Формат А3

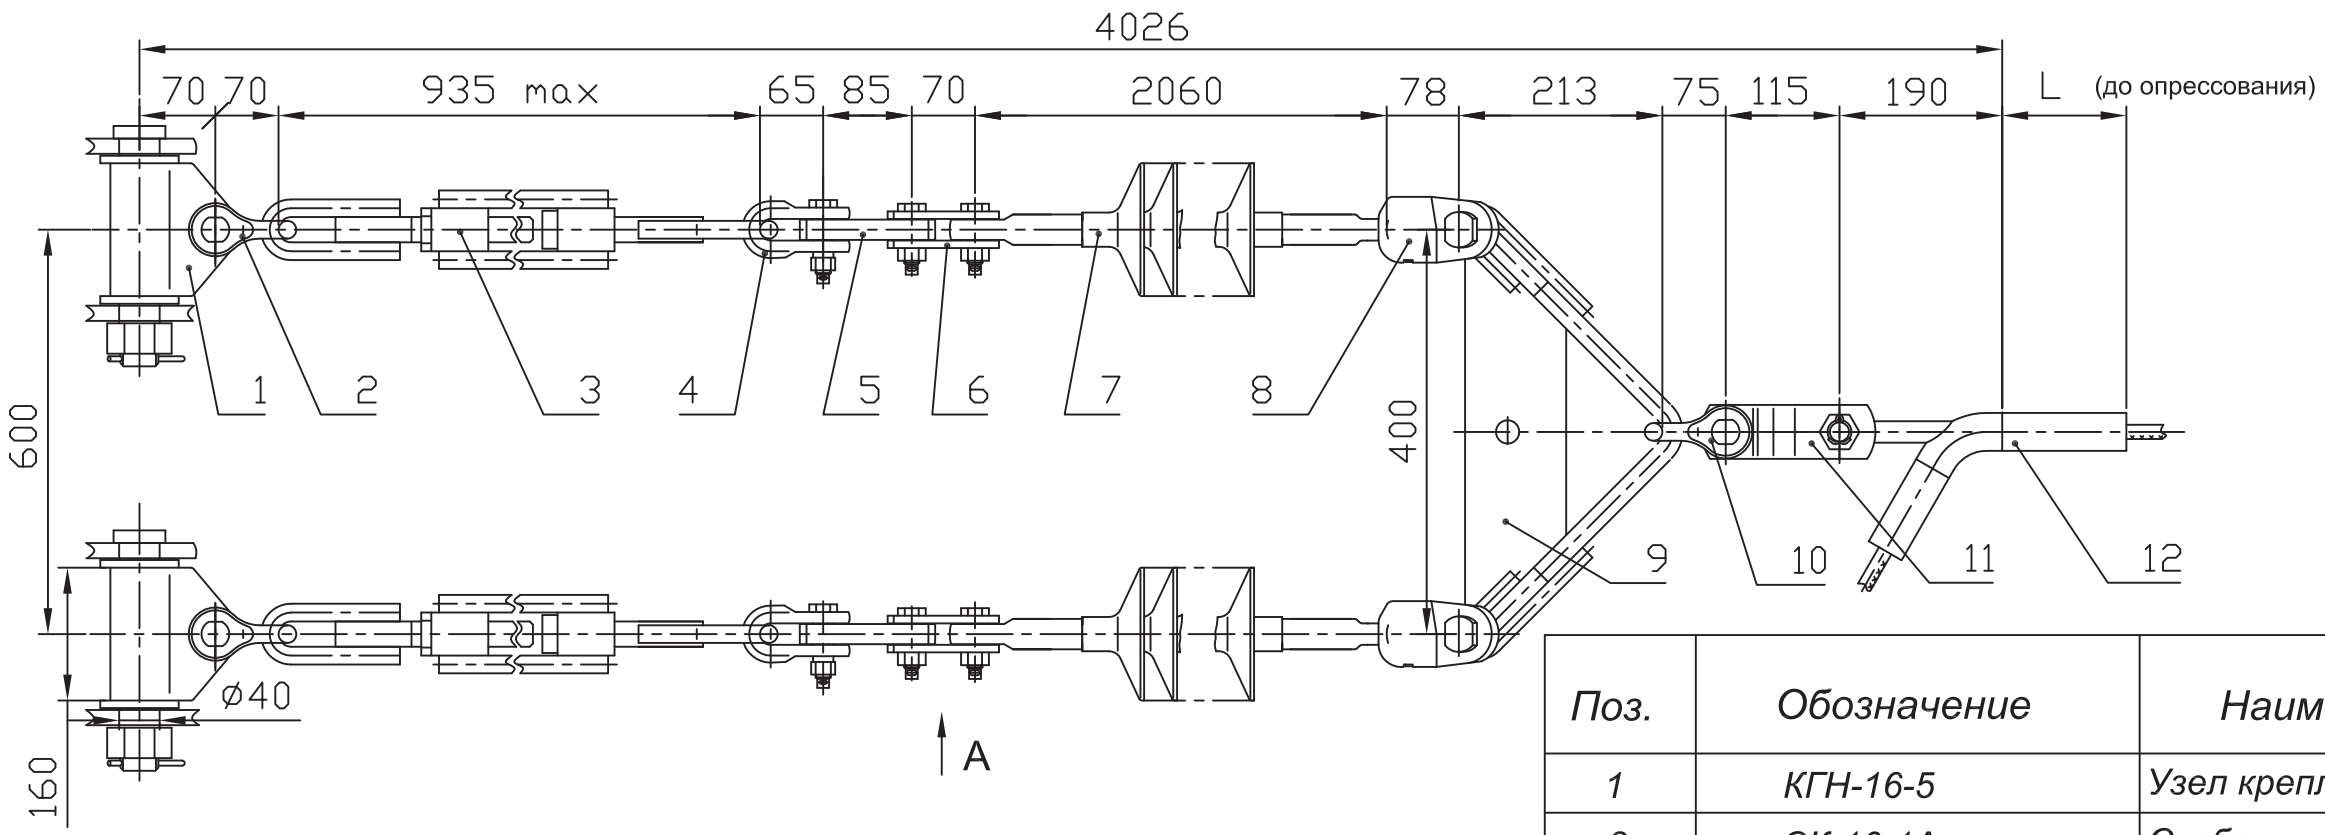

Вариант

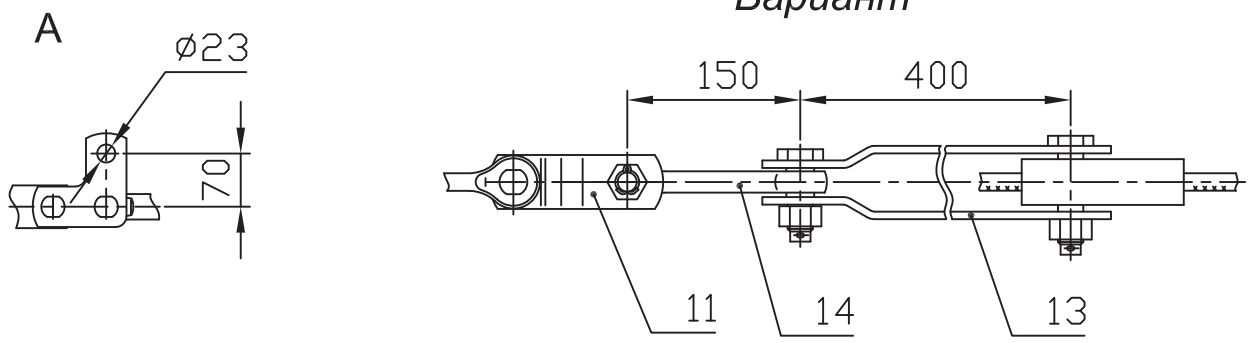

1. *При заказе натяжного клинового зажима типа НК-400-1 (поз.13) следует указывать марку провода. В спецификацию добавляется ПРВ-16-1 (поз.14).*

2. ** Масса указана с зажимом НАС-450-1Б и изолятором ЛК 120/220-3-СП.*

Провод по ГОСТ 839-80		Зажим, поз.12			Масса армат., кг
Марка	Диаметр, мм	Обозначение	L, мм	Масса, кг	
АС300/67	24,5	НАС-300-1Б	165	2,41	50,0
АС400/51	27,5	НАС-450-1Б	210	2,78	50,4

Поз.	Обозначение	Наименование	Кол.	Масса ед. кг	Прим.
1	КГН-16-5	Узел крепления	2	5,23	
2	СК-16-1А	Скоба	2	1,22	
3	ПТР-12-1	Талреп	2	5,67	
4	СК-120-1Б	Скоба	2	0,92	
5	ПР-12-6	Звено прямое	2	0,94	
6	ПТМ-12-3А	Звено монтажное	2	1,7	
7	ЛК 120/220-	Изолятор исп. СП	2	8,0	
8	УСК-12-16	Ушко специальное	2	2,07	
9	2КУ-30-1	Коромысло	1	8,46	
10	СК-21-1А	Скоба	1	1,82	
11	ПРТ-21/16-2	Звено переходное	1	1,8	
12	См. таблицу	Зажим натяжной	1	См. табл.	
13	НК-400-1	Зажим клиновой	1	5,2	
14	ПРВ-16-1	Звено вывернутое	1	0,91	
Масса арматуры, кг				см. табл.	
Масса изолирующей подвески, кг				66,4*	

ЭСИП-0070

ЭСС.001 ТМ - т.1

Утв.	Вигдергауз		
Пров.	Липунцов		
Разраб.	Власкина		


Натяжные двухцепные изолирующие с полимерными изоляторами ряда 120 кН подвески проводов АС300/67, АС400/51 к а/у металлическим опорам ВЛ 220 кВ

Стадия	Лист	Листов
Р		1


Филиал ОАО "ФСК ЕЭС" "Электросетьсервис"

Взам. инв. N | Подп. и дата | Инв. N подл.

Формат А3

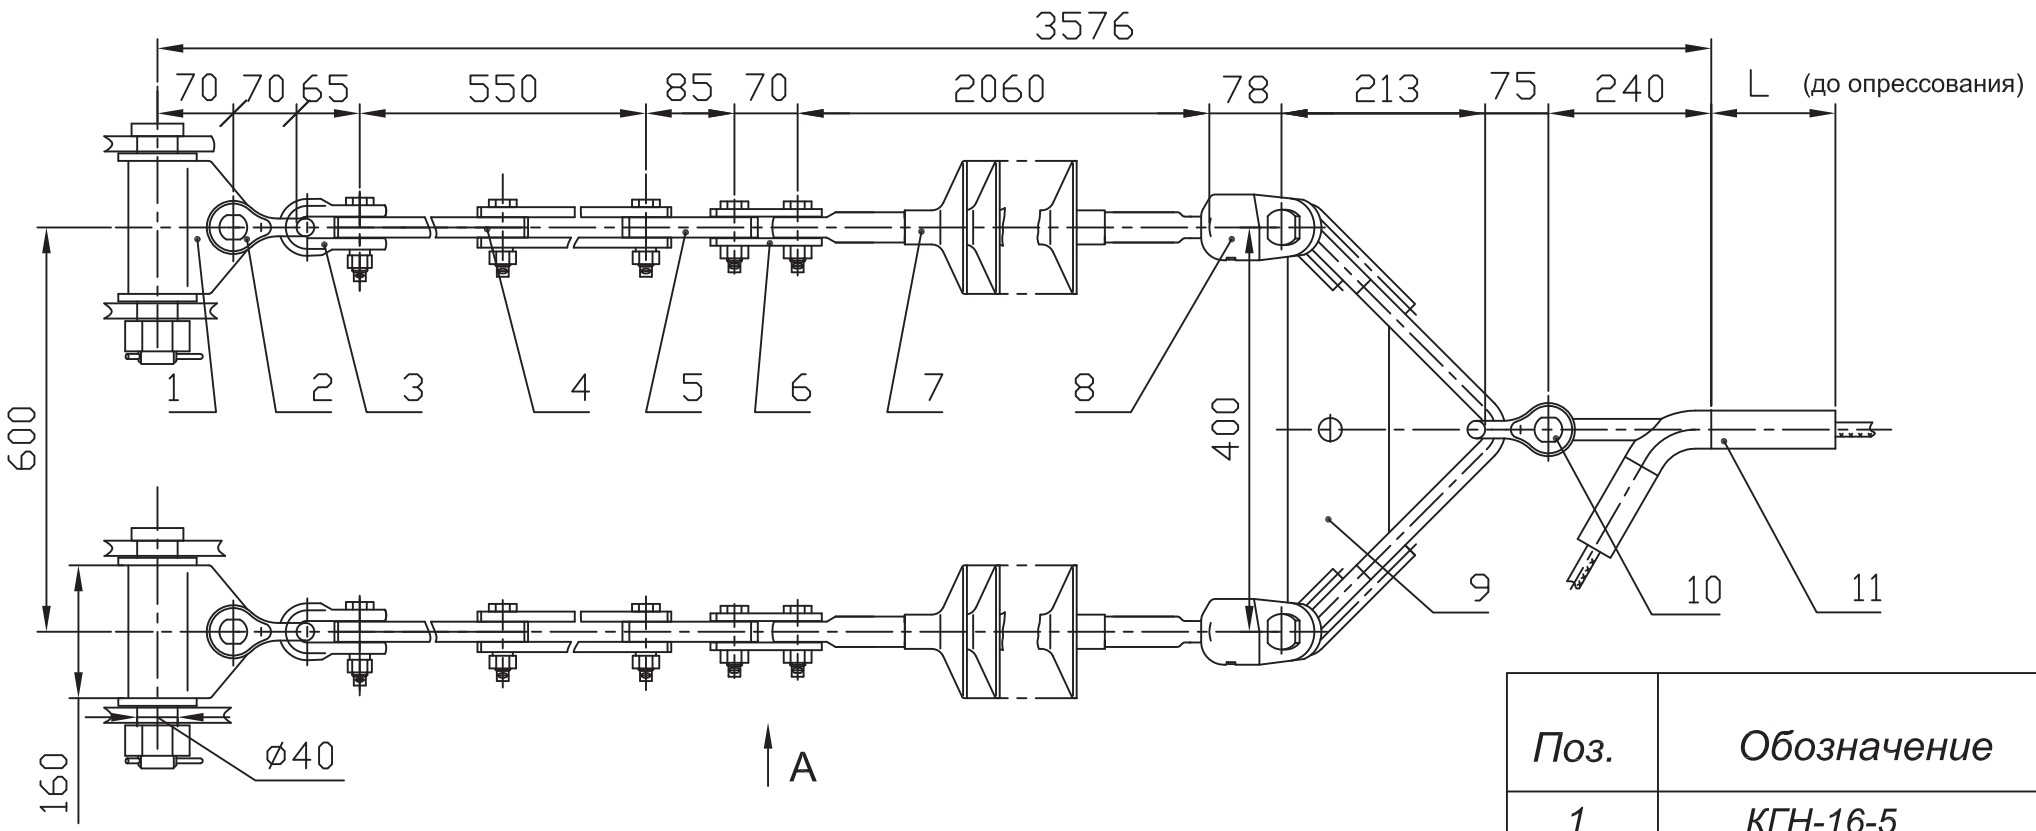

Вариант

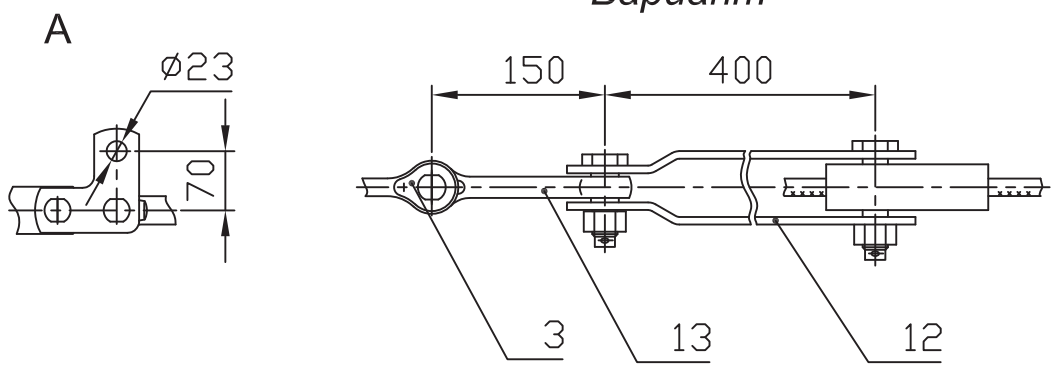

1. При заказе натяжного клинового зажима типа НК-500-1 (поз.12)следует указывать марку провода. В спецификацию добавляется ПРВ-21-1 (поз.13).

*2. * Масса указана с зажимом НАС-450-1Б и изолятором ЛК 120/220-3-СП.*

Провод по ГОСТ 839-80		Зажим, поз.11			Масса армат., кг
Марка	Диаметр, мм	Обозначение	L, мм	Масса, кг	
АС400/93	29,1	НАС-600-2Б	225	3,99	45,8
АС500/64	30,6	НАС-600-1Б	240	4,65	46,5

Поз.	Обозначение	Наименование	Кол.	Масса ед. кг	Прим.
1	КГН-16-5	Узел крепления	2	5,23	
2	СК-16-1А	Скоба	2	1,22	
3	СК-120-1Б	Скоба	2	0,92	
4	ПРР-12-1	Звено регулируемое	2	3,69	
5	ПР-12-6	Звено прямое	2	0,94	
6	ПТМ-12-3А	Звено монтажное	2	1,7	
7		Изолятор исп. СП	2	8,0	
8	УСК-12-16	Ушко специальное	2	2,07	
9	2КУ-30-1	Коромысло	1	8,46	
10	СК-21-1А	Скоба	1	1,82	
11	См. таблицу	Зажим натяжной	1	См. табл.	
12	НК-500-1	Зажим клиновой	1	5,3	
13	ПРВ-21-1	Звено вывернутое	1	1,3	
Масса арматуры, кг				см. табл.	
Масса изолирующей подвески, кг				62,5*	


ЭСИП-0071

ЭСС.001 ТМ - т.1


Утв.	Вигдергауз	Натяжные двухцепные изолирующие с полимерными изоляторами ряда 120 кН подвески проводов АС400/93, АС500/64 к а/у металлическим опорам ВЛ 220 кВ	Стадия: Р; Лист: ; Листов: 1
Пров.	Липунцов		Филиал ОАО "ФСК ЕЭС" "Электросетьсервис"
Разраб.	Власкина		

Взам. инв. N | Подп. и дата | Инв. N подл.

Формат А3

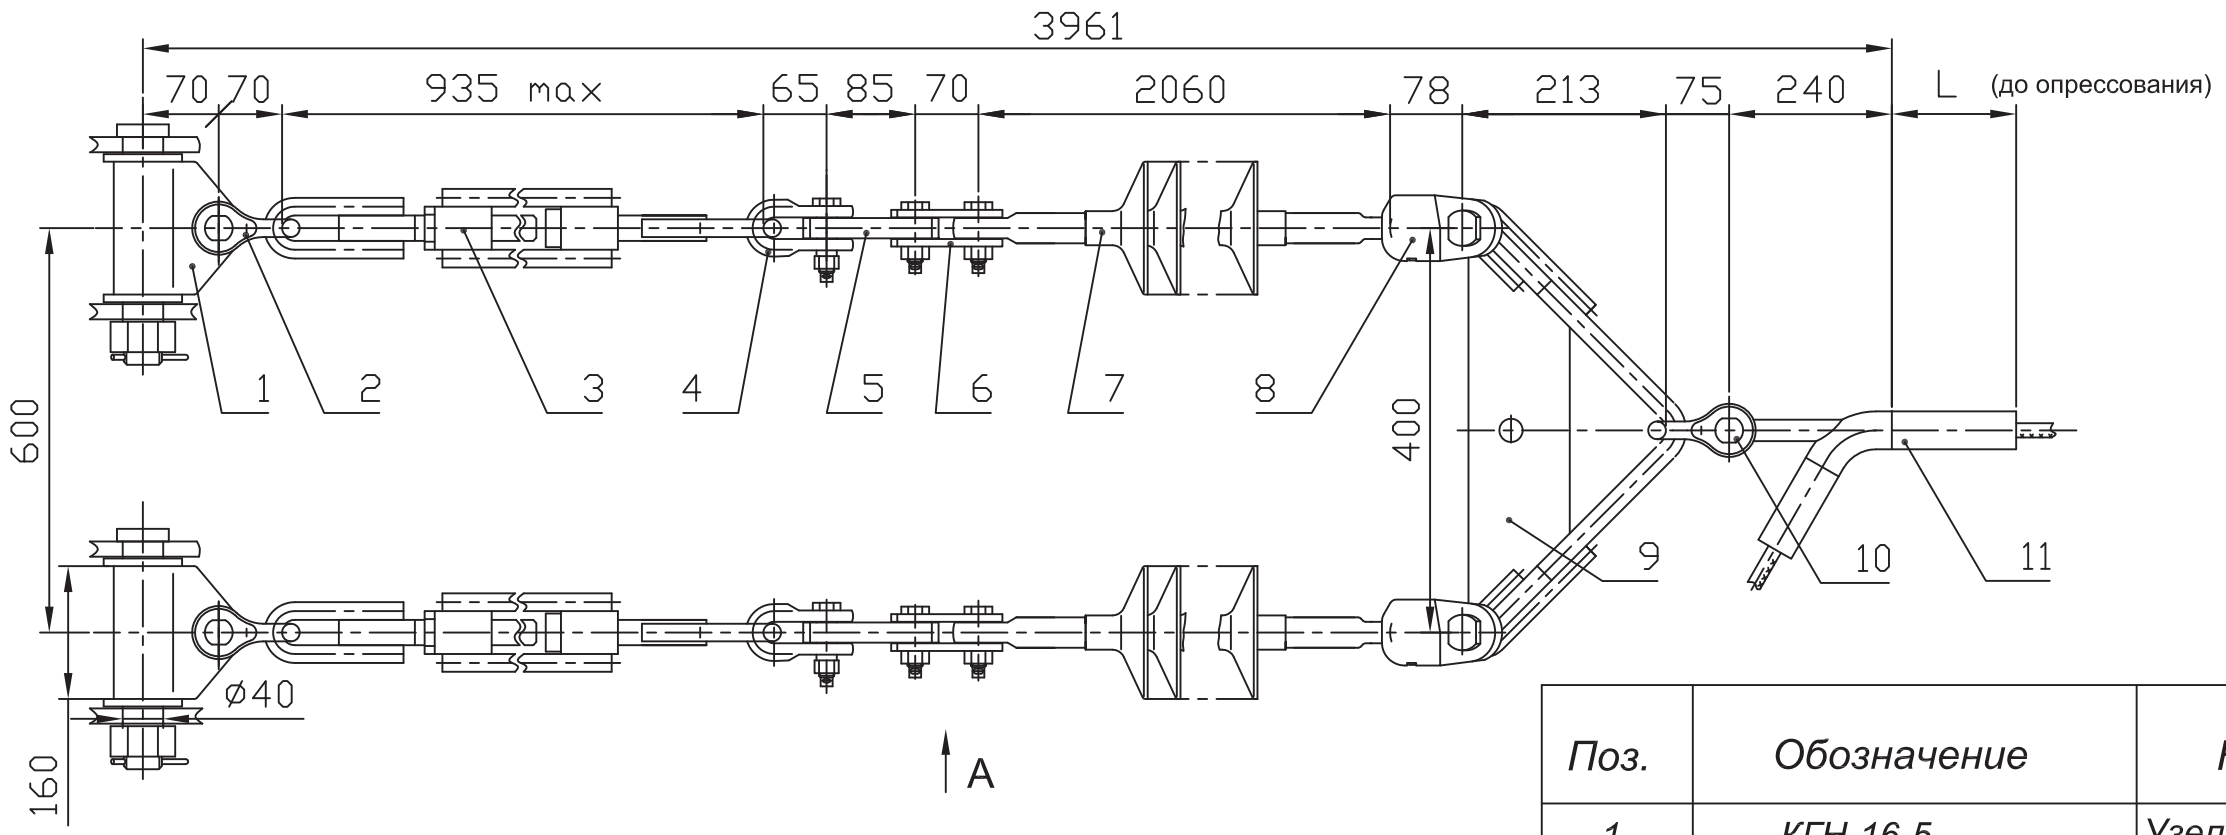

Вариант

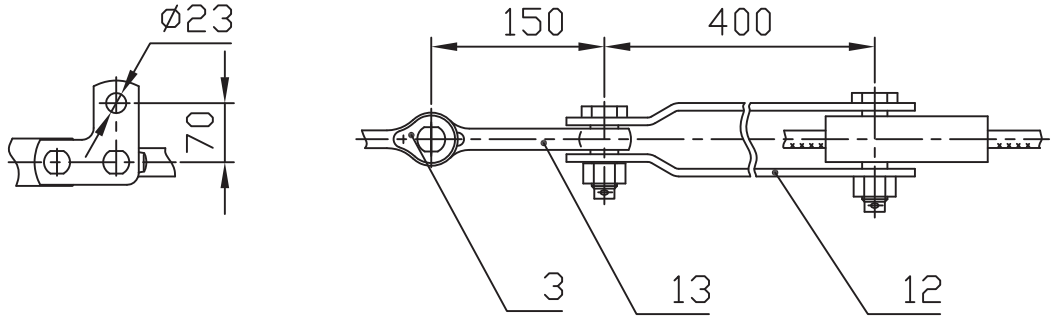

1. При заказе натяжного клинового зажима типа НК-500-1 (поз.12)следует указывать марку провода. В спецификацию добавляется ПРВ-21-1 (поз.13).

*2. * Масса указана с зажимом НАС-450-1Б и изолятором ЛК 120/220-3-СП.*


Провод по ГОСТ 839-80		Зажим, поз.11			Масса армат., кг
Марка	Диаметр, мм	Обозначение	L, мм	Масса, кг	
АС400/93	29,1	НАС-600-2Б	225	3,99	54,7
АС500/64	30,6	НАС-600-1Б	240	4,65	55,4

Поз.	Обозначение	Наименование	Кол.	Масса ед. кг	Прим.
1	КГН-16-5	Узел крепления	2	5,23	
2	СК-16-1А	Скоба	2	1,22	
3	ПТР-12-1	Талреп	2	5,67	
4	СК-120-1Б	Скоба	2	0,92	
5	ПР-12-6	Звено прямое	2	0,94	
6	ПТМ-12-3А	Звено монтажное	2	1,7	
7		Изолятор исп. СП	2	8,0	
8	УСК-12-16	Ушко специальное	2	2,07	
9	2КУ-30-1	Коромысло	1	8,46	
10	СК-21-1А	Скоба	1	1,82	
11	См. таблицу	Зажим натяжной	1	См. табл.	
12	НК-500-1	Зажим клиновой	1	5,3	
13	ПРВ-21-1	Звено вывернутое	1	1,3	
Масса арматуры, кг				см. табл.	
Масса изолирующей подвески, кг				71,4*	

		ЭСИП-0072	
		ЭСС.001 ТМ - т.1	
Утв.	Вигдергауз	Натяжные двухцепные изолирующие с полимерными изоляторами ряда 120 кН подвески проводов АС400/93, АС500/64 к а/у металлическим опорам ВЛ 220 кВ	Стадия: Р; Лист: ; Листов: 1
Пров.	Липунцов		Филиал ОАО "ФСК ЕЭС" "Электросетьсервис"
Разраб.	Власкина		

Взам. инв. N | Подп. и дата | Инв. N подл.

Формат А3

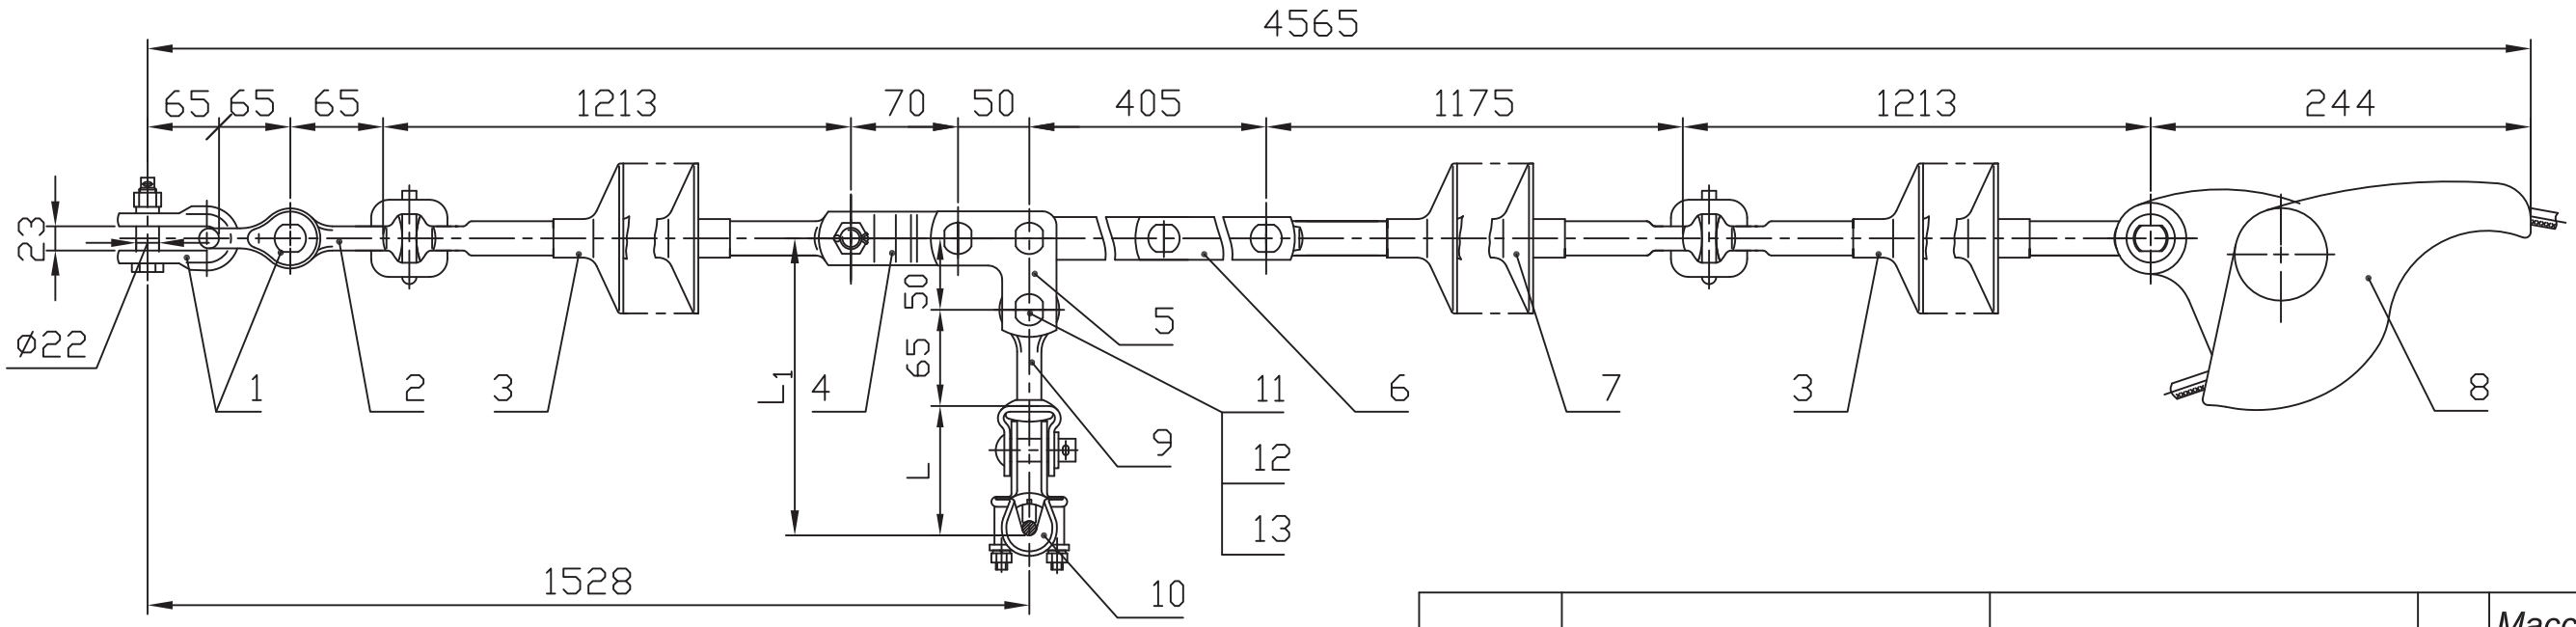

Поз.	Обозначение	Наименование	Кол.	Масса ед. кг	Прим.
1	СК-120-1Б	Скоба	2	0,92	
2	СР-12-16	Серьга	1	0,41	
3	ЛК 70/110-	Изолятор исп. ГС	2	3,5	
4	ПРТ-7-1	Звено трехлапчатое	1	0,46	
5	ПТМ-7-3А	Звено монтажное	1	0,63	
6	ПРР-7-1	Звено регулируемое	1	1,91	
7	ЛК 70/110-	Изолятор исп. СП	1	3,5	
8	НЗ-60/11-17	Зажим заклинивающий	1	1,5	
9	СР-7-16	Серьга	1	0,3	
10	См. талблицу	Зажим поддерживающ.	1	См. табл.	
11	СТП 2700000-92	Палец 16 х 50	1	0,078	
12	ГОСТ 5915-70	Гайка М12-7Н.4.0112	1	0,015	
13	ГОСТ 397-79	Шплинт 4х28.0112	1	0,003	
Масса арматуры, кг				см.табл.	
Масса изолирующей подвески, кг				19,0*	

Провод по ГОСТ 839-80		Зажим, поз.10			L1, мм	Масса армат., кг
Марка	Диаметр, мм	Обозначение	L, мм	Масса, кг		
АС70/11	11,4	ПГГ-25/6-12	93	1,21	208	8,3
АС95/16	13,5	ПГГ-30/12-20	103	1,35	218	8,5
АС120/19	15,2					
АС150/24	17,1					

* Масса арматуры указана с зажимом ПГГ-30/12-20 (поз.10)

Утв.	Вигдергауз		
Пров.	Липунцов		
Разраб.	Власкина		

ЭСИП-0073

ЭСС.001 ТМ - т.1

Натяжные транспозиционные одноцепные изолирующие с полимерными изоляторами ряда 70 кН подвески проводов АС70/11 - АС150/24 к а/у металлическим и деревянным опорам ВЛ 110 кВ

Стадия	Лист	Листов
Р		1


Филиал ОАО "ФСК ЕЭС" "Электросетьсервис"


Формат А3

Взам. инв. N

Подп. и дата

Инв. N подл.

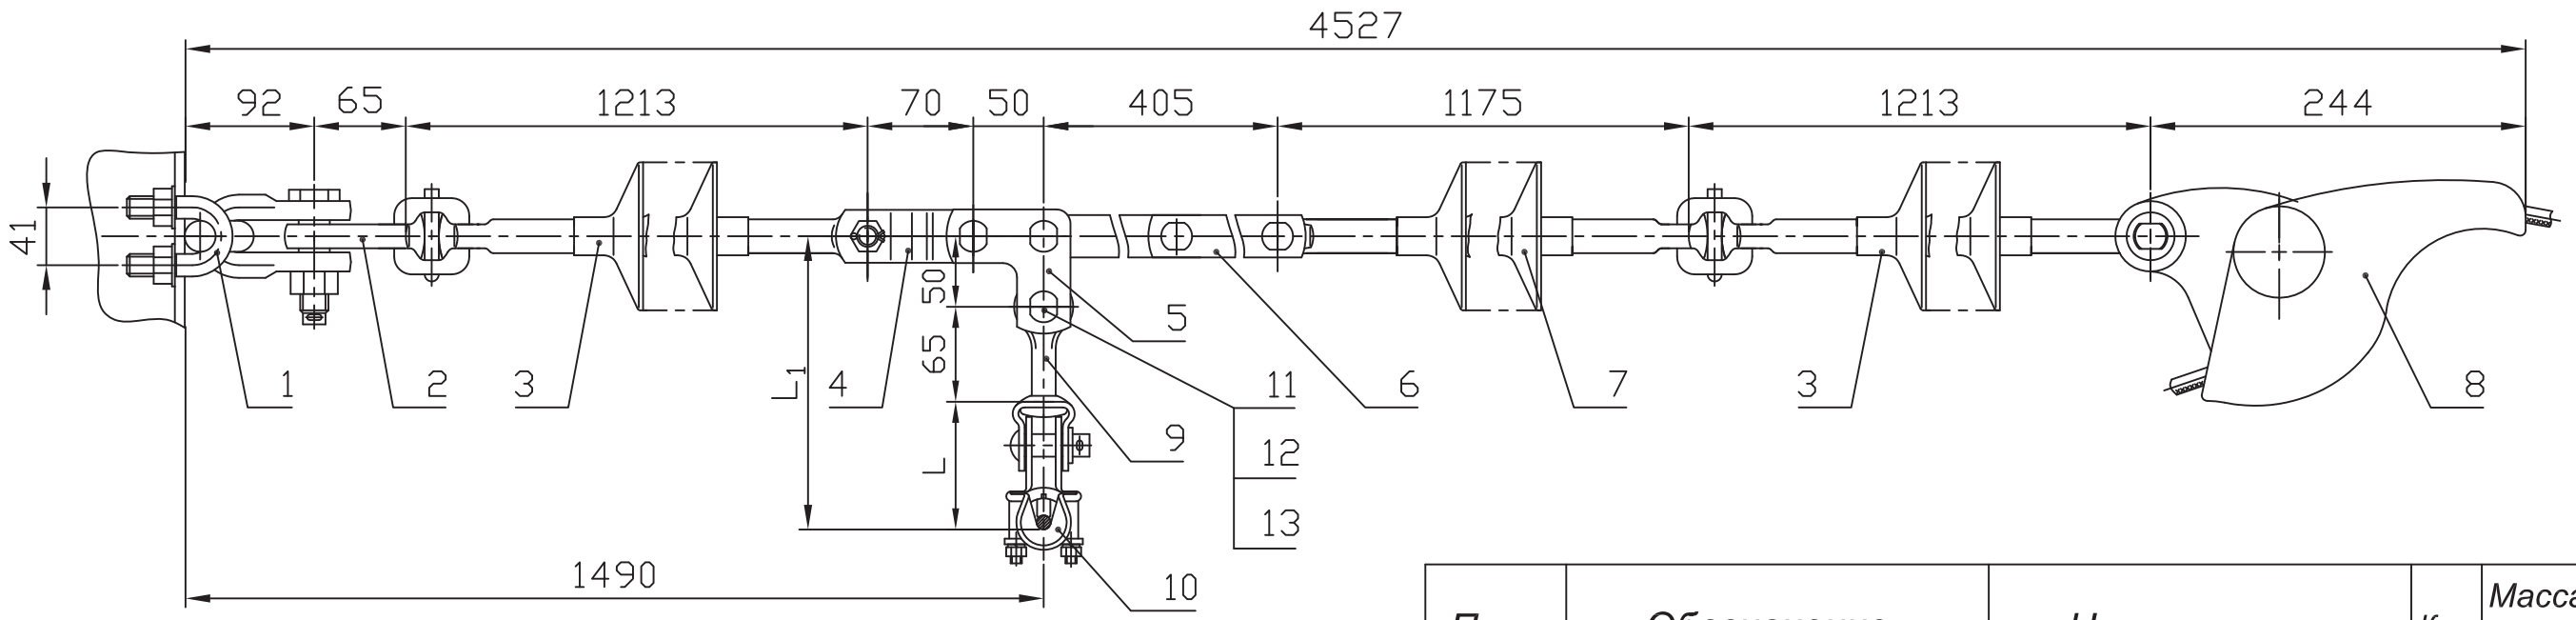

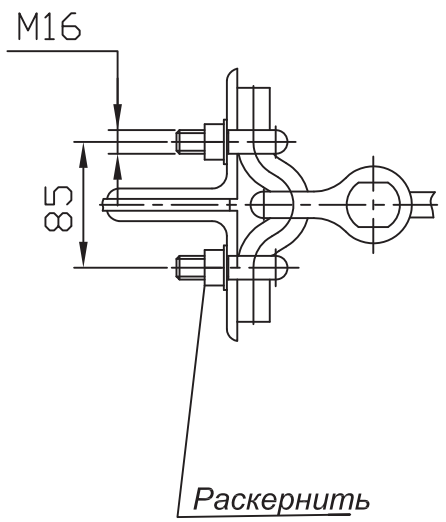

Провод по ГОСТ 839-80		Зажим, поз.10			L1, мм	Масса армат., кг
Марка	Диаметр, мм	Обозначение	L, мм	Масса, кг		
АС70/11	11,4	ПГГ-25/6-12	93	1,21	208	8,6
АС95/16	13,5	ПГГ-30/12-20	103	1,35	218	8,8
АС120/19	15,2					
АС150/24	17,1					

* Масса арматуры указана с зажимом ПГ-3-12У (поз.10)

Поз.	Обозначение	Наименование	Кол.	Масса ед. кг	Прим.
1	КГ-12-1	Узел крепления	1	2,15	
2	СР-12-16	Серьга	1	0,41	
3	ЛК 70/110-	Изолятор исп. ГС	2	3,5	
4	ПРТ-7-1	Звено трехлапчатое	1	0,46	
5	ПТМ-7-3А	Звено монтажное	1	0,63	
6	ПРР-7-1	Звено регулируемое	1	1,91	
7	ЛК 70/110-	Изолятор исп. СП	1	3,5	
8	НЗ-60/11-17	Зажим заклинивающий	1	1,5	
9	СР-7-16	Серьга	1	0,3	
10	См. талблицу	Зажим поддерживающ.	1	См. табл.	
11	СТП 2700000-92	Палец 16 х 50	1	0,078	
12	ГОСТ 5915-70	Гайка М12-7Н.4.0112	1	0,015	
13	ГОСТ 397-79	Шплинт 4х28.0112	1	0,003	
Масса арматуры, кг				см.табл.	
Масса изолирующей подвески, кг				19,4*	

			ЭСИП-0074
			ЭСС.001 ТМ - т.1
Утв.	Вигдергауз		Натяжные транспозиционные одноцепные изолирующие с полимерными изоляторами ряда 70 кН подвески проводов АС70/11 - АС150/24 к а/у металлическим опорам ВЛ 110 кВ
Пров.	Липунцов		
Разраб.	Власкина		

Стадия	Лист	Листов
Р		1


Филиал ОАО "ФСК ЕЭС" "Электросетьсервис"

Формат А3

Взам. инв. N

Подп. и дата

Инв. N подл.

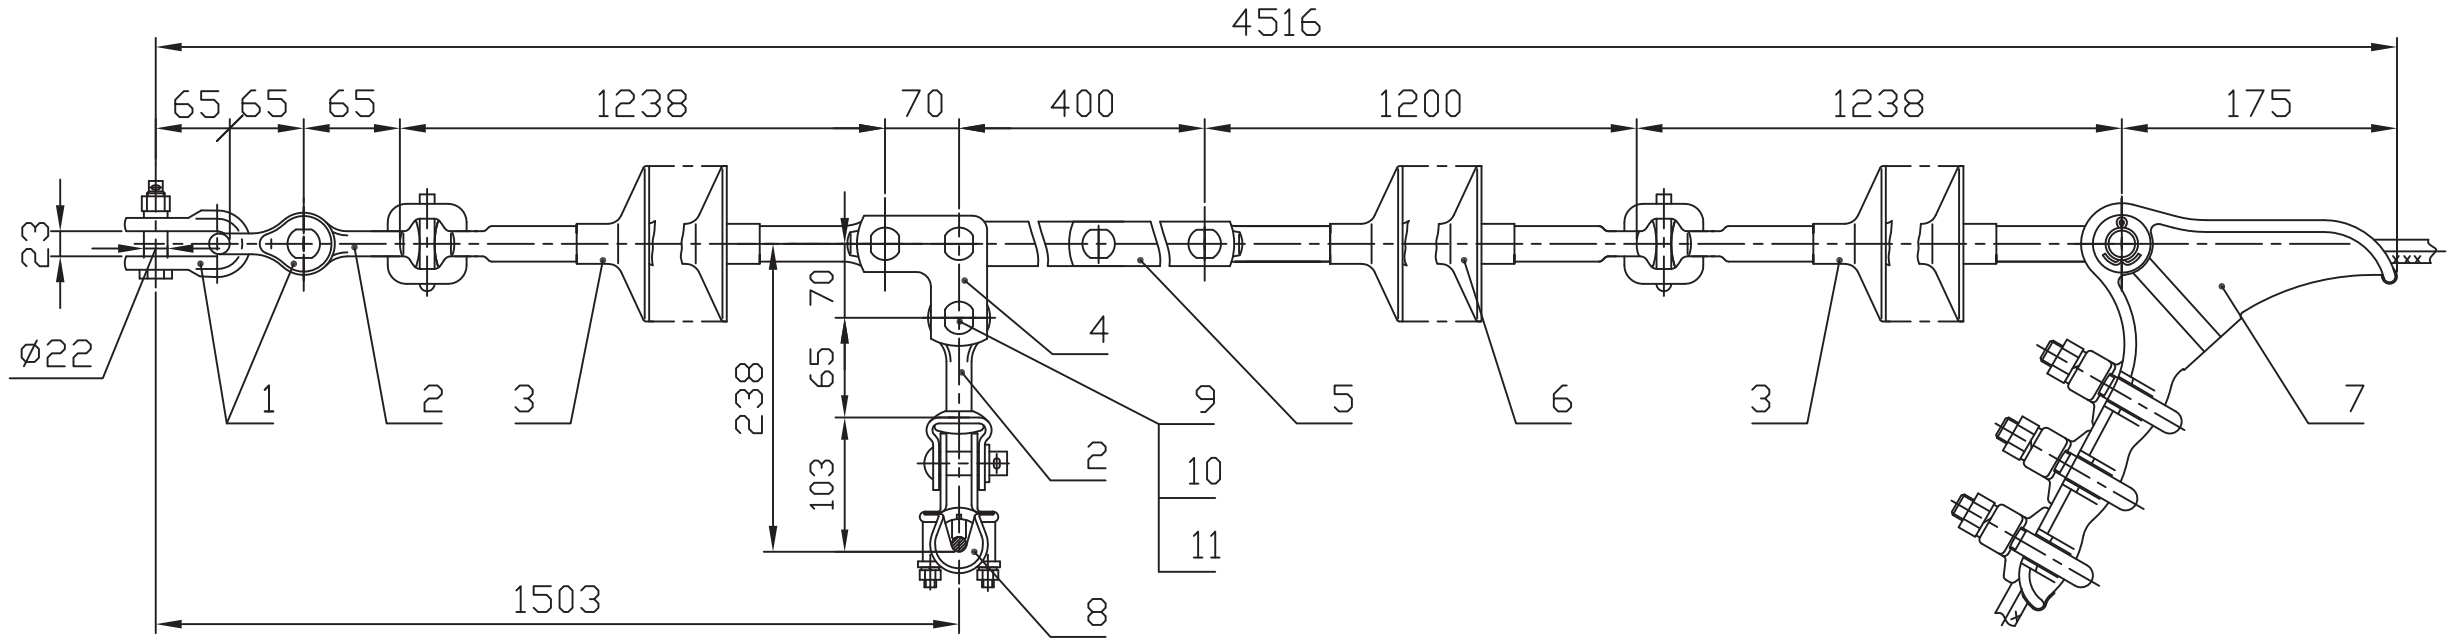

Поз.	Обозначение	Наименование	Кол.	Масса ед. кг	Прим.
1	СК-120-1Б	Скоба	2	0,92	
2	СР-12-16	Серьга	2	0,41	
3	ЛК 120/110-	Изолятор исп. ГС	2	4,0	
4	ПТМ-12-3А	Звено монтажное	1	1,7	
5	ПРР-12-1	Звено регулируемое	1	3,69	
6	ЛК 120/110-	Изолятор исп. СП	1	4,0	
7	НБ-90/15-22	Зажим натяжной	1	2,84	
8	ПГГ-30/12-20	Зажим поддерживающ.	1	1,35	
9	СТП 2700000-92	Палец 22 х 70	1	0,233	
10	ГОСТ 5915-70	Гайка М20-7Н.4.0112	1	0,064	
11	ГОСТ 397-79	Шплинт 4х28.0112	1	0,003	
Масса арматуры, кг				12,3	
Масса изолирующей подвески, кг				24,3*	

* Масса указана с изолятором ЛК 120/110-4

Взам. инв. N

Подп. и дата

Инв. N подл.

Утв.	Вигдергауз		
Пров.	Липунцов		
Разраб.	Власкина		

ЭСИП-0075


ЭСС.001 ТМ - т.1


Натяжные транспозиционные одноцепные изолирующие с полимерными изоляторами ряда 120 кН подвески проводов АС150/24 и АС185/29 к а/у металлическим и деревянным опорам ВЛ 110 кВ

Стадия	Лист	Листов
Р		1

Филиал ОАО "ФСК ЕЭС" "Электросетьсервис"

Формат А3

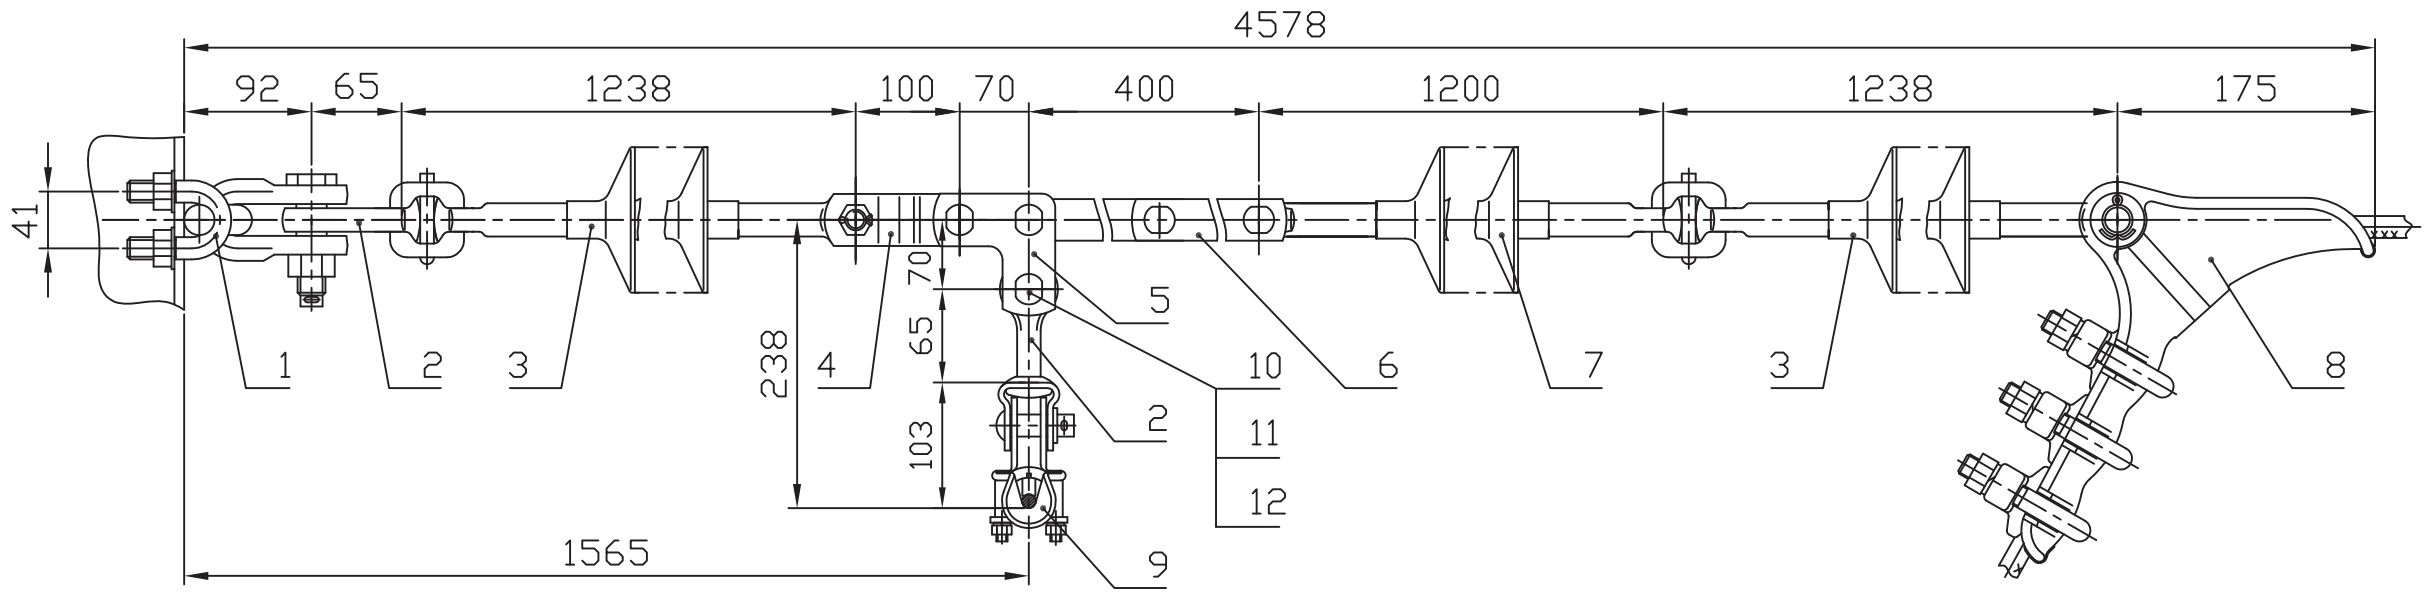

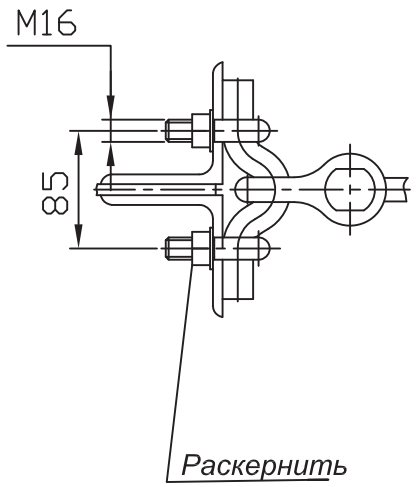

Поз.	Обозначение	Наименование	Кол.	Масса ед. кг	Прим.
1	КГ-12-1	Узел крепления	1	2,15	
2	СР-12-16	Серьга	2	0,41	
3	ЛК 120/110-	Изолятор исп. ГС	2	4,0	
4	ПРТ-12-1	Звено трехлапчатое	1	1,15	
5	ПТМ-12-3А	Звено монтажное	1	1,7	
6	ПРР-12-1	Звено регулируемое	1	3,69	
7	ЛК 120/110-	Изолятор исп. СП	1	4,0	
8	НБ-90/15-22	Зажим натяжной	1	2,84	
9	ПГГ-30/12-20	Зажим поддерживающ.	1	1,35	
10	СТП 2700000-92	Палец 22 х 70	1	0,233	
11	ГОСТ 5915-70	Гайка М20-7Н.4.0112	1	0,064	
12	ГОСТ 397-79	Шплинт 4 х 28.0112	1	0,003	
Масса арматуры, кг				13,8	
Масса изолирующей подвески, кг				25,8*	

* Масса указана с изолятором ЛК 120/110-4


Взам. инв. N

Подп. и дата

Инв. N подл.

				ЭСИП-0076	
				ЭСС.001 ТМ - т.1	
Утв.	Вигдергауз			Натяжные транспозиционные одноцепные изолирующие с полимерными изоляторами ряда 120 кН подвески проводов АС150/24 и АС185/29 к а/у металлическим опорам ВЛ 110 кВ	Стадия: Р; Лист: ; Листов: 1
Пров.	Липунцов				Филиал ОАО "ФСК ЕЭС" "Электросетьсервис"
Разраб.	Власкина				

Формат А3

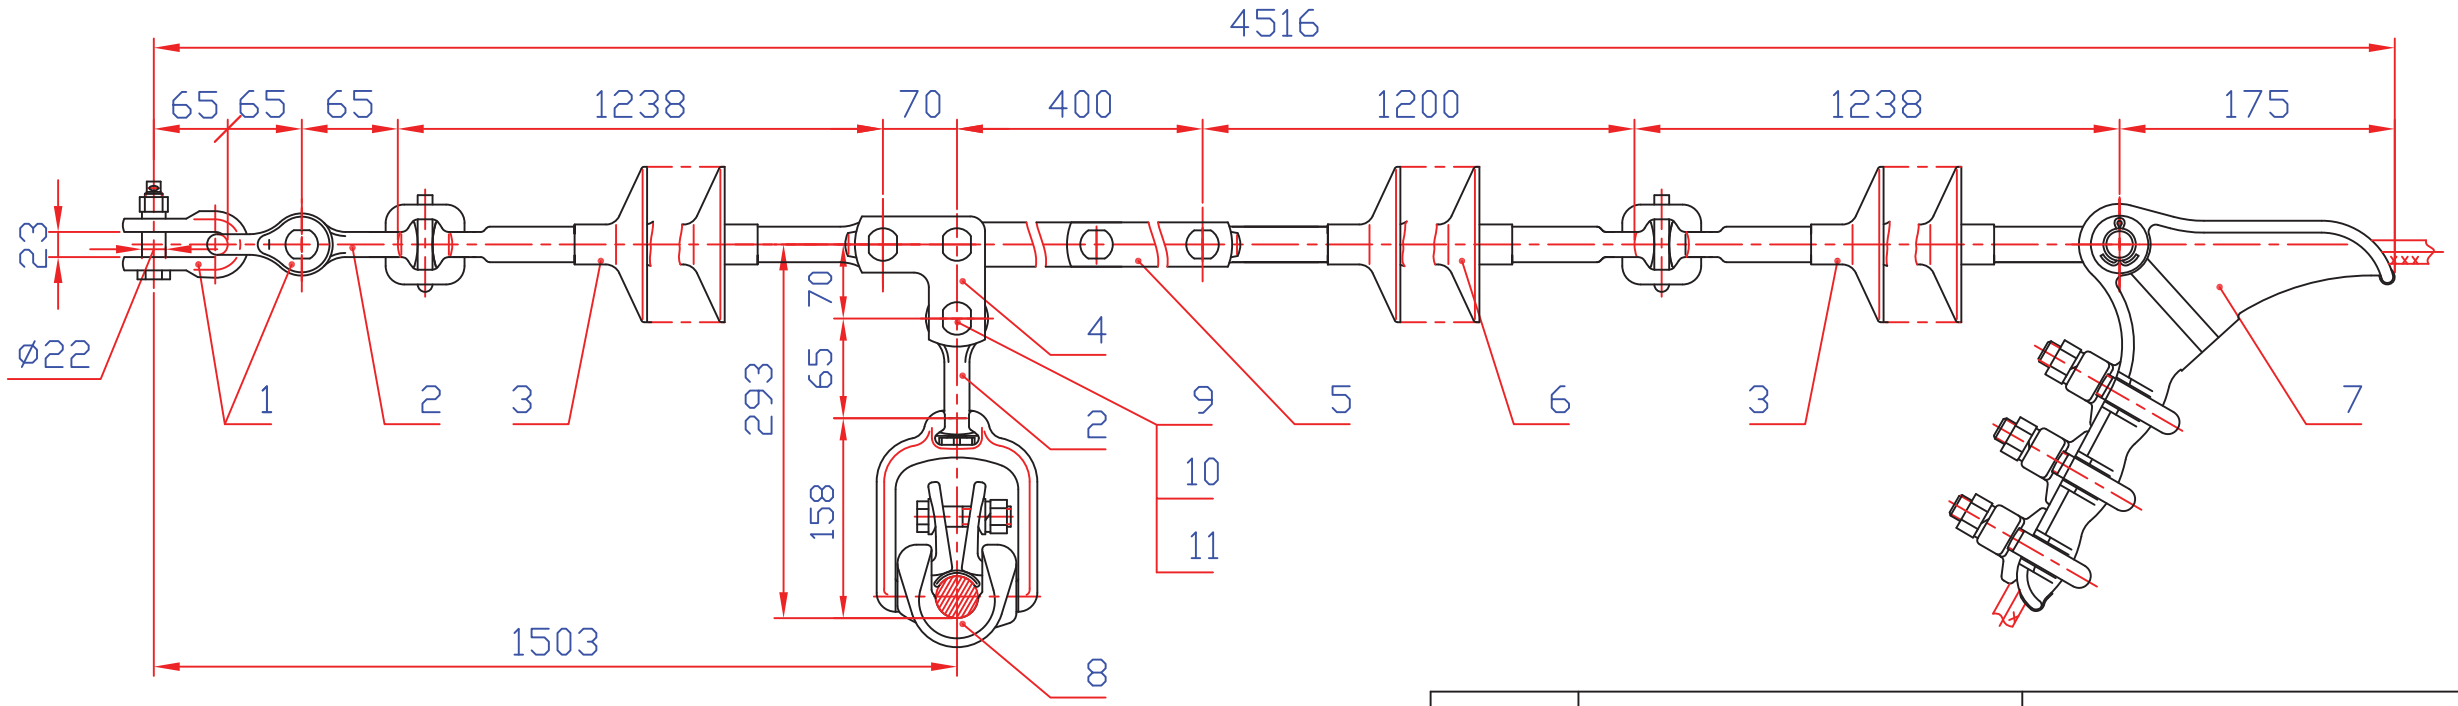

Поз.	Обозначение	Наименование	Кол.	Масса ед. кг	Прим.
1	СК-120-1Б	Скоба	2	0,92	
2	СР-12-16	Серьга	2	0,41	
3	ЛК 120/110-	Изолятор исп. ГС	2	4,0	
4	ПТМ-12-3А	Звено монтажное	1	1,7	
5	ПРР-12-1	Звено регулируемое	1	3,69	
6	ЛК 120/110-	Изолятор исп. СП	1	4,0	
7	НБ-90/15-22	Зажим натяжной	1	2,84	
8	ПГН-5-3	Зажим поддерживающ.	1	5,3	
9	СТП 2700000-92	Палец 22 х 70	1	0,233	
10	ГОСТ 5915-70	Гайка М20-7Н.4.0112	1	0,064	
11	ГОСТ 397-79	Шплинт 4х28.0112	1	0,003	
Масса арматуры, кг				16,5	
Масса изолирующей подвески, кг				28,5*	

* Масса указана с изолятором ЛК 120/110-4

Взам. инв. N

Подп. и дата


Инв. N подл.


			ЭСИП-0077
			ЭСС.001 ТМ - т.1
Утв.	Вигдергауз		Натяжные транспозиционные одноцепные изолирующие с полимерными изоляторами ряда 120 кН подвески проводов АС240/32, АС240/39 к а/у металлическим и деревянным опорам ВЛ 110 кВ
Пров.	Липунцов		
Разраб.	Власкина		

Стадия	Лист	Листов
Р		1

Филиал ОАО "ФСК ЕЭС" "Электросетьсервис"

Формат А3

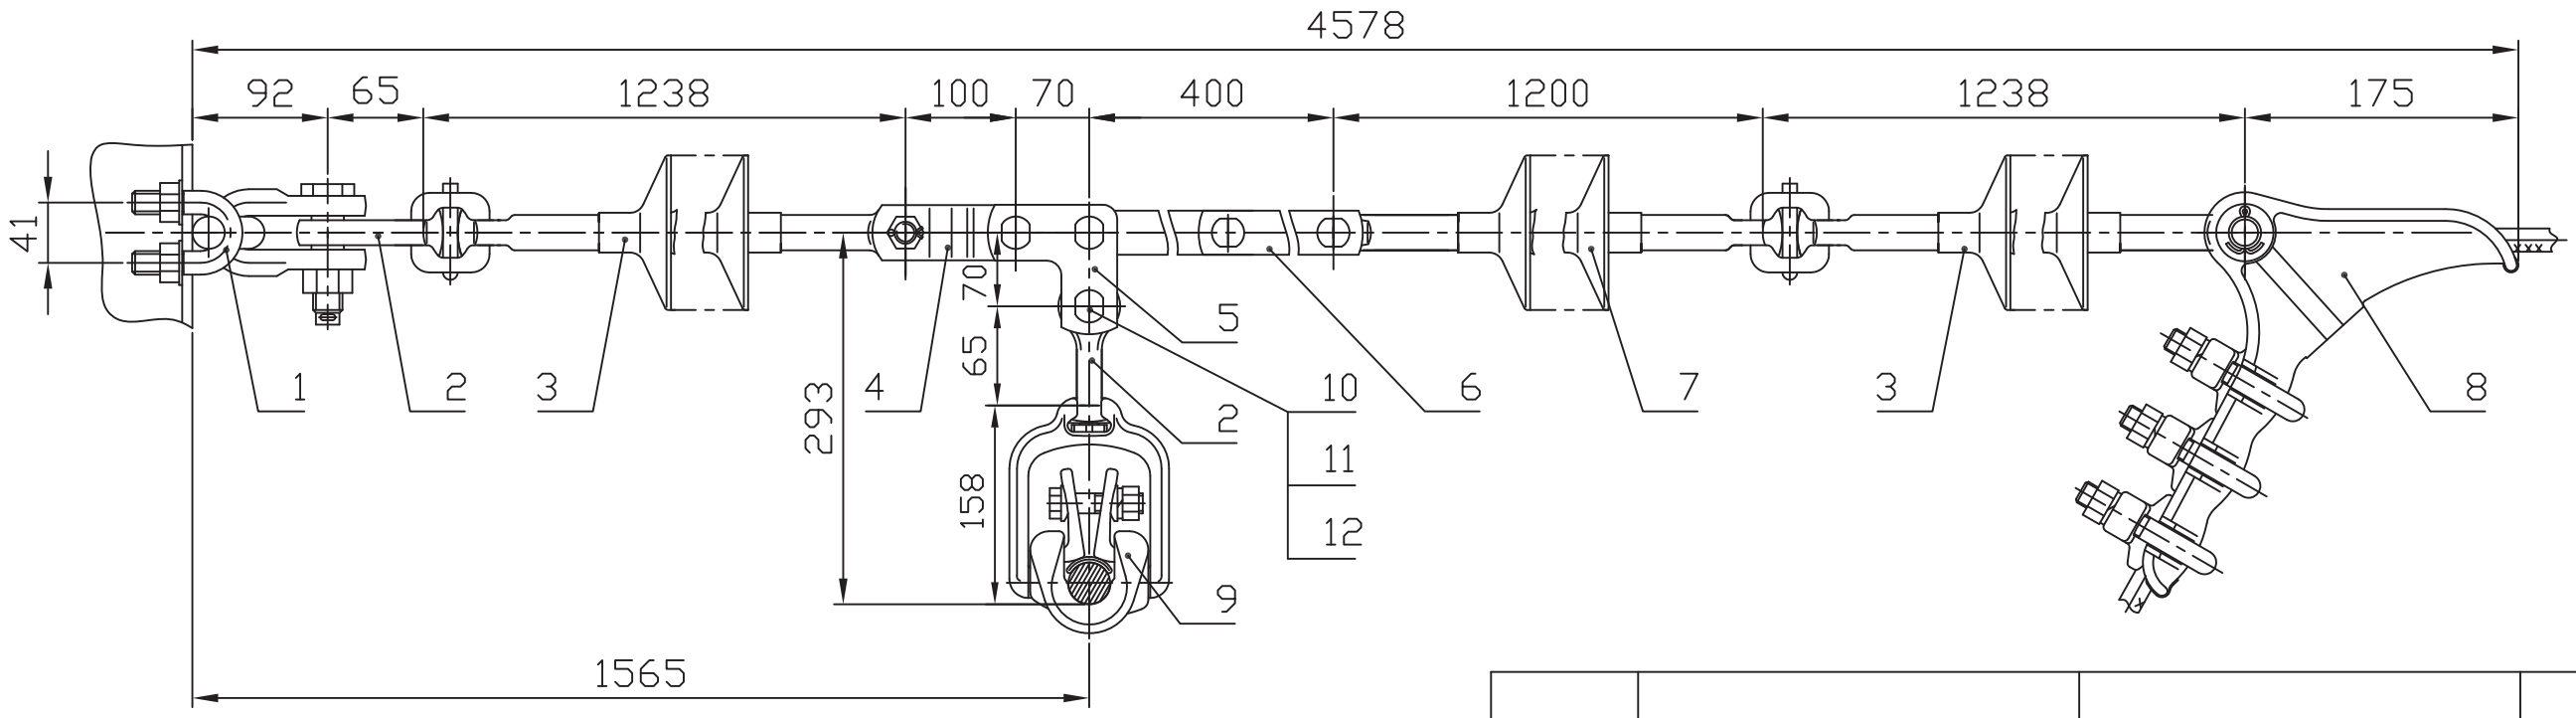

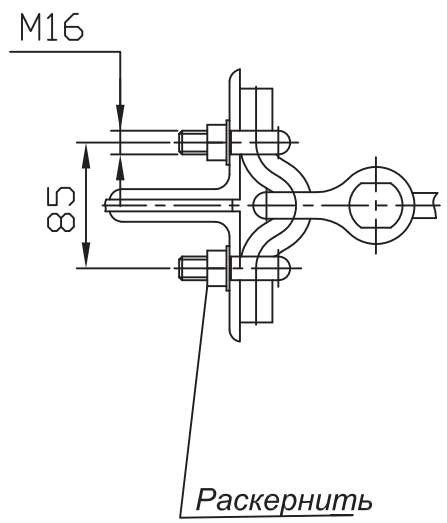

Поз.	Обозначение	Наименование	Кол.	Масса ед. кг	Прим.
1	КГ-12-1	Узел крепления	1	2,15	
2	СР-12-16	Серьга	2	0,41	
3	ЛК 120/110-	Изолятор исп. ГС	2	4,0	
4	ПРТ-12-1	Звено трехлапчатое	1	1,15	
5	ПТМ-12-3А	Звено монтажное	1	1,7	
6	ПРР-12-1	Звено регулируемое	1	3,69	
7	ЛК 120/110-	Изолятор исп. СП	1	4,0	
8	НБ-90/15-22	Зажим натяжной	1	2,84	
9	ПГН-5-3	Зажим поддерживающ.	1	5,3	
10	СТП 2700000-92	Палец 22 х 70	1	0,233	
11	ГОСТ 5915-70	Гайка М20-7Н.4.0112	1	0,064	
12	ГОСТ 397-79	Шплинт 4 х 28.0112	1	0,003	
Масса арматуры, кг				18,4	
Масса изолирующей подвески, кг				30,4*	

* Масса указана с изолятором ЛК 120/110-4


Взам. инв. N

Подп. и дата

Инв. N подл.

				ЭСИП-0078		
				ЭСС.001 ТМ - т.1		
Утв.	Вигдергауз			Натяжные транспозиционные одноцепные изолирующие с полимерными изоляторами ряда 120 кН подвески проводов АС150/24 и АС185/29 к а/у металлическим опорам ВЛ 110 кВ	Стадия	Лист	Листов
					Р		1
Пров.	Липунцов				Филиал ОАО "ФСК ЕЭС" "Электросетьсервис"		
Разраб.	Власкина						

Формат А3

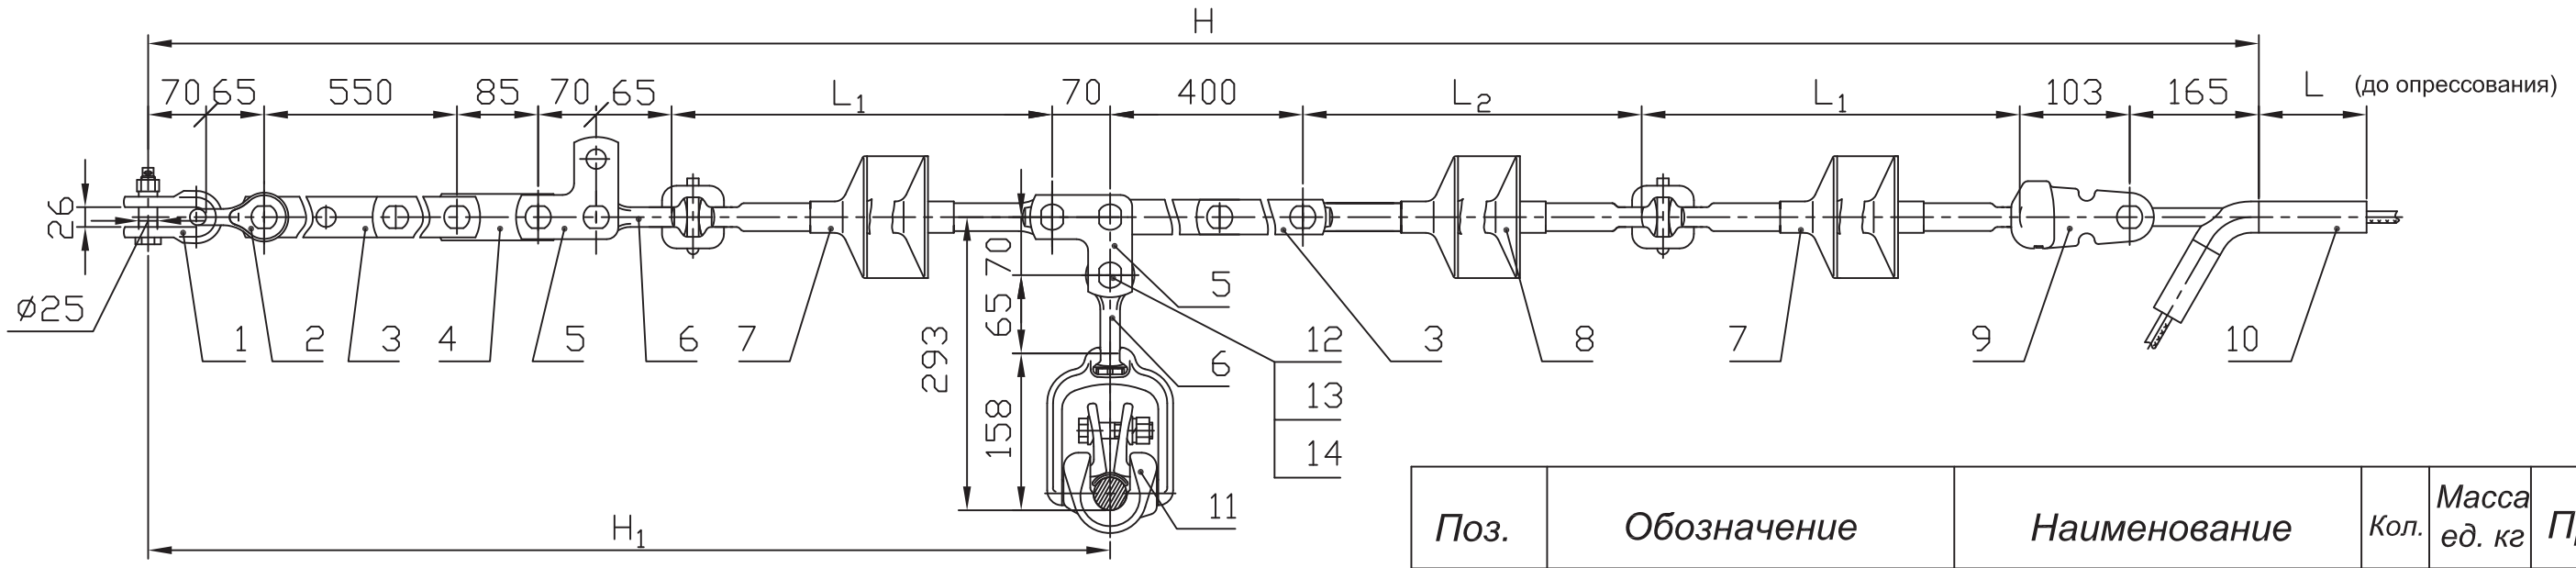

Вариант

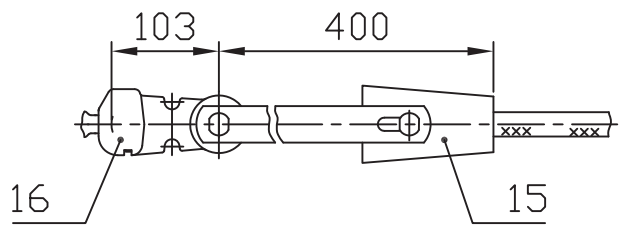


Таблица 1

Напряжение ВЛ, кВ	Провод по ГОСТ 839-80		Зажим, поз.10			Масса армат., кг
	Марка	Диаметр, мм	Обозначение	L, мм	Масса, кг	
110	АС240/32	21,6	НАС-240-1Б	160	1,63	23,4
	АС240/39		НАС-240-2Б		1,60	23,4
220	АС240/56	22,4	НАС-330-1Б	175	1,99	23,8
	АС300/39	24,0				
	АС300/48	24,1				

Таблица 2 *Размеры в мм*

Напряжение ВЛ, кВ	Изолятор поз.7		Изолятор поз.8		Изолирующая подвеска		
	L_1	Масса, кг	L_2	Масса, кг	H	H_1	Масса, кг
110	1238	4,0	1200	4,0	5319	2213	35,8*
220	2070	8,0	2060	8,0	7843	3045	47,8*

1. *При заказе натяжного клинового зажима типа НК-300-1 (поз.15)следует указывать марку провода. Ушко У2-12-16 (поз.9) заменить на У1-12-16 (поз.16).*

2. ** Масса указана с зажимом НАС-330-1Б .*

Поз.	Обозначение	Наименование	Кол.	Масса ед. кг	Прим.
1	СК-16-1А	Скоба	1	1,22	
2	СК-120-1Б	Скоба	1	0,92	
3	ПРР-12-1	Звено регулируемое	2	3,69	
4	ПР-12-6	Звено прямое	1	0,94	
5	ПТМ-12-3А	Звено монтажное	2	1,7	
6	СР-12-16	Серьга	2	0,41	
7		Изолятор исп. ГС	2	См. табл.2	
8		Изолятор исп. СП	1	См. табл.2	
9	У2-12-16	Ушко двухлапчатое	1	1,54	
10	См. таблицу	Зажим натяжной	1	См. табл.1	
11	ПГН-5-3	Зажим поддерживающ.	1	5,3	
12	СТП 2700000-92	Палец 22 х 70	1	0,233	
13	ГОСТ 5915-70	Гайка М20-7Н.4.0112	1	0,064	
14	ГОСТ 397-79	Шплинт 4х28.0112	1	0,003	
15	НК-300-1	Зажим клиновой	1	5,1	
16	У1-12-16	Ушко однолапчатое	1	1,05	
Масса арматуры, кг					См. табл. 1
Масса изолирующей подвески, кг					См. табл. 2

ЭСИП-0079

ЭСС.001 ТМ - т.1

Утв.	Вигдергауз		
Пров.	Липунцов		
Разраб.	Власкина		

Натяжные транспозиционные одноцепные изолирующие с полимерными изоляторами ряда 120 кН подвески проводов АС240/32 - АС300/48 к а/у ж/б опорам ВЛ 220 кВ и деревянным опорам ВЛ 110, 220 кВ

Стадия	Лист	Листов
Р		1


Филиал ОАО "ФСК ЕЭС" "Электросетьсервис"

Формат А3

Взам. инв. N

Подп. и дата

Инв. N подл.

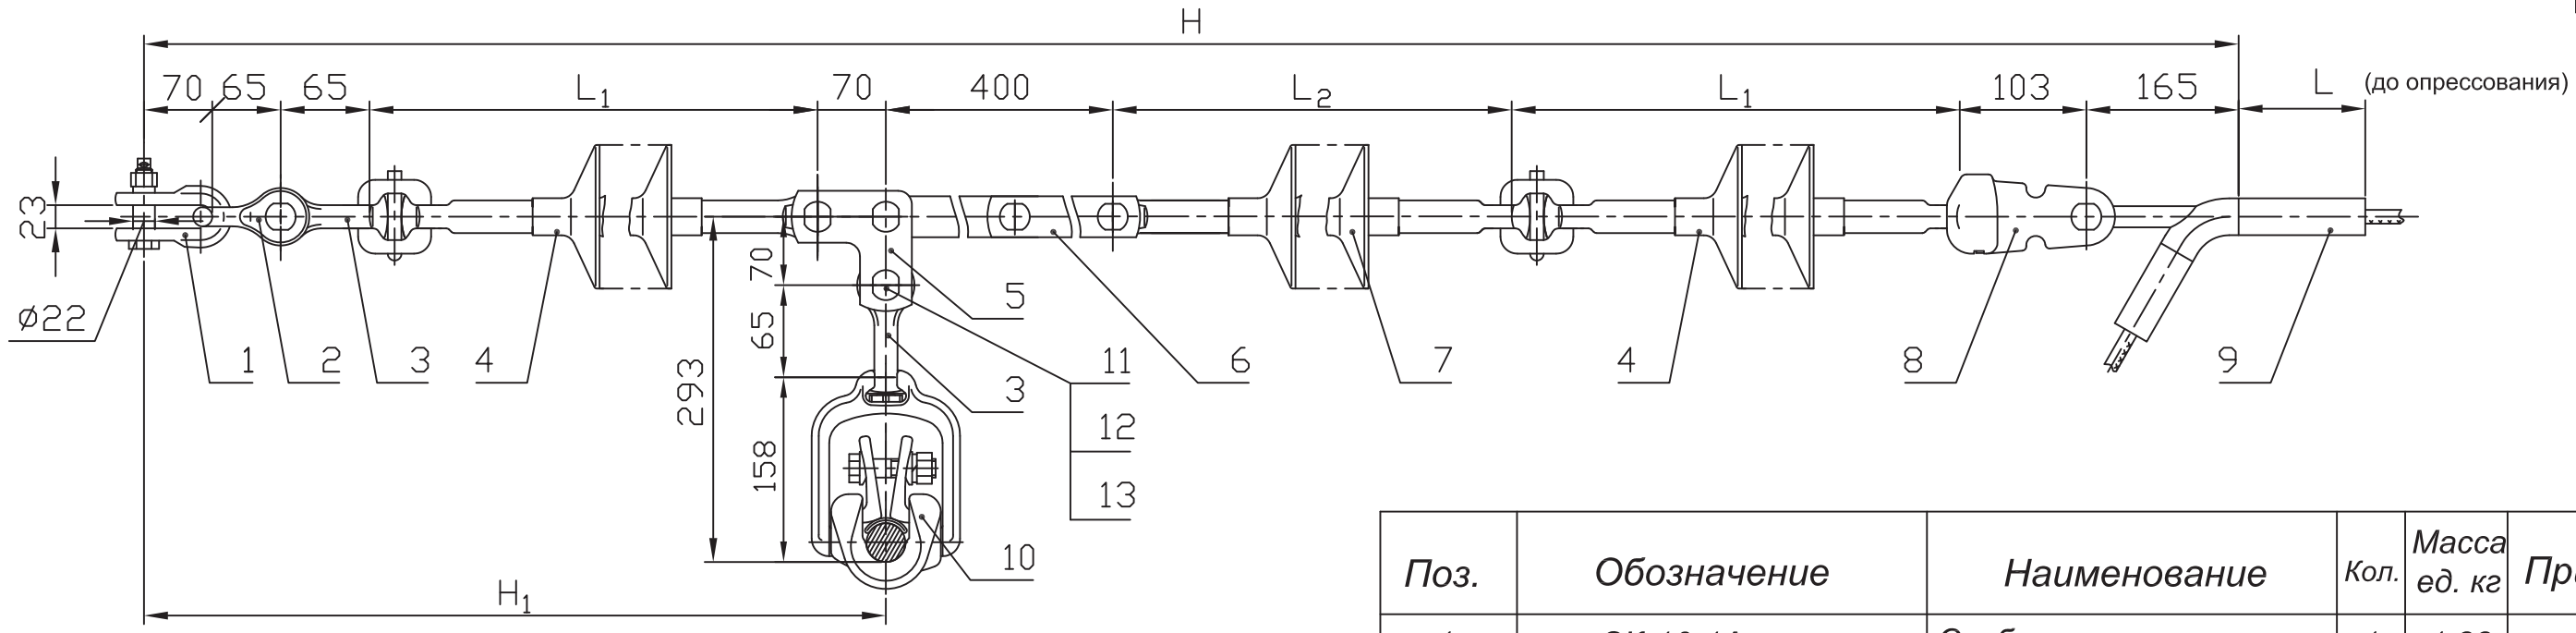

Вариант

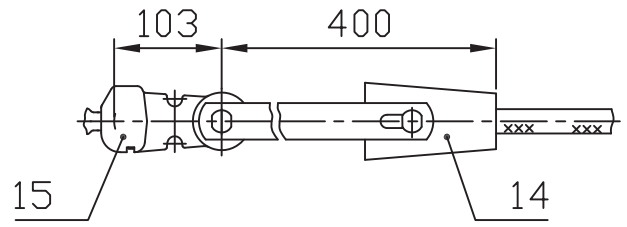


Таблица 1

Напряжение ВЛ, кВ	Провод по ГОСТ 839-80		Зажим, поз.9			Масса армат., кг
	Марка	Диаметр, мм	Обозначение	L, мм	Масса, кг	
110	АС240/32	21,6	НАС-240-1Б	160	1,63	17,1
	АС240/39		НАС-240-2Б		1,60	17,1
220	АС240/56	22,4	НАС-330-1Б	175	1,99	17,5
	АС300/39	24,0				
	АС300/48	24,1				

Таблица 2 Размеры в мм

Напряжение ВЛ, кВ	Изолятор поз.4		Изолятор поз.7		Изолирующая подвеска		
	L1	Масса, кг	L2	Масса, кг	H	H1	Масса, кг
110	1238	4,0	1200	4,0	4614	1508	29,5*
220	2070	8,0	2060	8,0	5446	2340	41,5*

1. При заказе натяжного клинового зажима типа НК-300-1 (поз.15)следует указывать марку провода. Ушко У2-12-16 (поз.9) заменить на У1-12-16 (поз.16).

2. * Масса указана с зажимом НАС-330-1Б .

Поз.	Обозначение	Наименование	Кол.	Масса ед. кг	Прим.
1	СК-16-1А	Скоба	1	1,22	
2	СК-120-1Б	Скоба	1	0,92	
3	СР-12-16	Серьга	2	0,41	
4		Изолятор исп. ГС	2	См. табл.2	
5	ПТМ-12-3А	Звено монтажное	1	1,7	
6	ПРР-12-1	Звено регулируемое	1	3,69	
7		Изолятор исп. СП	1	См. табл.2	
8	У2-12-16	Ушко двухлапчатое	1	1,54	
9	См. таблицу	Зажим натяжной	1	См. табл.1	
10	ПГН-5-3	Зажим поддерживающ.	1	5,3	
11	СТП 2700000-92	Палец 22 х 70	1	0,233	
12	ГОСТ 5915-70	Гайка М20-7Н.4.0112	1	0,064	
13	ГОСТ 397-79	Шплинт 4х28.0112	1	0,003	
14	НК-300-1	Зажим клиновой	1	5,1	
15	У1-12-16	Ушко однолапчатое	1	1,05	
Масса арматуры, кг				см. табл. 1	
Масса изолирующей подвески, кг				см. табл. 2	


ЭСИП-0080

ЭСС.001 ТМ - т.1

Утв.	Вигдергауз	Натяжные транспозиционные одноцепные изолирующие с полимерными изоляторами ряда 120 кН подвески проводов АС240/32 - АС300/48 к а/у ж/б опорам ВЛ 220 кВ и деревянным опорам ВЛ 110, 220 кВ	Стадия: Р; Лист: ; Листов: 1
Пров.	Липунцов		Филиал ОАО "ФСК ЕЭС" "Электросетьсервис"
Разраб.	Власкина		

Взам. инв. N | Подп. и дата | Инв. N подл.

Формат А3

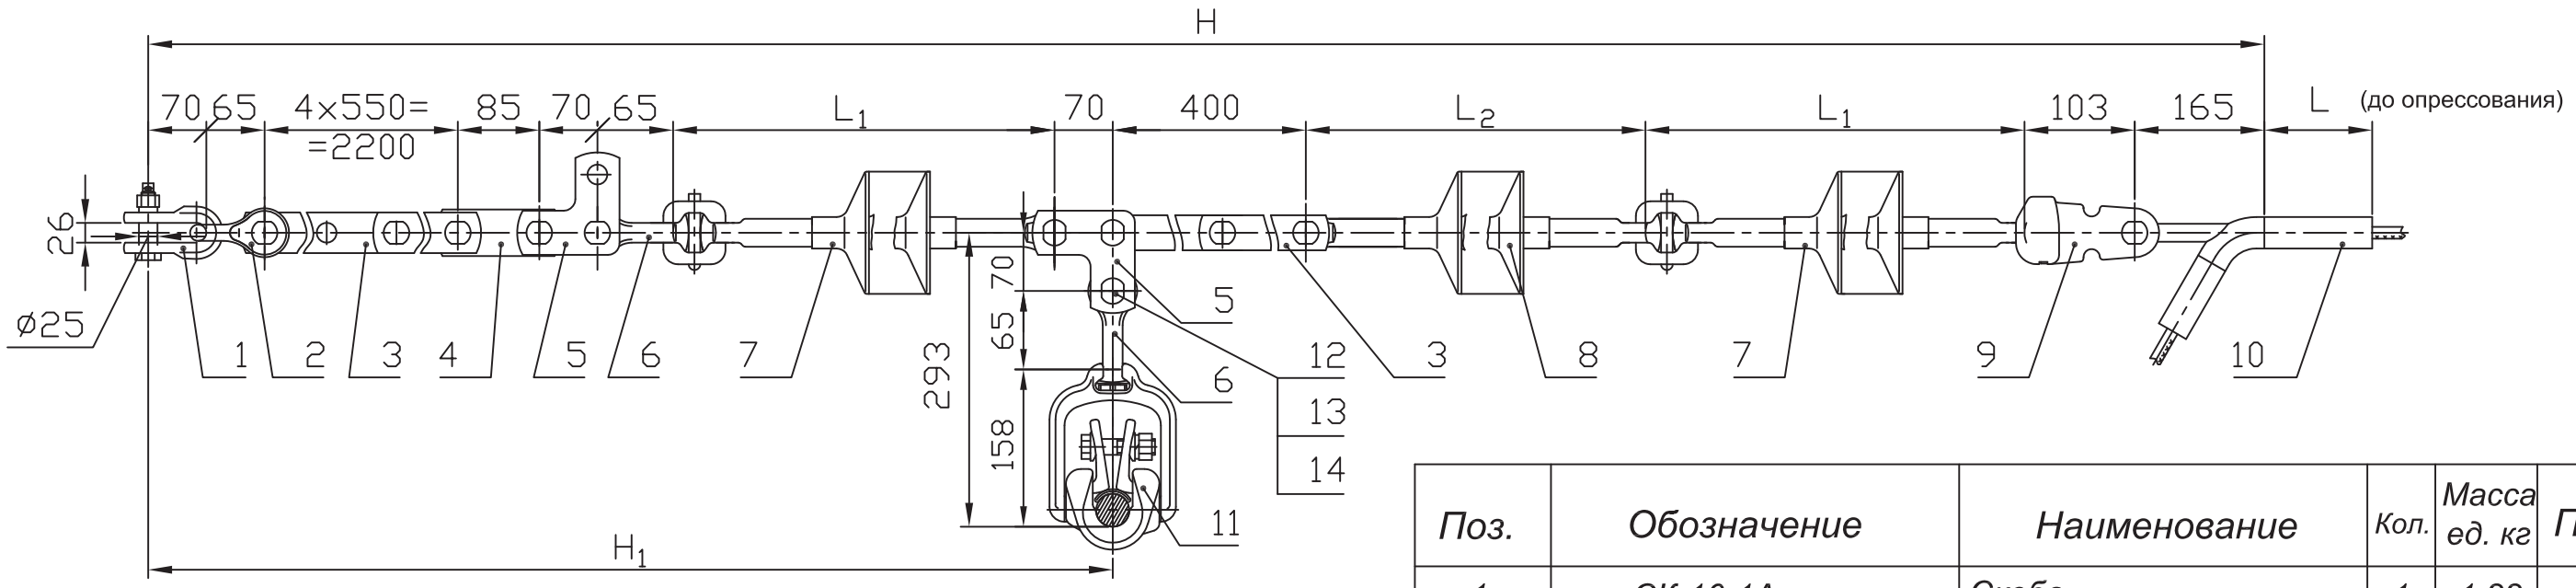

Вариант

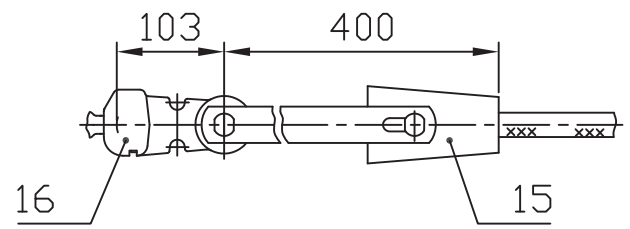


Таблица 1

Напряжение ВЛ, кВ	Провод по ГОСТ 839-80		Зажим, поз.10			Масса армат., кг
	Марка	Диаметр, мм	Обозначение	L, мм	Масса, кг	
110	АС240/32	21,6	НАС-240-1Б	160	1,63	34,5
	АС240/39		НАС-240-2Б		1,60	34,5
220	АС240/56	22,4	НАС-330-1Б	175	1,99	34,9
	АС300/39	24,0				
	АС300/48	24,1				

Таблица 2 *Размеры в мм*

Напряжение ВЛ, кВ	Изолятор поз.4		Изолятор поз.7		Изолирующая подвеска		
	L_1	Масса, кг	L_2	Масса, кг	H	H_1	Масса, кг
110	1238	4,0	1200	4,0	6969	3863	46,9*
220	2070	8,0	2070	8,0	9493	4695	58,9*

1. При заказе натяжного клинового зажима типа НК-300-1 (поз.15) следует указывать марку провода. Ушко У2-12-16 (поз.9) заменить на У1-12-16 (поз.16).

2. * Масса указана с зажимом НАС-330-1Б .

Поз.	Обозначение	Наименование	Кол.	Масса ед. кг	Прим.
1	СК-16-1А	Скоба	1	1,22	
2	СК-12-1А	Скоба	1	0,92	
3	ПРР-12-1	Звено регулируемое	5	3,69	
4	ПР-12-6	Звено прямое	1	0,94	
5	ПТМ-12-3А	Звено монтажное	2	1,7	
6	СР-12-16	Серьга	2	0,41	
7		Изолятор исп. ГС	2	См. табл.2	
8		Изолятор исп. СП	1	См. табл.2	
9	У2-12-16	Ушко двухлапчатое	1	1,54	
10	См. таблицу	Зажим натяжной	1	См. табл.1	
11	ПГН-5-3	Зажим поддерживающ.	1	5,3	
12	СТП 2700000-92	Палец 22 х 70	1	0,233	
13	ГОСТ 5915-70	Гайка М20-7Н.4.0112	1	0,064	
14	ГОСТ 397-79	Шплинт 4х28.0112	1	0,003	
15	НК-300-1	Зажим клиновой	1	5,1	
16	У1-12-16	Ушко однолапчатое	1	1,05	
Масса арматуры, кг					См. табл. 1
Масса изолирующей подвески, кг					См. табл. 2

ЭСИП-0081

ЭСС.001 ТМ - т.1

Утв.	Вигдергауз		
Пров.	Липунцов		
Разраб.	Власкина		

Натяжные транспозиционные одноцепные изолирующие с полимерными изоляторами ряда 120 кН подвески проводов АС240/32 - АС300/48 к а/у ж/б опорам ВЛ 110, 220 кВ

Стадия	Лист	Листов
Р		1


Филиал ОАО "ФСК ЕЭС" "Электросетьсервис"


Формат А3

Взам. инв. N


Подп. и дата

Инв. N подл.

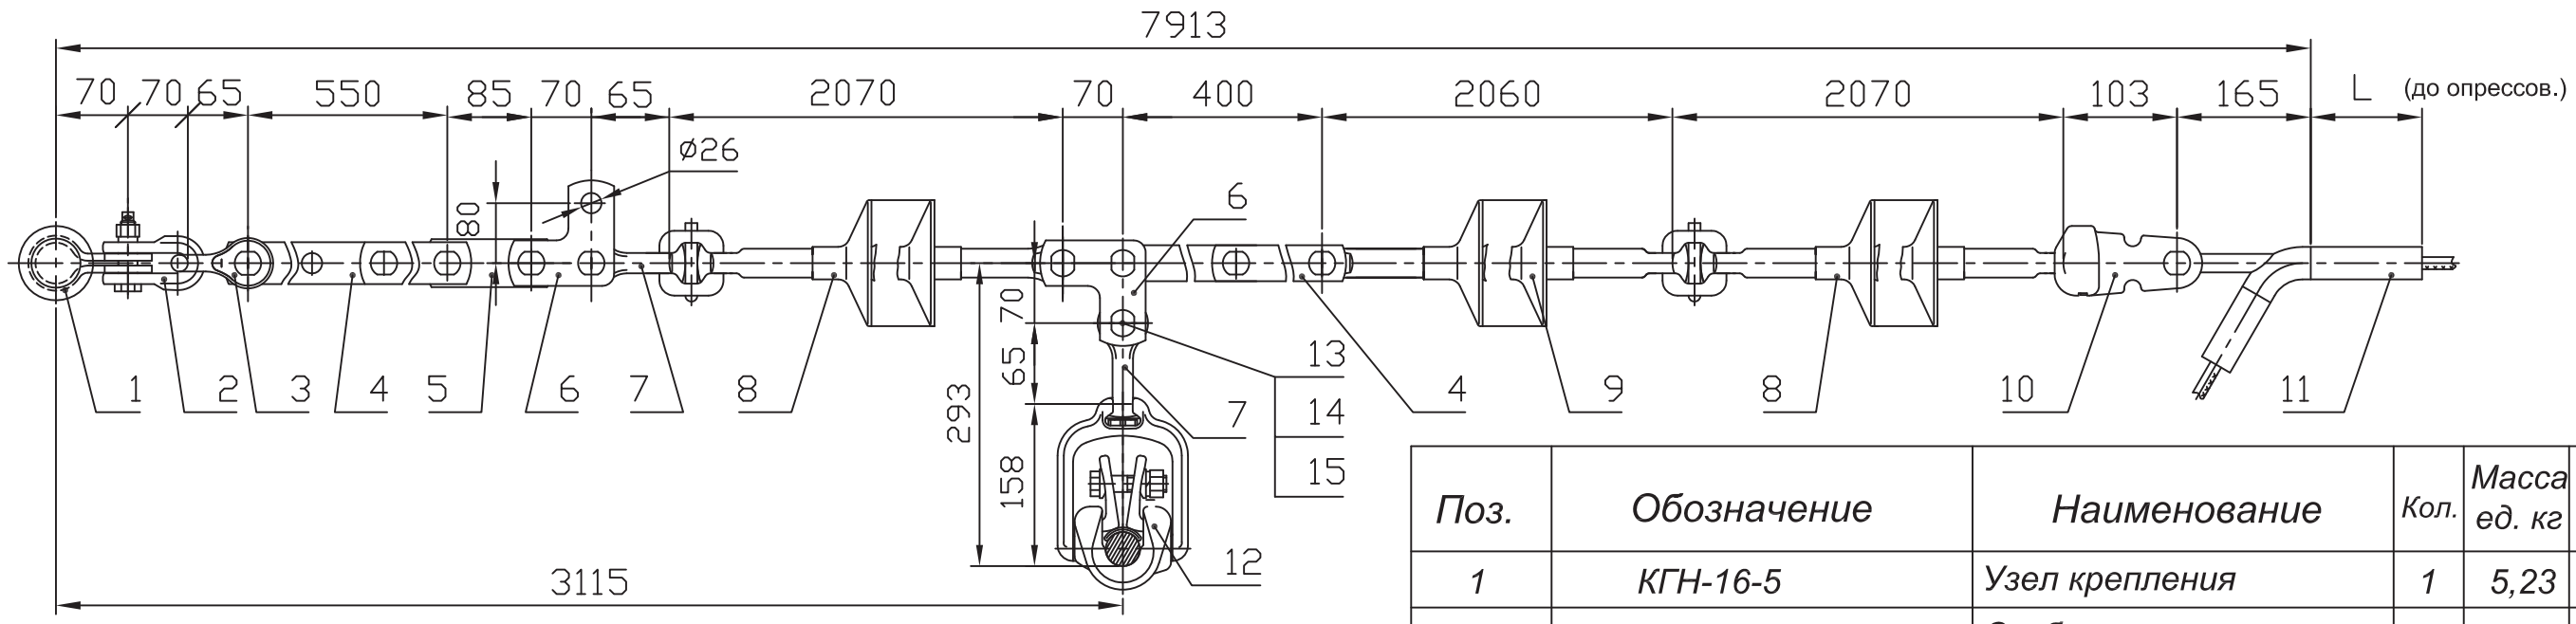

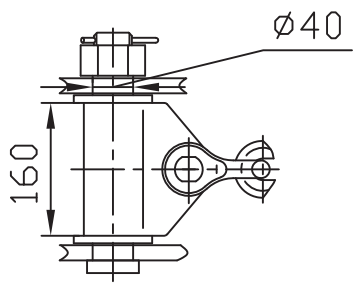

Вариант

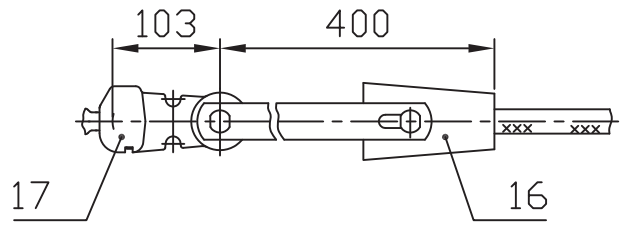

Провод по ГОСТ 839-80		Зажим, поз.11			Масса армат., кг
Марка	Диаметр, мм	Обозначение	L, мм	Масса, кг	
АС240/32	21,6	НАС-240-1Б	160	1,63	28,7
АС240/39		НАС-240-2Б		1,60	28,7
АС240/56	22,4	НАС-330-1Б	175	1,99	29,1
АС300/39	24,0				
АС300/48	24,1				

1. При заказе натяжного клинового зажима типа НК-300-1 (поз.16) следует указывать марку провода. Ушко У2-12-16 (поз.10) заменить на У1-12-16 (поз.17).

2. * Масса указана с зажимом НАС-330-1Б и изолятором ЛК 120/220-3..

Поз.	Обозначение	Наименование	Кол.	Масса ед. кг	Прим.
1	КГН-16-5	Узел крепления	1	5,23	
2	СК-16-1А	Скоба	1	1,22	
3	СК-120-1Б	Скоба	1	0,92	
4	ПРР-12-1	Звено регулируемое	2	3,69	
5	ПР-12-6	Звено прямое	1	0,94	
6	ПТМ-12-3А	Звено монтажное	2	1,7	
7	СР-12-16	Серьга	2	0,41	
8		Изолятор исп. ГС	2	8,0	
9		Изолятор исп. СП	1	8,0	
10	У2-12-16	Ушко двухлапчатое	1	1,54	
11	См. таблицу	Зажим натяжной	1	См. табл.	
12	ПГН-5-3	Зажим поддерживающ.	1	5,3	
13	СТП 2700000-92	Палец 22 х 70	1	0,233	
14	ГОСТ 5915-70	Гайка М12-7Н.4.0112	1	0,064	
15	ГОСТ 397-79	Шплинт 4х28.0112	1	0,003	
16	НК-300-1	Зажим клиновой	1	5,1	
17	У1-12-16	Ушко однолапчатое	1	1,05	
Масса арматуры, кг				См. табл.	
Масса изолирующей подвески, кг				53,1*	

ЭСИП-0082

ЭСС.001 ТМ - т.1


Утв.	Вигдергауз	Натяжные транспозиционные одноцепные изолирующие с полимерными изоляторами ряда 120 кН подвески проводов АС240/32 - АС300/48 к а/у металлическим опорам ВЛ 220 кВ	Стадия: Р; Лист: ; Листов: 1
Пров.	Липунцов		Филиал ОАО "ФСК ЕЭС" "Электросетьсервис"
Разраб.	Власкина		


Формат А3

Взам. инв. N


Подп. и дата

Инв. N подл.

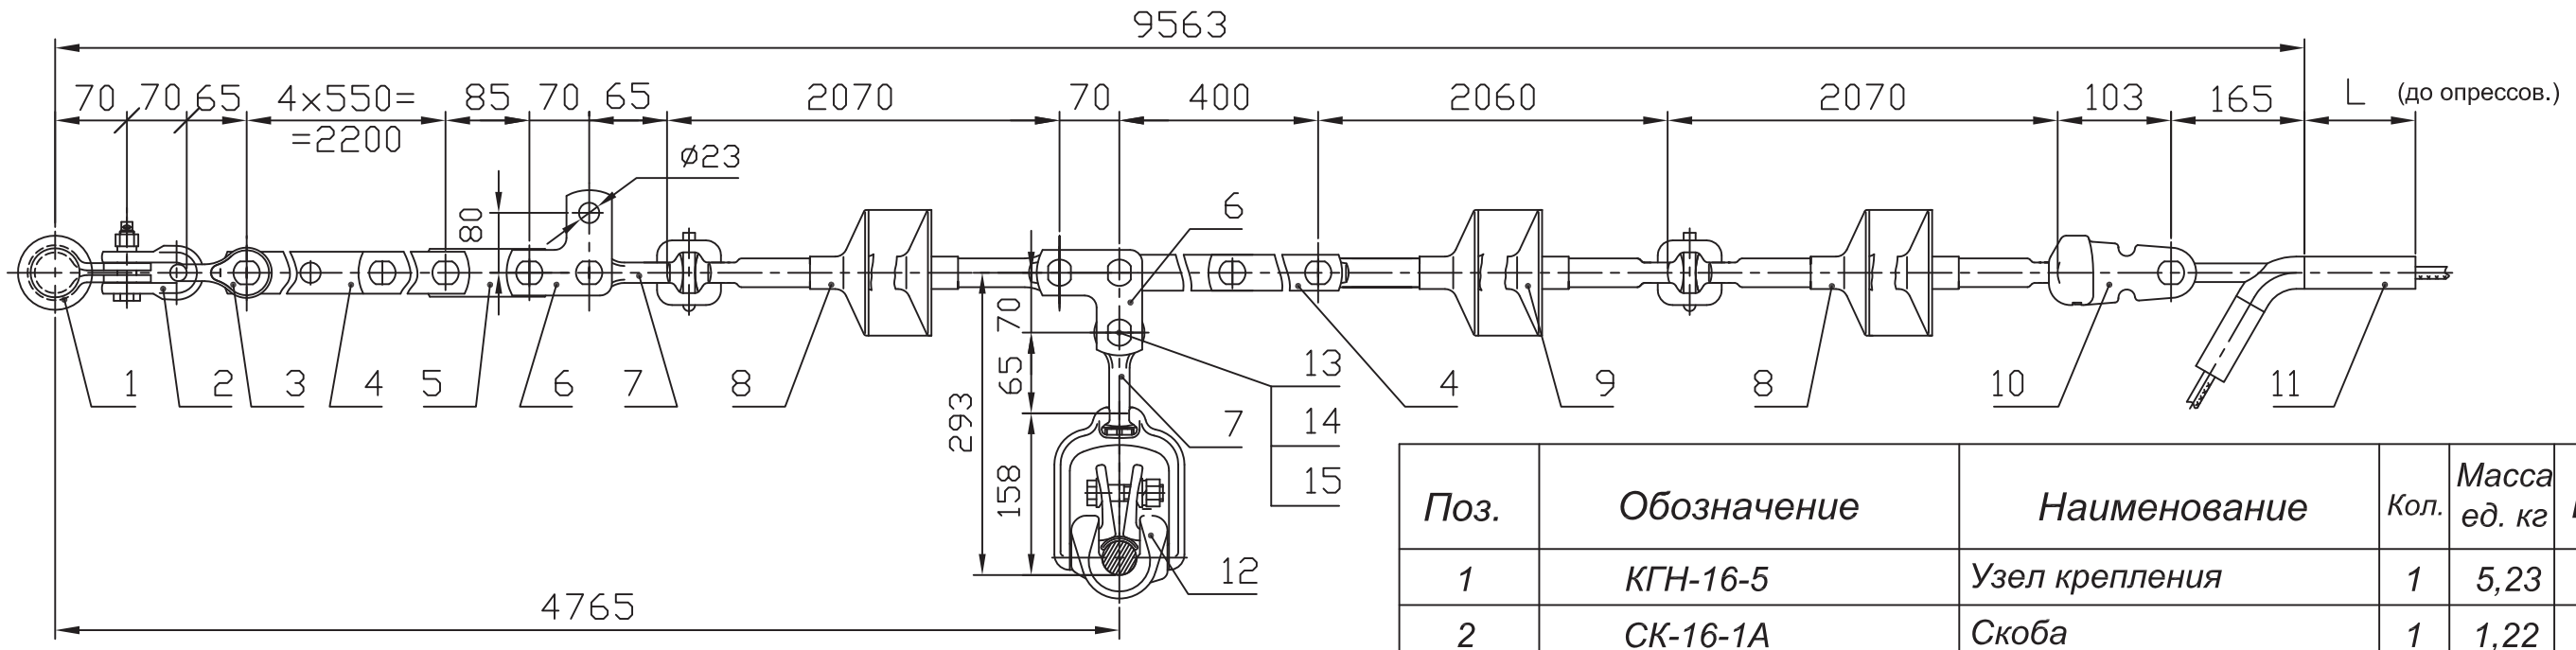

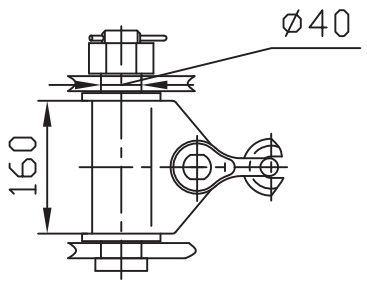

Вариант

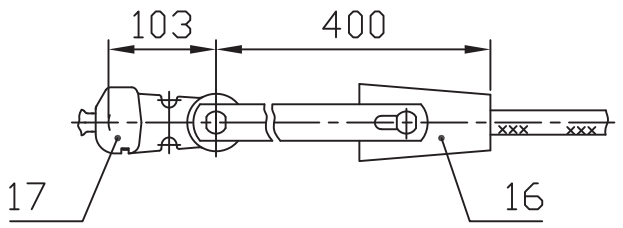

Провод по ГОСТ 839-80		Зажим, поз.11			Масса армат., кг
Марка	Диаметр, мм	Обозначение	L, мм	Масса, кг	
АС240/32	21,6	НАС-240-1Б	160	1,63	41,3
АС240/39		НАС-240-2Б		1,60	41,3
АС240/56	22,4	НАС-330-1Б	175	1,99	41,7
АС300/39	24,0				
АС300/48	24,1				

1. При заказе натяжного клинового зажима типа НК-300-1 (поз.15) следует указывать марку провода. Ушко У2-12-16 (поз.9) заменить на У1-12-16 (поз.16).

2. * Масса указана с зажимом НАС-330-1Б и изолятором ЛК 120/220-3.

Поз.	Обозначение	Наименование	Кол.	Масса ед. кг	Прим.
1	КГН-16-5	Узел крепления	1	5,23	
2	СК-16-1А	Скоба	1	1,22	
3	СК-120-1Б	Скоба	1	0,92	
4	ПРР-12-1	Звено регулируемое	5	3,69	
5	ПР-12-6	Звено прямое	1	0,94	
6	ПТМ-12-3А	Звено монтажное	2	1,7	
7	СР-12-16	Серьга	2	0,41	
8	ЛК 120/220-	Изолятор исп. ГС	2	8,0	
9	ЛК 120/220-	Изолятор исп. СП	1	8,0	
10	У2-12-16	Ушко двухлапчатое	2	1,54	
11	См. таблицу	Зажим натяжной	1	См. табл.	
12	ПГН-5-3	Зажим поддерживающ.	1	5,3	
13	СТП 2700000-92	Палец 22 х 70	1	0,233	
14	ГОСТ 5915-70	Гайка М12-7Н.4.0112	1	0,064	
15	ГОСТ 397-79	Шплинт 4х28.0112	1	0,003	
16	НК-300-1	Зажим клиновой	1	5,1	
17	У1-12-16	Ушко однолапчатое	1	1,05	
Масса арматуры, кг				См. табл.	
Масса изолирующей подвески, кг				65,7*	

ЭСИП-0083

ЭСС.001 ТМ - т.1

Утв.	Вигдергауз		
Пров.	Липунцов		
Разраб.	Власкина		


Натяжные транспозиционные одноцепные изолирующие с полимерными изоляторами ряда 120 кН подвески проводов АС240/32 - АС300/48 к а/у металлическим опорам ВЛ 220 кВ

Стадия	Лист	Листов
Р		1


Филиал ОАО "ФСК ЕЭС" "Электросетьсервис"

Взам. инв. N | Подп. и дата | Инв. N подл.

Формат А3

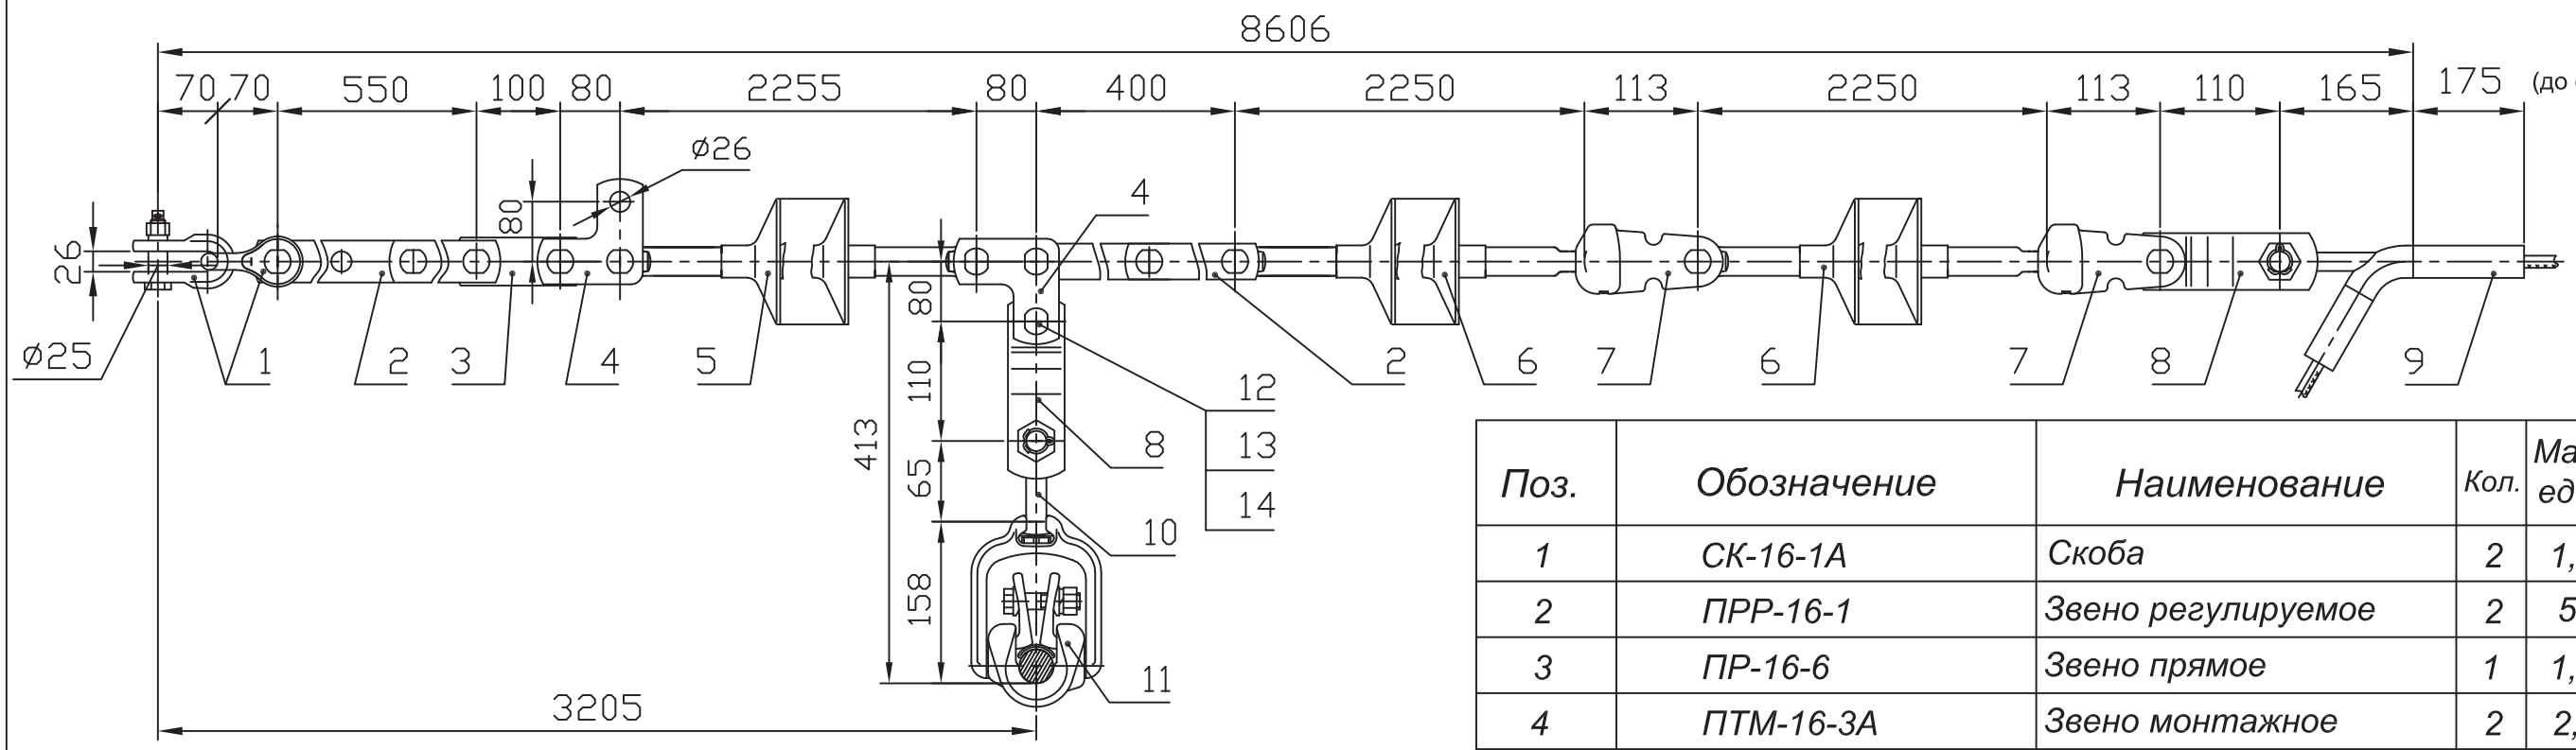

Вариант

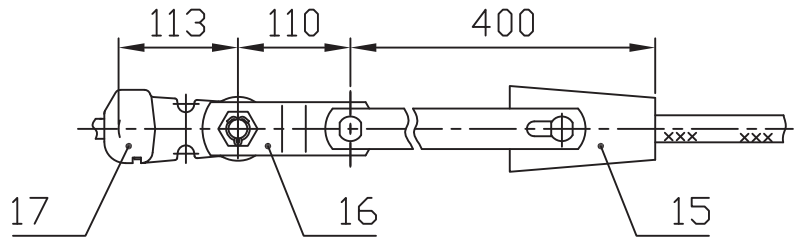

Поз.	Обозначение	Наименование	Кол.	Масса ед. кг	Прим.
1	СК-16-1А	Скоба	2	1,22	
2	ПРР-16-1	Звено регулируемое	2	5,0	
3	ПР-16-6	Звено прямое	1	1,36	
4	ПТМ-16-3А	Звено монтажное	2	2,34	
5	ЛК 160/220-	Изолятор исп. СС	1	9,0	
6	ЛК 160/220-	Изолятор исп. СП	2	9,0	
7	У2-16-20	Ушко двухлапчатое	2	2,17	
8	ПРТ-16/12-2	Звено переходное	2	1,5	
9	НАС-330-1Б	Зажим натяжной	1	1,99	
10	СР-12-16	Серьга	1	0,41	
11	ПГН-5-3	Зажим поддерживающ.	1	5,3	
12	СТП 2700000-92	Палец 22 х 70	1	0,233	
13	ГОСТ 5915-70	Гайка М20-7Н.4.0112	1	0,064	
14	ГОСТ 397-79	Шплинт 4х28.0112	1	0,003	
15	НК-300-1	Зажим клиновой	1	5,1	
16	ПРТ-12/16-2	Звено переходное	1	1,6	
17	У1-16-20	Ушко однолапчатое	1	1,6	
Масса арматуры, кг				33,8	
Масса изолирующей подвески, кг				60,8*	


1. *При заказе натяжного клинового зажима типа НК-300-1 (поз.15) следует указывать марку провода. Ушко У2-16-20 (поз.7) заменить на У1-16-20 (поз.17), а звено ПРТ-16/12-2 (поз.8) на ПРТ-12/16-2 (поз.16)..*

2. ** Масса указана с изолятором ЛК 160/220-3.*


		ЭСИП-0084	
		ЭСС.001 ТМ - т.1	
Утв.	Вигдергауз	Натяжные транспозиционные одноцепные изолирующие с полимерными изоляторами ряда 160 кН подвески проводов АС240/56, АС300/39 и АС330/43 к а/у ж/б опорам ВЛ 220 кВ	Стадия: Р; Лист: ; Листов: 1
Пров.	Липунцов		Филиал ОАО "ФСК ЕЭС" "Электросетьсервис"
Разраб.	Власкина		

Взам. инв. N | Подп. и дата | Инв. N подл.

Формат А3

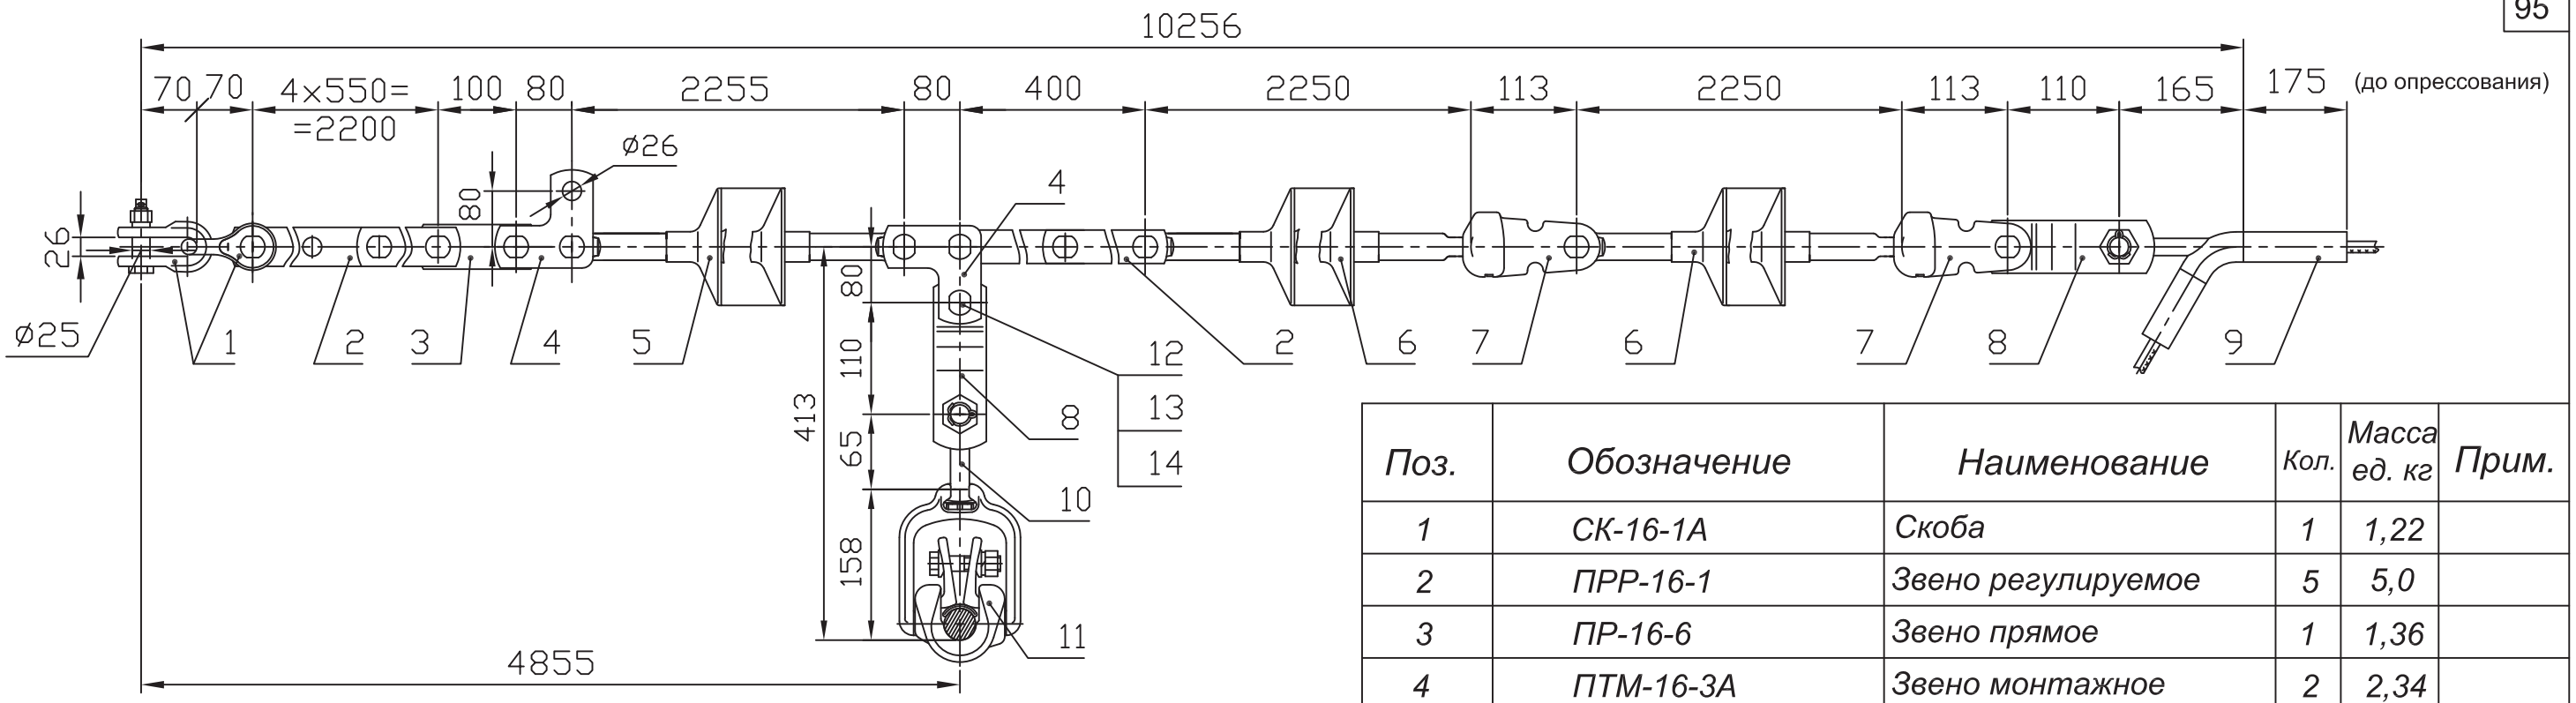

Вариант

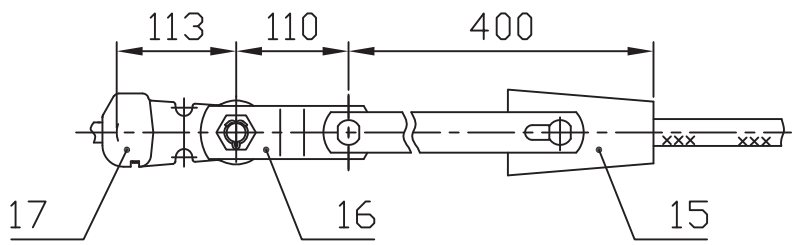

Поз.	Обозначение	Наименование	Кол.	Масса ед. кг	Прим.
1	СК-16-1А	Скоба	1	1,22	
2	ПРР-16-1	Звено регулируемое	5	5,0	
3	ПР-16-6	Звено прямое	1	1,36	
4	ПТМ-16-3А	Звено монтажное	2	2,34	
5	ЛК 160/220-	Изолятор исп. СС	1	9,0	
6	ЛК 160/220-	Изолятор исп. СП	2	9,0	
7	У2-16-20	Ушко двухлапчатое	2	2,17	
8	ПРТ-16/12-2	Звено переходное	2	1,5	
9	НАС-330-1Б	Зажим натяжной	1	1,99	
10	СР-12-16	Серьга	1	0,41	
11	ПГН-5-3	Зажим поддерживающ.	1	5,3	
12	СТП 2700000-92	Палец 22 х 70	1	0,233	
13	ГОСТ 5915-70	Гайка М20-7Н.4.0112	1	0,064	
14	ГОСТ 397-79	Шплинт 4х28.0112	1	0,003	
15	НК-300-1	Зажим клиновой	1	5,1	
16	ПРТ-12/16-2	Звено переходное	1	1,6	
17	У1-16-20	Ушко однолапчатое	1	1,6	
Масса арматуры, кг				48,8	
Масса изолирующей подвески, кг				75,8*	


1. *При заказе натяжного клинового зажима типа НК-300-1 (поз.15) следует указывать марку провода. Ушко У2-16-20 (поз.7) заменить на У1-16-20 (поз.17), а звено ПРТ-16/12-2 (поз.8) на ПРТ-12/16-2 (поз.16)..*


2. ** Масса указана с изолятором ЛК 160/220-3.*

		ЭСИП-0085	
		ЭСС.001 ТМ - т.1	
Утв.	Вигдергауз	Натяжные транспозиционные одноцепные изолирующие с полимерными изоляторами ряда 160 кН подвески проводов АС240/56, АС300/39 и АС330/43 к а/у ж/б опорам ВЛ 220 кВ	Стадия: Р; Лист: ; Листов: 1
Пров.	Липунцов		Филиал ОАО "ФСК ЕЭС" "Электросетьсервис"
Разраб.	Власкина		

Взам. инв. N | Подп. и дата | Инв. N подл.

Формат А3

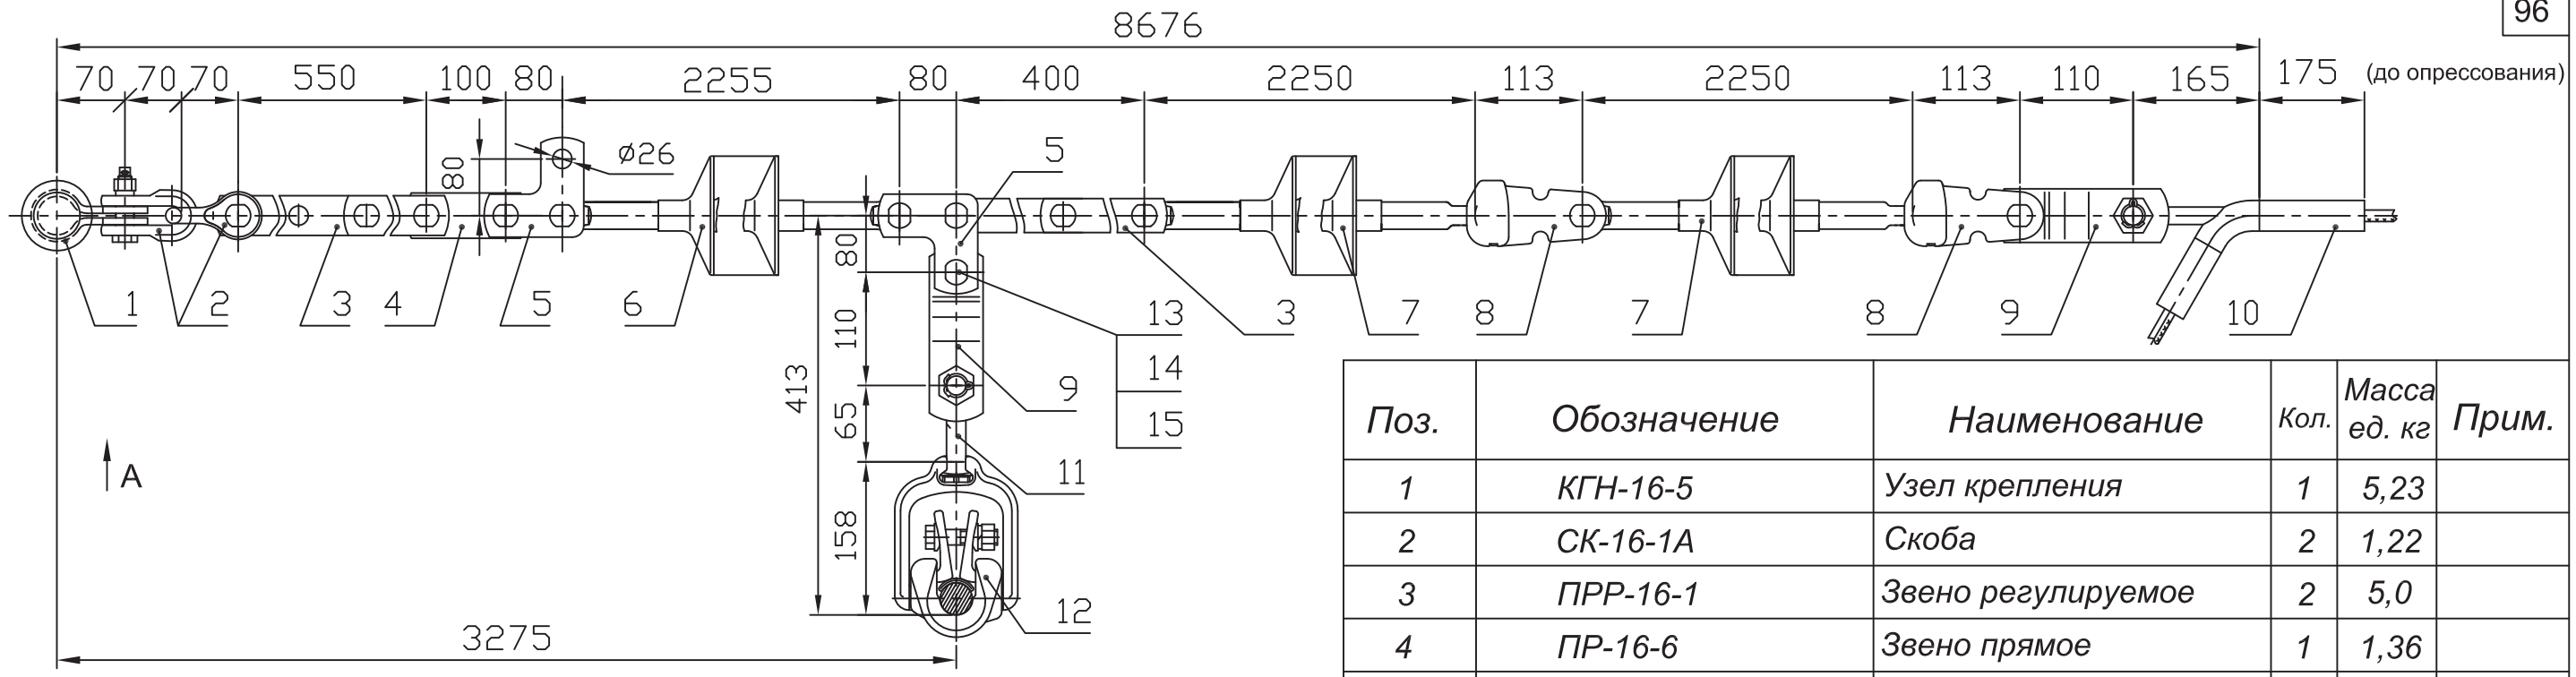

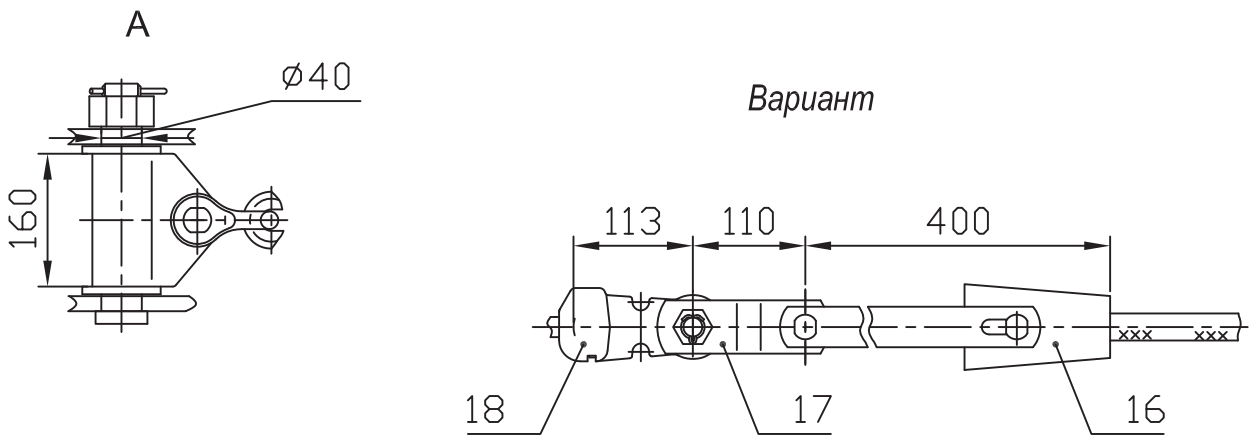

Поз.	Обозначение	Наименование	Кол.	Масса ед. кг	Прим.
1	КГН-16-5	Узел крепления	1	5,23	
2	СК-16-1А	Скоба	2	1,22	
3	ПРР-16-1	Звено регулируемое	2	5,0	
4	ПР-16-6	Звено прямое	1	1,36	
5	ПТМ-16-3А	Звено монтажное	2	2,34	
6	ЛК 160/220-	Изолятор исп. СС	1	9,0	
7	ЛК 160/220-	Изолятор исп. СП	2	9,0	
8	У2-16-20	Ушко двухлапчатое	2	2,17	
9	ПРТ-16/12-2	Звено переходное	2	1,5	
10	НАС-330-1Б	Зажим натяжной	1	1,99	
11	СР-12-16	Серьга	1	0,41	
12	ПГН-5-3	Зажим поддерживающ.	1	5,3	
13	СТП 2700000-92	Палец 22 х 70	1	0,233	
14	ГОСТ 5915-70	Гайка М20-7Н.4.0112	1	0,064	
15	ГОСТ 397-79	Шплинт 4х28.0112	1	0,003	
16	НК-300-1	Зажим клиновой	1	5,1	
17	ПРТ-12/16-2	Звено переходное	1	1,6	
18	У1-16-20	Ушко однолапчатое	1	1,6	
Масса арматуры, кг				39,0	
Масса изолирующей подвески, кг				66,0*	

1. *При заказе натяжного клинового зажима типа НК-300-1 (поз.16) следует указывать марку провода. Ушко У2-16-20 (поз.8) заменить на У1-16-20 (поз.18), а звено ПРТ-16/12-2 (поз.9) на ПРТ-12/16-2 (поз.17)..*

2. ** Масса указана с изолятором ЛК 160/220-3.*


ЭСИП-0086


ЭСС.001 ТМ - т.1

Утв.	Вигдергауз	Натяжные транспозиционные одноцепные изолирующие с полимерными изоляторами ряда 160 кН подвески проводов АС240/56, АС300/39 и АС330/43 к а/у металлическим опорам ВЛ 220 кВ	Стадия: Р; Лист: ; Листов: 1
Пров.	Липунцов		Филиал ОАО "ФСК ЕЭС" "Электросетьсервис"
Разраб.	Власкина		


Взам. инв. N | Подп. и дата | Инв. N подл.

Формат А3

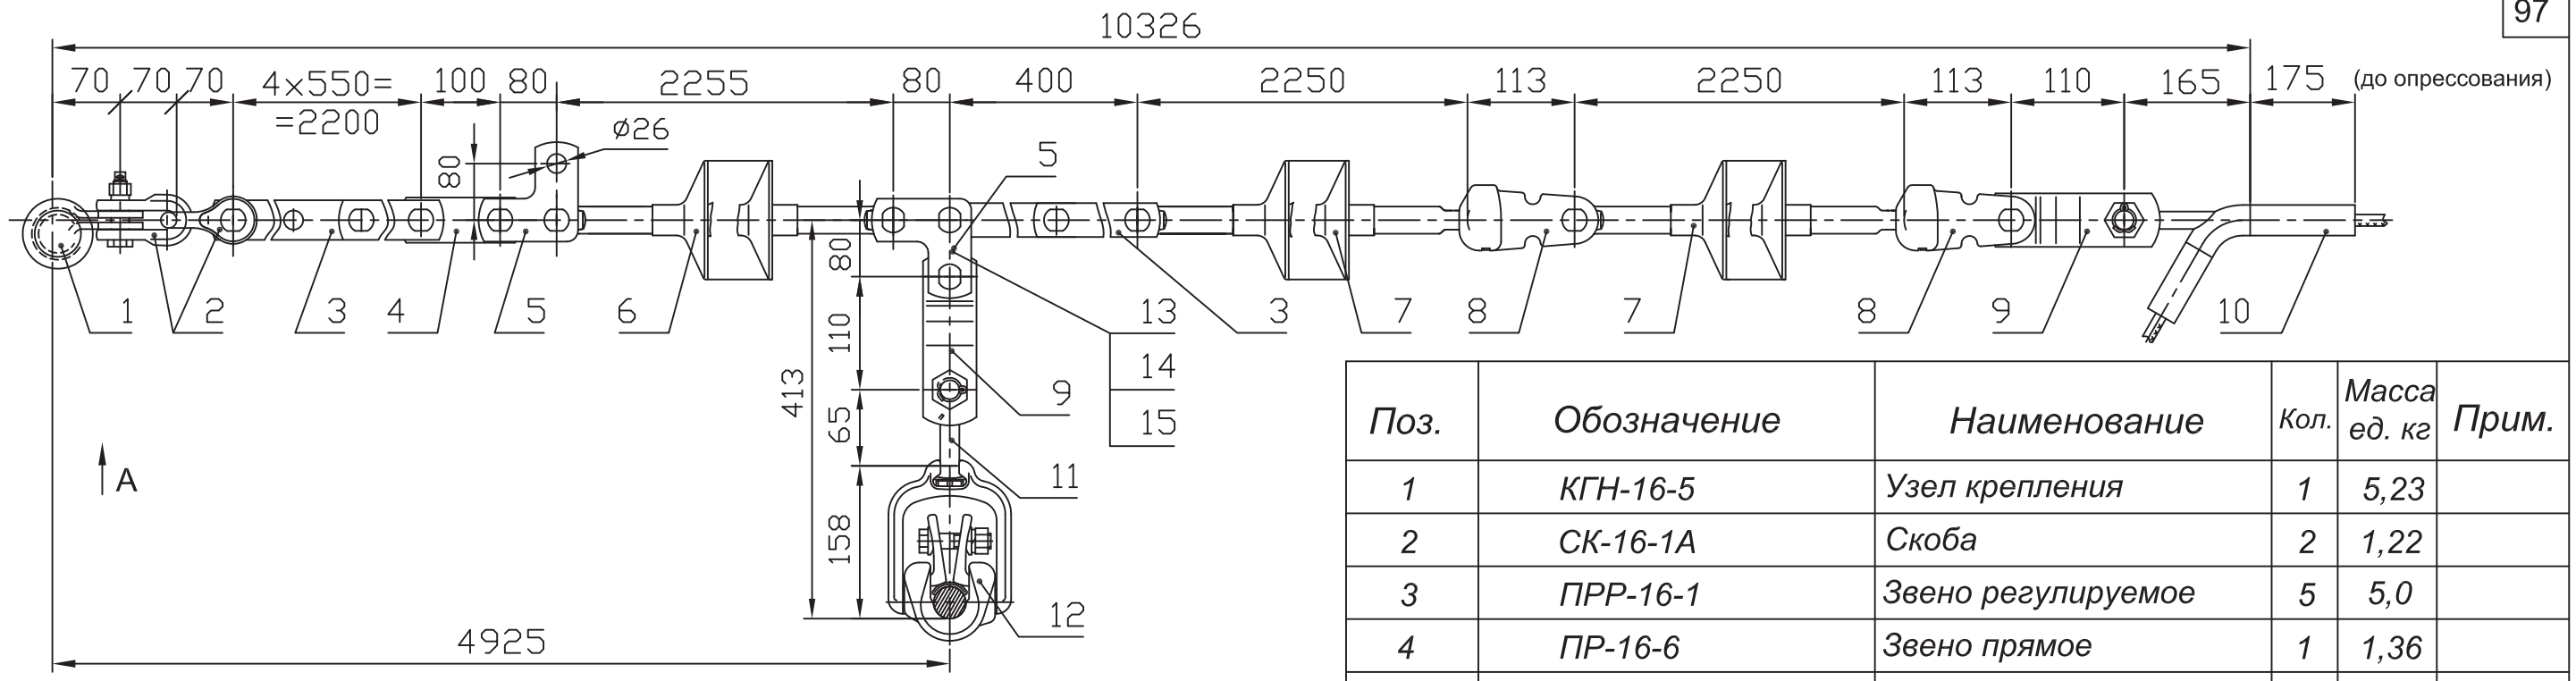

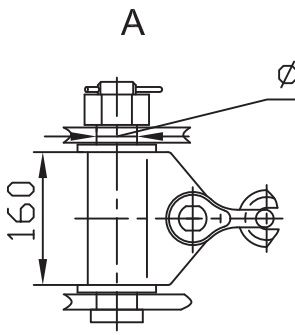

Вариант

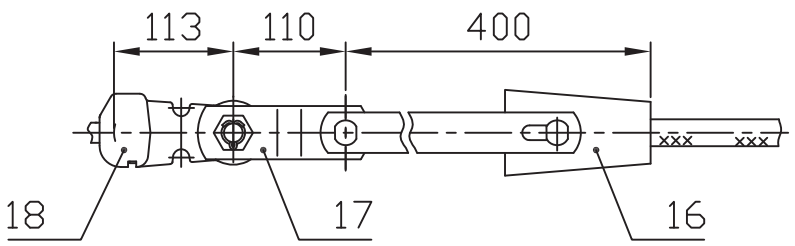

Поз.	Обозначение	Наименование	Кол.	Масса ед. кг	Прим.
1	КГН-16-5	Узел крепления	1	5,23	
2	СК-16-1А	Скоба	2	1,22	
3	ПРР-16-1	Звено регулируемое	5	5,0	
4	ПР-16-6	Звено прямое	1	1,36	
5	ПТМ-16-3А	Звено монтажное	2	2,34	
6	ЛК 160/220-	Изолятор исп. СС	1	9,0	
7	ЛК 160/220-	Изолятор исп. СП	2	9,0	
8	У2-16-20	Ушко двухлапчатое	2	2,17	
9	ПРТ-16/12-2	Звено переходное	2	1,5	
10	НАС-330-1Б	Зажим натяжной	1	1,99	
11	СР-12-16	Серьга	1	0,41	
12	ПГН-5-3	Зажим поддерживающ.	1	5,3	
13	СТП 2700000-92	Палец 22 х 70	1	0,233	
14	ГОСТ 5915-70	Гайка М20-7Н.4.0112	1	0,064	
15	ГОСТ 397-79	Шплинт 4х28.0112	1	0,003	
16	НК-400-1	Зажим клиновой	1	5,1	
17	ПРТ-12/16-2	Звено переходное	1	1,6	
18	У1-16-20	Ушко однолапчатое	1	1,6	
Масса арматуры, кг				54,0*	
Масса изолирующей подвески, кг				81,0*	

1. *При заказе натяжного клинового зажима типа НК-400-1 (поз.16) следует указывать марку провода. Ушко У2-16-20 (поз.8) заменить на У1-16-20 (поз.18), а звено ПРТ-16/12-2 (поз.9) на ПРТ-12/16-2 (поз.17).*

2. ** Масса указана с изолятором ЛК 160/220-3.*


ЭСИП-0087

ЭСС.001 ТМ - т.1


Утв.	Вигдергауз	Натяжные транспозиционные одноцепные изолирующие с полимерными изоляторами ряда 160 кН подвески проводов АС240/56 и АС330/43 к а/у металлическим опорам ВЛ 220 кВ	Стадия: Р; Лист: ; Листов: 1
Пров.	Липунцов		Филиал ОАО "ФСК ЕЭС" "Электросетьсервис"
Разраб.	Власкина		

Взам. инв. N | Подп. и дата | Инв. N подл.

Формат А3

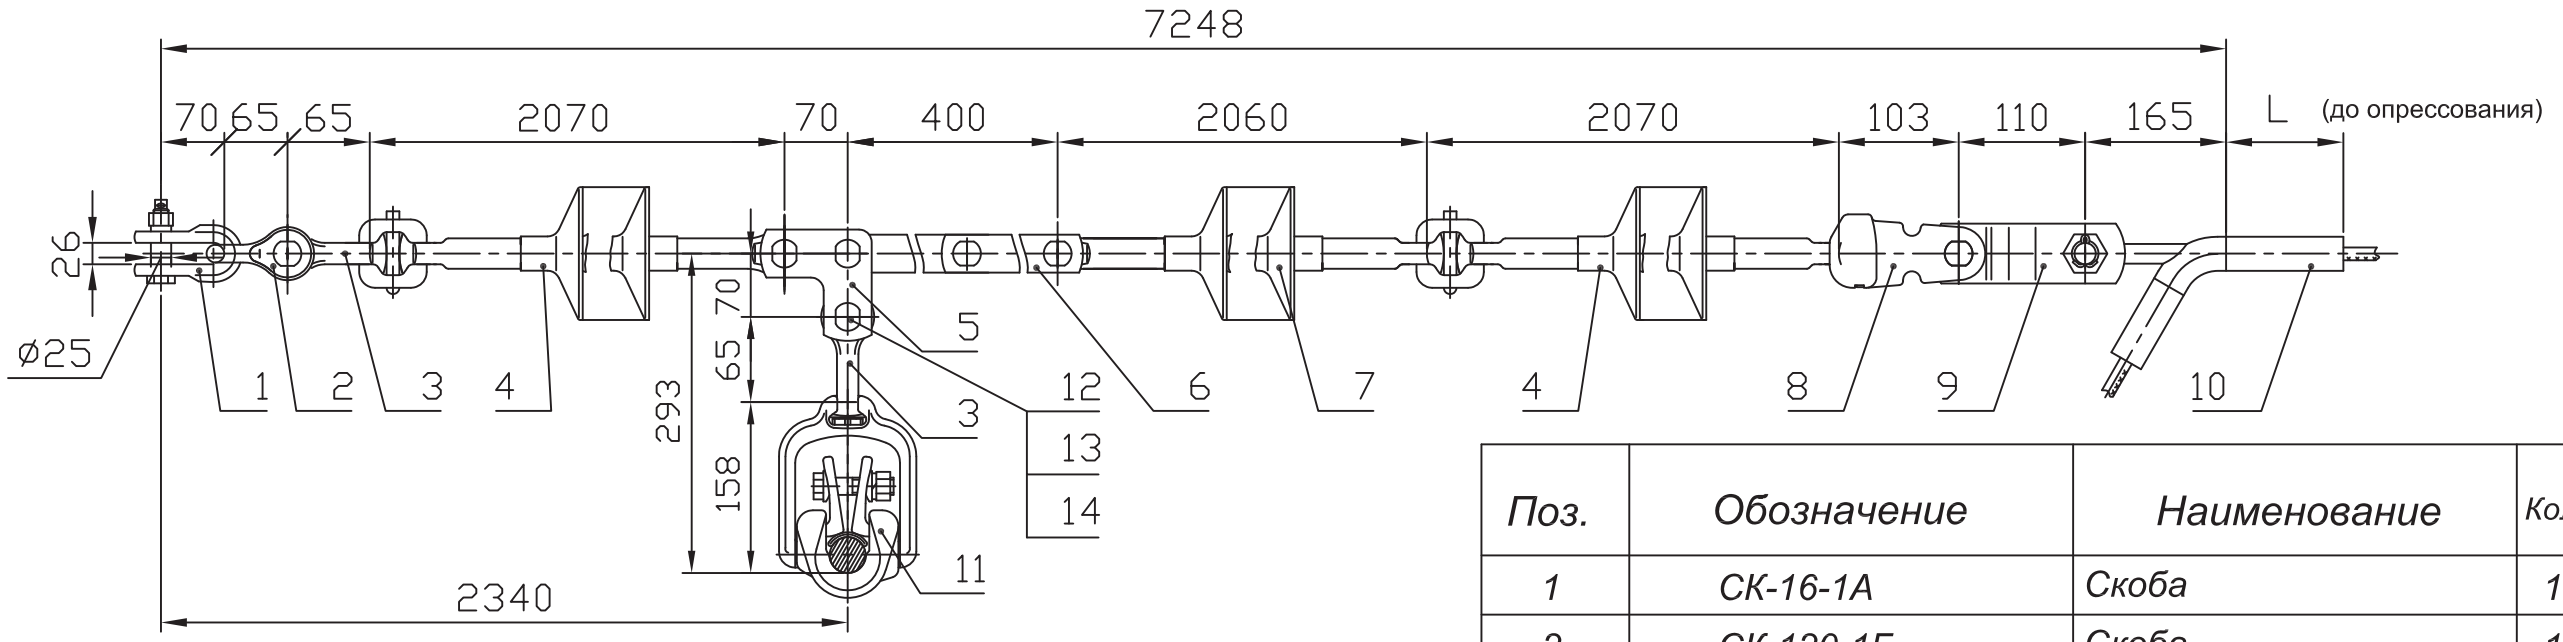

Вариант

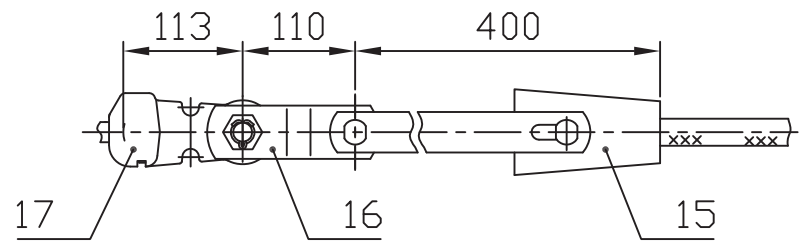

Провод по ГОСТ 839-80		Зажим, поз.10			Масса армат., кг
Марка	Диаметр, мм	Обозначение	L, мм	Масса, кг	
АС300/67	24,5	НАС-300-1Б	165	2,41	19,5
АС400/51	27,5	НАС-450-1Б	210	2,78	19,9

1. При заказе натяжного клинового зажима типа НК-400-1 (поз.15) следует указывать марку провода. Ушко У2-16-20 (поз.8) заменить на У1-16-20 (поз.17), а звено ПРТ-12/16-2 (поз.9) на ПРТ-16/12-2 (поз.16)..

2. * Масса указана с зажимом НАС-450-1Б и изолятором ЛК 120/220-3.

Поз.	Обозначение	Наименование	Кол.	Масса ед. кг	Прим.
1	СК-16-1А	Скоба	1	1,22	
2	СК-120-1Б	Скоба	1	0,92	
3	СР-12-16	Серьга	2	0,41	
4	ЛК 120/220-	Изолятор исп. ГС	2	8,0	
5	ПТМ-12-3А	Звено монтажное	1	1,7	
6	ПРР-12-1	Звено регулируемое	1	3,69	
7	ЛК 120/220-	Изолятор исп. СП	1	8,0	
8	У2-12-16	Ушко двухлапчатое	1	1,54	
9	ПРТ-12/16-2	Звено переходное	1	1,6	
10	См. таблицу	Зажим натяжной	1	См. табл.	
11	ПГН-5-3	Зажим поддерживающ.	1	5,3	
12	СТП 2700000-92	Палец 22 х 70	1	0,233	
13	ГОСТ 5915-70	Гайка М20-7Н.4.0112	1	0,064	
14	ГОСТ 397-79	Шплинт 4х28.0112	1	0,003	
15	НК-400-1	Зажим клиновой	1	5,2	
16	ПРТ-16/12-2	Звено переходное	1	1,5	
17	У1-12-16	Ушко однолапчатое	1	1,05	
Масса арматуры, кг				См. табл.	
Масса изолирующей подвески, кг				43,9*	


ЭСИП-0088

ЭСС.001 ТМ - т.1


Утв.	Вигдергауз	Натяжные транспозиционные одноцепные изолирующие с полимерными изоляторами ряда 120 кН подвески проводов АС300/67, АС400/51 к а/у деревянным опорам ВЛ 220 кВ	Стадия: Р; Лист: ; Листов: 1
Пров.	Липунцов		Филиал ОАО "ФСК ЕЭС" "Электросетьсервис"
Разраб.	Власкина		

Взам. инв. N | Подп. и дата | Инв. N подл.

Формат А3

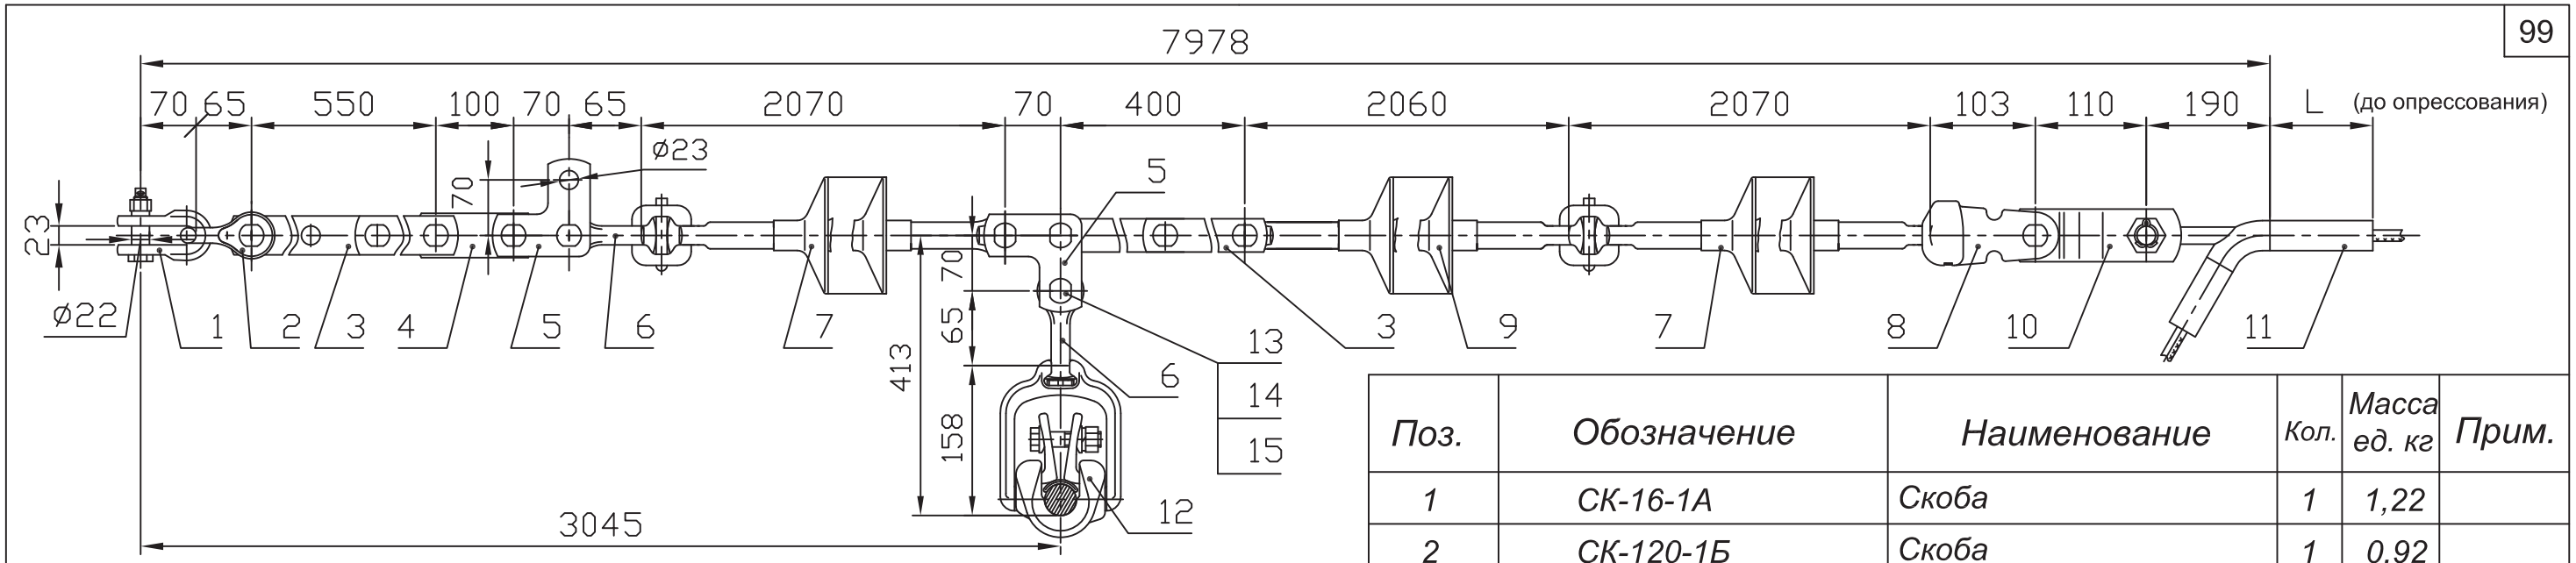

Вариант

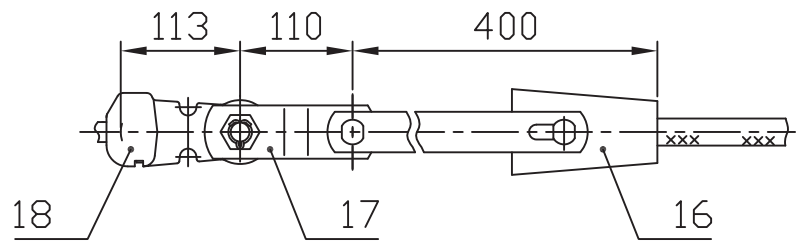

Провод по ГОСТ 839-80		Зажим, поз.11			Масса армат., кг
Марка	Диаметр, мм	Обозначение	L, мм	Масса, кг	
АС300/67	24,5	НАС-300-1Б	165	2,41	25,8
АС400/51	27,5	НАС-450-1Б	210	2,78	26,2

1. При заказе натяжного клинового зажима типа НК-400-1 (поз.16) следует указывать марку провода. Ушко У2-16-20 (поз.8) заменить на У1-16-20 (поз.18), а звено ПРТ-12/16-2 (поз.10) на ПРТ-16/12-2 (поз.17).

2. * Масса указана с зажимом НАС-450-1Б и изолятором ЛК 120/220-3.

Поз.	Обозначение	Наименование	Кол.	Масса ед. кг	Прим.
1	СК-16-1А	Скоба	1	1,22	
2	СК-120-1Б	Скоба	1	0,92	
3	ПРР-12-1	Звено регулируемое	2	3,69	
4	ПР-12-6	Звено прямое	1	0,94	
5	ПТМ-12-3А	Звено монтажное	2	1,7	
6	СР-12-16	Серьга	2	0,41	
7	ЛК 120/220-	Изолятор исп. ГС	2	8,0	
8	У2-12-16	Ушко двухлапчатое	1	1,54	
9	ЛК 120/220-	Изолятор исп. СП	1	8,0	
10	ПРТ-12/16-2	Звено переходное	1	1,6	
11	См. таблицу	Зажим натяжной	1	См. табл.	
12	ПГН-5-3	Зажим поддерживающ.	1	5,3	
13	СТП 2700000-92	Палец 22 х 70	1	0,233	
14	ГОСТ 5915-70	Гайка М20-7Н.4.0112	1	0,064	
15	ГОСТ 397-79	Шплинт 4х28.0112	1	0,003	
16	НК-400-1	Зажим клиновой	1	5,2	
17	ПРТ-16/12-2	Звено переходное	1	1,5	
18	У1-12-16	Ушко однолапчатое	1	1,05	
Масса арматуры, кг				См. табл.	
Масса изолирующей подвески, кг				50,2*	

ЭСИП-0089

ЭСС.001 ТМ - т.1


Утв.	Вигдергауз	Натяжные транспозиционные одноцепные изолирующие с полимерными изоляторами ряда 120 кН подвески проводов АС240/56 и АС330/43 к а/у деревянным опорам ВЛ 220 кВ	
Пров.	Липунцов		
Разраб.	Власкина		

Стадия	Лист	Листов
Р		1


Филиал ОАО "ФСК ЕЭС" "Электросетьсервис"

Взам. инв. N | Подп. и дата | Инв. N подл.

Формат А3

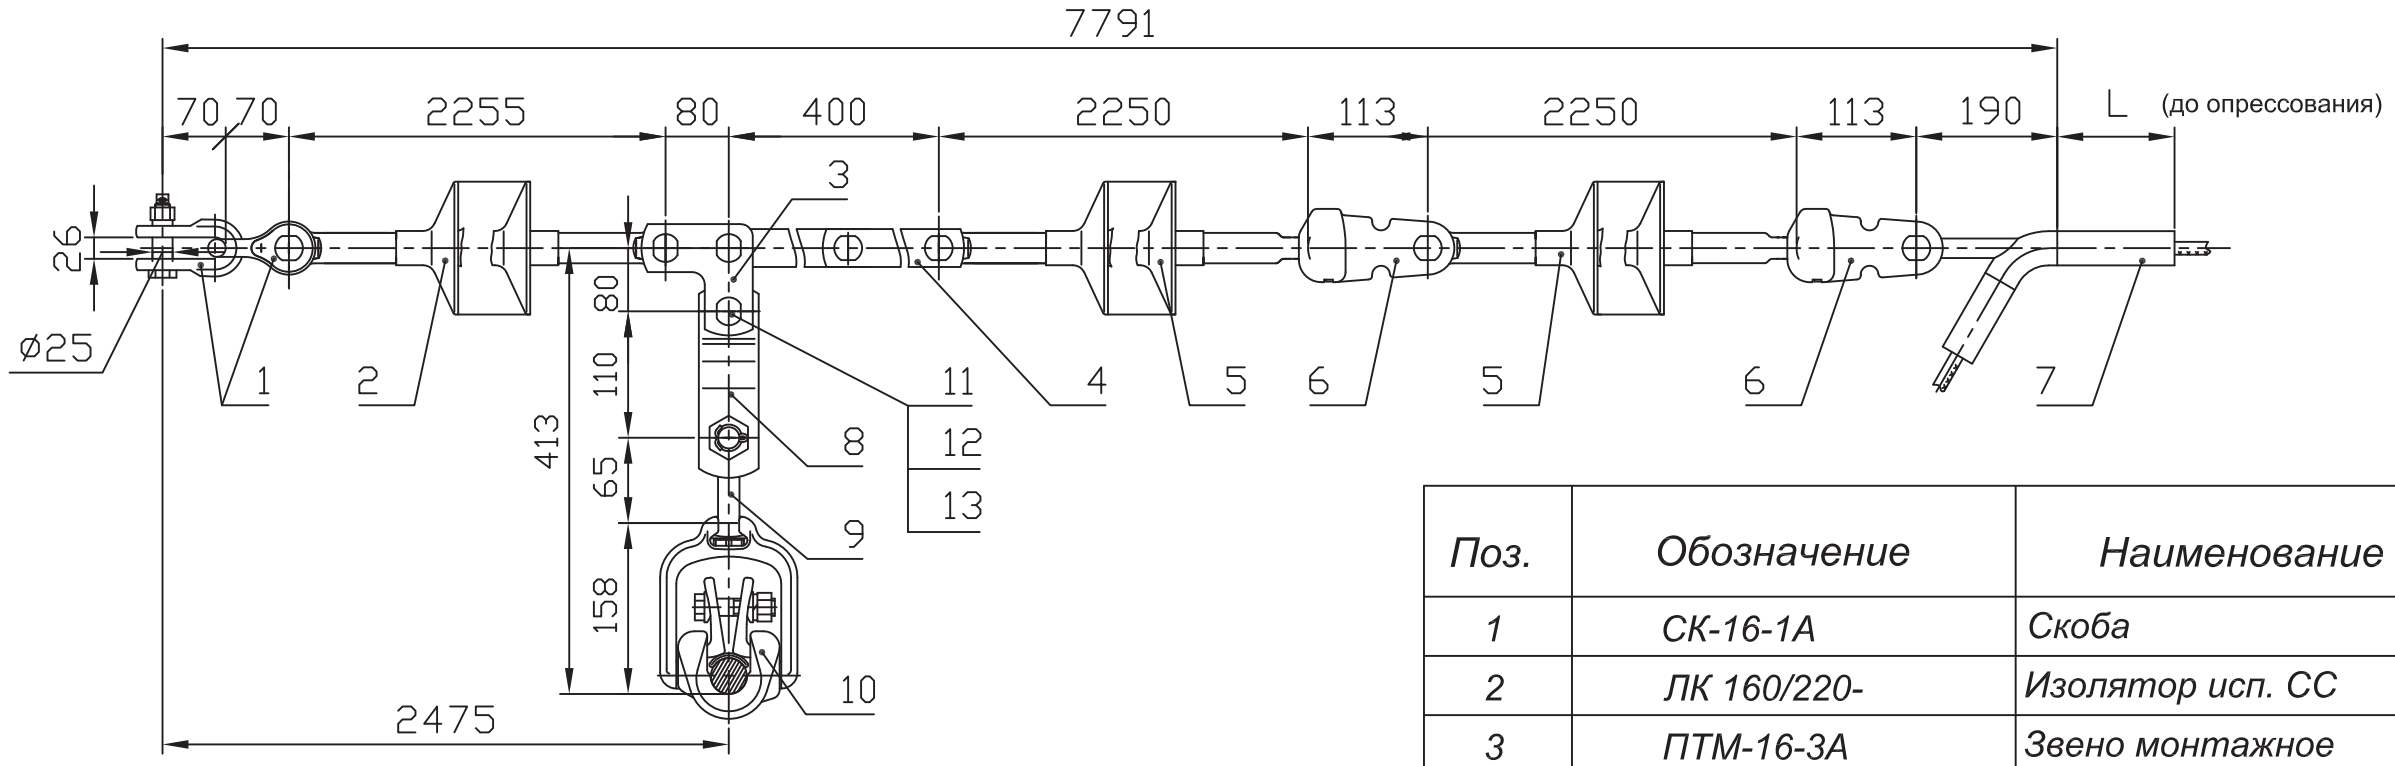

Вариант

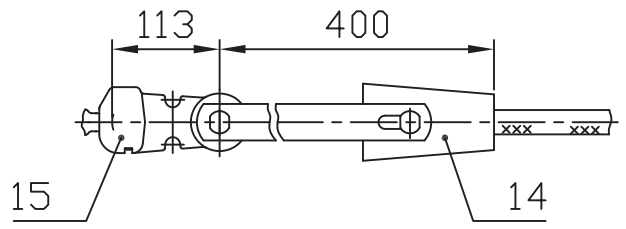

Провод по ГОСТ 839-80		Зажим, поз.7			Масса армат., кг
Марка	Диаметр, мм	Обозначение	L, мм	Масса, кг	
АС300/67	24,5	НАС-300-1Б	165	2,41	24,0
АС400/51	27,5	НАС-450-1Б	210	2,78	24,4

1. При заказе натяжного клинового зажима типа НК-400-1 (поз.14) следует указывать марку провода. Ушко У2-16-20 (поз.6) заменить на У1-16-20 (поз.15).

2. * Масса указана с зажимом НАС-450-1Б и изолятором ЛК 160/220-3.

Поз.	Обозначение	Наименование	Кол.	Масса ед. кг	Прим.
1	СК-16-1А	Скоба	2	1,22	
2	ЛК 160/220-	Изолятор исп. СС	1	8,0	
3	ПТМ-16-3А	Звено монтажное	1	2,34	
4	ПРР-16-1	Звено регулируемое	1	5,0	
5	ЛК 160/220-	Изолятор исп. СП	2	8,0	
6	У2-16-20	Ушко двухлапчатое	2	2,17	
7	См. таблицу	Зажим натяжной	1	См. табл.	
8	ПРТ-16/12-2	Звено переходное	1	1,5	
9	СР-12-16	Серьга	1	0,41	
10	ПГН-5-3	Зажим поддерживающ.	1	5,3	
11	СТП 2700000-92	Палец 22 х 70	1	0,233	
12	ГОСТ 5915-70	Гайка М20-7Н.4.0112	1	0,064	
13	ГОСТ 397-79	Шплинт 4х28.0112	1	0,003	
14	НК-400-1	Зажим клиновой	1	5,2	
15	У1-16-20	Ушко однолапчатое	1	1,6	
Масса арматуры, кг				См. табл.	
Масса изолирующей подвески, кг				48,4*	


ЭСИП-0090

ЭСС.001 ТМ - т.1


Утв.	Вигдергауз	Натяжные транспозиционные одноцепные изолирующие с полимерными изоляторами ряда 160 кН подвески проводов АС300/67 и АС400/51 к а/у деревянным опорам ВЛ 220 кВ	Стадия: Р; Лист; Листов: 1
Пров.	Липунцов		Филиал ОАО "ФСК ЕЭС" "Электросетьсервис"
Разраб.	Власкина		

Взам. инв. N | Подп. и дата | Инв. N подл.

Формат А3

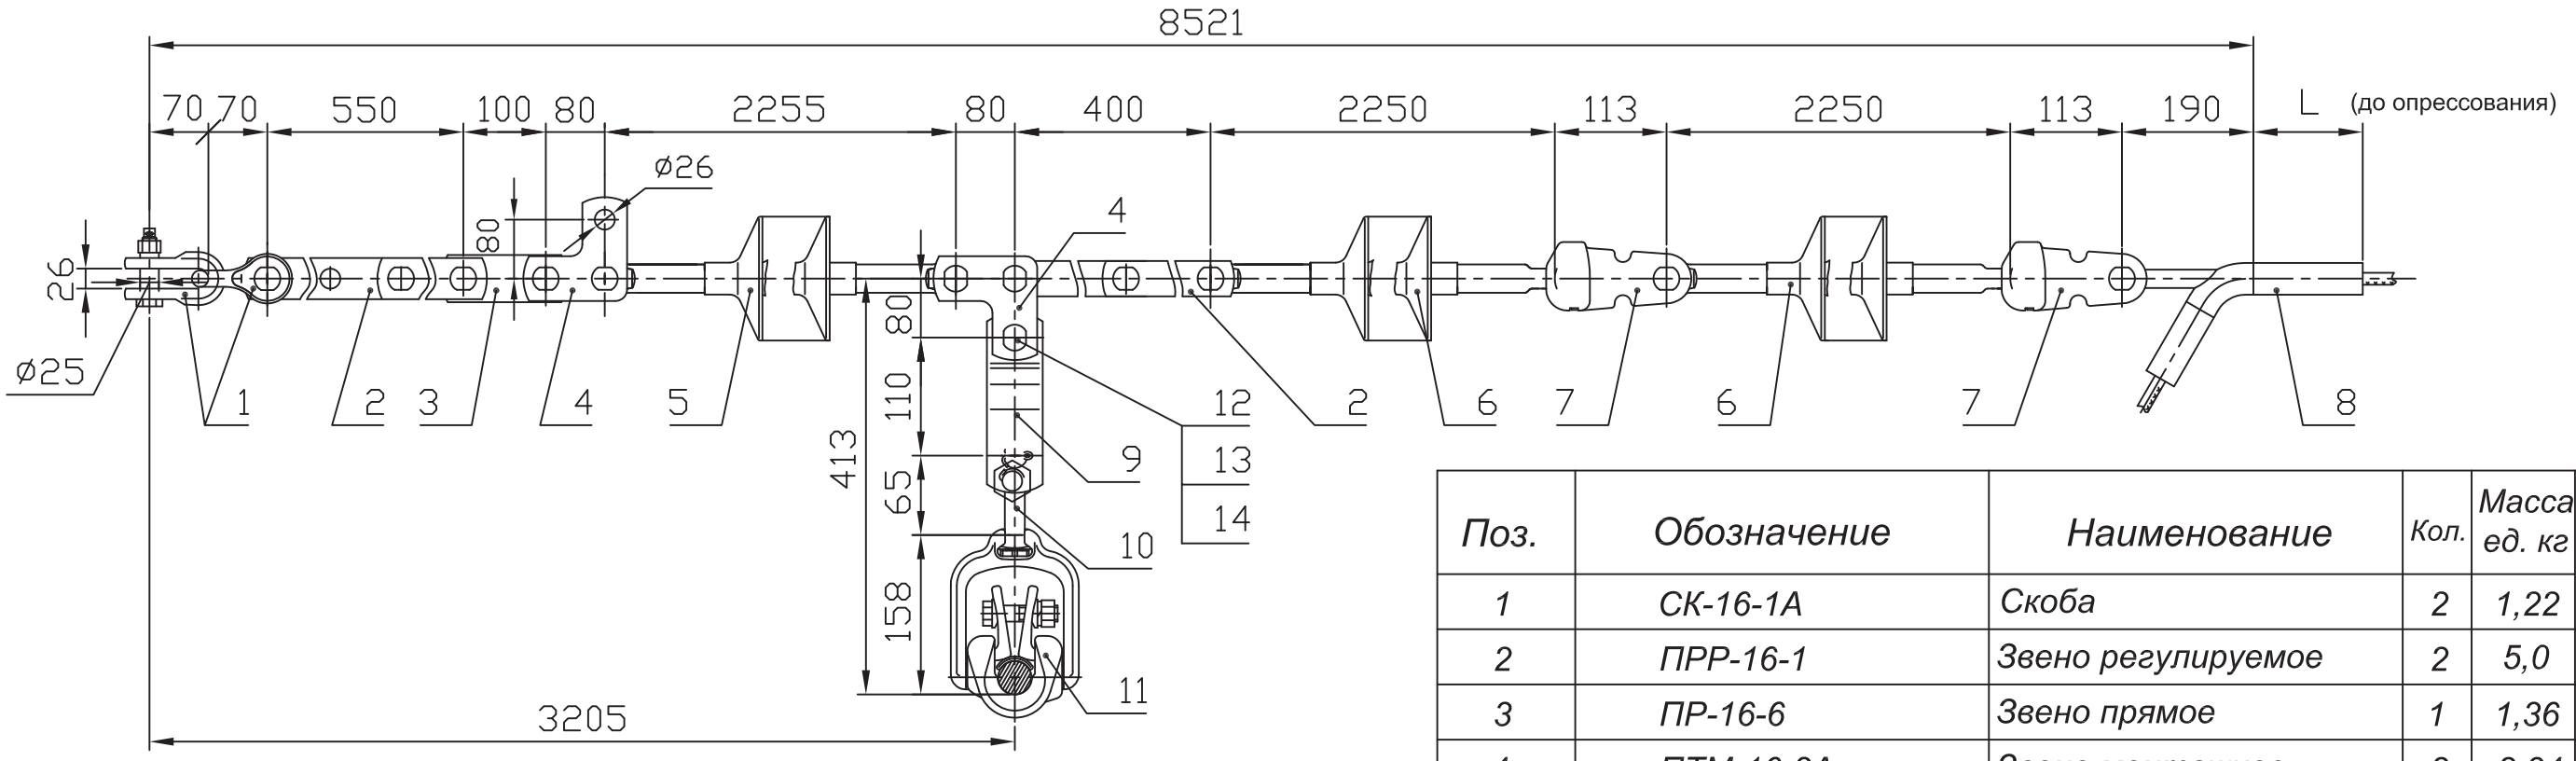

Вариант

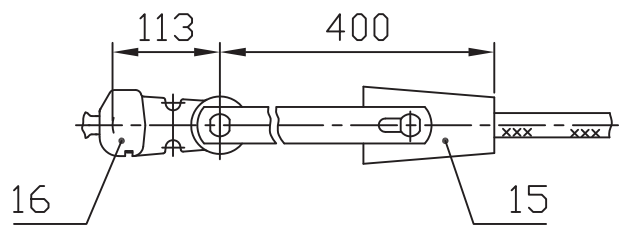

Провод по ГОСТ 839-80		Зажим, поз.8			Масса армат., кг
Марка	Диаметр, мм	Обозначение	L, мм	Масса, кг	
АС300/67	24,5	НАС-300-1Б	165	2,41	32,7
АС400/51	27,5	НАС-450-1Б	210	2,78	33,1

1. При заказе натяжного клинового зажима типа НК-400-1 (поз.15) следует указывать марку провода. Ушко У2-16-20 (поз.7) заменить на У1-16-20 (поз.16).

2. * Масса указана с зажимом НАС-450-1Б и изолятором ЛК 160/220-3.

Поз.	Обозначение	Наименование	Кол.	Масса ед. кг	Прим.
1	СК-16-1А	Скоба	2	1,22	
2	ПРР-16-1	Звено регулируемое	2	5,0	
3	ПР-16-6	Звено прямое	1	1,36	
4	ПТМ-16-3А	Звено монтажное	2	2,34	
5	ЛК 160/220-	Изолятор исп. СС	1	9,0	
6	ЛК 160/220-	Изолятор исп. СП	2	9,0	
7	У2-16-20	Ушко двухлапчатое	2	2,17	
8	См. таблицу	Зажим натяжной	1	См. табл.	
9	ПРТ-16/12-2	Звено переходное	1	1,5	
10	СР-12-16	Серьга	1	0,41	
11	ПГН-5-3	Зажим поддерживающ.	1	5,3	
12	СТП 2700000-92	Палец 22 х 70	1	0,233	
13	ГОСТ 5915-70	Гайка М20-7Н.4.0112	1	0,064	
14	ГОСТ 397-79	Шплинт 4х28.0112	1	0,003	
15	НК-400-1	Зажим клиновой	1	5,2	
16	У1-16-20	Ушко однолапчатое	1	1,6	
Масса арматуры, кг				См. табл.	
Масса изолирующей подвески, кг				60,1*	

ЭСИП-0091

ЭСС.001 ТМ - т.1

Утв.	Вигдергауз		
Пров.	Липунцов		
Разраб.	Власкина		

Натяжные транспозиционные одноцепные изолирующие с полимерными изоляторами ряда 160 кН подвески проводов АС300/67 и АС400/51 к а/у ж/б и деревянным опорам ВЛ 220 кВ

Стадия	Лист	Листов
Р		1


Филиал ОАО "ФСК ЕЭС" "Электросетьсервис"

Формат А3


Взам. инв. N

Подп. и дата

Инв. N подл.

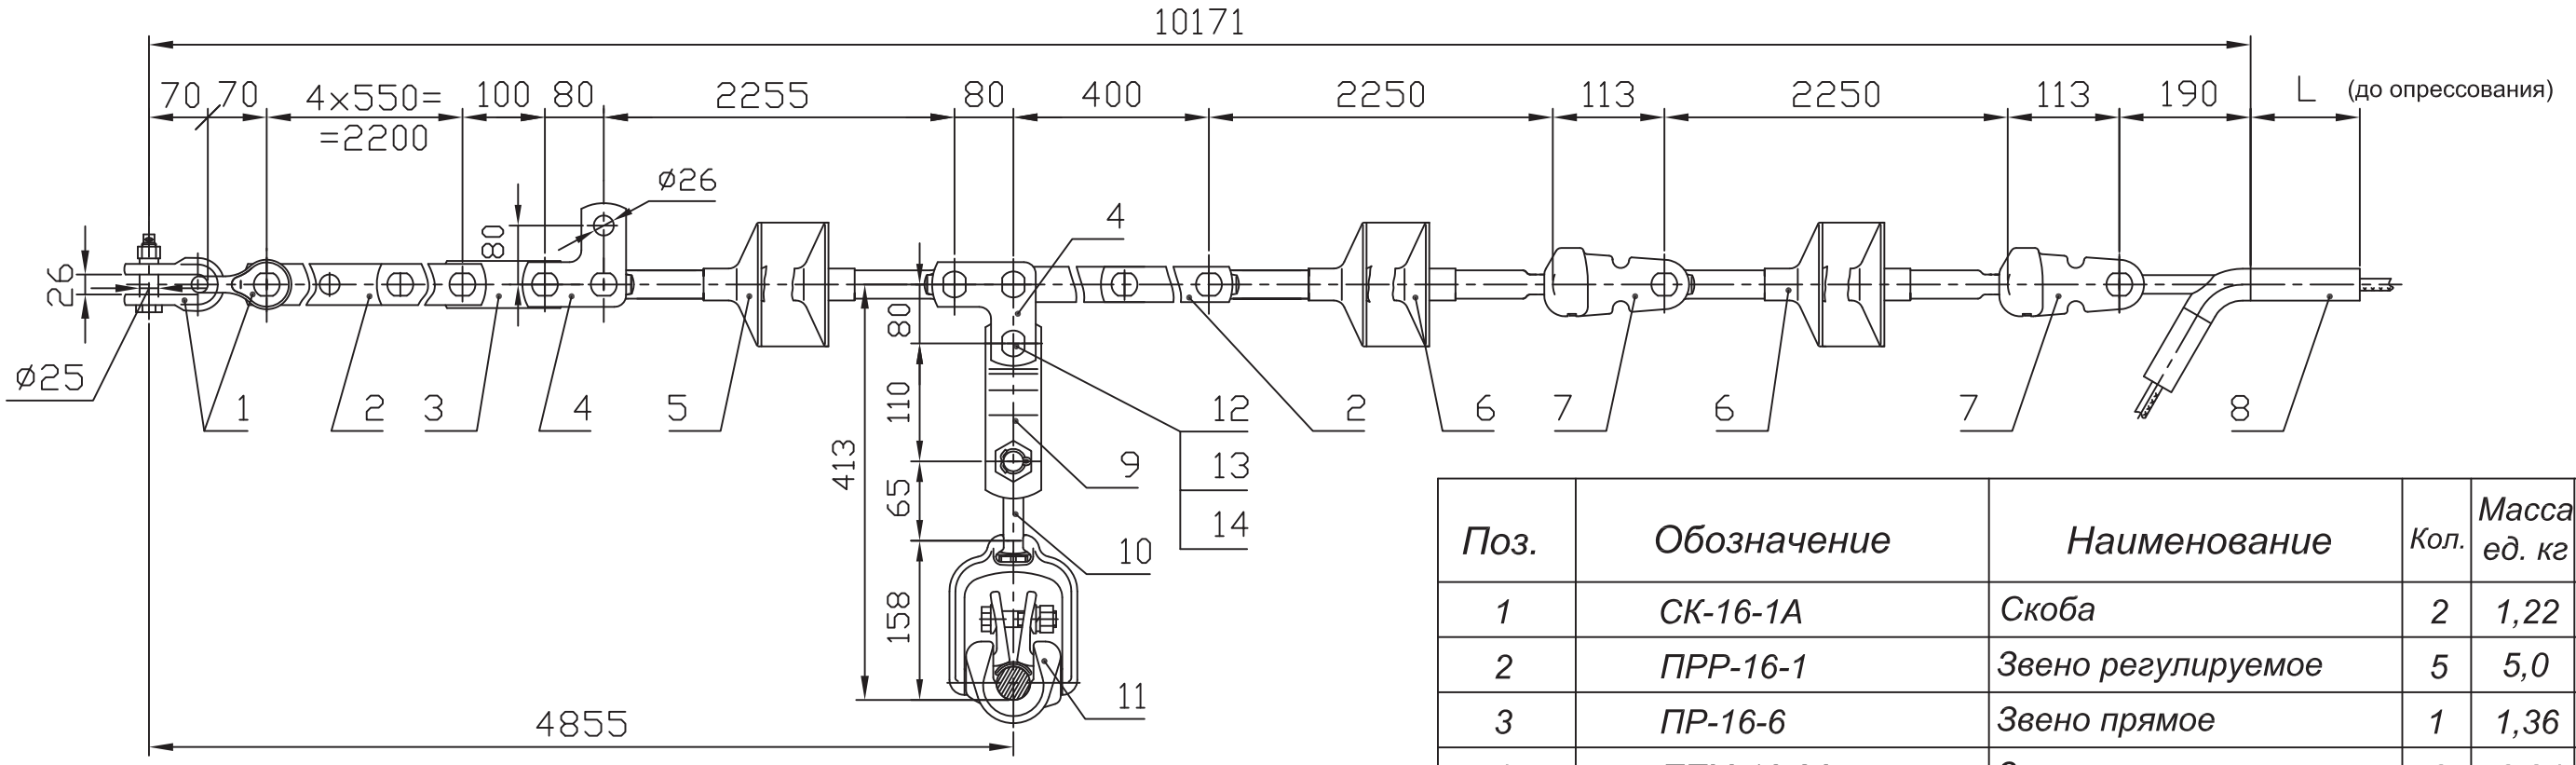

Вариант

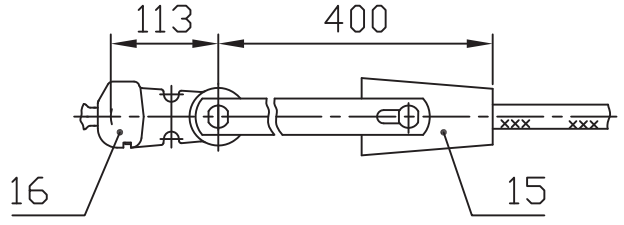

Провод по ГОСТ 839-80		Зажим, поз.8			Масса армат., кг
Марка	Диаметр, мм	Обозначение	L, мм	Масса, кг	
АС300/67	24,5	НАС-300-1Б	165	2,41	47,7
АС400/51	27,5	НАС-450-1Б	210	2,78	48,1

1. *При заказе натяжного клинового зажима типа НК-400-1 (поз.15) следует указывать марку провода. Ушко У2-16-20 (поз.7) заменить на У1-16-20 (поз.16).*


2. ** Масса указана с зажимом НАС-450-1Б и изолятором ЛК 160/220-3.*


Поз.	Обозначение	Наименование	Кол.	Масса ед. кг	Прим.
1	СК-16-1А	Скоба	2	1,22	
2	ПРР-16-1	Звено регулируемое	5	5,0	
3	ПР-16-6	Звено прямое	1	1,36	
4	ПТМ-16-3А	Звено монтажное	2	2,34	
5	ЛК 160/220-	Изолятор исп. СС	1	9,0	
6	ЛК 160/220-	Изолятор исп. СП	2	9,0	
7	У2-16-20	Ушко двухлапчатое	2	2,17	
8	См. таблицу	Зажим натяжной	1	См. табл.	
9	ПРТ-16/12-2	Звено переходное	1	1,5	
10	СР-12-16	Серьга	1	0,41	
11	ПГН-5-3	Зажим поддерживающ.	1	5,3	
12	СТП 2700000-92	Палец 22 х 70	1	0,233	
13	ГОСТ 5915-70	Гайка М20-7Н.4.0112	1	0,064	
14	ГОСТ 397-79	Шплинт 4х28.0112	1	0,003	
15	НК-400-1	Зажим клиновой	1	5,2	
16	У1-16-20	Ушко однолапчатое	1	1,6	
Масса арматуры, кг				См. табл.	
Масса изолирующей подвески, кг				75,1*	

		ЭСИП-0092	
		ЭСС.001 ТМ - т.1	
Утв.	Вигдергауз	Натяжные транспозиционные одноцепные изолирующие с полимерными изоляторами ряда 160 кН подвески проводов АС300/67 и АС400/51 к а/у ж/б опорам ВЛ 220 кВ	Стадия: Р; Лист: ; Листов: 1
Пров.	Липунцов		Филиал ОАО "ФСК ЕЭС" "Электросетьсервис"
Разраб.	Власкина		


Взам. инв. N | Подп. и дата | Инв. N подл.

Формат А3

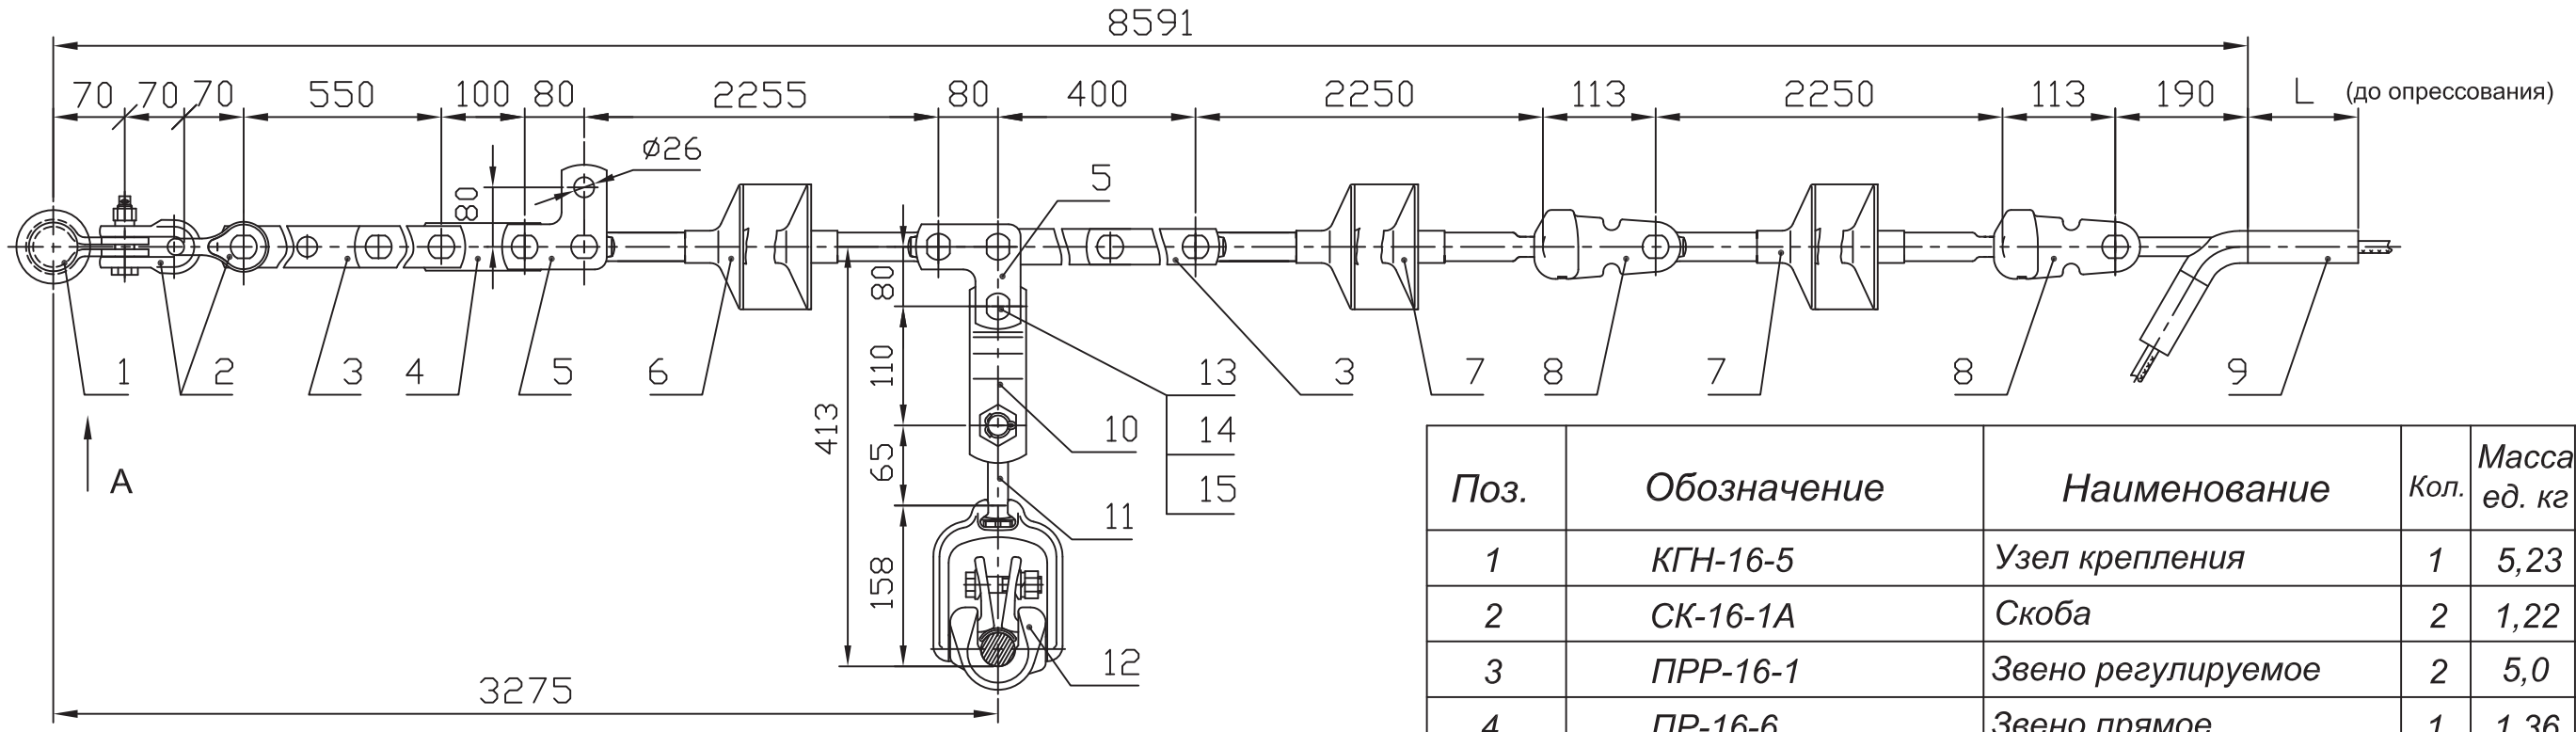

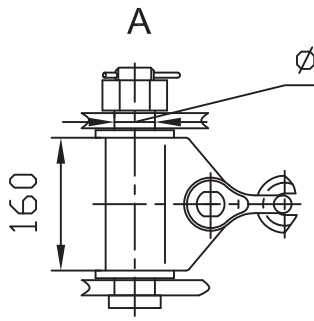

Вариант

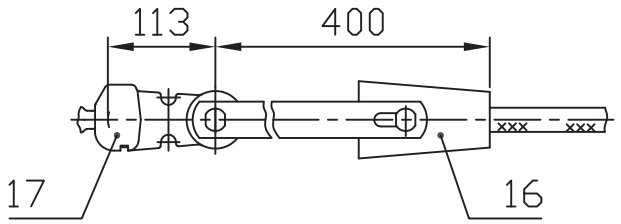

Провод по ГОСТ 839-80		Зажим, поз.9			Масса армат., кг
Марка	Диаметр, мм	Обозначение	L, мм	Масса, кг	
АС300/67	24,5	НАС-300-1Б	165	2,41	38,0
АС400/51	27,5	НАС-450-1Б	210	2,78	38,4

Поз.	Обозначение	Наименование	Кол.	Масса ед. кг	Прим.
1	КГН-16-5	Узел крепления	1	5,23	
2	СК-16-1А	Скоба	2	1,22	
3	ПРР-16-1	Звено регулируемое	2	5,0	
4	ПР-16-6	Звено прямое	1	1,36	
5	ПТМ-16-3А	Звено монтажное	2	2,34	
6	ЛК 160/220-	Изолятор исп. СС	1	9,0	
7	ЛК 160/220-	Изолятор исп. СП	2	9,0	
8	У2-16-20	Ушко двухлапчатое	2	2,17	
9	См. таблицу	Зажим натяжной	1	См. табл.	
10	ПРТ-16/12-2	Звено переходное	1	1,5	
11	СР-12-16	Серьга	1	0,41	
12	ПГН-5-3	Зажим поддерживающ.	1	5,3	
13	СТП 2700000-92	Палец 22 х 70	1	0,233	
14	ГОСТ 5915-70	Гайка М20-7Н.4.0112	1	0,064	
15	ГОСТ 397-79	Шплинт 4х28.0112	1	0,003	
16	НК-400-1	Зажим клиновой	1	5,2	
17	У1-16-20	Ушко однолапчатое	1	1,6	
Масса арматуры, кг				См. табл.	
Масса изолирующей подвески, кг				65,4*	


1. *При заказе натяжного клинового зажима типа НК-400-1 (поз.16) следует указывать марку провода. Ушко У2-16-20 (поз.8) заменить на У1-16-20 (поз.17).*


2. ** Масса указана с зажимом НАС-450-1Б и изолятором ЛК 160/220-3.*

			ЭСИП-0093
			ЭСС.001 ТМ - т.1
Утв.	Вигдергауз		Натяжные транспозиционные одноцепные изолирующие с полимерными изоляторами ряда 160 кН подвески проводов АС300/67 и АС400/51 к а/у металлическим опорам ВЛ 220 кВ
Пров.	Липунцов		Стадия: Р; Лист: ; Листов: 1
Разраб.	Власкина		Филиал ОАО "ФСК ЕЭС" "Электросетьсервис"


Взам. инв. N | Подп. и дата | Инв. N подл.

Формат А3

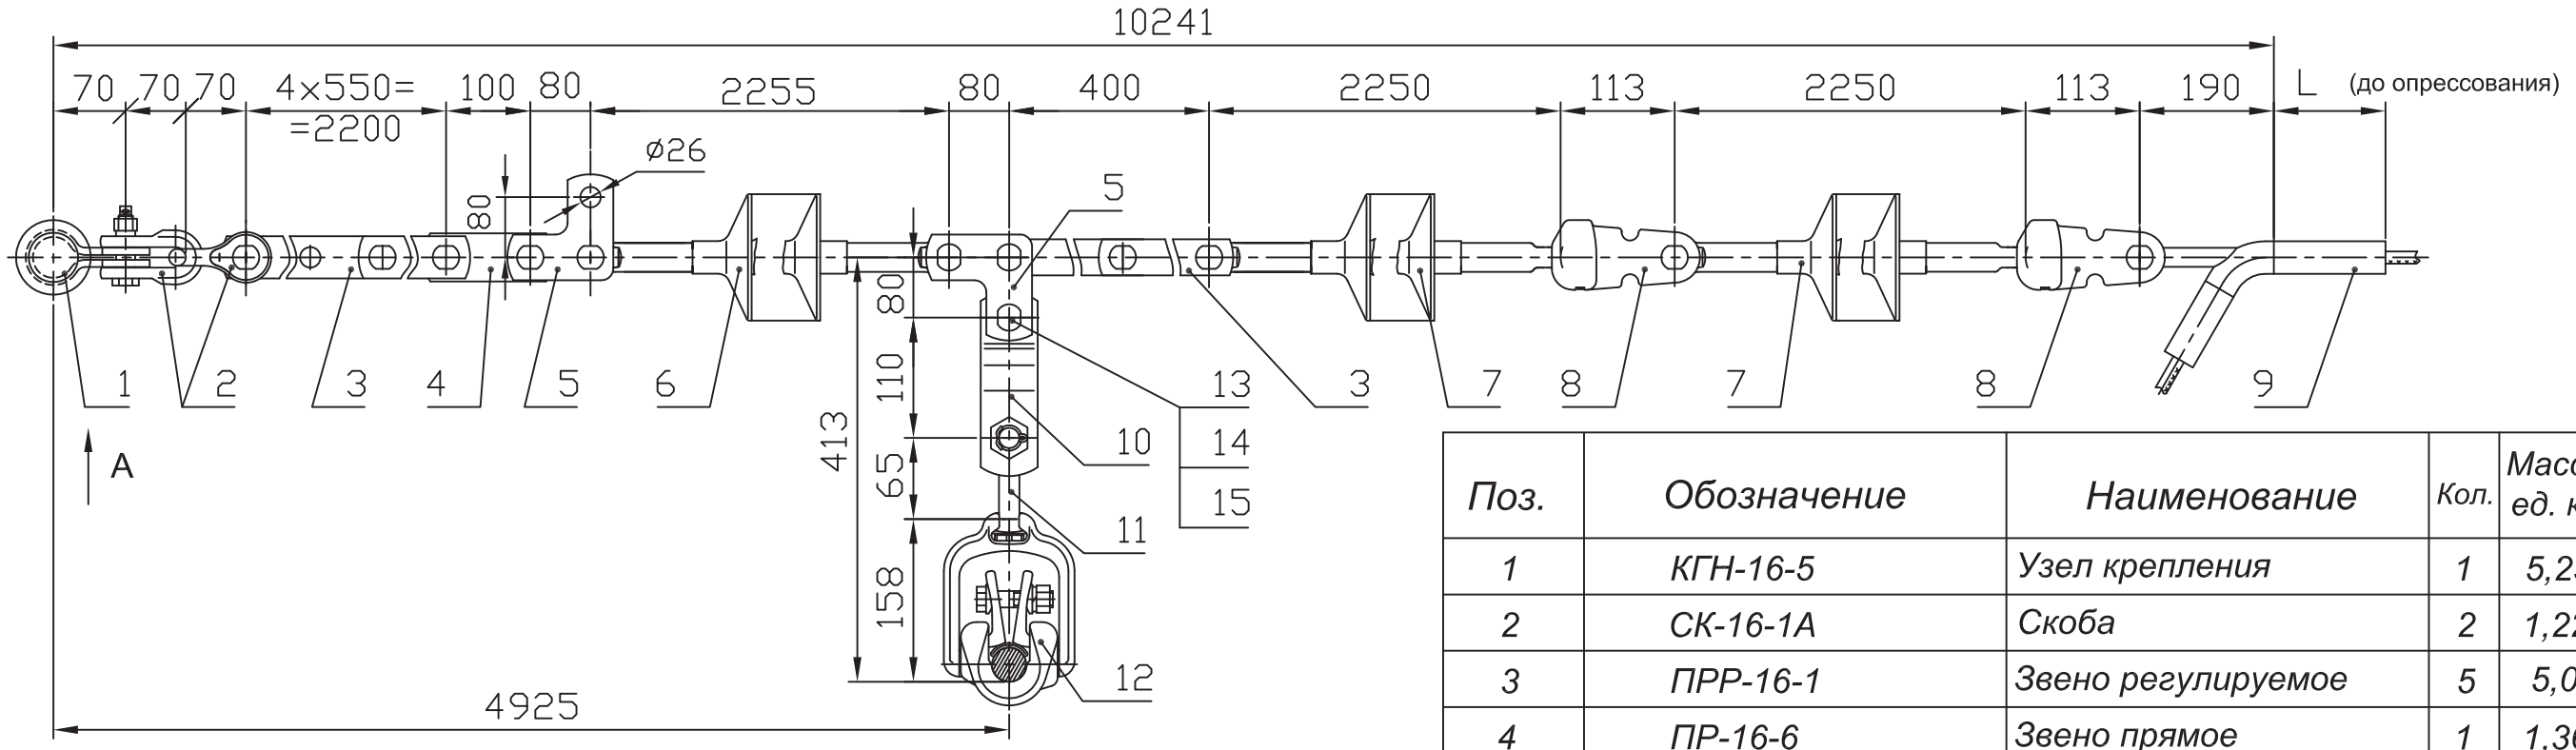

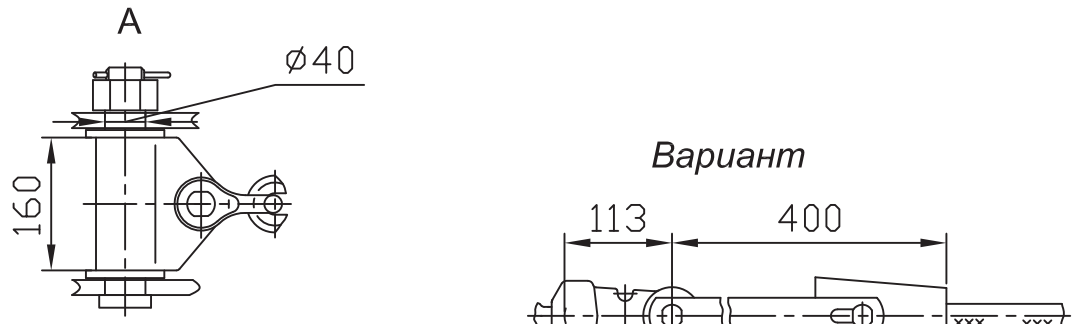

Вариант

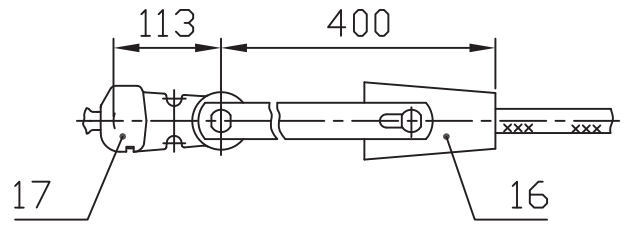

Провод по ГОСТ 839-80		Зажим, поз.9			Масса армат., кг
Марка	Диаметр, мм	Обозначение	L, мм	Масса, кг	
АС300/67	24,5	НАС-300-1Б	165	2,41	53,0
АС400/51	27,5	НАС-450-1Б	210	2,78	53,4

1. При заказе натяжного клинового зажима типа НК-400-1 (поз.16) следует указывать марку провода. Ушко У2-16-20 (поз.8) заменить на У1-16-20 (поз.17).

2. * Масса указана с зажимом НАС-450-1Б и изолятором ЛК 160/220-3.

Поз.	Обозначение	Наименование	Кол.	Масса ед. кг	Прим.
1	КГН-16-5	Узел крепления	1	5,23	
2	СК-16-1А	Скоба	2	1,22	
3	ПРР-16-1	Звено регулируемое	5	5,0	
4	ПР-16-6	Звено прямое	1	1,36	
5	ПТМ-16-3А	Звено монтажное	2	2,34	
6	ЛК 160/220-	Изолятор исп. СС	1	9,0	
7	ЛК 160/220-	Изолятор исп. СП	2	9,0	
8	У2-16-20	Ушко двухлапчатое	2	2,17	
9	См. таблицу	Зажим натяжной	1	См. табл.	
10	ПРТ-16/12-2	Звено переходное	1	1,5	
11	СР-12-16	Серьга	1	0,41	
12	ПГН-5-3	Зажим поддерживающ.	1	5,3	
13	СТП 2700000-92	Палец 22 х 70	1	0,233	
14	ГОСТ 5915-70	Гайка М20-7Н.4.0112	1	0,064	
15	ГОСТ 397-79	Шплинт 4х28.0112	1	0,003	
16	НК-400-1	Зажим клиновой	1	5,2	
17	У1-16-20	Ушко однолапчатое	1	1,6	
Масса арматуры, кг				См. табл.	
Масса изолирующей подвески, кг				80,4*	

ЭСИП-0094

ЭСС.001 ТМ - т.1

Утв.	Вигдергауз		
Пров.	Липунцов		
Разраб.	Власкина		


Натяжные транспозиционные одноцепные изолирующие с полимерными изоляторами ряда 160 кН подвески проводов АС240/56 и АС330/43 к а/у ж/б опорам ВЛ 220 кВ

Стадия	Лист	Листов
Р		1


Филиал ОАО "ФСК ЕЭС" "Электросетьсервис"

Взам. инв. N | Подп. и дата | Инв. N подл.

Формат А3

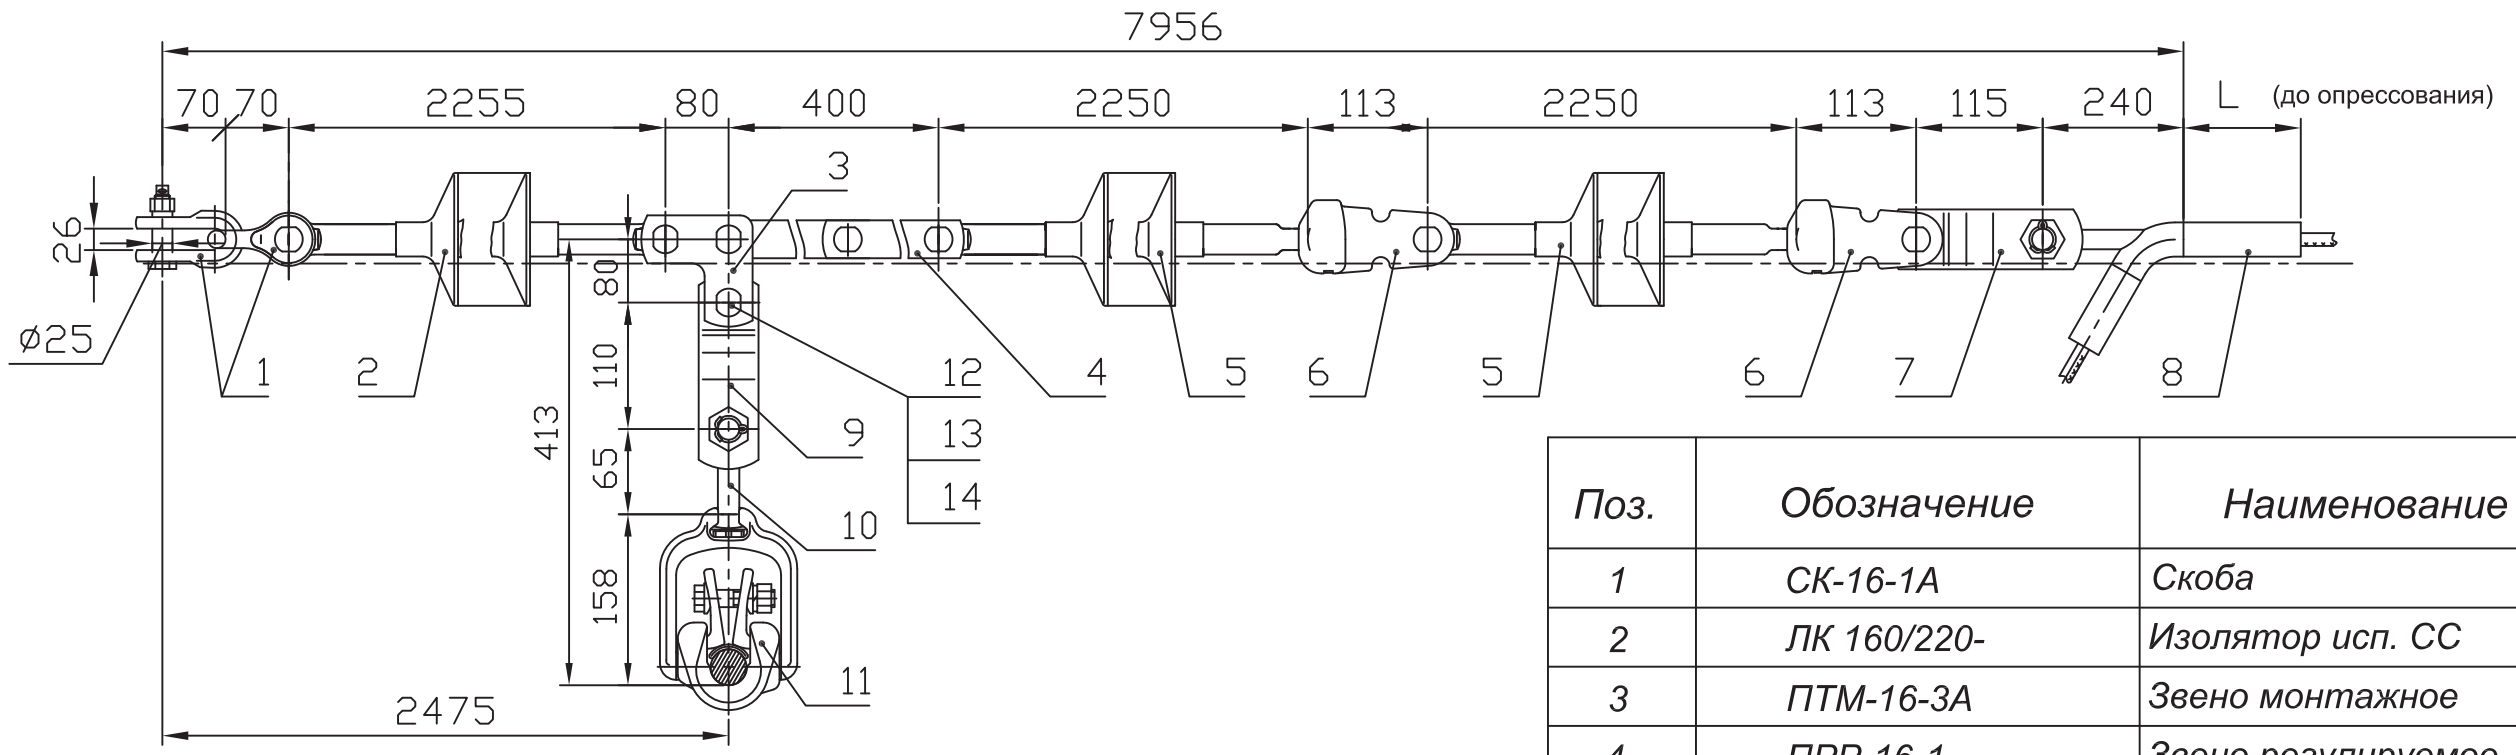

Вариант

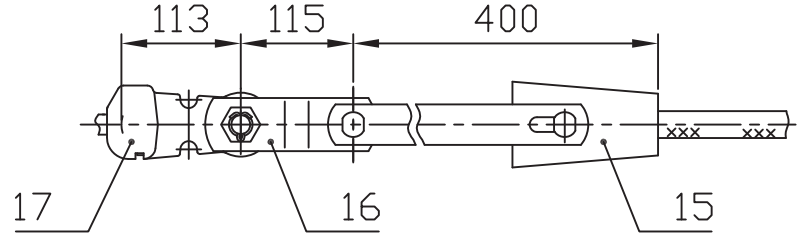

Провод по ГОСТ 839-80		Зажим, поз.8			Масса армат., кг
Марка	Диаметр, мм	Обозначение	L, мм	Масса, кг	
АС400/93	29,1	НАС-600-2Б	225	3,99	27,5
АС500/64	30,6	НАС-600-1Б	240	4,65	28,2

1. При заказе натяжного клинового зажима типа НК-500-1 (поз.15) следует указывать марку провода. Ушко У2-16-20 (поз.6) заменить на У1-16-20 (поз.17), а звено ПРТ-16/21-2 (поз.7) на ПРТ-21/16-2 (поз.16).


2. * Масса указана с зажимом НАС-600-1Б и изолятором ЛК 160/220-3.

Поз.	Обозначение	Наименование	Кол.	Масса ед. кг	Прим.
1	СК-16-1А	Скоба	2	1,22	
2	ЛК 160/220-	Изолятор исп. СС	1	9,0	
3	ПТМ-16-3А	Звено монтажное	1	2,34	
4	ПРР-16-1	Звено регулируемое	1	5,0	
5	ЛК 160/220-	Изолятор исп. СП	2	9,0	
6	У2-16-20	Ушко двухлапчатое	2	2,17	
7	ПРТ-16/21-2	Звено переходное	1	1,9	
8	См. таблицу	Зажим натяжной	1	См. табл.	
9	ПРТ-16/12-2	Звено переходное	1	1,5	
10	СР-12-16	Серьга	1	0,41	
11	ПГН-5-3	Зажим поддерживающ.	1	5,3	
12	СТП 2700000-92	Палец 22 х 70	1	0,233	
13	ГОСТ 5915-70	Гайка М20-7Н.4.0112	1	0,064	
14	ГОСТ 397-79	Шплинт 4х28.0112	1	0,003	
15	НК-500-1	Зажим клиновой	1	5,3	
16	ПРТ-21/16-2	Звено переходное	1	1,8	
17	У1-16-20	Ушко однолапчатое	1	1,6	
Масса арматуры, кг				См. табл.	
Масса изолирующей подвески, кг				55,2*	


Взам. инв. N | Подп. и дата | Инв. N подл.

		ЭСИП-0095	
		ЭСС.001 ТМ - т.1	
Утв.	Вигдергауз	Натяжные транспозиционные одноцепные изолирующие с полимерными изоляторами ряда 160 кН подвески проводов АС400/93 и АС500/64 к а/у деревянным опорам ВЛ 220 кВ	Стадия: Р; Лист: ; Листов: 1
Пров.	Липунцов		Филиал ОАО "ФСК ЕЭС" "Электросетьсервис"
Разраб.	Власкина		

Формат А3

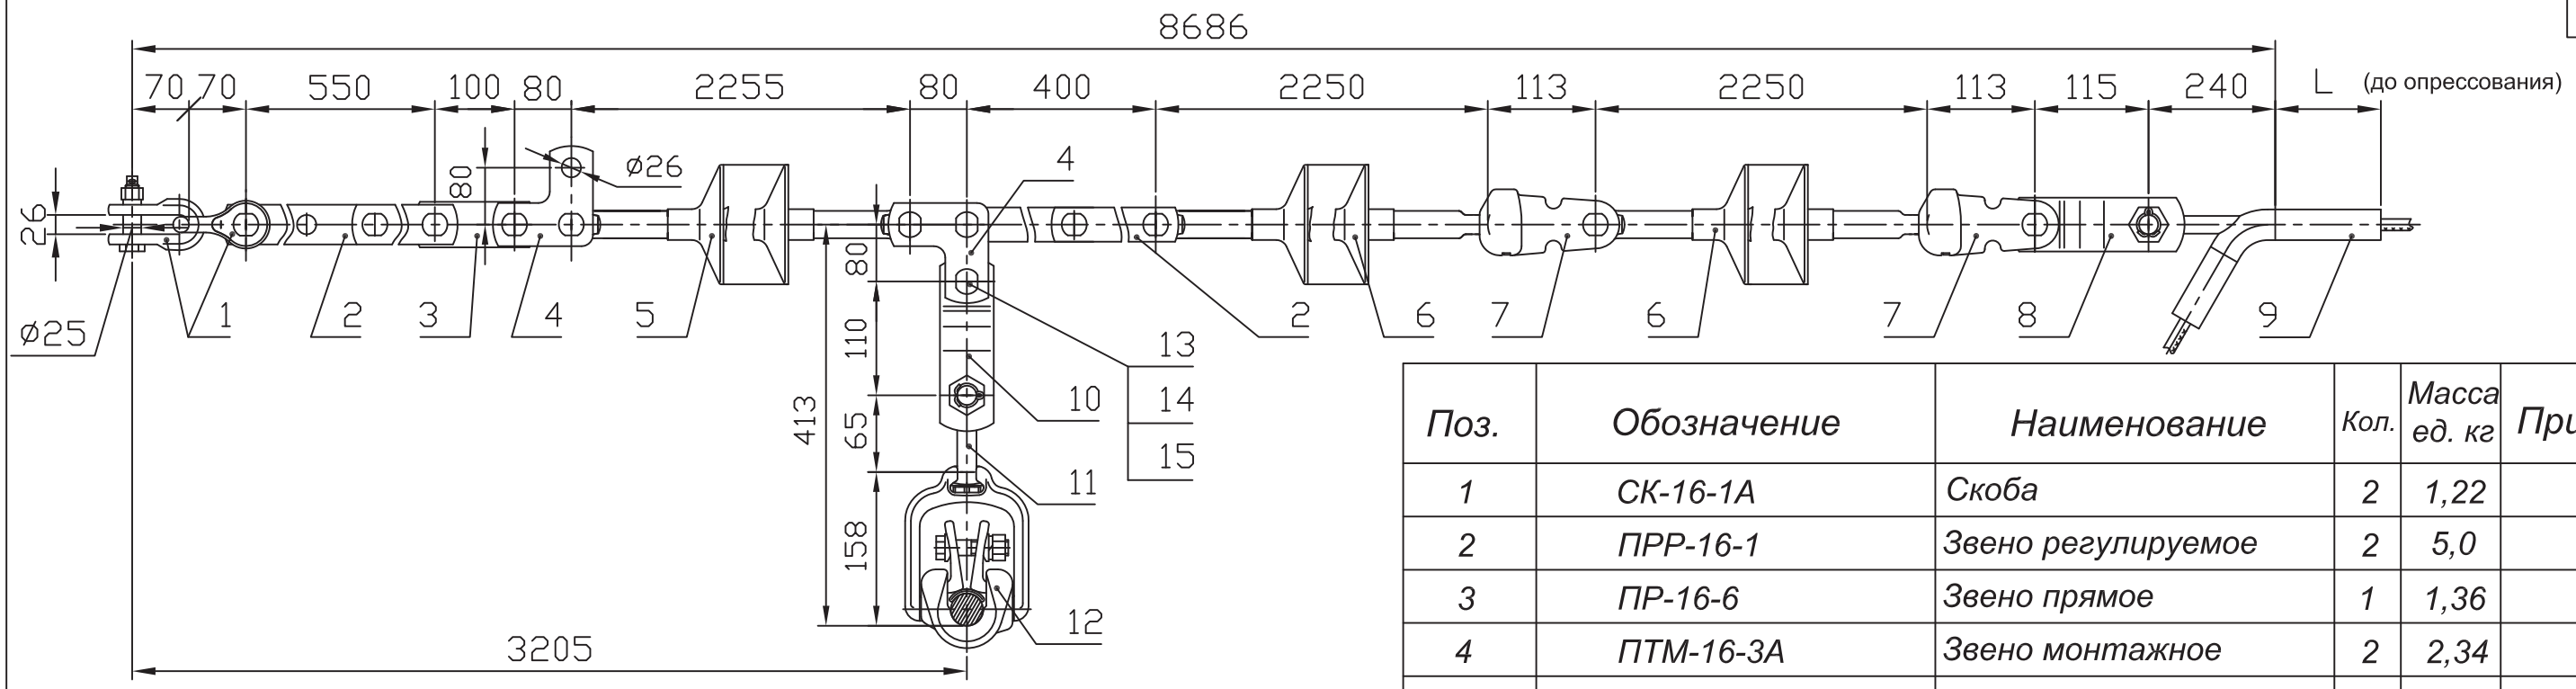

Вариант

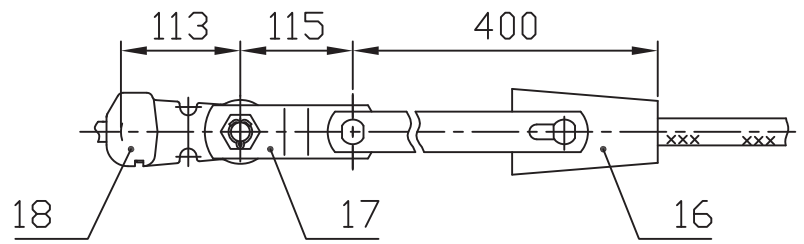

Провод по ГОСТ 839-80		Зажим, поз.10			Масса армат., кг
Марка	Диаметр, мм	Обозначение	L, мм	Масса, кг	
АС400/93	29,1	НАС-600-2Б	225	3,99	36,2
АС500/64	30,6	НАС-600-1Б	240	4,65	36,9

Поз.	Обозначение	Наименование	Кол.	Масса ед. кг	Прим.
1	СК-16-1А	Скоба	2	1,22	
2	ПРР-16-1	Звено регулируемое	2	5,0	
3	ПР-16-6	Звено прямое	1	1,36	
4	ПТМ-16-3А	Звено монтажное	2	2,34	
5	ЛК 160/220-	Изолятор исп. СС	1	9,0	
6	ЛК 160/220-	Изолятор исп. СП	2	9,0	
7	У2-16-20	Ушко двухлапчатое	2	2,17	
8	ПРТ-16/21-2	Звено переходное	1	1,9	
9	См. таблицу	Зажим натяжной	1	См. табл.	
10	ПРТ-16/12-2	Звено переходное	1	1,5	
11	СР-12-16	Серьга	1	0,41	
12	ПГН-5-3	Зажим поддерживающ.	1	5,3	
13	СТП 2700000-92	Палец 22 х 70	1	0,233	
14	ГОСТ 5915-70	Гайка М20-7Н.4.0112	1	0,064	
15	ГОСТ 397-79	Шплинт 4х28.0112	1	0,003	
16	НК-500-1	Зажим клиновой	1	5,3	
17	ПРТ-21/16-2	Звено переходное	1	1,8	
18	У1-16-20	Ушко однолапчатое	1	1,6	
Масса арматуры, кг				См. табл.	
Масса изолирующей подвески, кг				63,9*	


1. *При заказе натяжного клинового зажима типа НК-500-1 (поз.16) следует указывать марку провода. Ушко У2-16-20 (поз.7) заменить на У1-16-20 (поз.18), а звено ПРТ-16/21-2 (поз.8) на ПРТ-21/16-2 (поз.17).*


2. ** Масса указана с зажимом НАС-600-1Б и изолятором ЛК 160/220-3.*

		ЭСИП-0096	
		ЭСС.001 ТМ - т.1	
Утв.	Вигдергауз	Натяжные транспозиционные одноцепные изолирующие с полимерными изоляторами ряда 160 кН подвески проводов АС400/56 и АС500/64 к а/у деревянным опорам ВЛ 220 кВ	Стадия: Р; Лист: ; Листов: 1
Пров.	Липунцов		Филиал ОАО "ФСК ЕЭС" "Электросетьсервис"
Разраб.	Власкина		

Взам. инв. N | Подп. и дата | Инв. N подл.

Формат А3

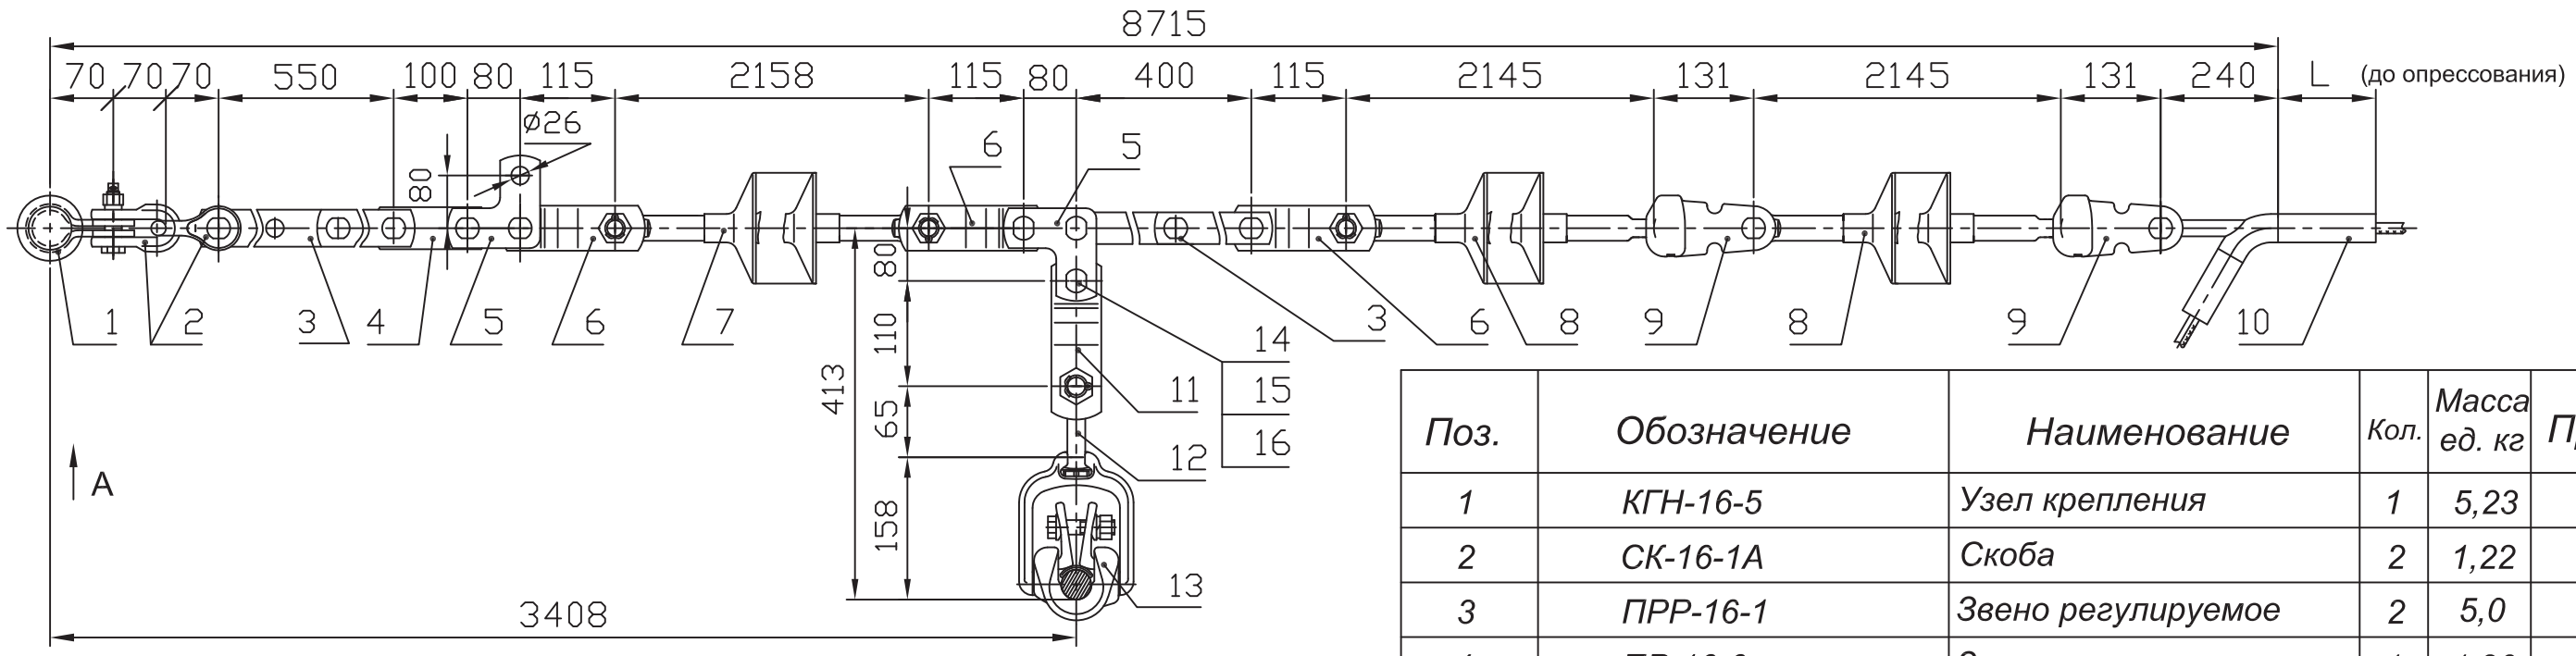

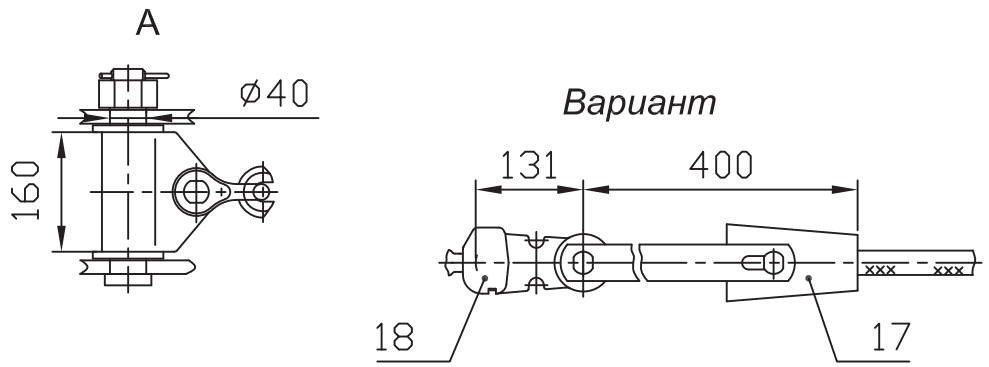

Провод по ГОСТ 839-80		Зажим, поз.10			Масса армат., кг
Марка	Диаметр, мм	Обозначение	L, мм	Масса, кг	
АС400/93	29,1	НАС-600-2Б	225	3,99	48,1
АС500/64	30,6	НАС-600-1Б	240	4,65	48,7

1. При заказе натяжного клинового зажима типа НК-500-1 (поз.17) следует указывать марку провода. Ушко У2-21-20 (поз.9) заменить на У1-21-20 (поз.18).

2. * Масса указана с зажимом НАС-600-1Б и изолятором ЛК 210/220-3.

Поз.	Обозначение	Наименование	Кол.	Масса ед. кг	Прим.
1	КГН-16-5	Узел крепления	1	5,23	
2	СК-16-1А	Скоба	2	1,22	
3	ПРР-16-1	Звено регулируемое	2	5,0	
4	ПР-16-6	Звено прямое	1	1,36	
5	ПТМ-16-3А	Звено монтажное	2	2,34	
6	ПРТ-16/21-2	Звено переходное	3	1,9	
7	ЛК 210/220-	Изолятор исп. СС	1	11,0	
8	ЛК 210/220-	Изолятор исп. СП	2	11,0	
9	У2-21-20	Ушко двухлапчатое	2	3,58	
10	См. таблицу	Зажим натяжной	1	См. табл.	
11	ПРТ-16/12-2	Звено переходное	1	1,5	
12	СР-12-16	Серьга	1	0,41	
13	ПГН-5-3	Зажим поддерживающ.	1	5,3	
14	СТП 2700000-92	Палец 22 х 70	1	0,233	
15	ГОСТ 5915-70	Гайка М20-7Н.4.0112	1	0,064	
16	ГОСТ 397-79	Шплинт 4х28.0112	1	0,003	
17	НК-500-1	Зажим клиновой	1	5,3	
18	У1-21-20	Ушко однолапчатое	1	2,23	
Масса арматуры, кг					См. табл.
Масса изолирующей подвески, кг					81,7*


ЭСИП-0097


ЭСС.001 ТМ - т.1


Утв.	Вигдергауз	Натяжные транспозиционные одноцепные изолирующие с полимерными изоляторами ряда 210 кН подвески проводов АС400/93 и АС500/61 к а/у металлическим опорам ВЛ 220 кВ	Стадия: Р; Лист: ; Листов: 1
Пров.	Липунцов		Филиал ОАО "ФСК ЕЭС" "Электросетьсервис"
Разраб.	Власкина		

Формат А3

Взам. инв. N | Подп. и дата | Инв. N подл.

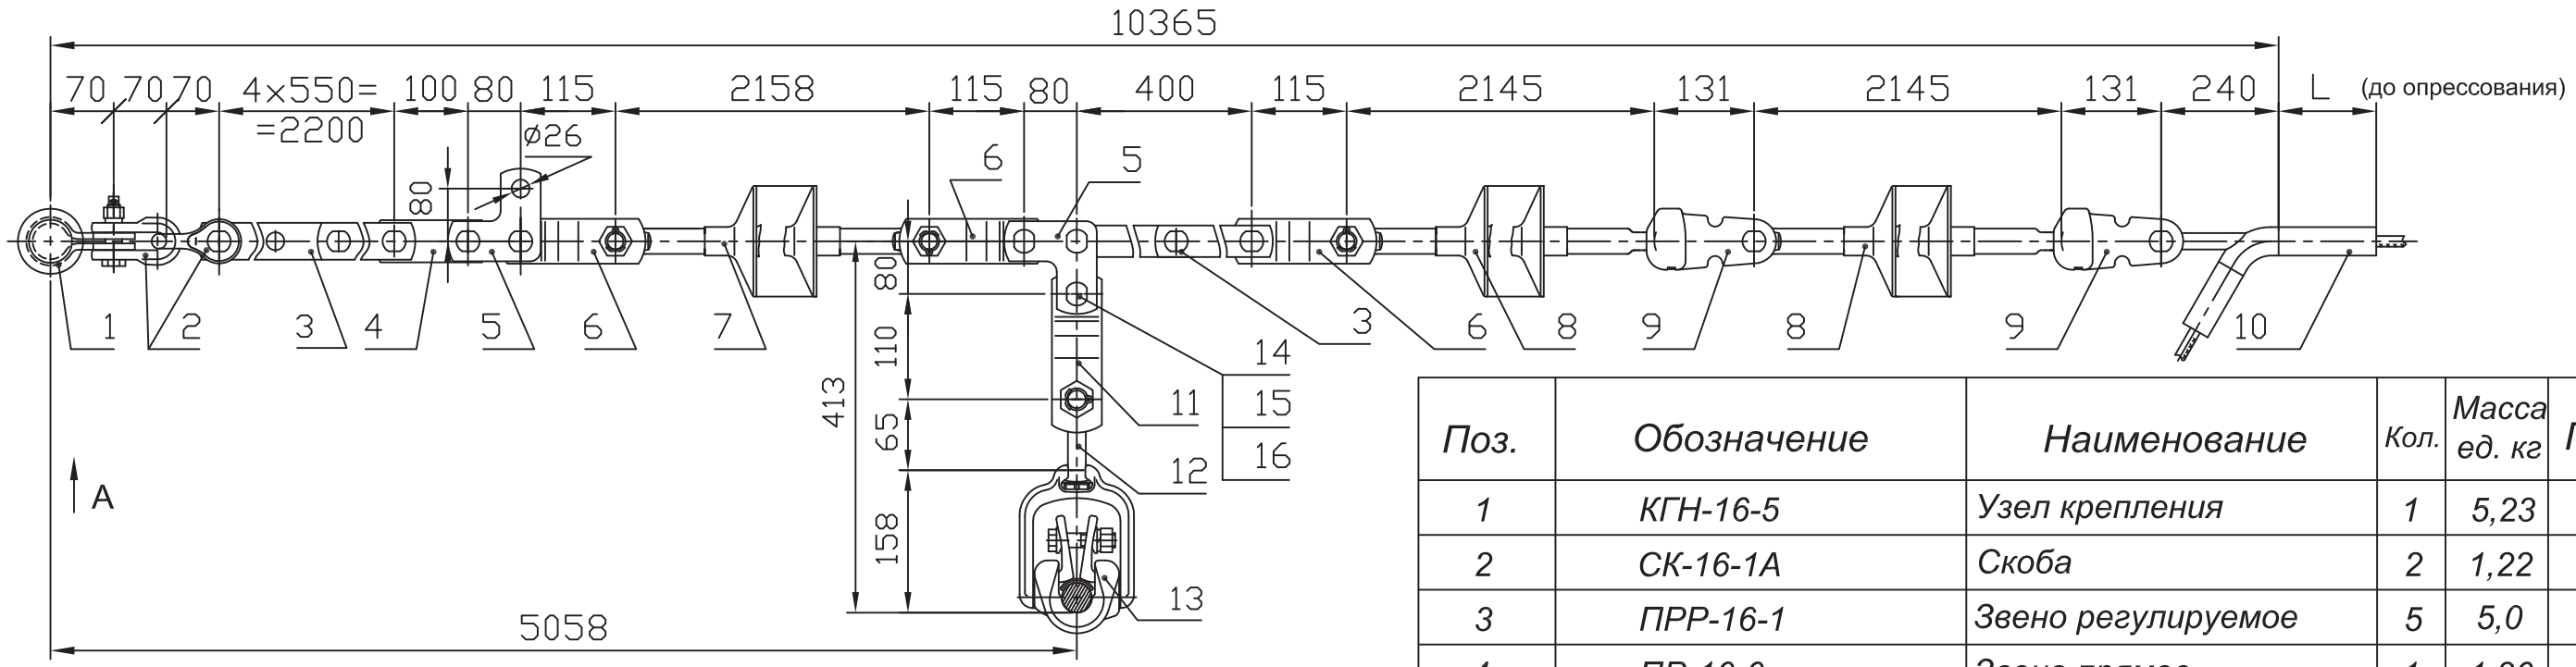

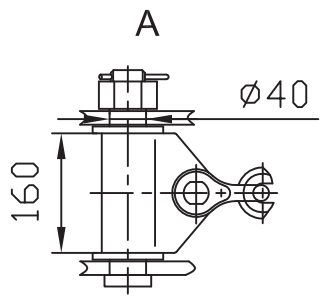

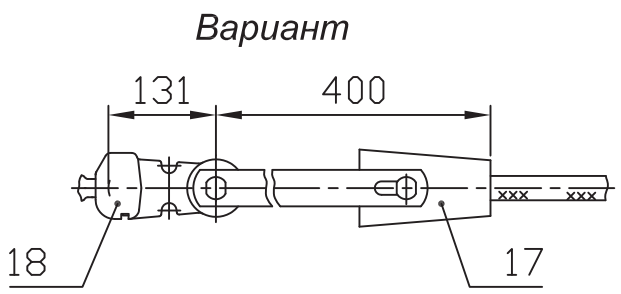

Провод по ГОСТ 839-80		Зажим, поз.10			Масса армат., кг
Марка	Диаметр, мм	Обозначение	L, мм	Масса, кг	
АС400/93	29,1	НАС-600-2Б	225	3,99	63,0
АС500/64	30,6	НАС-600-1Б	240	4,65	63,7

1. При заказе натяжного клинового зажима типа НК-500-1 (поз.17) следует указывать марку провода. Ушко У2-21-20 (поз.9) заменить на У1-21-20 (поз.18).


2. * Масса указана с зажимом НАС-600-1Б и изолятором ЛК 210/220-3.


Поз.	Обозначение	Наименование	Кол.	Масса ед. кг	Прим.
1	КГН-16-5	Узел крепления	1	5,23	
2	СК-16-1А	Скоба	2	1,22	
3	ПРР-16-1	Звено регулируемое	5	5,0	
4	ПР-16-6	Звено прямое	1	1,36	
5	ПТМ-16-3А	Звено монтажное	2	2,34	
6	ПРТ-16/21-2	Звено переходное	3	1,9	
7	ЛК 210/220-	Изолятор исп. СС	1	11,0	
8	ЛК 210/220-	Изолятор исп. СП	2	11,0	
9	У2-21-20	Ушко двухлапчатое	2	3,58	
10	См. таблицу	Зажим натяжной	1	См. табл.	
11	ПРТ-16/12-2	Звено переходное	1	1,5	
12	СР-12-16	Серьга	1	0,41	
13	ПГН-5-3	Зажим поддерживающ.	1	5,3	
14	СТП 2700000-92	Палец 22 х 70	1	0,233	
15	ГОСТ 5915-70	Гайка М20-7Н.4.0112	1	0,064	
16	ГОСТ 397-79	Шплинт 4х28.0112	1	0,003	
17	НК-500-1	Зажим клиновой	1	5,3	
18	У1-21-20	Ушко однолапчатое	1	2,23	
Масса арматуры, кг					См. табл.
Масса изолирующей подвески, кг					96,7*

		ЭСИП-0098	
		ЭСС.001 ТМ - т.1	
Утв.	Вигдергауз	Натяжные транспозиционные одноцепные изолирующие с полимерными изоляторами ряда 210 кН подвески проводов АС400/93 и АС500/61 к а/у металлическим опорам ВЛ 220 кВ	Стадия: Р; Лист: ; Листов: 1
Пров.	Липунцов		Филиал ОАО "ФСК ЕЭС" "Электросетьсервис"
Разраб.	Власкина		


Взам. инв. N | Подп. и дата | Инв. N подл.

Формат А3

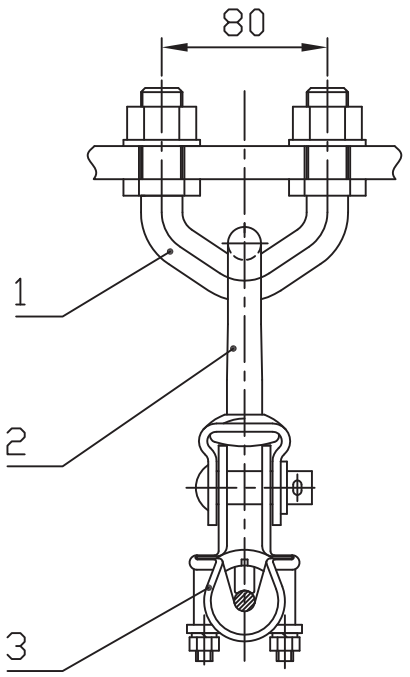

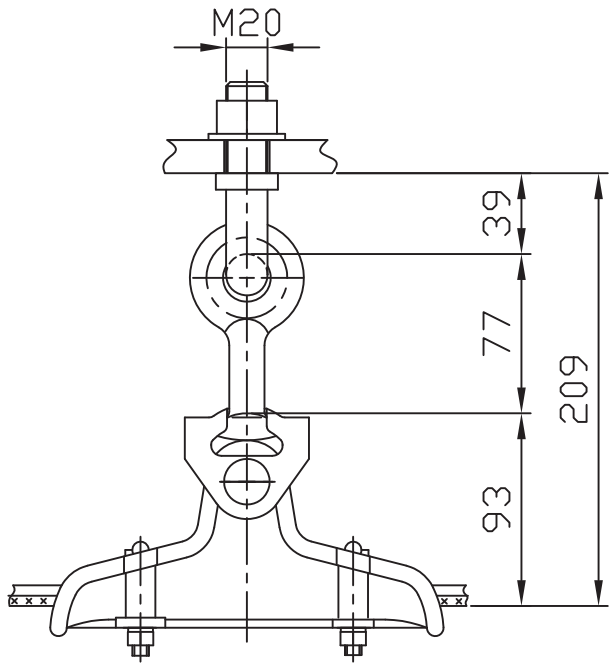

Вариант крепления троса с заземлением

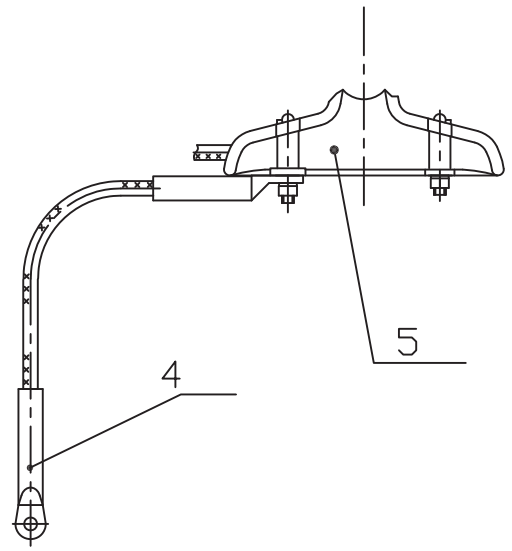

Напряжение ВЛ, кВ	Трос (стальной канат по ГОСТ 3062-80)		Зажим заземляющий, поз. 4	
	Марка	Диаметр, мм	Обозначение	Масса, кг
35	С 35	7,8	ЗПС-35-3Г	0,057
110	С 50	9,2	ЗПС-50-3Г	0,068

Поз.	Обозначение	Наименование	Кол.	Масса ед. кг	Прим.
1	КГП-16-3	Узел крепления	1	0,81	
2	СРС-7-16	Серьга	1	0,32	
3	ПГГ-25/6-12	Зажим поддерживающ.	1	1,21	
4	См. таблицу	Зажим заземляющий	2	см.табл.	для варианта
5	ПГГ-25/6-12А	Зажим поддерживающий	1	1,21	для варианта
Масса арматуры, кг				2,34	

Взам. инв. N

Подп. и дата


Инв. N подл.


				ЭСИП-0099
				ЭСС.001 ТМ - т.1
Утв.	Вигдергауз			Поддерживающее неизолированное крепление троса С 35, С 50 к ж/б опорам ВЛ 35, 110 кВ
Пров.	Липунцов			
Разраб.	Власкина			

Стадия	Лист	Листов
Р		1


Филиал ОАО "ФСК ЕЭС" "Электросетьсервис"

Формат А3

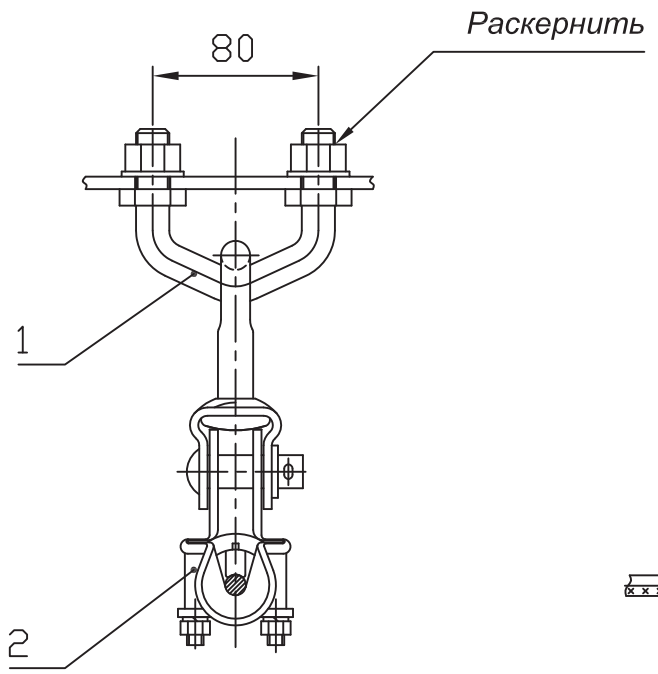

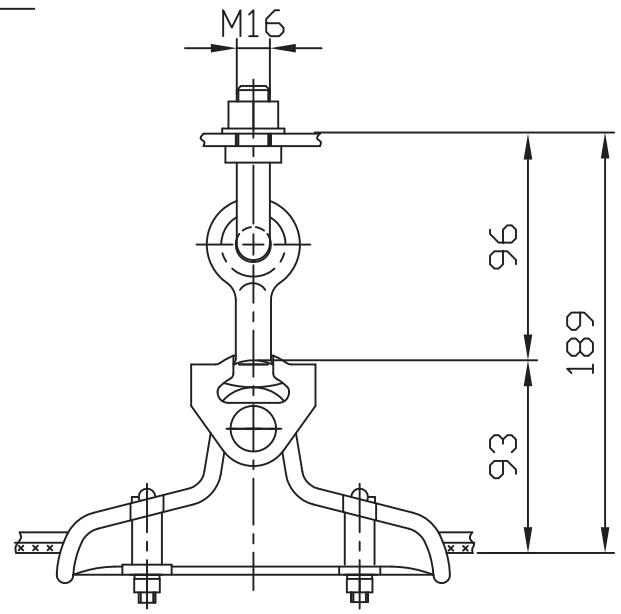

Вариант крепления троса с заземлением

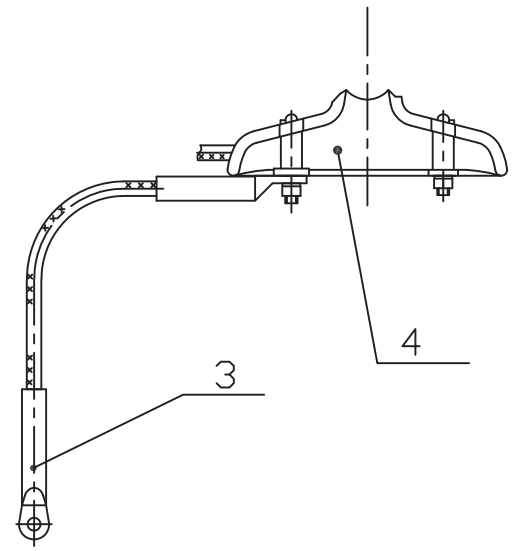

Напряжение ВЛ, кВ	Трос (стальной канат по ГОСТ 3062-80)		Зажим заземляющий, поз. 4	
	Марка	Диаметр, мм	Обозначение	Масса, кг
35	С 35	7,8	ЗПС-35-3Г	0,057
110	С 50	9,2	ЗПС-50-3Г	0,068

Поз.	Обозначение	Наименование	Кол.	Масса ед. кг	Прим.
1	КГП-7-2В	Узел крепления	1	0,70	
2	ПГГ-25/6-12	Зажим поддерживающ.	1	1,21	
3	См. таблицу	Зажим заземляющий.	2	см.табл.	для варианта
4	ПГГ-25/6-12	Зажим поддерживающ.	1	1,21	для варианта
Масса арматуры, кг				1,91	


				ЭСИП-0100
				ЭСС.001 ТМ - т.1
Утв.	Вигдергауз			Поддерживающее неизолированное крепление троса С 35, С 50 к ж/б опорам ВЛ 35, 110 кВ
Пров.	Липунцов			
Разраб.	Власкина			

Стадия	Лист	Листов
Р		1

Филиал ОАО "ФСК ЕЭС" "Электросетьсервис"


Взам. инв. N | Подп. и дата | Инв. N подл.

Формат А3

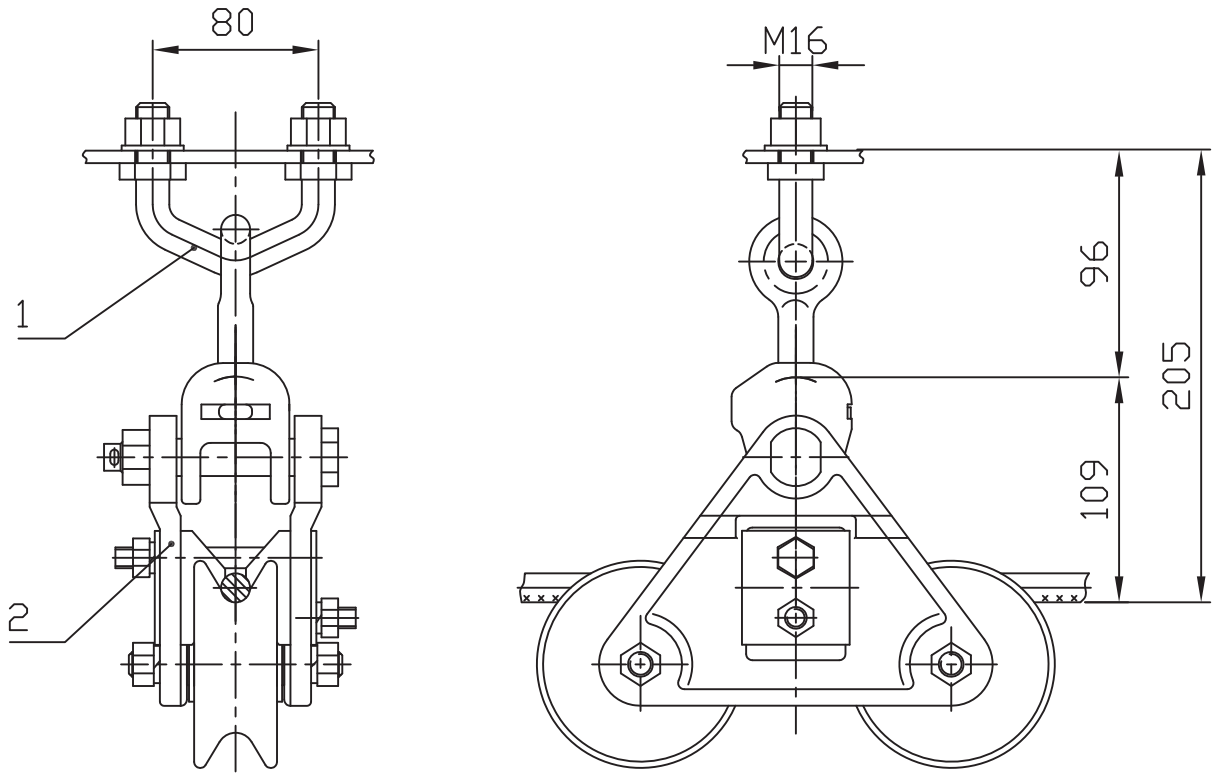

Поз.	Обозначение	Наименование	Кол.	Масса ед. кг	Прим.
1	КГП-7-2В	Узел крепления	1	0,70	
2	ПГУ-2-1	Зажим поддерживающ.	1	3,1	
3	ПС-2-1	Зажим плашечный.	1	0,42	для варианта
4	ЗПС-50-3Г	Зажим заземляющ.	1	0,068	для варианта
Масса арматуры, кг				3,8	

Вариант крепления троса с заземлением

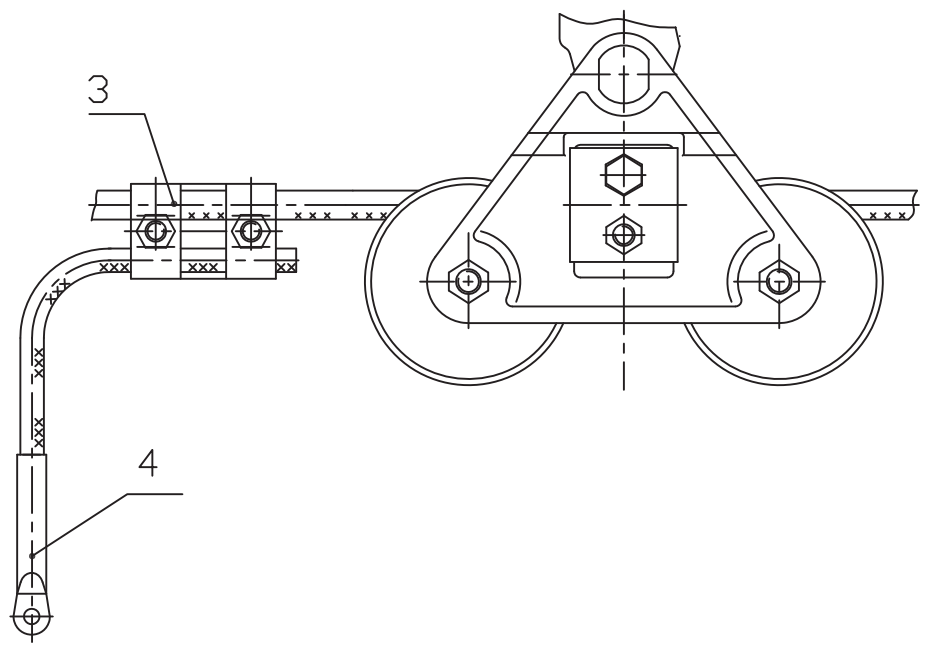

Взам. инв. N

Подп. и дата


Инв. N подл.

				ЭСИП-0101
				ЭСС.001 ТМ - т.1
Утв.	Вигдергауз			Поддерживающее неизолированное крепление троса С 50 к ж/б опорам ВЛ 110 кВ
Пров.	Липунцов			
Разраб.	Власкина			

Стадия	Лист	Листов
Р		1


Филиал ОАО "ФСК ЕЭС" "Электросетьсервис"

Формат А3

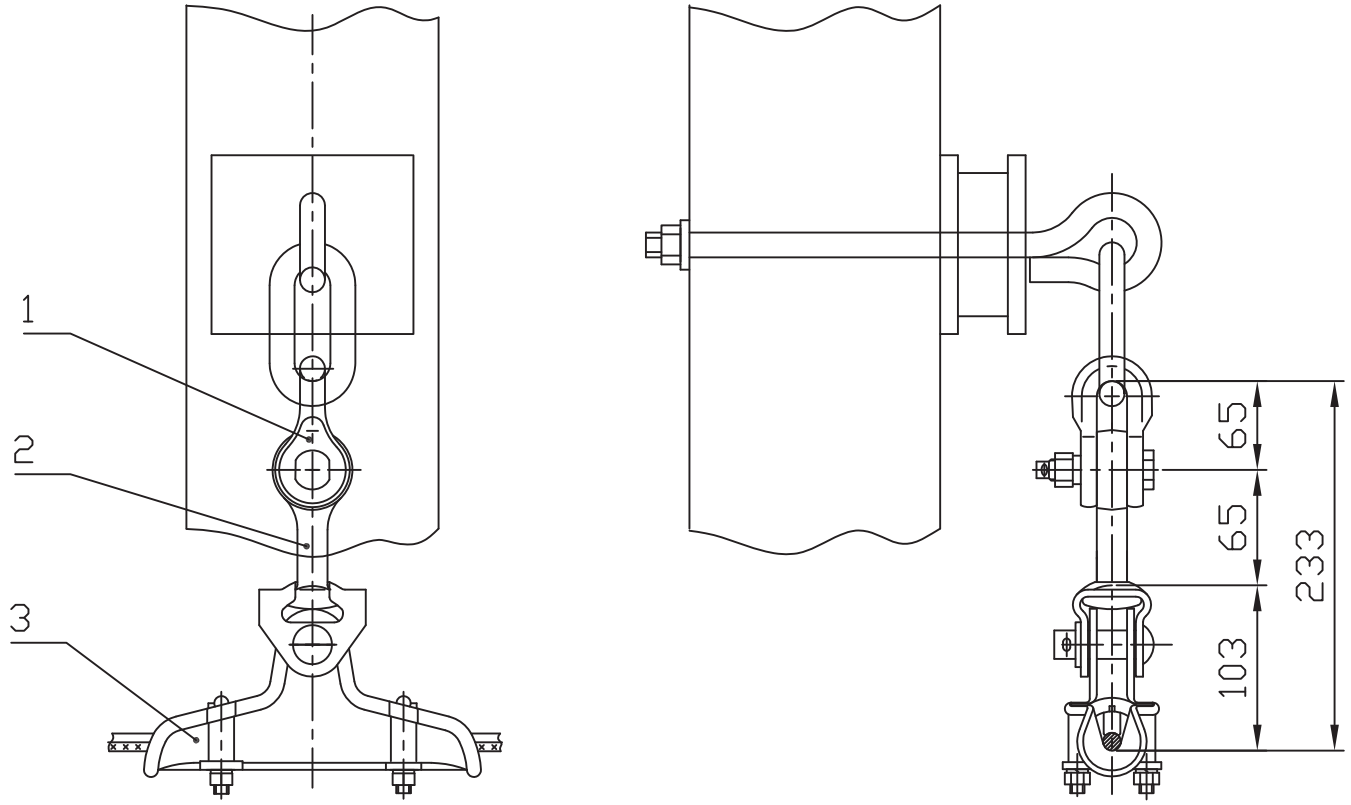

Поз.	Обозначение	Наименование	Кол.	Масса ед. кг	Прим.
1	СК-12-1А	Скоба	1	0,92	
2	СР-12-16	Серьга	1	0,41	
3	ПГГ-25/6-12	Зажим поддерживающ.	1	1,21	
4	ЗПС-50-3Г	Зажим заземляющ.	2	0,068	
5	ПГГ-25/6-12А	Зажим поддерживающ.	1	1,21	
Масса арматуры, кг				1,88	

Вариант крепления троса с заземлением

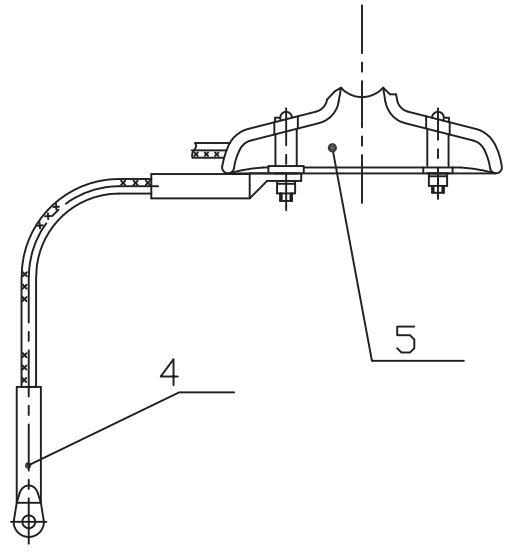


Взам. инв. N

Подп. и дата

Инв. N подл.


				ЭСИП-0102		
				ЭСС.001 ТМ - т.1		
Утв.	Вигдергауз			Поддерживающее неизолированное крепление троса С 50 к промежуточным деревянным опорам ВЛ 110 кВ	Стадия	Лист	Листов
					Р		1
Пров.	Липунцов				Филиал ОАО "ФСК ЕЭС" "Электросетьсервис"		
Разраб.	Власкина						

Формат А3

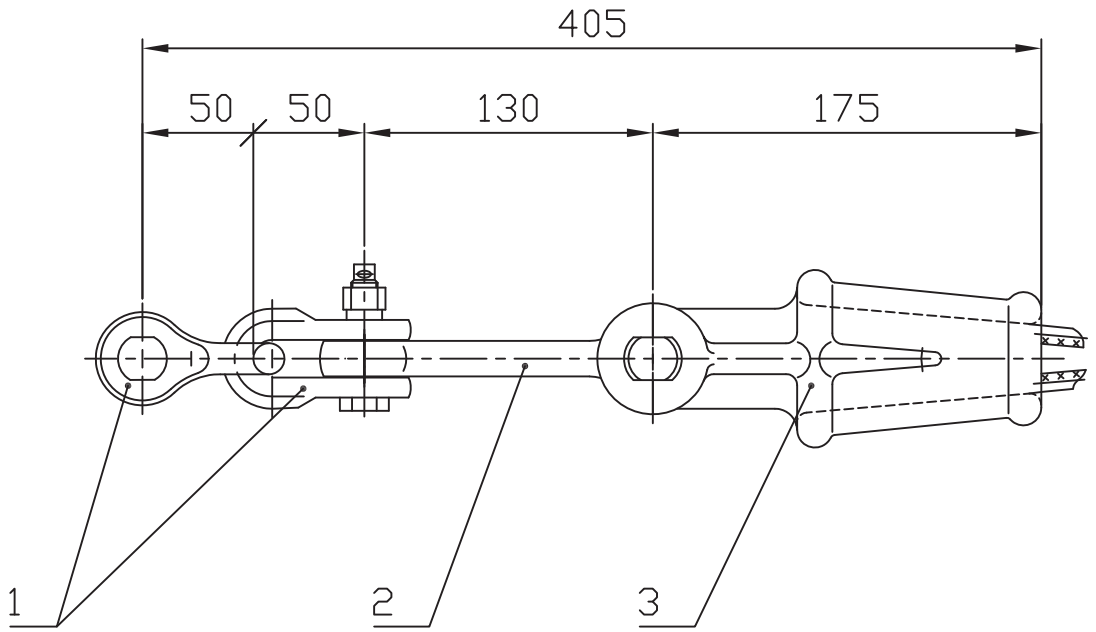

Поз.	Обозначение	Наименование	Кол.	Масса ед. кг	Прим.
1	СК-70-1Б	Скоба	2	0,38	
2	ПРВ-7-1	Звено вывернутое	1	0,43	
3	НКК-1-1Б	Зажим натяжной			
		(с клином №2)	1	0,78	
4	ПС-2-1	Зажим плашечный	1	0,42	для варианта
5	ЗПС-50-3Г	Зажим заземляющий	1	0,068	для варианта
Масса арматуры, кг				1,97	

Вариант крепления троса с зазаемлением

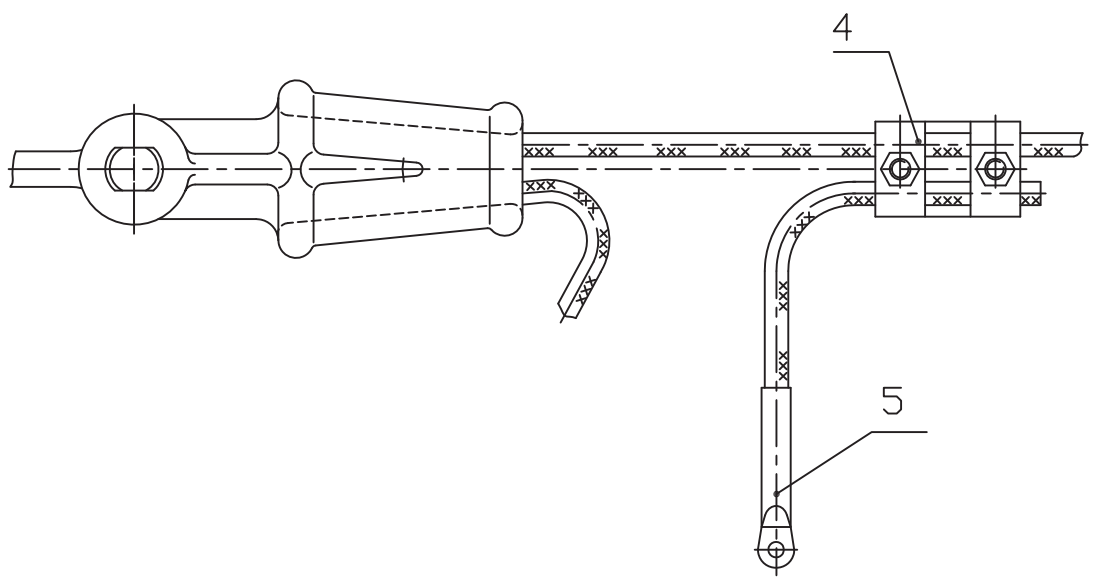


Взам. инв. N

Подп. и дата

Инв. N подл.

				ЭСИП-0103		
				ЭСС.001 ТМ - т.1		
Утв.	Вигдергауз			Натяжное неизолированное крепление троса С 50 к а/у деревянным опорам ВЛ 35, 110 кВ	Стадия	Лист	Листов
					Р		1
Пров.	Липунцов				Филиал ОАО "ФСК ЕЭС" "Электросетьсервис"		
Разраб.	Власкина						

Формат А3

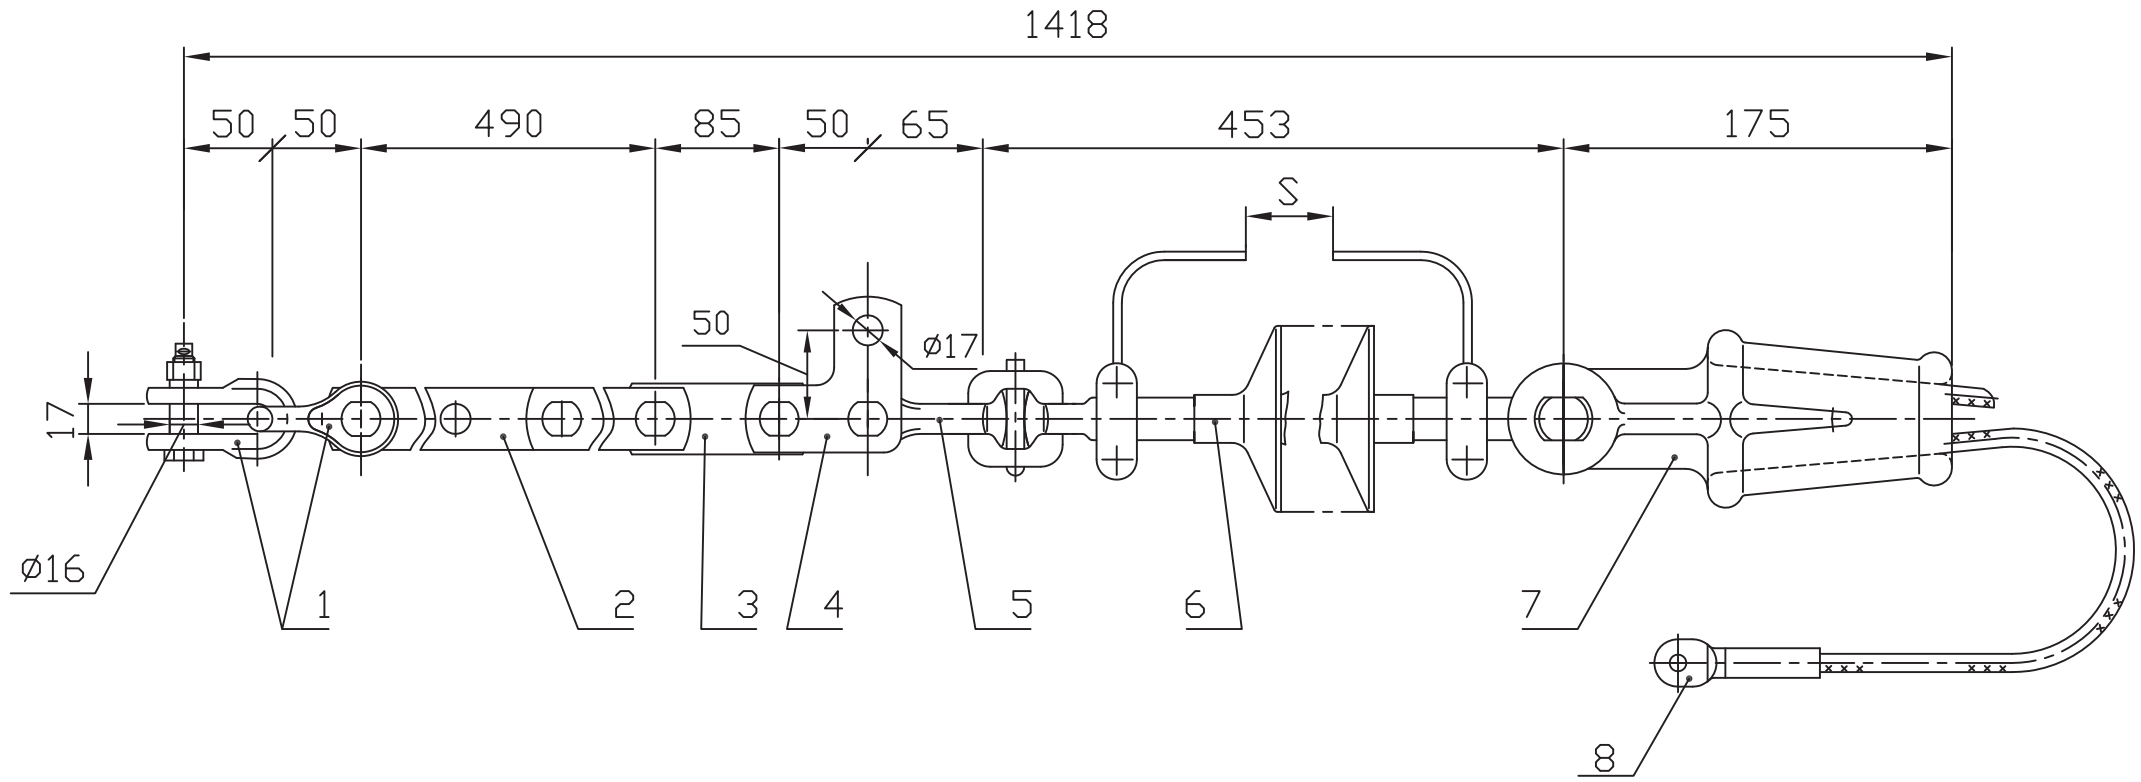


Напряжение ВЛ, кВ	Трос		Зажим, поз.8	
	Тип	Диаметр, мм	Обозначение	Масса, кг
35	С 35	7,8	ЗПС-35-3Г	0,057
110	С 50	9,2	ЗПС-50-3Г	0,068

Поз.	Обозначение	Наименование	Кол.	Масса ед. кг	Прим.
1	СК-70-1Б	Скоба	2	0,38	
2	ПРР-7-1	Звено регулируемое	1	1,91	
3	ПР-7-6	Звено прямое	1	0,34	
4	ПТМ-7-3А	Звено монтажное	1	0,63	
5	СР-7-16	Серьга	1	0,3	
6	ЛКГ 70-	Изолятор исп. ГС с рогами	1	См. табл.4	
7	НКК-1-1Б	Зажим натяжной			
		(с клином №2)	1	0,78	
8	См. таблицу	Зажим заземляющий	1	См. табл.	
Масса арматуры, кг				4,8	
Масса изолирующей подвески, кг					

Утв.	Вигдергауз	ЭСИП-0104	
		ЭСС.001 ТМ - т.1	
Пров.	Липунцов	Натяжное изолированное с полимерным изолятором ряда 70 кН крепление тросов С 35, С 50 к металлическим и ж/б опорам ВЛ 35, 110 кВ	Стадия: Р; Лист: ; Листов: 1
Разраб.	Власкина		Филиал ОАО "ФСК ЕЭС" "Электросетьсервис"

Взам. инв. N | Подп. и дата | Инв. N подл.

Формат А3

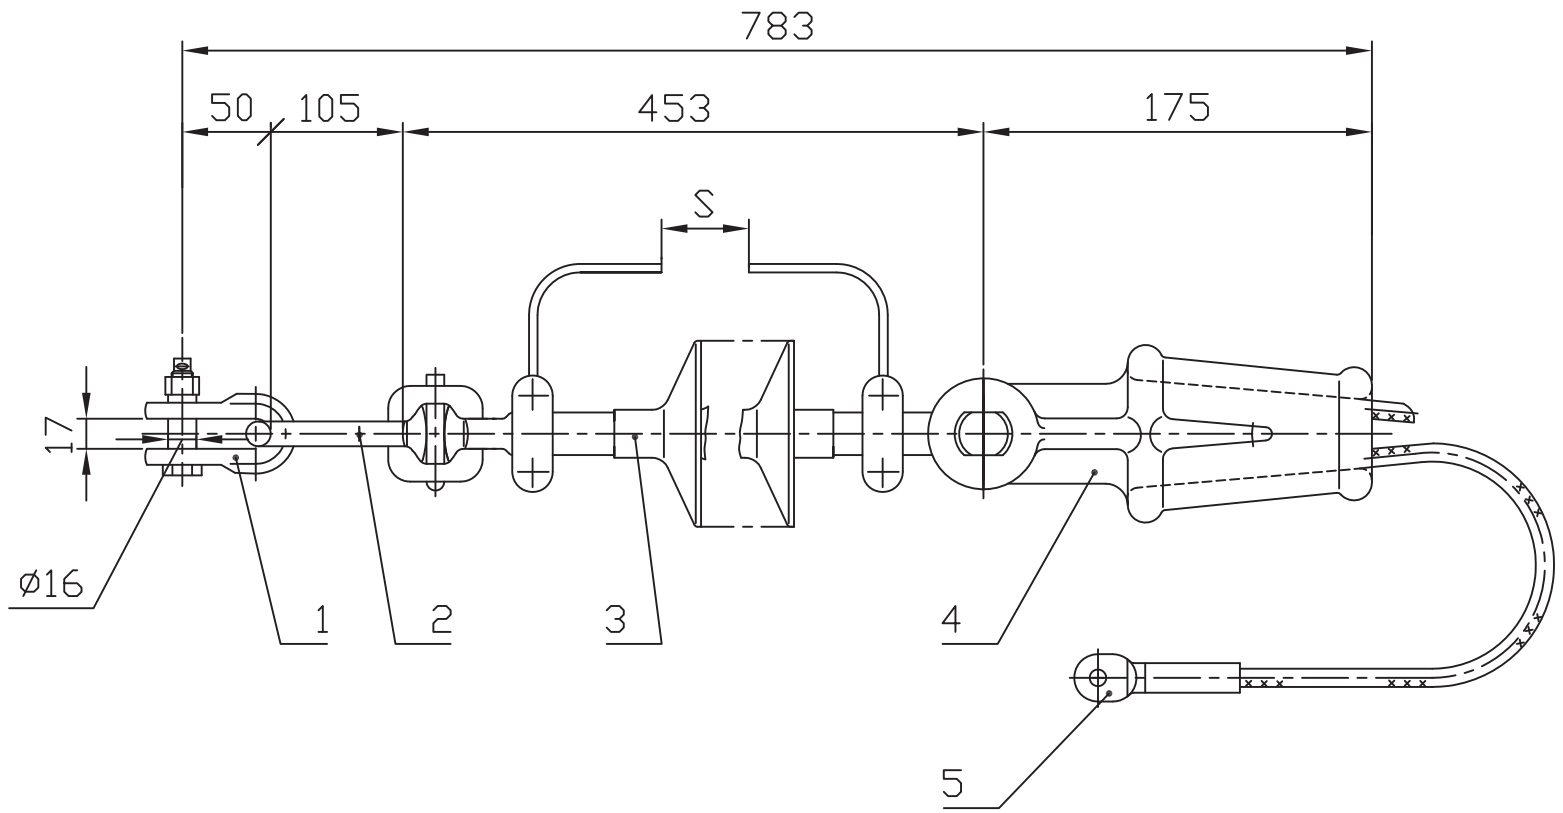

Напряжение ВЛ, кВ	Трос		Зажим, поз.8	
	Тип	Диаметр, мм	Обозначение	Масса, кг
35	С 35	7,8	ЗПС-35-3Г	0,057
110	С 50	9,2	ЗПС-50-3Г	0,068

Поз.	Обозначение	Наименование	Кол.	Масса ед. кг	Прим.
1	СК-70-1Б	Скоба	1	0,38	
2	СРД-70-16	Серьга длинная	1	0,35	
3	ЛКГ 70-	Изолятор исп. ГС с рогами	1	См. табл.4	
4	НКК-1-1Б	Зажим натяжной			
		(с клином №2)	1	0,78	
5	См. таблицу	Зажим заземляющий	1	См. табл.	
Масса арматуры, кг				1,58	
Масса изолирующей подвески, кг					


			ЭСИП-0105
			ЭСС.001 ТМ - т.1
Утв.	Вигдергауз		Натяжное изолированное с полимерным изолятором ряда 70 кН крепление тросов С 35, С 50 к металлическим и ж/б опорам ВЛ 35, 110 кВ
Пров.	Липунцов		
Разраб.	Власкина		

Стадия	Лист	Листов
Р		1

Филиал ОАО "ФСК ЕЭС" "Электросетьсервис"

Взам. инв. N | Подп. и дата | Инв. N подл.

Формат А3

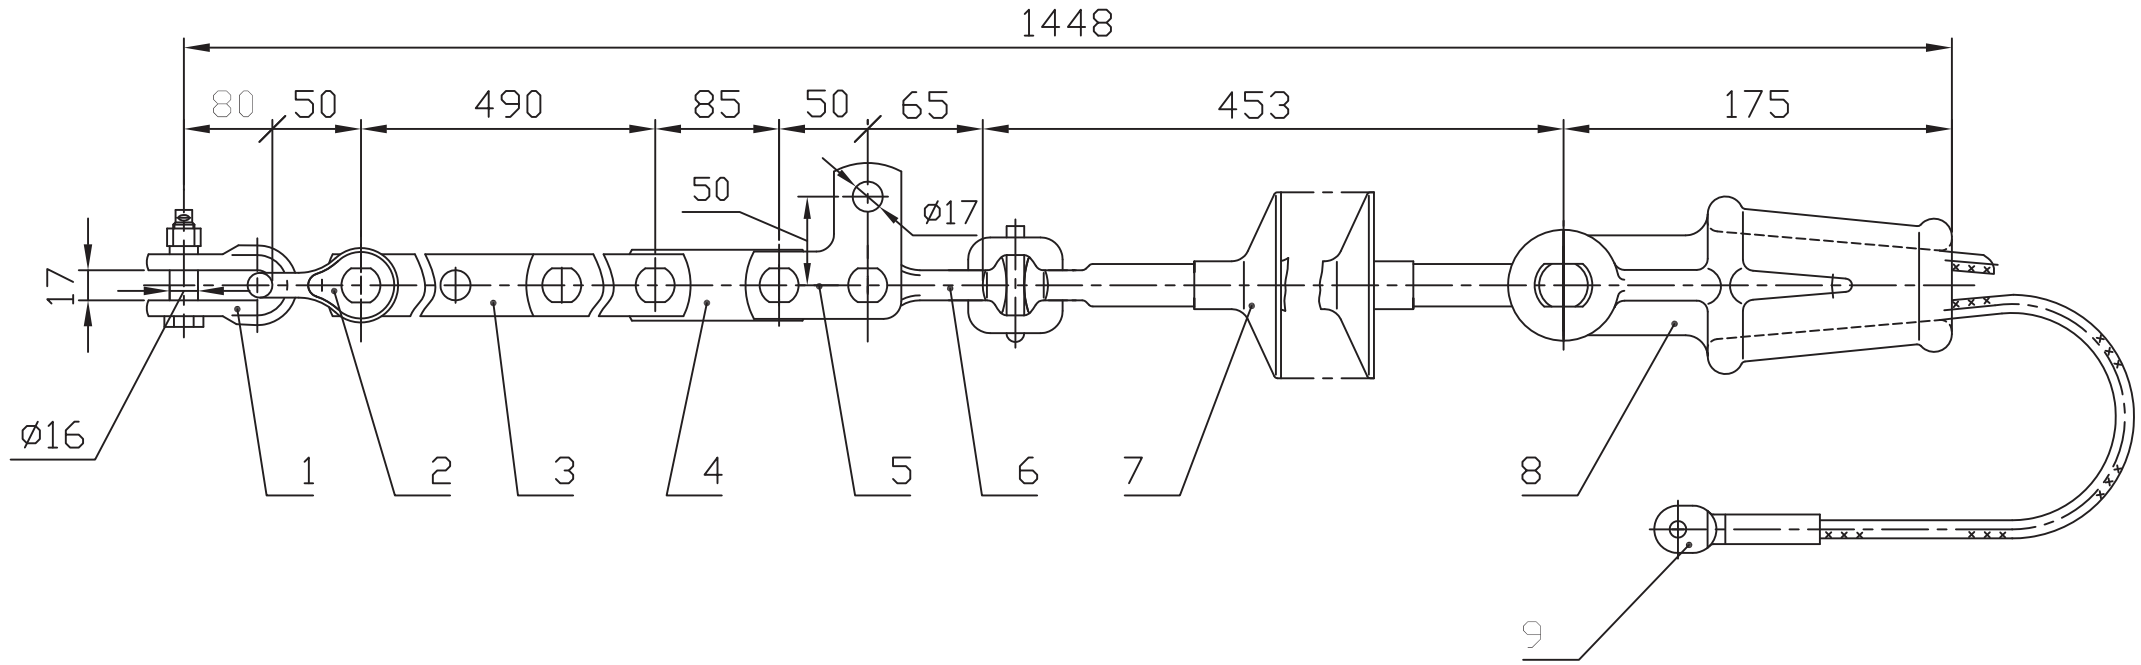

Поз.	Обозначение	Наименование	Кол.	Масса ед. кг	Прим.
1	СКД-10-1	Скоба	1	0,67	
2	СК-70-1Б	Скоба	1	0,38	
3	ПРР-7-1	Звено регулируемое	1	1,91	
4	ПР-7-6	Звено прямое	1	0,34	
5	ПТМ-7-3А	Звено монтажное	1	0,63	
6	СР-7-16	Серьга	1	0,3	
7	ЛКГ 70-	Изолятор исп. ГС без рогов	1	См. табл.4	
8	НКК-1-1Б	Зажим натяжной			
		(с клином №2)	1	0,78	
9	См. таблицу	Зажим заземляющий	1	См. табл.	
Масса арматуры, кг				5,1	
Масса изолирующей подвески, кг					

Напряжение ВЛ, кВ	Трос		Зажим, поз.9	
	Тип	Диаметр, мм	Обозначение	Масса, кг
35	С 35	7,8	ЗПС-35-3Г	0,057
110	С 50	9,2	ЗПС-50-3Г	0,068

Взам. инв. N

Подп. и дата

Инв. N подл.

Утв.	Вигдергауз		
Пров.	Липунцов		
Разраб.	Власкина		

ЭСИП-0106


ЭСС.001 ТМ - т.1

Натяжное изолированное с полимерным изолятором ряда 70 кН крепление тросов С 35, С 50 к металлическим и ж/б опорам ВЛ 35, 110 кВ

Стадия	Лист	Листов
Р		1

Филиал ОАО "ФСК ЕЭС" "Электросетьсервис"

Формат А3

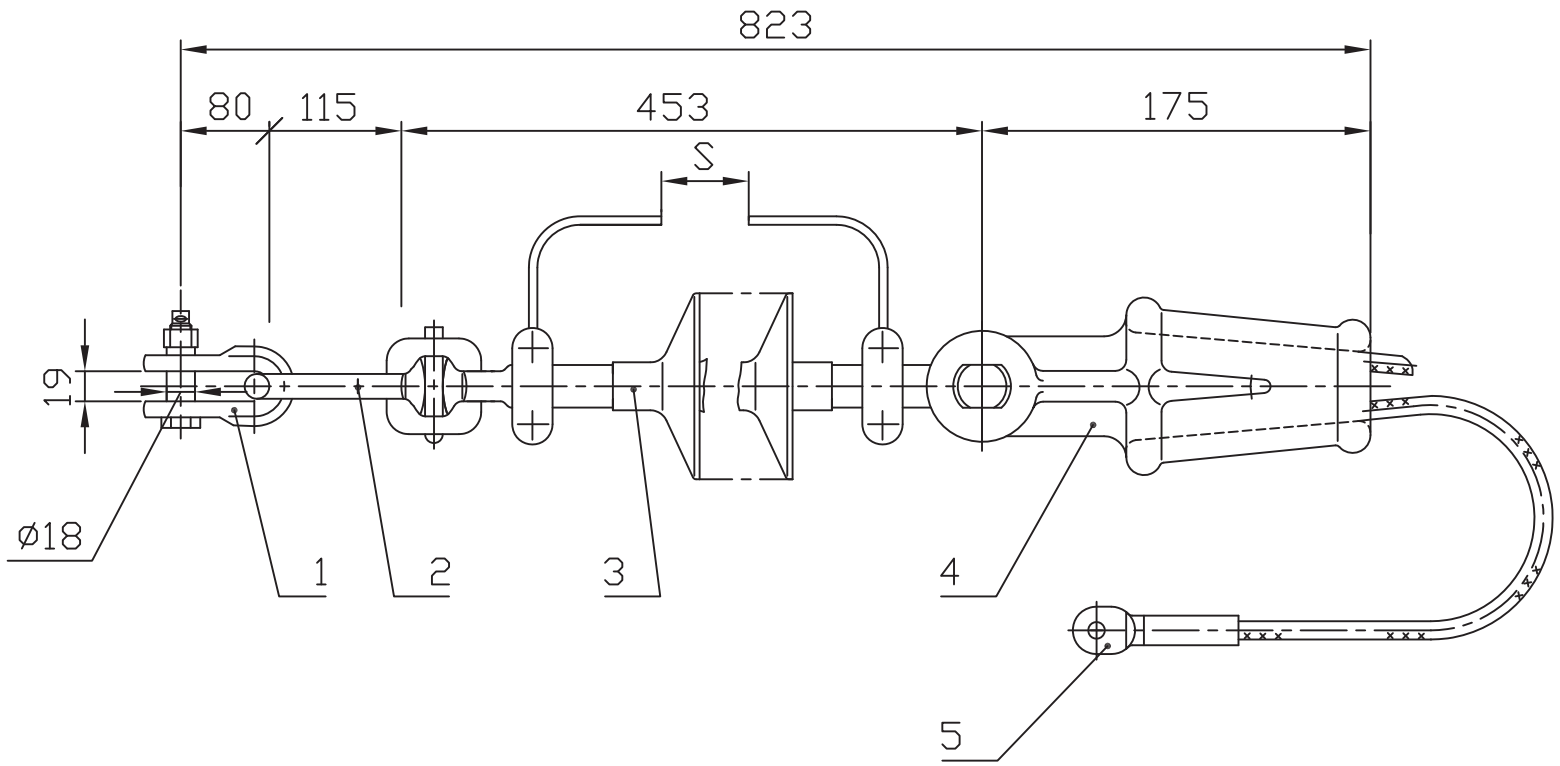

Напряжение ВЛ, кВ	Трос		Зажим, поз.5	
	Тип	Диаметр, мм	Обозначение	Масса, кг
35	С 35	7,8	ЗПС-35-3Г	0,057
110	С 50	9,2	ЗПС-50-3Г	0,068

Поз.	Обозначение	Наименование	Кол.	Масса ед. кг	Прим.
1	СКД-10-1	Скоба	1	0,67	
2	СРД-120-16	Серьга длинная	1	0,5	
3	ЛКГ 70-	Изолятор исп. ГС с рогами	1	См. табл. 4	
4	НКК-1-1Б	Зажим натяжной			
		(с клином №2)	1	0,78	
5	См. таблицу	Зажим заземляющий	1	См. табл.	
Масса арматуры, кг				2,02	
Масса изолирующей подвески, кг					

Утв.	Вигдергауз		
Пров.	Липунцов		
Разраб.	Власкина		

ЭСИП-0107

ЭСС.001 ТМ - т.1

Натяжное изолированное с полимерным изолятором ряда 70 кН крепление тросов С 35, С 50 к металлическим и ж/б опорам ВЛ 35, 110 кВ

Стадия	Лист	Листов
Р		1


Филиал ОАО "ФСК ЕЭС" "Электросетьсервис"

Взам. инв. N

Подп. и дата

Инв. N подл.

Формат А3

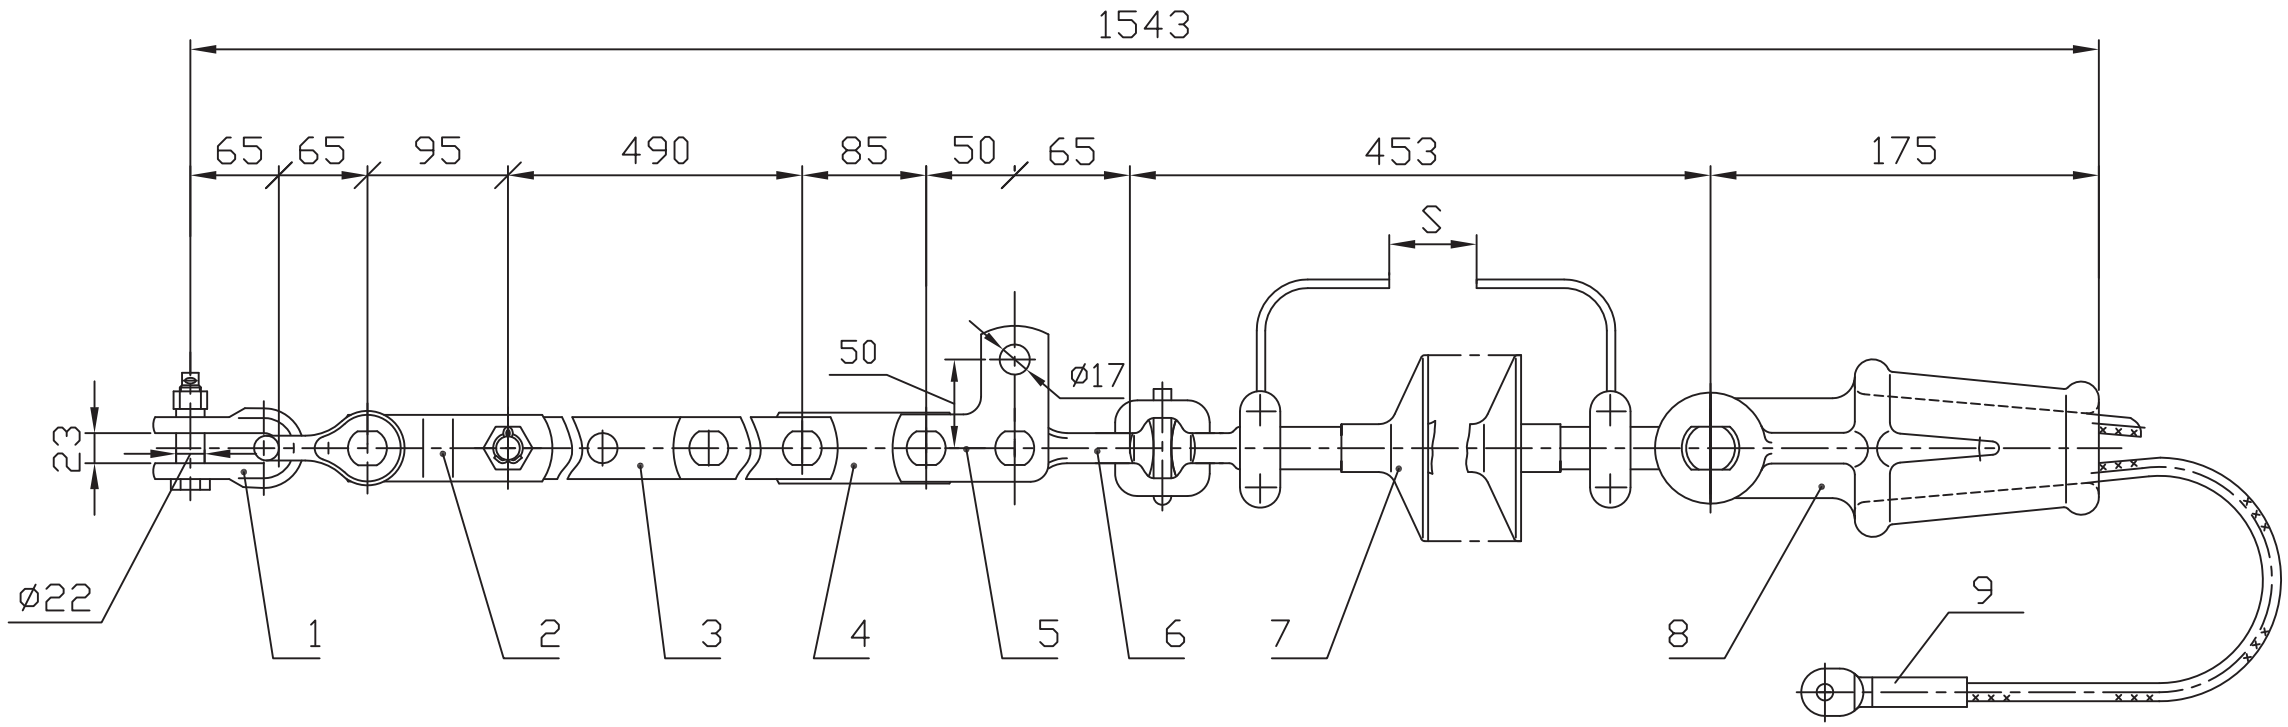


Напряжение ВЛ, кВ	Трос		Зажим, поз.9	
	Тип	Диаметр, мм	Обозначение	Масса, кг
35	С 35	7,8	ЗПС-35-3Г	0,057
110	С 50	9,2	ЗПС-50-3Г	0,068

Поз.	Обозначение	Наименование	Кол.	Масса ед. кг	Прим.
1	СК-120-1Б	Скоба	2	0,92	
2	ПРТ-12/7-2	Звено переходное	1	0,7	
3	ПРР-7-1	Звено регулируемое	1	1,91	
4	ПР-7-6	Звено прямое	1	0,34	
5	ПТМ-7-3А	Звено монтажное	1	0,63	
6	СР-7-16	Серьга	1	0,3	
7	ЛКГ 70-	Изолятор исп. ГС с рогами	1	См. табл.4	
8	НКК-1-1Б	Зажим натяжной			
		(с клином №2)	1	0,78	
9	См. таблицу	Зажим заземляющий	1	См. табл.	
Масса арматуры, кг				6,6	
Масса изолирующей подвески, кг					

Утв.	Вигдергауз	ЭСИП-0108	
		ЭСС.001 ТМ - т.1	
Пров.	Липунцов	Натяжное изолированное с полимерным изолятором ряда 70 кН крепление тросов С 35, С 50 к металлическим опорам ВЛ 35, 110 кВ	Стадия: Р; Лист: ; Листов: 1
Разраб.	Власкина		Филиал ОАО "ФСК ЕЭС" "Электросетьсервис"

Взам. инв. N | Подп. и дата | Инв. N подл.

Формат А3

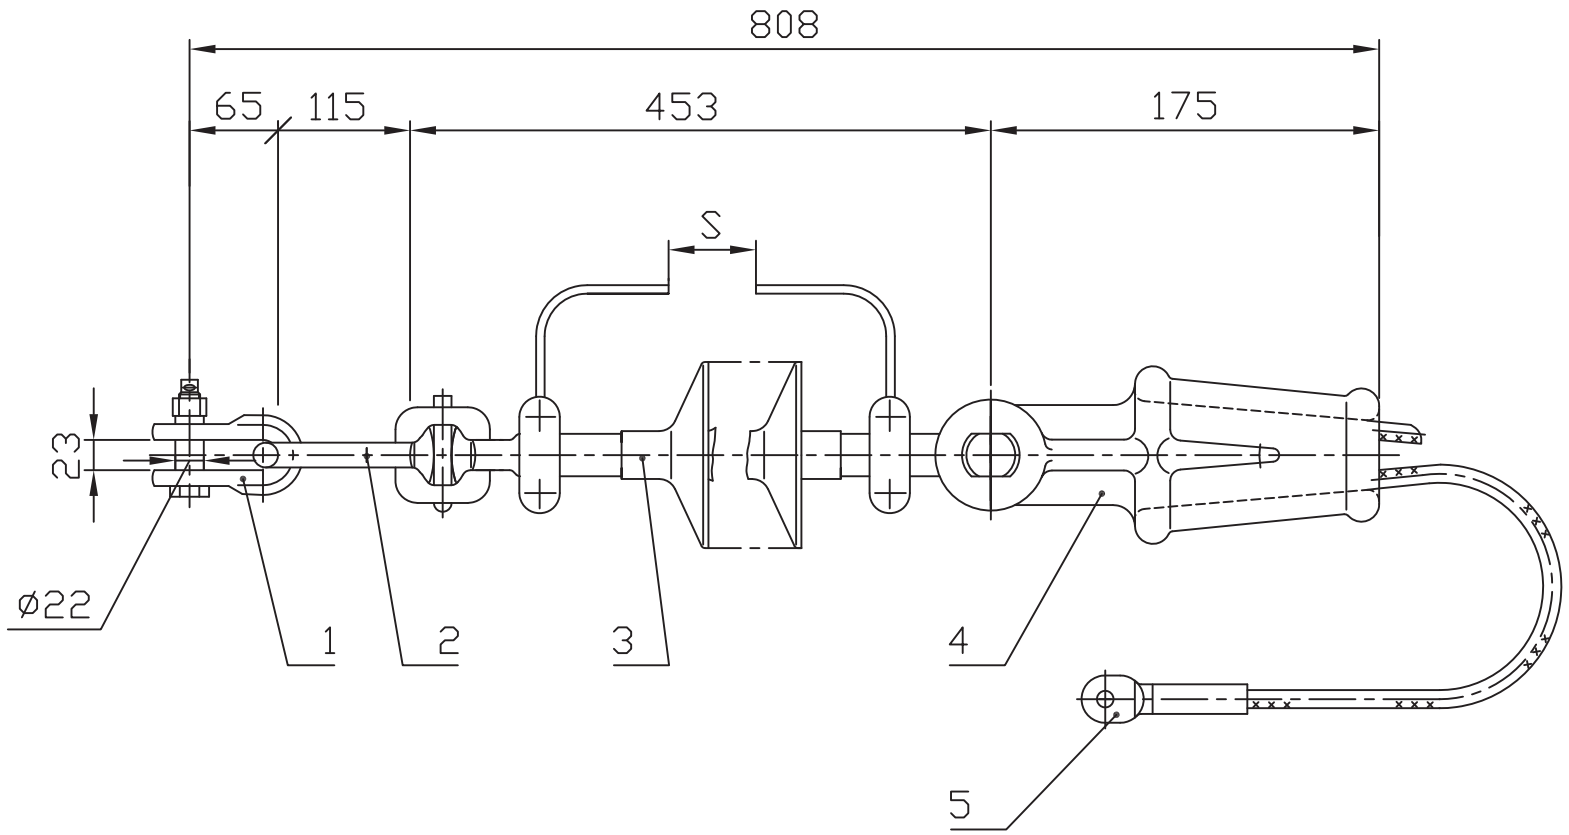

Напряжение ВЛ, кВ	Трос		Зажим, поз.5	
	Тип	Диаметр, мм	Обозначение	Масса, кг
35	С 35	7,8	ЗПС-35-3Г	0,057
110	С 50	9,2	ЗПС-50-3Г	0,068

Поз.	Обозначение	Наименование	Кол.	Масса ед. кг	Прим.
1	СК-120-1Б	Скоба	1	0,92	
2	СРД-120-16	Серьга длинная	1	0,5	
3	ЛКГ 70-	Изолятор исп. ГС с рогами	1	См. табл.4	
4	НКК-1-1Б	Зажим натяжной			
		(с клином №2)	1	0,78	
5	См. таблицу	Зажим заземляющий	1	См. табл.	
Масса арматуры, кг				2,3	
Масса изолирующей подвески, кг					

Взам. инв. N

Подп. и дата


Инв. N подл.

			ЭСИП-0109
			ЭСС.001 ТМ - т.1
Утв.	Вигдергауз		Натяжное изолированное с полимерным изолятором ряда 70 кН крепление тросов С 35, С 50 к металлическим опорам ВЛ 35, 110 кВ
Пров.	Липунцов		
Разраб.	Власкина		

Стадия	Лист	Листов
Р		1

Филиал ОАО "ФСК ЕЭС" "Электросетьсервис"

Формат А3

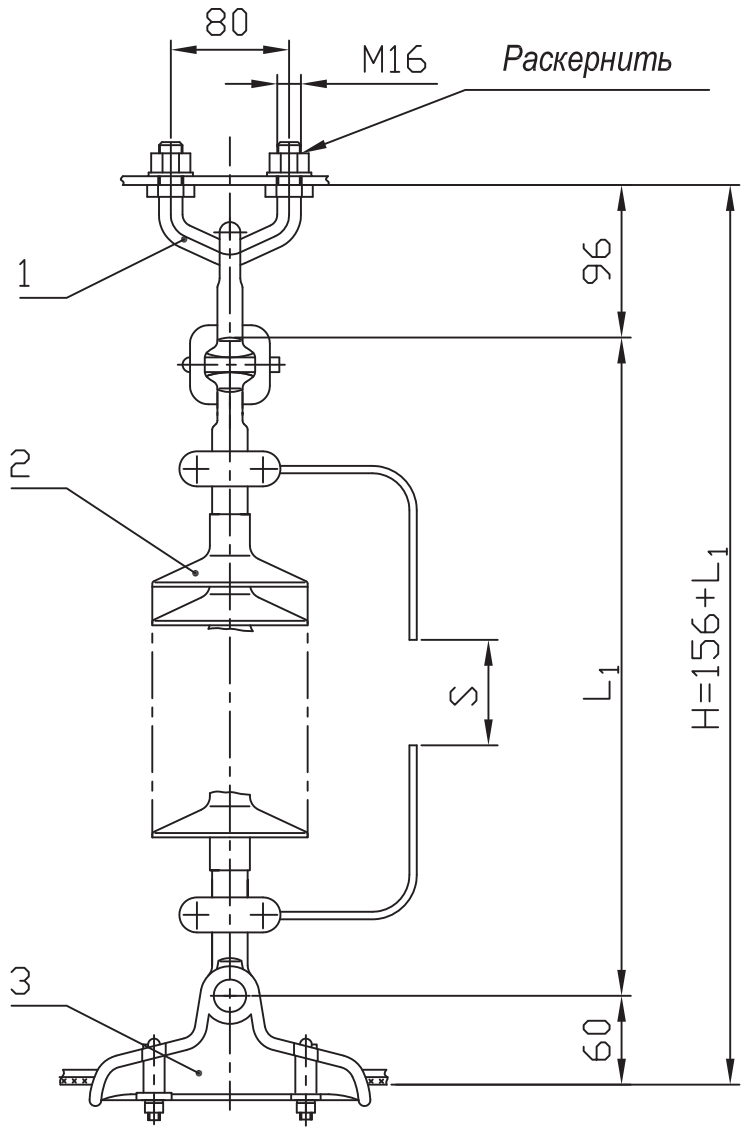

Поз.	Обозначение	Наименование	Кол.	Масса ед. кг	Прим.
1	КГП-7-2В	Узел крепления	1	0,7	
2	ЛКГ 70-	Изолятор исп. ГС с рогами	1	См. табл.4	
3	ПГ-25/6-12	Зажим поддерживающ.	1	1,01	
Масса арматуры, кг				1,71	
Масса изолирующей подвески, кг					


Взам. инв. N

Подп. и дата

Инв. N подл.

		ЭСИП-0110	
		ЭСС.001 ТМ - т.1	
Утв.	Вигдергауз	Поддерживающее изолированное с полимерным изолятором ряда 70 кН крепление троса С 70 (с искровым промежутком) к промежуточным металлическим и ж/б опорам ВЛ 220 кВ	Стадия: Р; Лист: ; Листов: 1
Пров.	Липунцов		Филиал ОАО "ФСК ЕЭС" "Электросетьсервис"
Разраб.	Власкина		

Формат А3

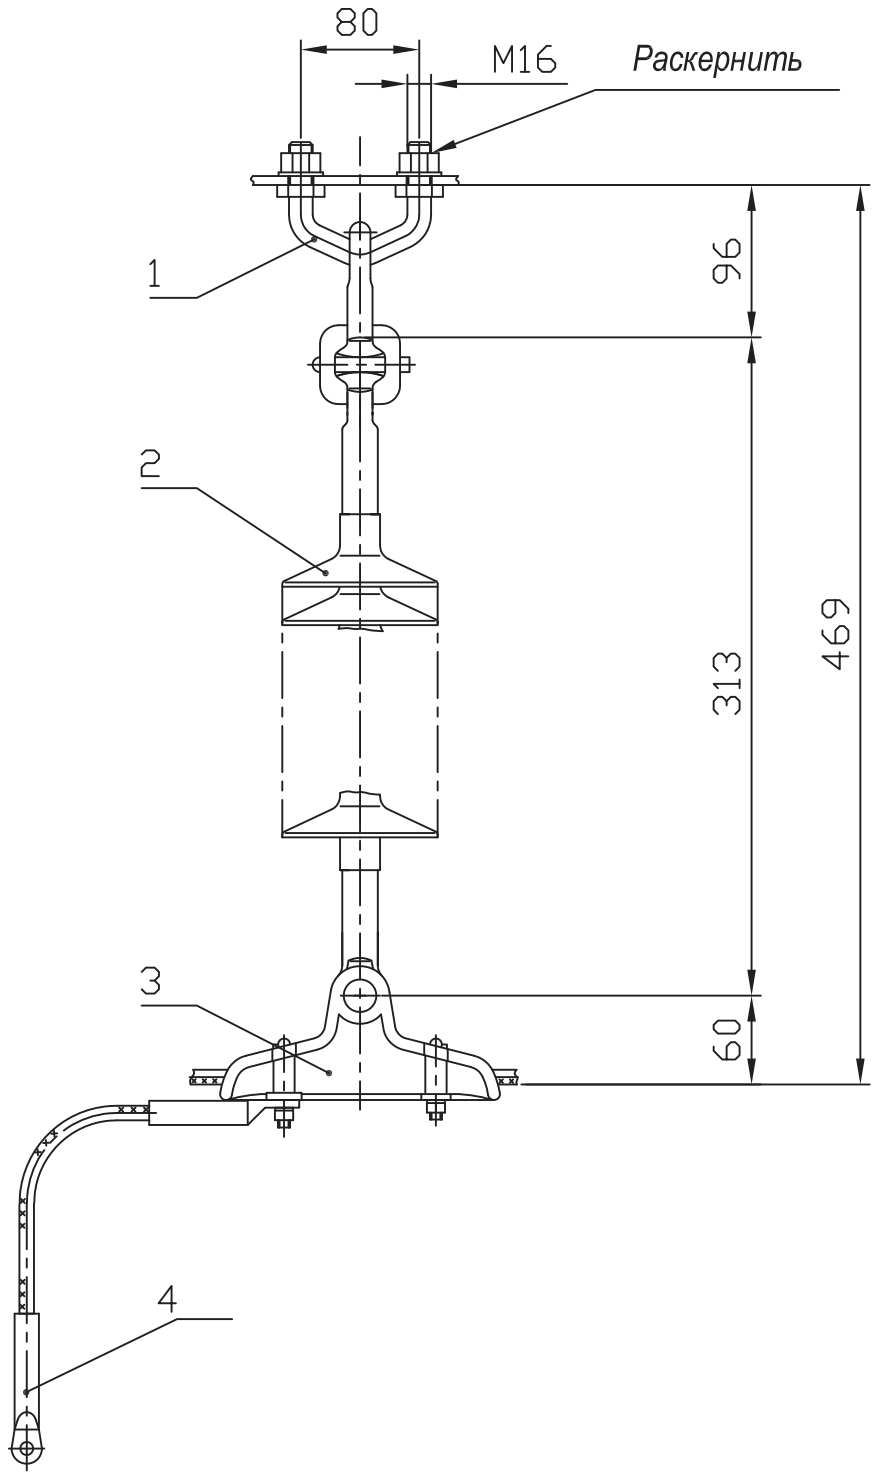

Поз.	Обозначение	Наименование	Кол.	Масса ед. кг	Прим.
1	КГП-7-2В	Узел крепления	1	0,7	
2	ЛКГ 70-	Изолятор исп. ГС без рогов	1	См. табл.4	
3	ПГ-25/6-12.А	Зажим поддерживающ.	1	1,01	
3	ЗПС-70-3Г	Зажим заземляющий	2	0,085	
Масса арматуры, кг				1,88	
Масса изолирующей подвески, кг					


Взам. инв. N

Подп. и дата

Инв. N подл.

			ЭСИП-0111
			ЭСС.001 ТМ - т.1
Утв.	Вигдергауз		Поддерживающее изолированное с полимерным изолятором ряда 70 кН крепление троса С 70 (с заземлением) к промежуточным металлическим и ж/б опорам ВЛ 220 кВ
Пров.	Липунцов		Стадия: Р; Лист: ; Листов: 1
Разраб.	Власкина		Филиал ОАО "ФСК ЕЭС" "Электросетьсервис"

Формат А3

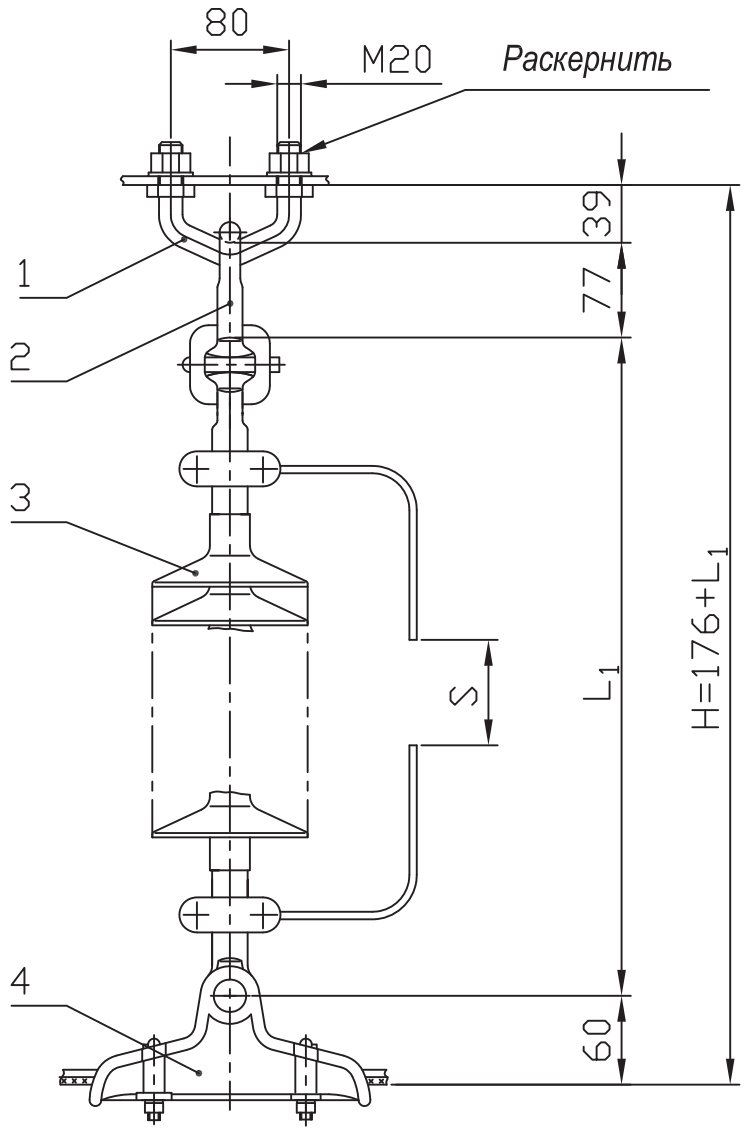

Поз.	Обозначение	Наименование	Кол.	Масса ед. кг	Прим.
1	КГП-16-3	Узел крепления	1	0,81	
2	СРС-7-16	Серьга	1	0,32	
3	ЛКГ 70-	Изолятор исп. ГС с рогами	1	См. табл.4	
4	ПГ-25/6-12	Зажим поддерживающ.	1	1,01	
Масса арматуры, кг				2,12	
Масса изолирующей подвески, кг					


Взам. инв. N

Подп. и дата

Инв. N подл.

				ЭСИП-0112		
				ЭСС.001 ТМ - т.1		
Утв.	Вигдергауз			Поддерживающее изолированное с полимерным изолятором ряда 70 кН крепление троса С 70 (с искровым промежутком) к промежуточным металлическим и ж/б ВЛ 220 кВ	Стадия	Лист	Листов
					Р		1
Пров.	Липунцов				Филиал ОАО "ФСК ЕЭС" "Электросетьсервис"		
Разраб.	Власкина						

Формат А3

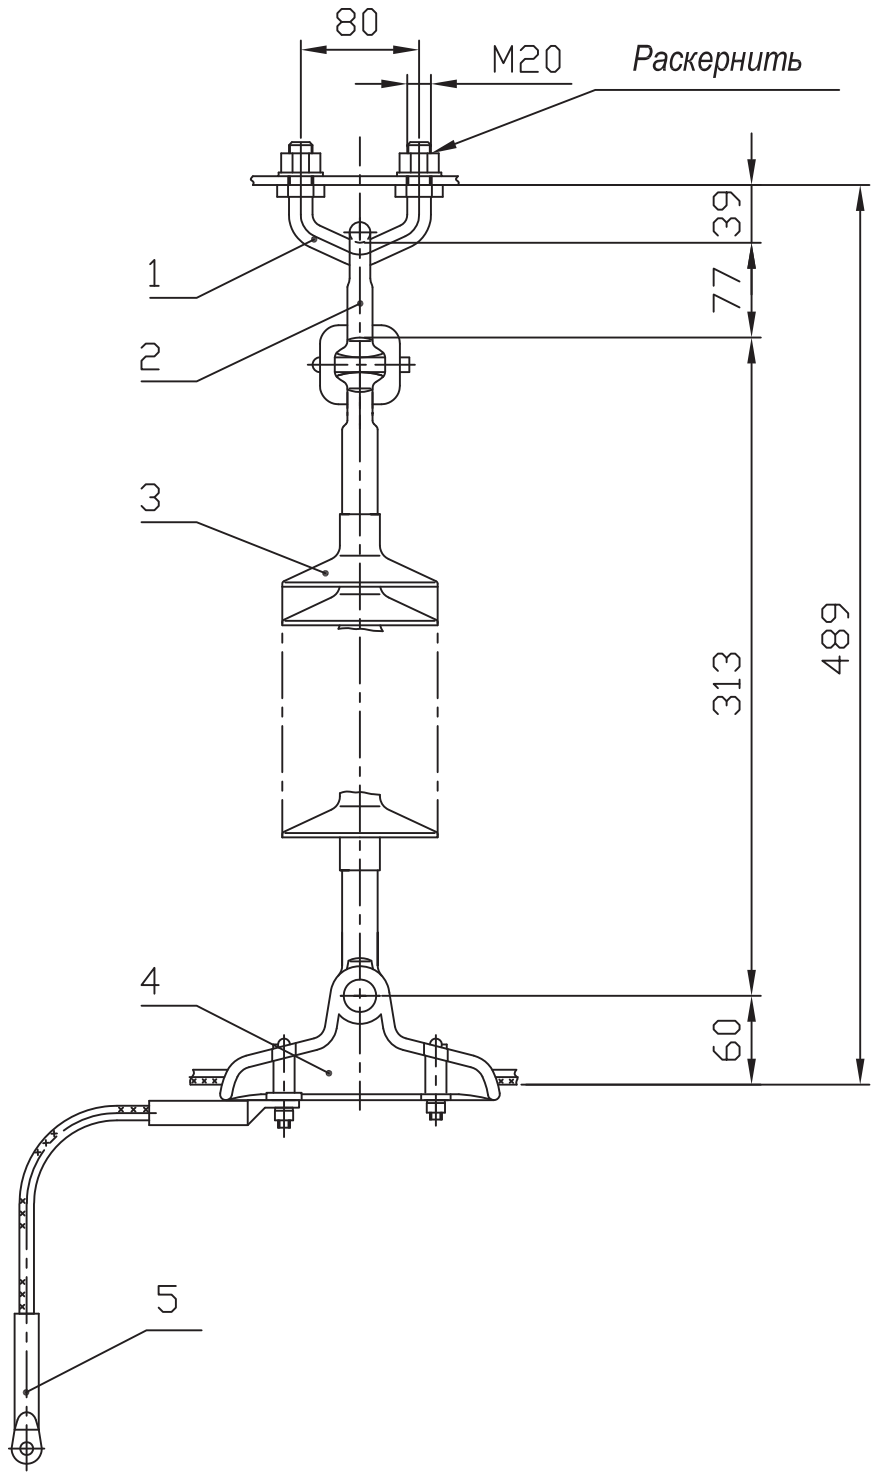

Поз.	Обозначение	Наименование	Кол.	Масса ед. кг	Прим.
1	КГП-16-3	Узел крепления	1	0,81	
2	СРС-7-16	Серьга	1	0,32	
3	ЛКГ 70-	Изолятор исп. ГС без рогов	1	См. табл.4	
4	ПГ-25/6-12.А	Зажим поддерживающ.	1	1,01	
5	ЗПС-70-3Г	Зажим заземляющий	2	0,085	
Масса арматуры, кг				2,3	
Масса изолирующей подвески, кг					

Взам. инв. N

Подп. и дата


Инв. N подл.

			ЭСИП-0113
			ЭСС.001 ТМ - т.1
Утв.	Вигдергауз		Поддерживающее изолированное с полимерным изолятором ряда 70 кН крепление троса С 70 (с заземлением) к промежуточным металлическим и ж/б ВЛ 220 кВ
Пров.	Липунцов		
Разраб.	Власкина		

Стадия	Лист	Листов
Р		1

Филиал ОАО "ФСК ЕЭС" "Электросетьсервис"

Формат А3

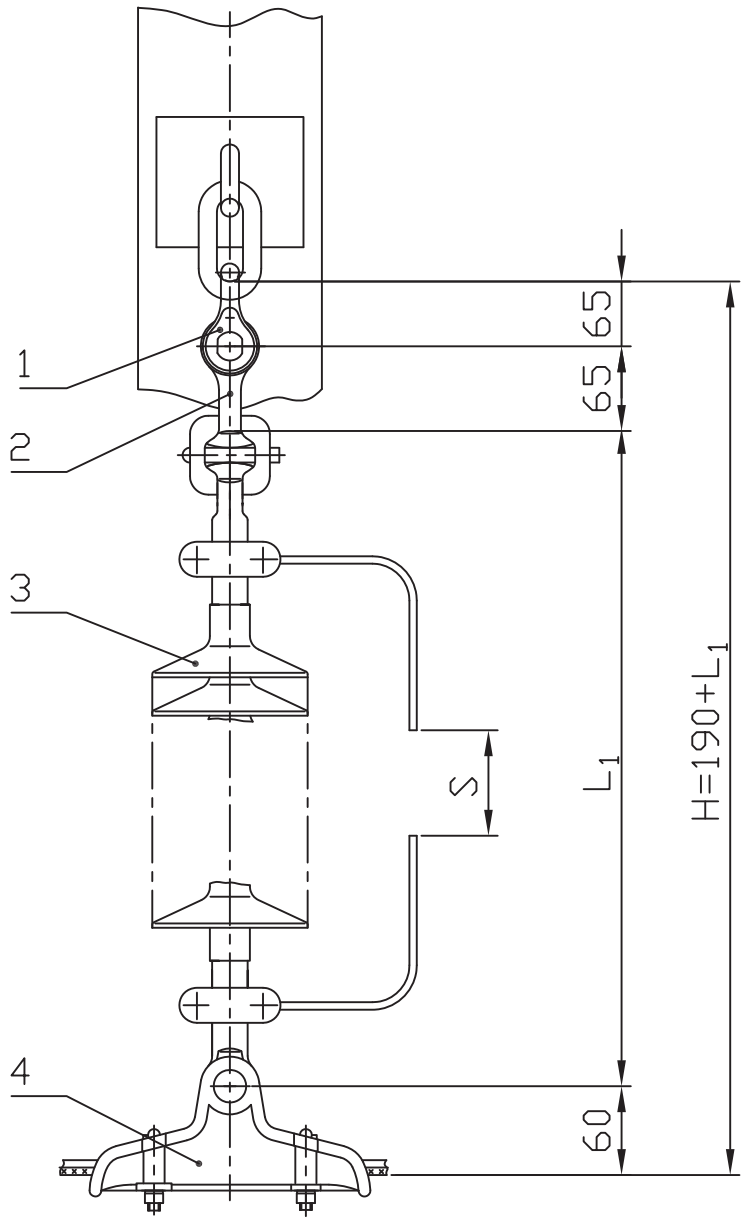

Поз.	Обозначение	Наименование	Кол.	Масса ед. кг	Прим.
1	СК-120-1Б	Скоба	1	0,92	
2	СР-12-16	Серьга	1	0,41	
3	ЛКГ 70-	Изолятор исп. ГС без рогов	1	См. табл.4	
4	ПГ-25/6-12	Зажим поддерживающ.	1	1,01	
Масса арматуры, кг				2,34	
Масса изолирующей подвески, кг					


Взам. инв. N

Подп. и дата

Инв. N подл.

				ЭСИП-0114		
				ЭСС.001 ТМ - т.1		
Утв.	Вигдергауз			Поддерживающее изолированное с полимерным изолятором ряда 70 кН крепление троса С 70 (с искровым промежутком) к промежуточным деревянным опорам ВЛ 220 кВ	Стадия: Р; Лист: ; Листов: 1	
Пров.	Липунцов				Филиал ОАО "ФСК ЕЭС" "Электросетьсервис"	
Разраб.	Власкина					

Формат А3

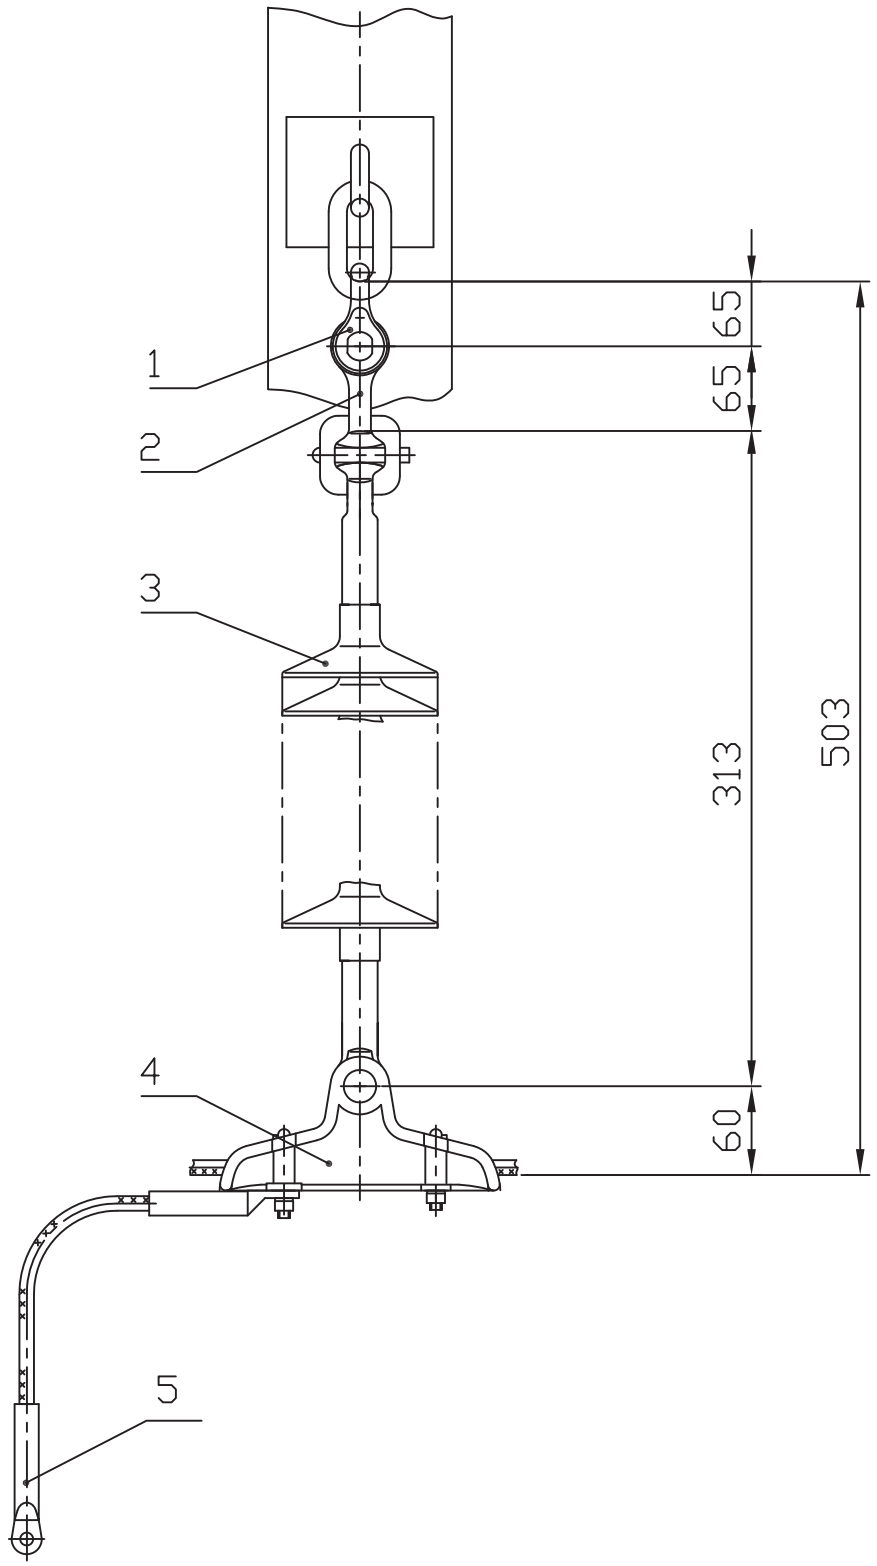

Поз.	Обозначение	Наименование	Кол.	Масса ед. кг	Прим.
1	СК-120-1Б	Скоба	1	0,92	
2	СР-12-16	Серьга	1	0,41	
3	ЛКГ 70-	Изолятор исп. ГС без рогов	1	См. табл.4	
4	ПГ-25/6-12.А	Зажим поддерживающ.	1	1,01	
5	ЗПС-70-3Г	Зажим заземляющий	2	0,085	
Масса арматуры, кг				2,51	
Масса изолирующей подвески, кг					


Взам. инв. N

Подп. и дата

Инв. N подл.

		ЭСИП-0115	
		ЭСС.001 ТМ - т.1	
Утв.	Вигдергауз	Поддерживающее изолированное с полимерным изолятором ряда 70 кН крепление троса С 70 (с заземлением) к промежуточным деревянным опорам ВЛ 220 кВ	Стадия: Р; Лист: ; Листов: 1
Пров.	Липунцов		Филиал ОАО "ФСК ЕЭС" "Электросетьсервис"
Разраб.	Власкина		

Формат А3

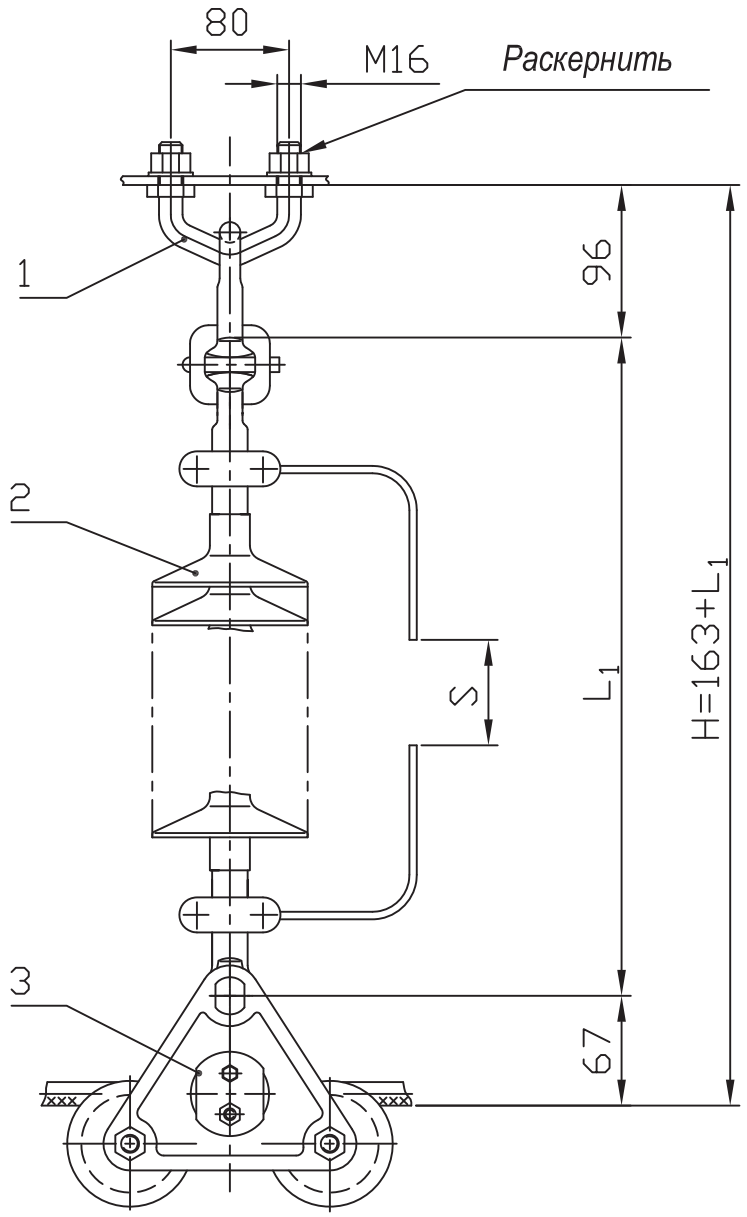

Поз.	Обозначение	Наименование	Кол.	Масса ед. кг	Прим.
1	КГП-7-2В	Узел крепления	1	0,70	
2	ЛКГ 70-	Изолятор исп. ГС с рогами	1	См. табл.4	
3	ПГУ-2-2	Зажим поддерживающ.	1	1,88	
Масса арматуры, кг				2,58	
Масса изолирующей подвески, кг					


Взам. инв. N

Подп. и дата

Инв. N подл.

Утв.	Вигдергауз	ЭСИП-0116	
		ЭСС.001 ТМ - т.1	
Пров.	Липунцов	Поддерживающее изолированное с полимерным изолятором ряда 70 кН крепление троса С 70 (с искровым промежутком) для опоры типа ПУС 220 ВЛ 220 кВ	Стадия: Р; Лист: ; Листов: 1
Разраб.	Власкина		Филиал ОАО "ФСК ЕЭС" "Электросетьсервис"

Формат А3

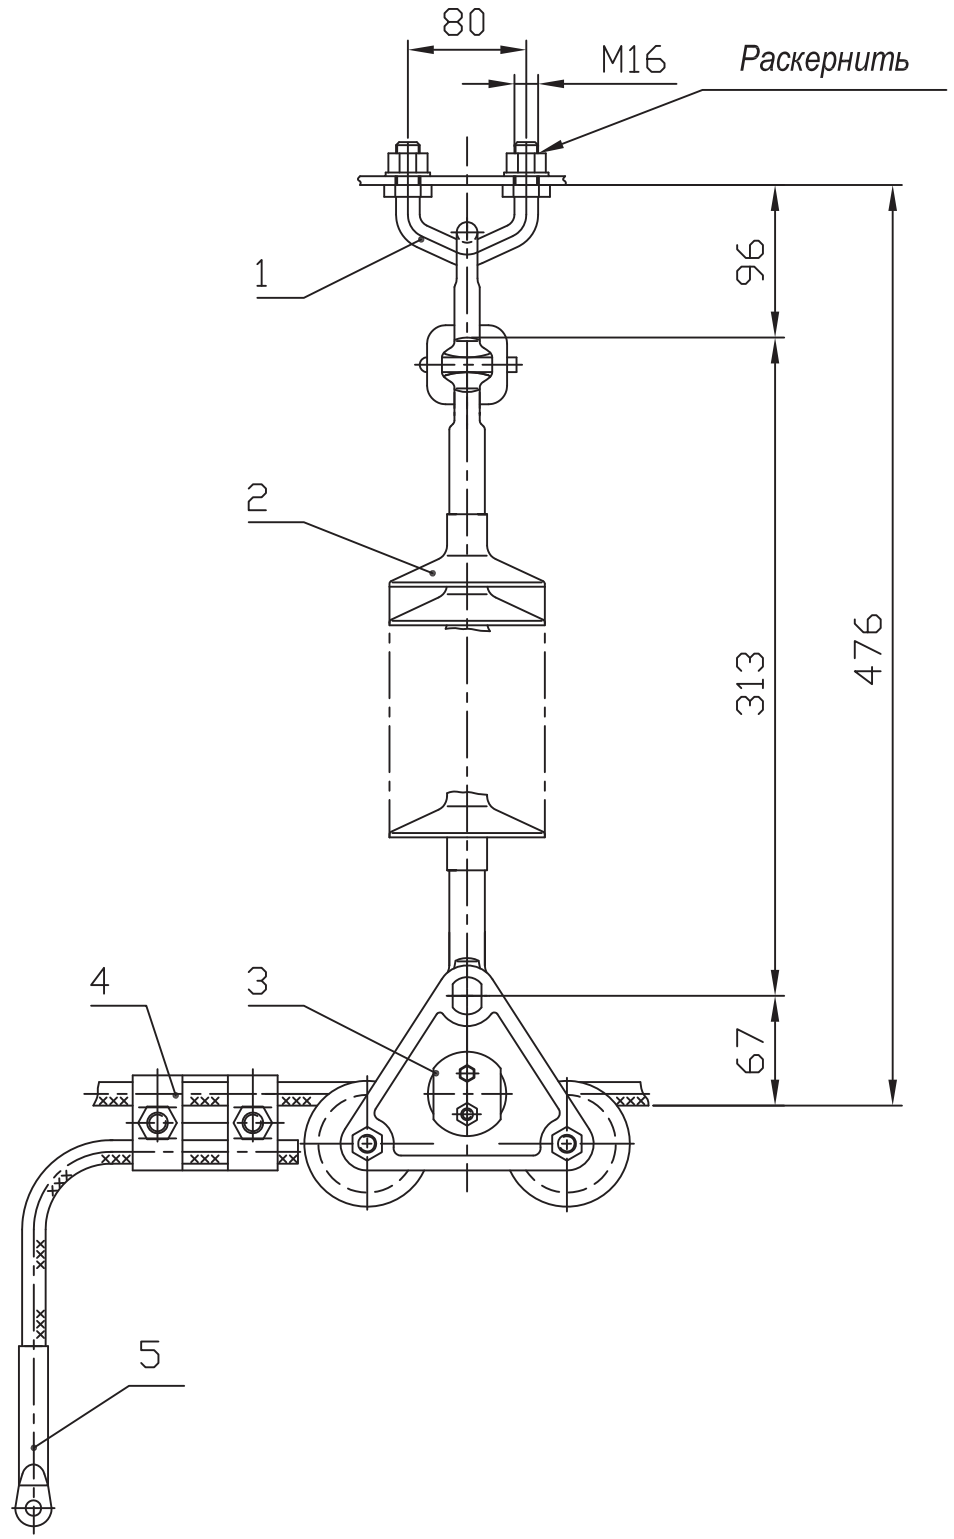

Поз.	Обозначение	Наименование	Кол.	Масса ед. кг	Прим.
1	КГП-7-2В	Узел крепления	1	0,70	
2	ЛКГ 70-	Изолятор исп. ГС без рогов	1	См. табл.4	
3	ПГУ-2-2	Зажим поддерживающ.	1	1,88	
4	ПС-2-1	Зажим петлевой болтов.	1	0,25	
5	ЗПС-70-3Г	Зажим заземляющих	1	0,085	
Масса арматуры, кг				2,92	
Масса изолирующей подвески, кг					


Взам. инв. N

Подп. и дата

Инв. N подл.

		ЭСИП-0117	
		ЭСС.001 ТМ - т.1	
Утв.	Вигдергауз	Поддерживающее изолированное с полимерным изолятором ряда 70 кН крепление троса С 70 (с искровым промежутком) для опоры типа ПУС 220 ВЛ 220 кВ	Стадия: Р; Лист: ; Листов: 1
Пров.	Липунцов		Филиал ОАО "ФСК ЕЭС" "Электросетьсервис"
Разраб.	Власкина		

Формат А3

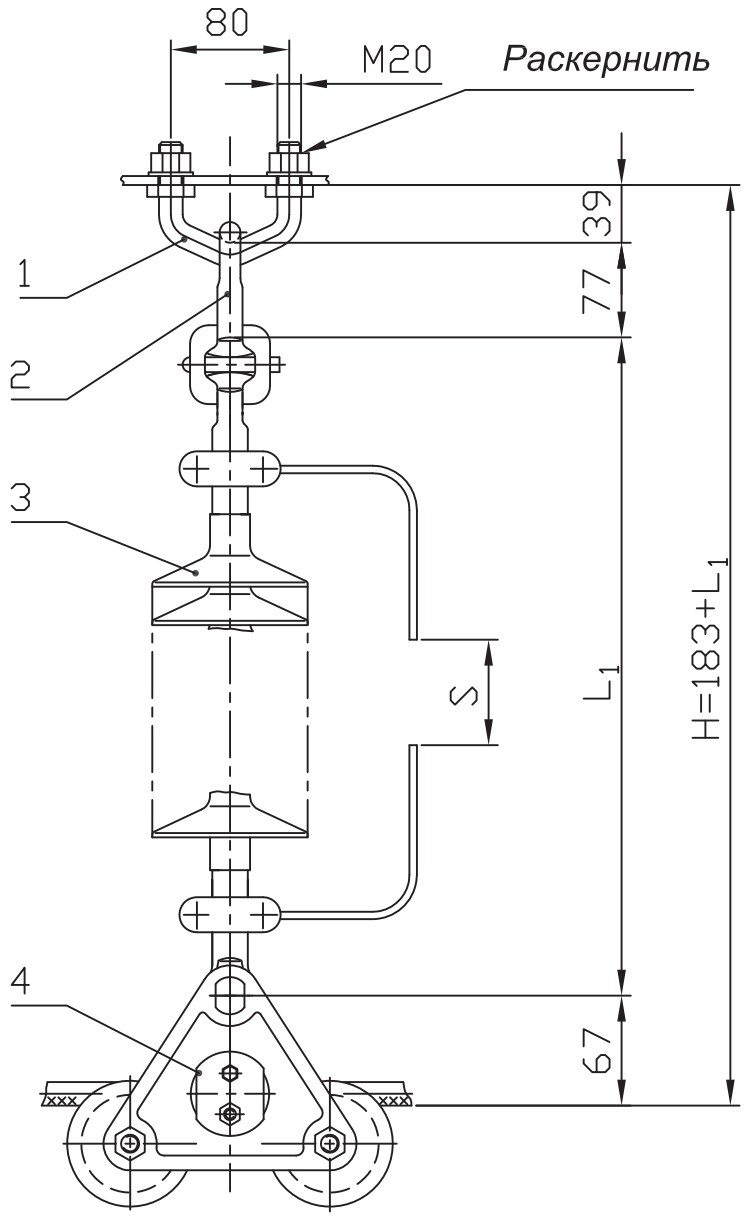

Поз.	Обозначение	Наименование	Кол.	Масса ед. кг	Прим.
1	КГП-16-3	Узел крепления	1	0,70	
2	СРС-7-16	Серьга	1	0,32	
3	ЛКГ 70-	Изолятор исп. ГС с рогами	1	См. табл.4	
4	ПГУ-2-2	Зажим поддерживающ.	1	1,88	
Масса арматуры, кг				3,01	
Масса изолирующей подвески, кг					


Взам. инв. N

Подп. и дата

Инв. N подл.

Утв.	Вигдергауз	ЭСИП-0118	
		ЭСС.001 ТМ - т.1	
Пров.	Липунцов	Поддерживающее изолированное с полимерным изолятором ряда 70 кН крепление троса С 70 (с искровым промежутком) для опоры типа ПУС 220 ВЛ 220 кВ	Стадия: Р; Лист: ; Листов: 1
Разраб.	Власкина		Филиал ОАО "ФСК ЕЭС" "Электросетьсервис"

Формат А3

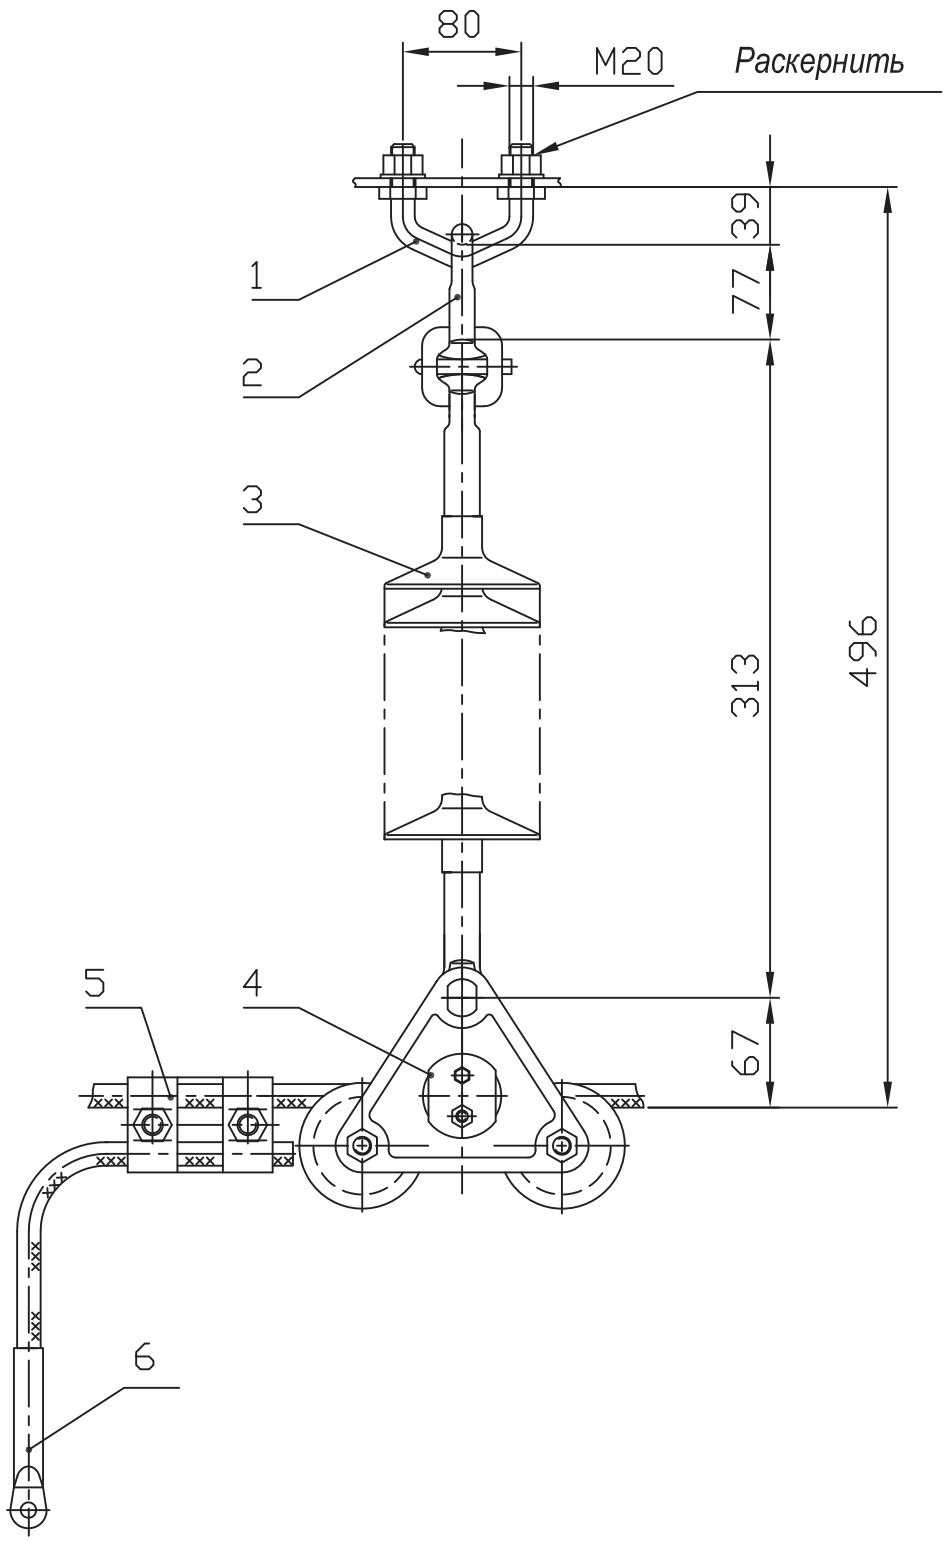

Поз.	Обозначение	Наименование	Кол.	Масса ед. кг	Прим.
1	КГП-16-3	Узел крепления	1	0,81	
2	СРС-7-16	Серьга	1	0,32	
3	ЛКГ 70-	Изолятор исп. ГС без рогов	1	См. табл.4	
4	ПГУ-2-2	Зажим поддерживающ.	1	1,88	
5	ПС-2-1	Зажим петлевой болтов.	1	0,25	
6	ЗПС-70-3Г	Зажим заземляющих	1	0,085	
Масса арматуры, кг				3,35	
Масса изолирующей подвески, кг					


Взам. инв. N


Подп. и дата


Инв. N подл.

Утв.	Вигдергауз	ЭСИП-0119	
		ЭСС.001 ТМ - т.1	
Пров.	Липунцов	Поддерживающее изолированное с полимерным изолятором ряда 70 кН крепление троса С 70 (с заземлением) для опоры типа ПУС 220 ВЛ 220 кВ	Стадия: Р; Лист: ; Листов: 1
Разраб.	Власкина		Филиал ОАО "ФСК ЕЭС" "Электросетьсервис"

Формат А3

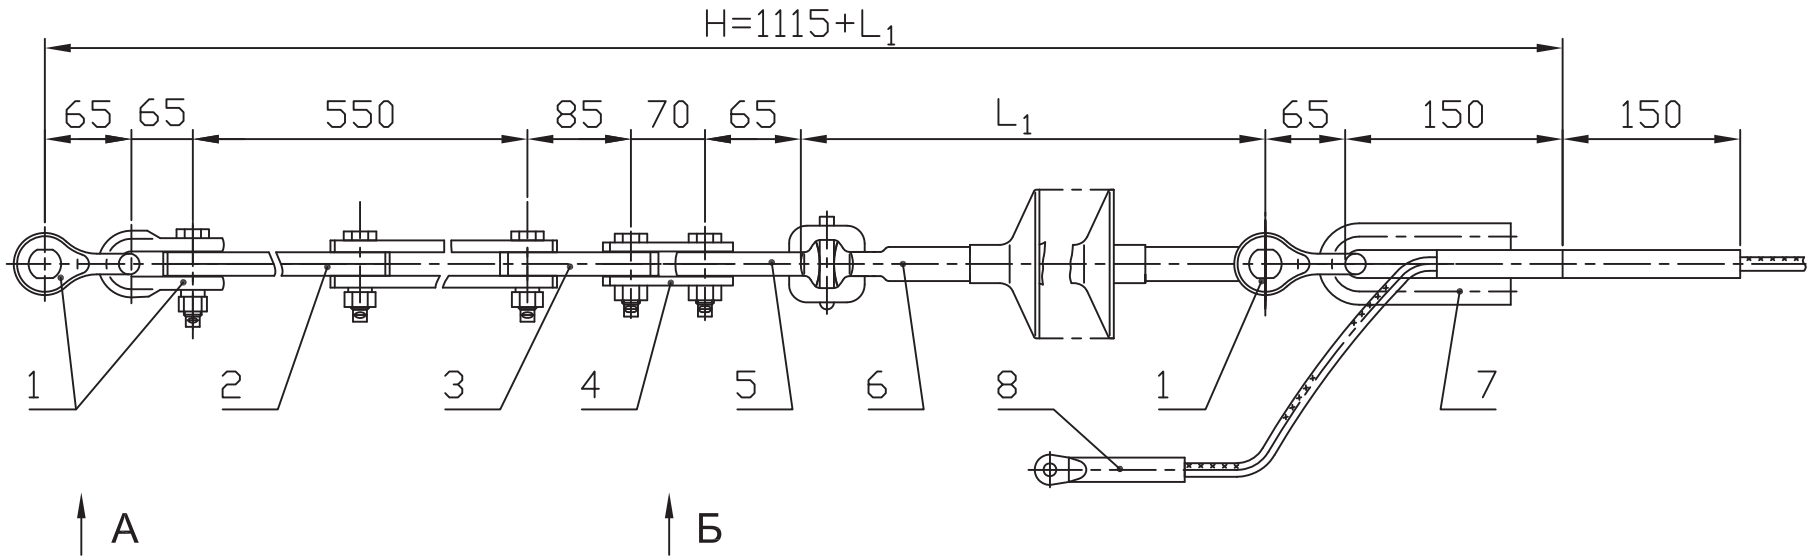

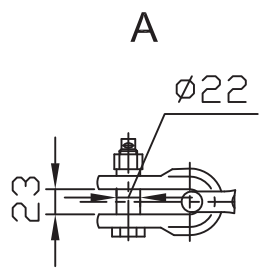

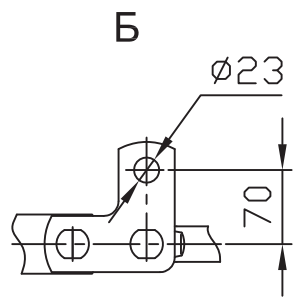

Поз.	Обозначение	Наименование	Кол.	Масса ед. кг	Прим.
1	СК-120-1Б	Скоба	3	0,92	
2	ПРР-12-1	Звено регулируемое	1	3,69	
3	ПР-12-6	Звено прямое	1	0,94	
4	ПТМ-12-3А	Звено монтажное	1	0,63	
5	СР-12-16	Серьга	1	0,41	
6	ЛКГ 120-	Изолятор исп. ГС без рогов	1	См. табл.4	
7	НС-70-3А	Зажим натяжной	1	1,68	
8	ЗПС-70-3Г	Зажим заземляющий	1	0,085	
Масса арматуры, кг				11,3	
Масса изолирующей подвески, кг					

Взам. инв. N

Подп. и дата


Инв. N подл.

			ЭСИП-0120
			ЭСС.001 ТМ - т.1
Утв.	Вигдергауз		Натяжное изолированное с полимерным изолятором ряда 120 кН крепление троса С70 (с заземлением) к а/у металлическим, ж/б и деревянным опорам ВЛ 220 кВ
Пров.	Липунцов		
Разраб.	Власкина		

Стадия	Лист	Листов
Р		1


Филиал ОАО "ФСК ЕЭС" "Электросетьсервис"


Формат А3

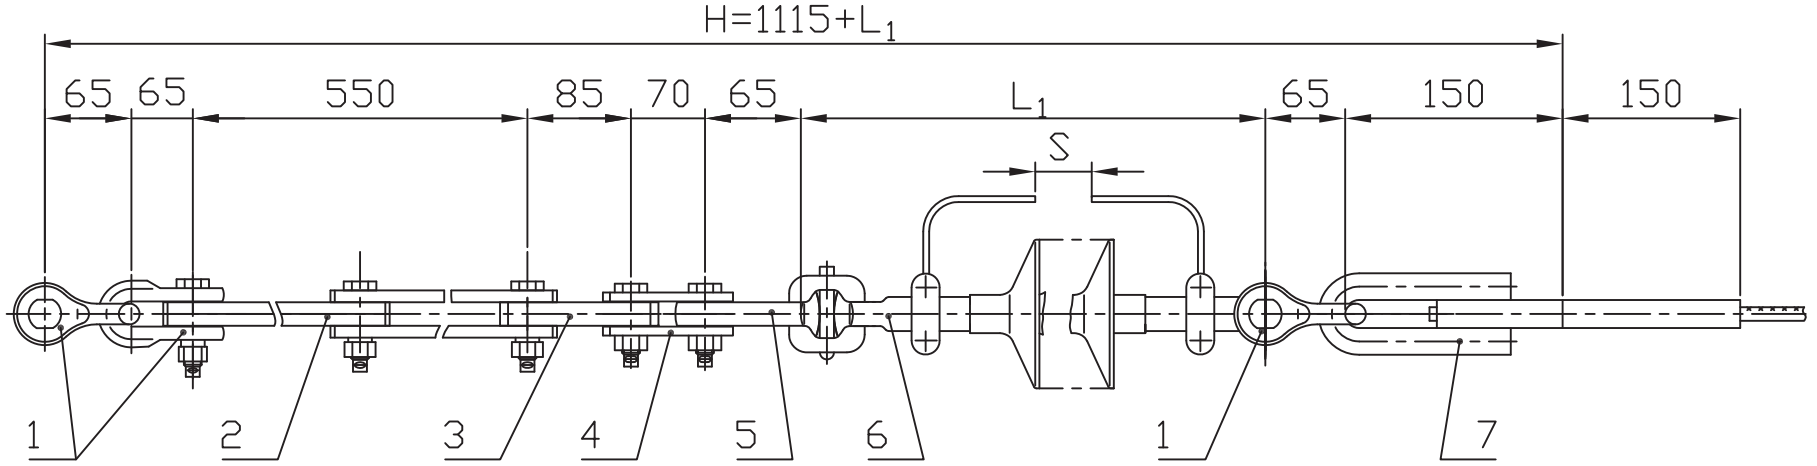

А

Б

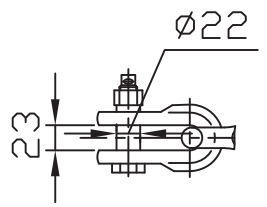

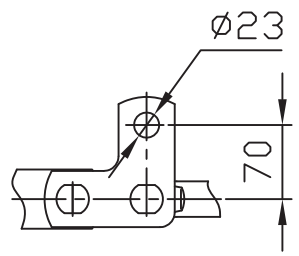

Поз.	Обозначение	Наименование	Кол.	Масса ед. кг	Прим.
1	СК-120-1Б	Скоба	3	0,92	
2	ПРР-12-1	Звено регулируемое	1	3,69	
3	ПР-12-6	Звено прямое	1	0,94	
4	ПТМ-12-3А	Звено монтажное	1	0,63	
5	СР-12-16	Серьга	1	0,41	
6	ЛКГ 120-	Изолятор исп. ГС с рогами	1	См. табл.4	
7	НС-70-3А	Зажим натяжной	1	1,68	
8	ЗПС-70-3Г	Зажим заземляющий	1	0,085	
Масса арматуры, кг				11,2	
Масса изолирующей подвески, кг					

Взам. инв. N

Подп. и дата

Инв. N подл.

Утв.	Вигдергауз		
Пров.	Липунцов		
Разраб.	Власкина		

ЭСИП-0121


ЭСС.001 ТМ - т.1


Натяжное изолированное с полимерным изолятором ряда 120 кН крепление троса С70 (с искровым промежутком) к а/у металлическим, ж/б и деревянным опорам ВЛ 220 кВ

Стадия	Лист	Листов
Р		1

Филиал ОАО "ФСК ЕЭС" "Электросетьсервис"

Формат А3

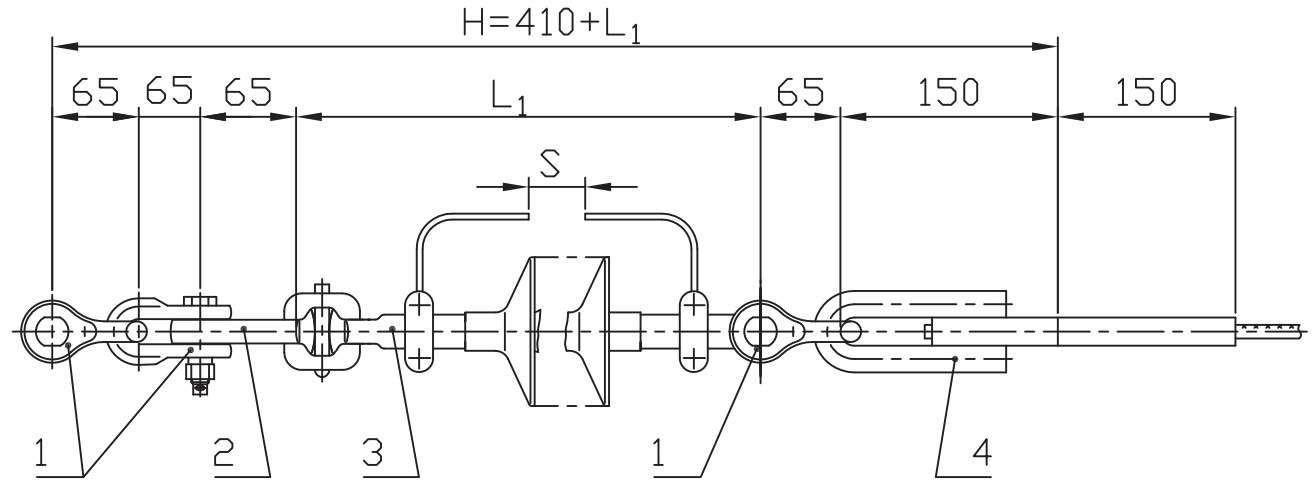

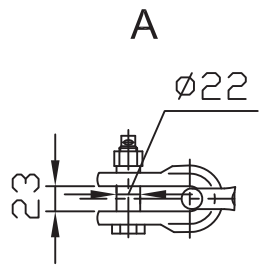

Поз.	Обозначение	Наименование	Кол.	Масса ед. кг	Прим.
1	СК-120-1Б	Скоба	3	0,92	
2	СР-12-16	Серьга	1	0,41	
3	ЛКГ 120-	Изолятор исп. ГС с рогами	1	См. табл.4	
4	НС-70-3А	Зажим натяжной	1	1,68	
Масса арматуры, кг				4,85	
Масса изолирующей подвески, кг					


Взам. инв. N


Подп. и дата

Инв. N подл.

Утв.	Вигдергауз			ЭСИП-0122	
				ЭСС.001 ТМ - т.1	
Пров.	Липунцов			Натяжное изолированное с полимерным изолятором ряда 120 кН крепление троса С70 (с искровым промежутком) к а/у металлическим, ж/б и деревянным опорам ВЛ 220 кВ	Стадия: Р; Лист: ; Листов: 1
Разраб.	Власкина				Филиал ОАО "ФСК ЕЭС" "Электросетьсервис"

Формат А3

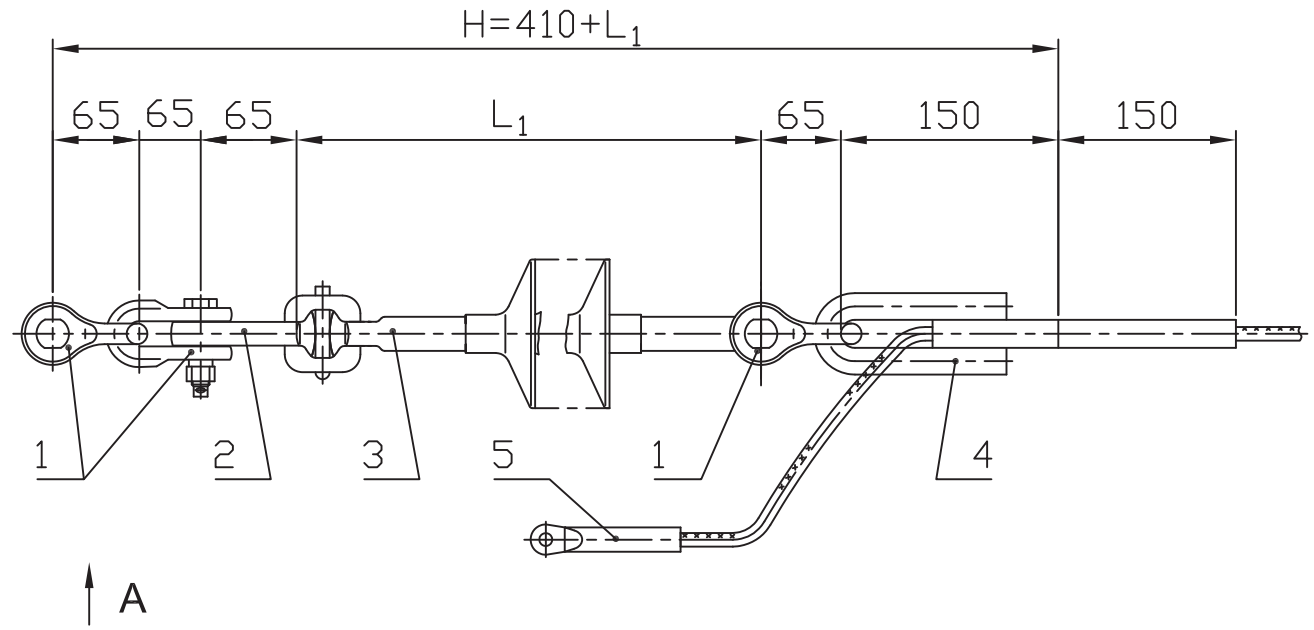

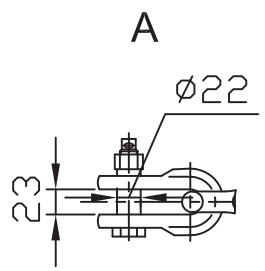

Поз.	Обозначение	Наименование	Кол.	Масса ед. кг	Прим.
1	СК-120-1Б	Скоба	3	0,92	
2	СР-12-16	Серьга	1	0,41	
3	ЛКГ 120-	Изолятор исп. ГС без рогов	1	См. табл.4	
4	НС-70-3Г	Зажим натяжной	1	1,68	
5	ЗПС-70-3Г	Зажим заземляющий	1	0,085	
Масса арматуры, кг				4,94	
Масса изолирующей подвески, кг					

Взам. инв. N

Подп. и дата


Инв. N подл.


			ЭСИП-0123
			ЭСС.001 ТМ - т.1
Утв.	Вигдергауз		Натяжное изолированное с полимерным изолятором ряда 120 кН крепление троса С70 (с заземлением) к а/у металлическим, ж/б и деревянным опорам ВЛ 220 кВ
Пров.	Липунцов		
Разраб.	Власкина		

Стадия	Лист	Листов
Р		1

Филиал ОАО "ФСК ЕЭС" "Электросетьсервис"

Формат А3

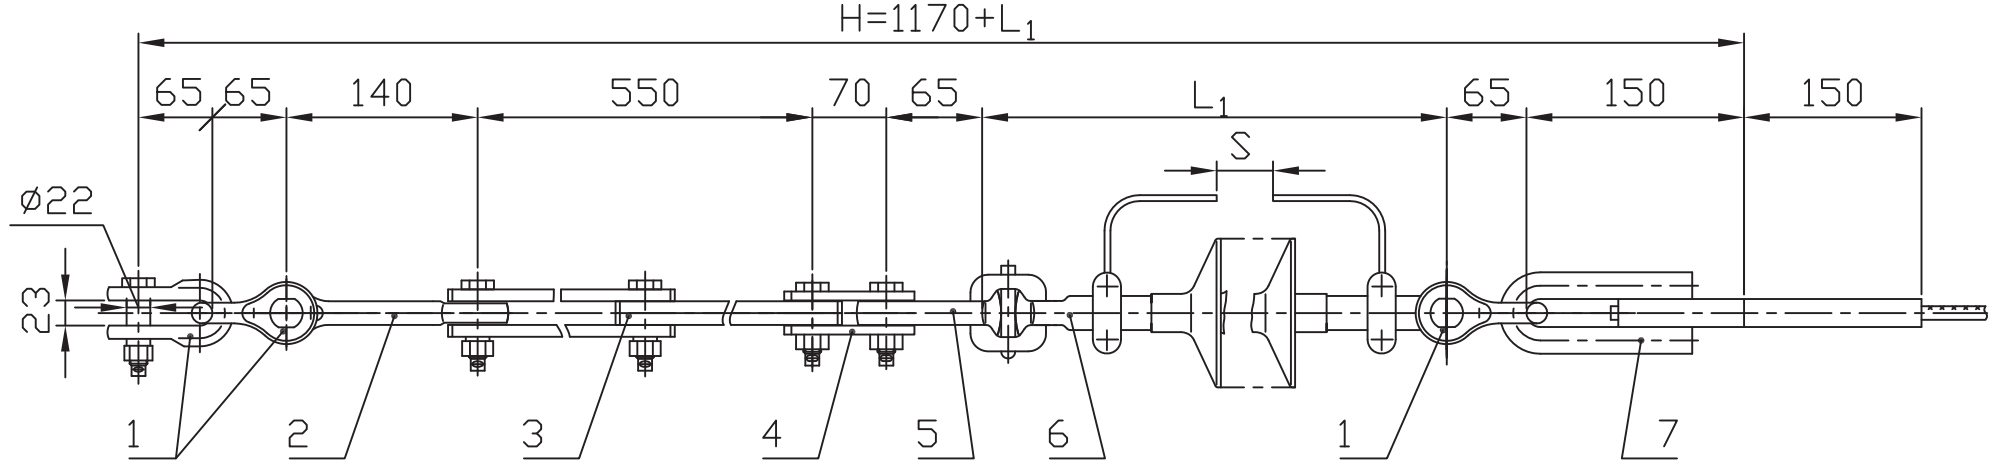

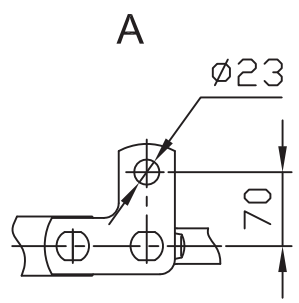

Поз.	Обозначение	Наименование	Кол.	Масса ед. кг	Прим.
1	СК-120-1Б	Скоба	3	0,92	
2	ПРВ-12-1	Звено вывернутое	1	0,74	
3	ПРР-12-1	Звено регулируемое	1	3,69	
4	ПТМ-12-3А	Звено монтажное	1	0,63	
5	СР-12-16	Серьга	1	0,41	
6	ЛКГ 120-	Изолятор исп. ГС с рогами	1	См. табл.4	
7	НС-70-3А	Зажим натяжной	1	1,68	
Масса арматуры, кг				11,0	
Масса изолирующей подвески, кг					


Взам. инв. N


Подп. и дата

Инв. N подл.

				ЭСИП-0124	
				ЭСС.001 ТМ - т.1	
Утв.	Вигдергауз			Натяжное изолированное с полимерным изолятором ряда 120 кН крепление троса С70 (с искровым промежутком) к а/у металлическим, ж/б и деревянным опорам ВЛ 220 кВ	Стадия: Р; Лист: ; Листов: 1
Пров.	Липунцов				Филиал ОАО "ФСК ЕЭС" "Электросетьсервис"
Разраб.	Власкина				

Формат А3

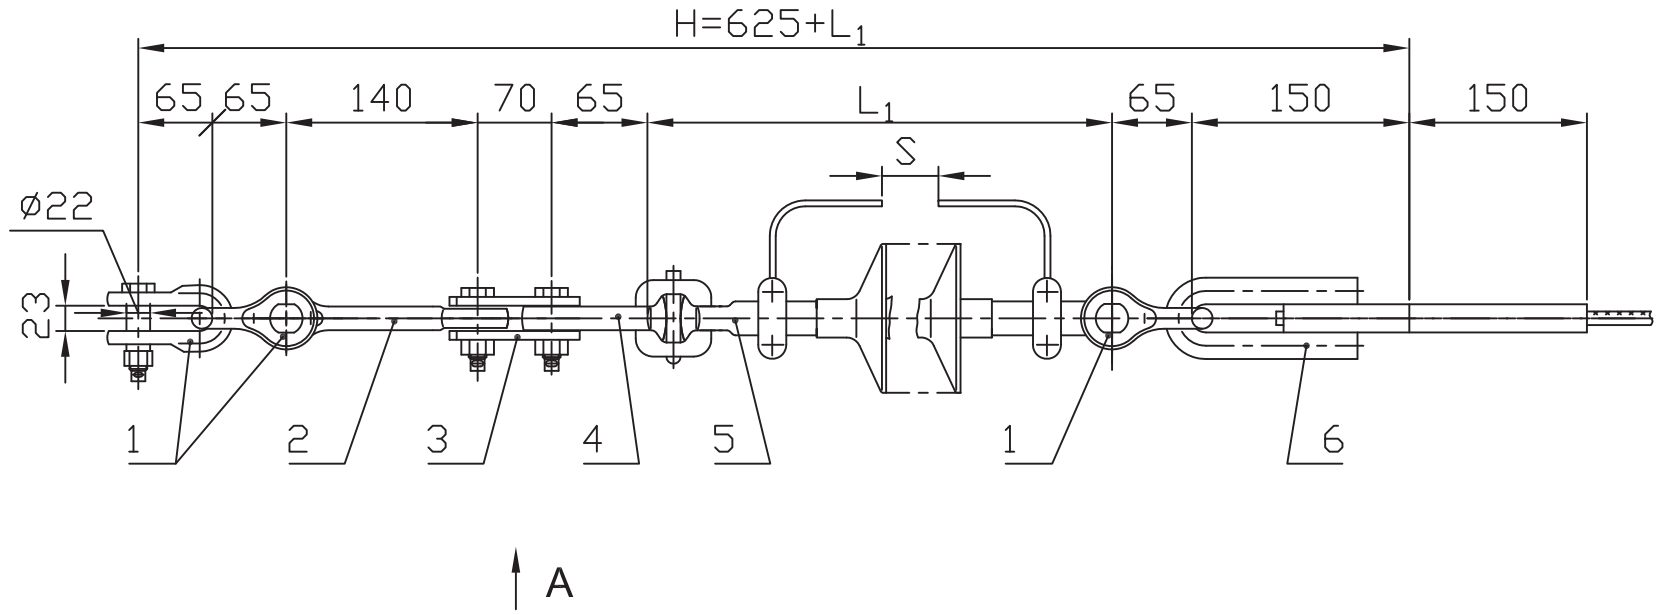

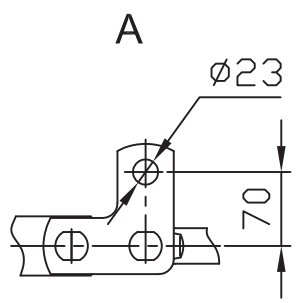

Поз.	Обозначение	Наименование	Кол.	Масса ед. кг	Прим.
1	СК-120-1Б	Скоба	3	0,92	
2	ПРВ-12-1	Звено вывернутое	1	0,74	
3	ПТМ-12-3А	Звено монтажное	1	1,07	
4	СР-12-16	Серьга	1	0,41	
5	ЛКГ 120-	Изолятор исп. ГС с рогами	1	См. табл.4	
6	НС-70-3А	Зажим натяжной	1	1,68	
Масса арматуры, кг				7,3	
Масса изолирующей подвески, кг					


Взам. инв. N


Подп. и дата

Инв. N подл.

				ЭСИП-0125		
				ЭСС.001 ТМ - т.1		
Утв.	Вигдергауз			Натяжное изолированное с полимерным изолятором ряда 120 кН крепление троса С70 (с искровым промежутком) к а/у металлическим, ж/б и деревянным опорам ВЛ 220 кВ	Стадия: Р; Лист: ; Листов: 1	
Пров.	Липунцов				Филиал ОАО "ФСК ЕЭС" "Электросетьсервис"	
Разраб.	Власкина					

Формат А3

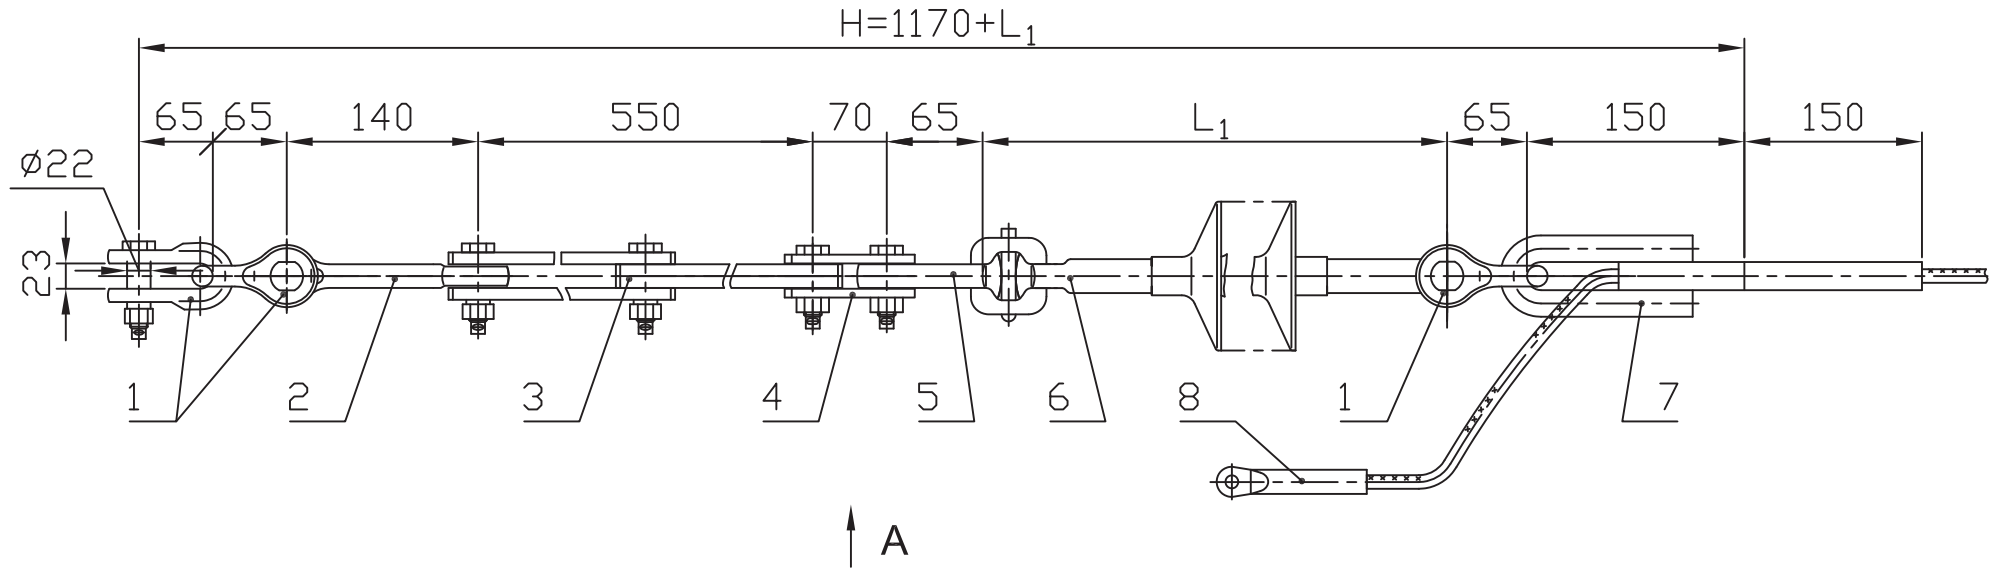

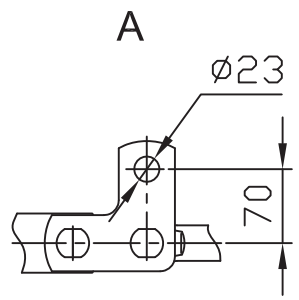

Поз.	Обозначение	Наименование	Кол.	Масса ед. кг	Прим.
1	СК-120-1Б	Скоба	3	0,92	
2	ПРР-12-1	Звено регулируемое	1	3,69	
3	ПР-12-6	Звено прямое	1	0,94	
4	ПТМ-12-3А	Звено монтажное	1	0,63	
5	СР-12-16	Серьга	1	0,41	
6	ЛКГ 120-	Изолятор исп. ГС (без рогов)	1	См. табл.4	
7	НС-70-3А	Зажим натяжной	1	1,68	
8	ЗПС-70-3Г	Зажим заземляющий	1	0,085	
Масса арматуры, кг				11,0	
Масса изолирующей подвески, кг					

Взам. инв. N

Подп. и дата


Инв. N подл.


				ЭСИП-0126
				ЭСС.001 ТМ - т.1
Утв.	Вигдергауз			Натяжное изолированное с полимерным изолятором ряда 120 кН крепление троса С70 (с заземлением) к а/у металлическим, ж/б и деревянным опорам ВЛ 220 кВ
Пров.	Липунцов			
Разраб.	Власкина			

Стадия	Лист	Листов
Р		1

Филиал ОАО "ФСК ЕЭС" "Электросетьсервис"

Формат А3

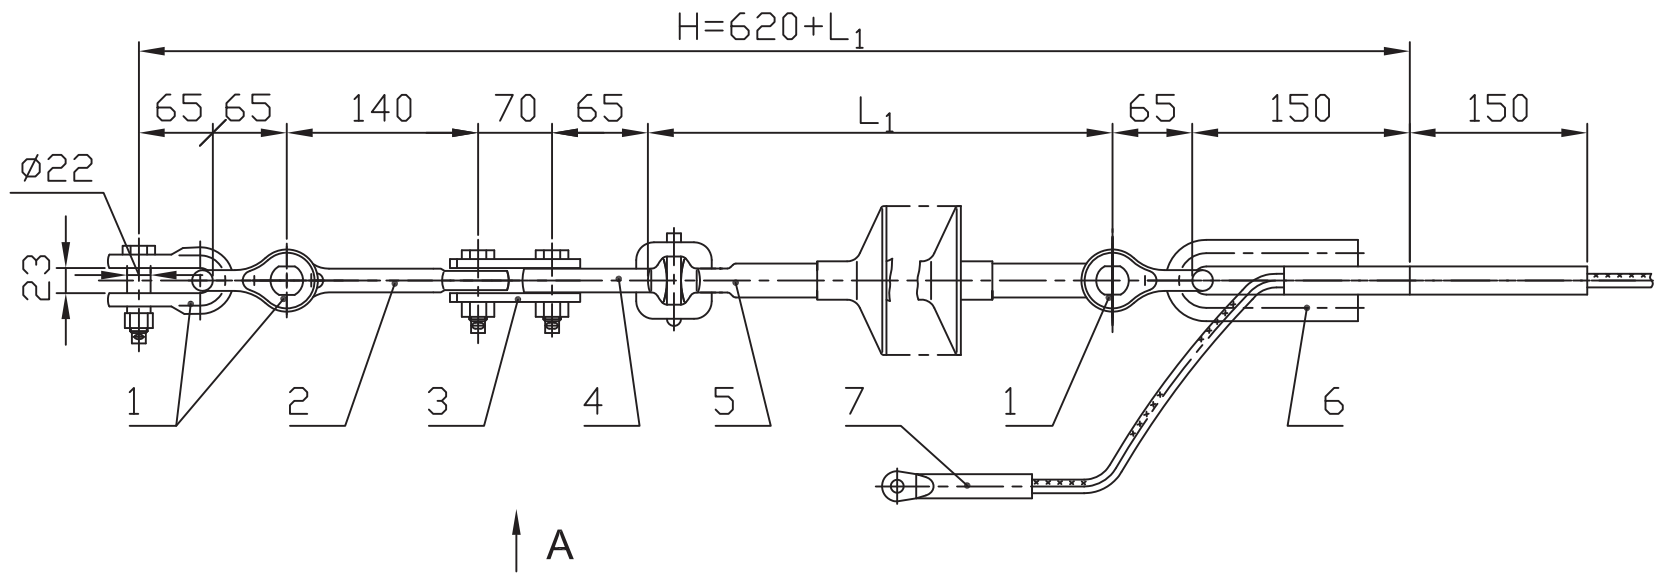

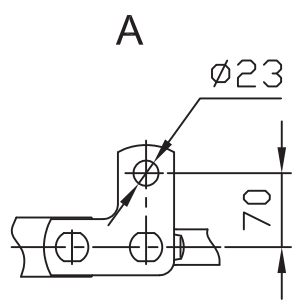

Поз.	Обозначение	Наименование	Кол.	Масса ед. кг	Прим.
1	СК-120-1Б	Скоба	3	0,92	
2	ПРВ-12-1	Звено вывернутое	1	0,74	
3	ПТМ-12-3А	Звено монтажное	1	1,07	
4	СР-12-16	Серьга	1	0,41	
5	ЛКГ 120-	Изолятор исп. ГС без рогов	1	См. табл.4	
6	НС-70-3	Зажим натяжной	1	1,68	
7	ЗПС-70-3Г	Зажим заземляющий	1	0,085	
Масса арматуры, кг				4,5	
Масса изолирующей подвески, кг					

Взам. инв. N

Подп. и дата

Инв. N подл.

		ЭСИП-0127	
		ЭСС.001 ТМ - т.1	
Утв.	Вигдергауз	Натяжное изолированное с полимерным изолятором ряда 120 кН крепление троса С70 (с заземлением) к а/у металлическим, ж/б и деревянным опорам ВЛ 220 кВ	Стадия: Р; Лист: ; Листов: 1
Пров.	Липунцов		Филиал ОАО "ФСК ЕЭС" "Электросетьсервис"
Разраб.	Власкина		

Формат А3